
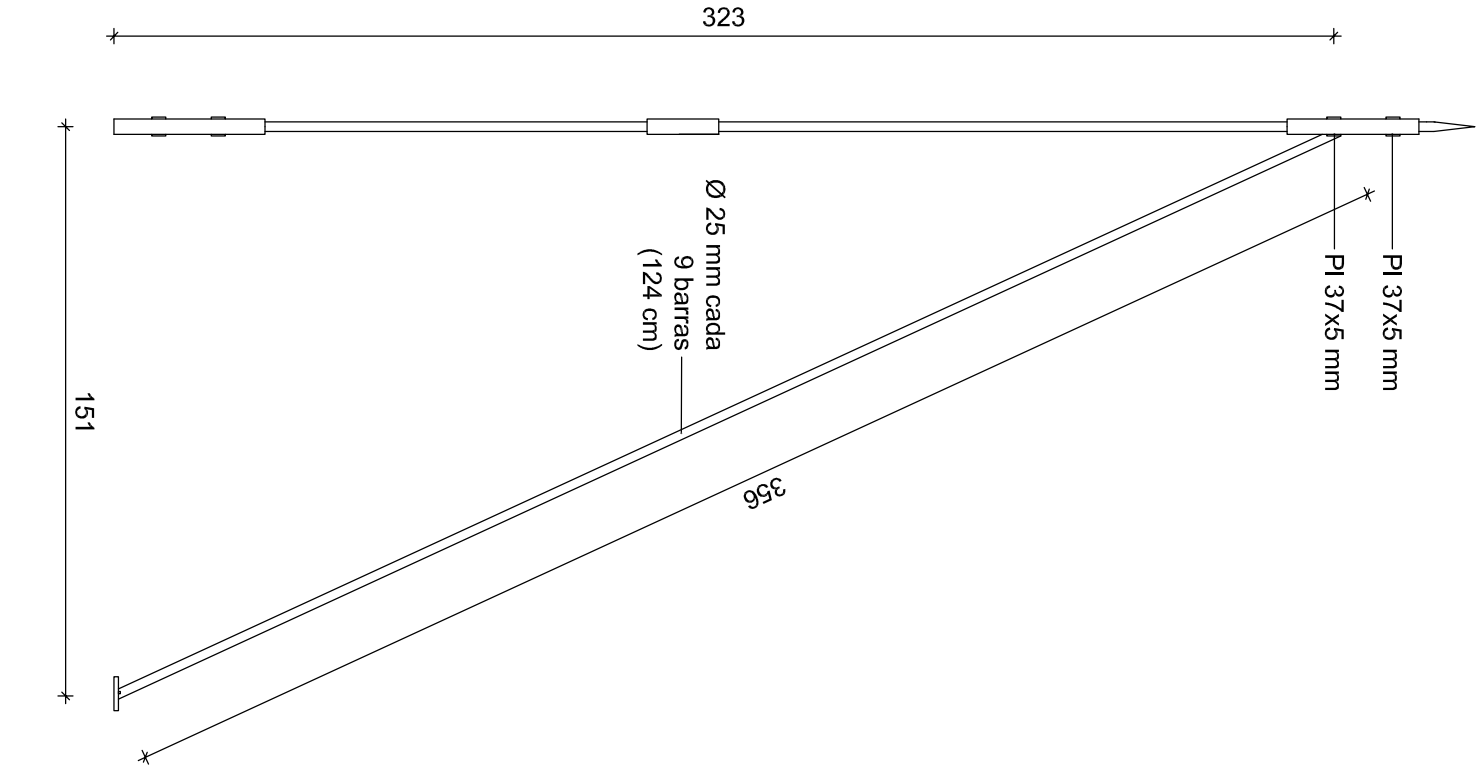


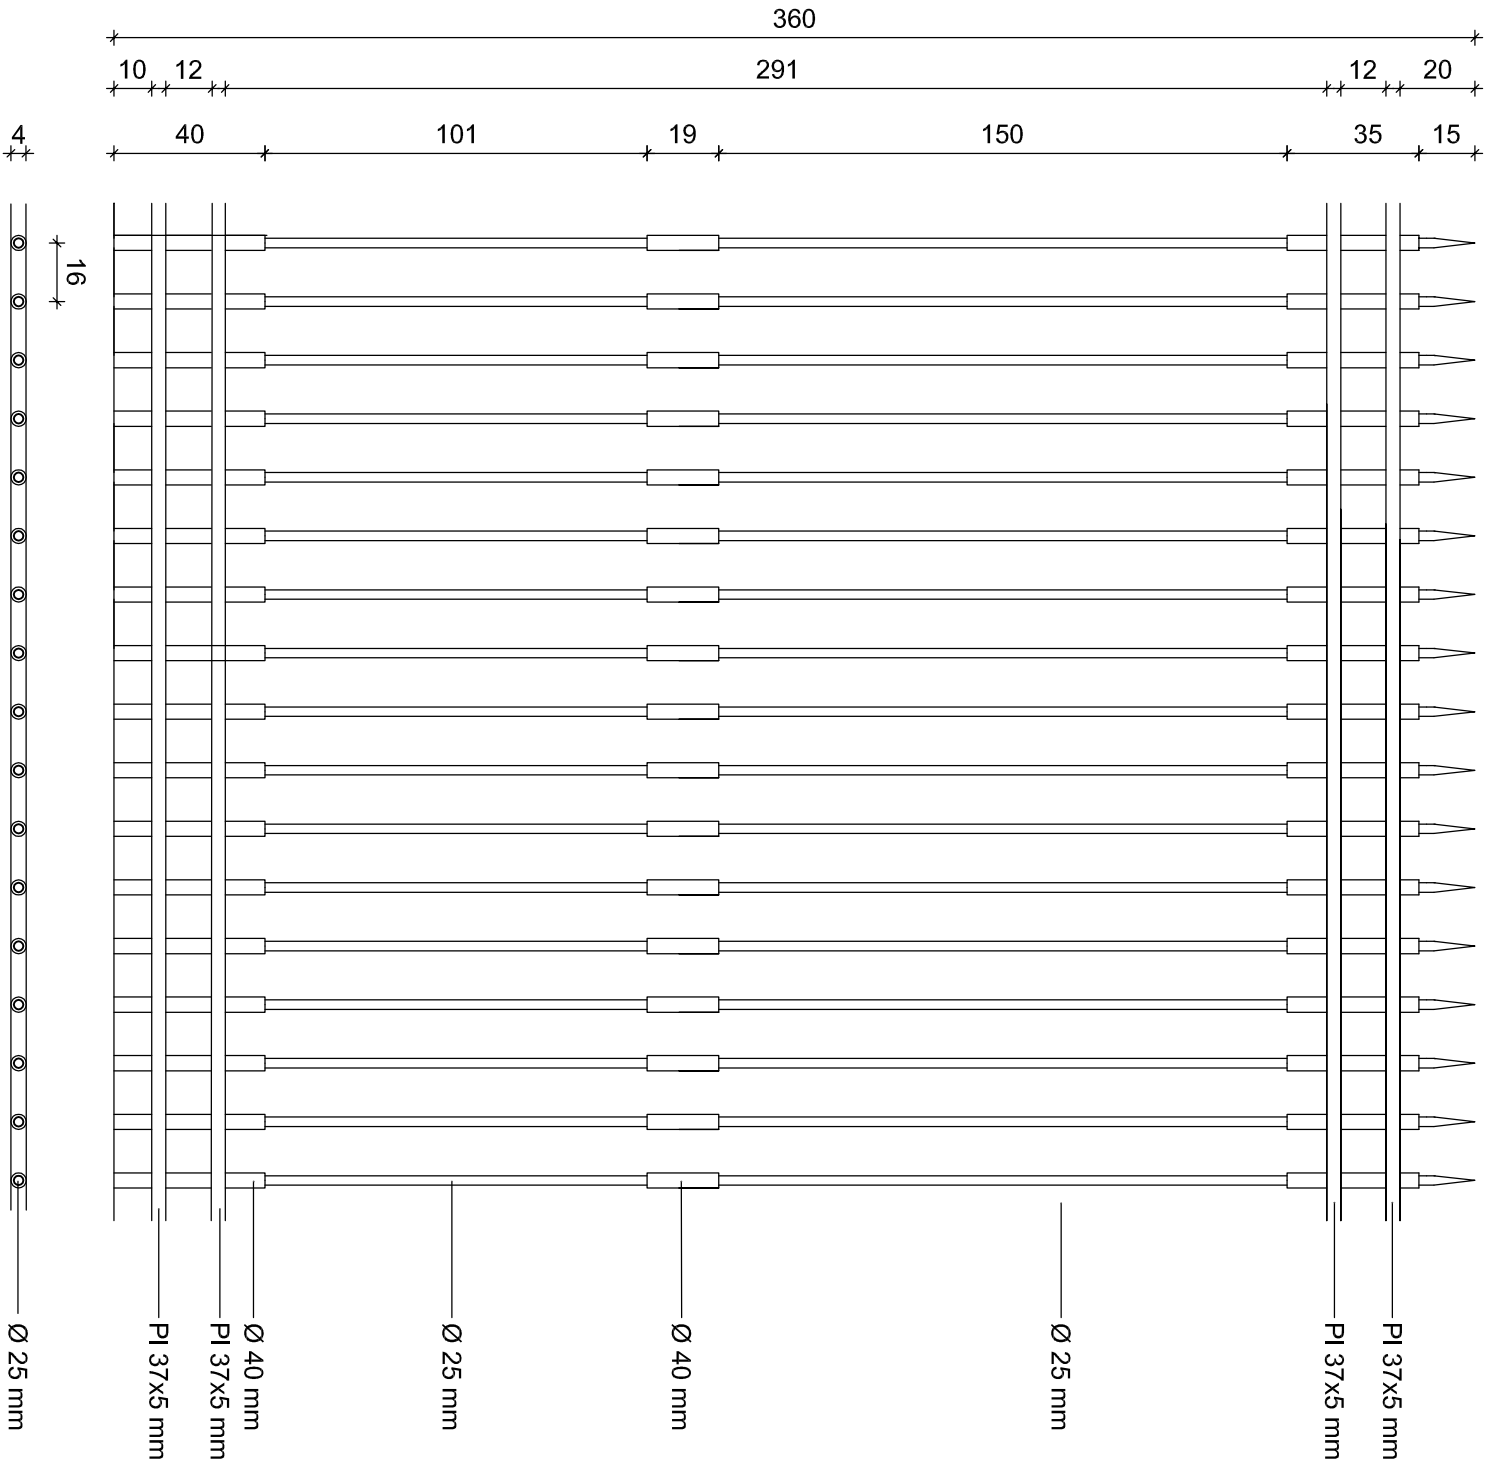

ELEVACIÓN Y PLANTA TRAMO TIPO

Esc. 1/20

DETALLE DIAGONAL

Esc. 1/20

Ubicación

PROYECTO

Dirección de
Arquitectura
Ministerio de Obras
Públicas
Gobierno de Chile

Arqto. Dino Bozzi F.

TÁNDEM Limitada

contacto@tandemlimitada.cl

PROYECTO: REPARACIÓN PARCIAL BASÍLICA DEL
SALVADOR STGO

DIRECCIÓN DE ARQUITECTURA

DIRECCIÓN REGIONAL METROPOLITANA

BASÍLICA DEL SALVADOR

Huérfanos 1796 - Santiago

Región Metropolitana

LEVANTAMIENTO

REJA 01 - fachada

1/20

Ago. 13

1305

LEV

DET

-

A

Emisor

Proyecto

Fase

Tipo

Zona

Índice


Dibuj: RL

Control : VI


Archivo de ref.: TD_1212_LEV_ES_Rev09

Re-01


ES

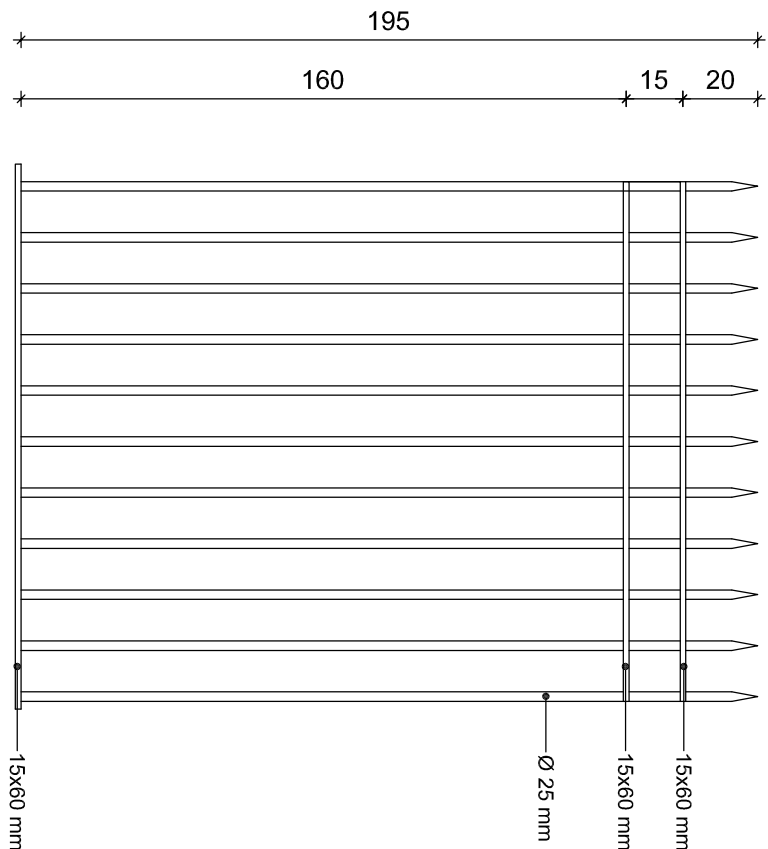


ELEVACIÓN Y PLANTA
REJA 02
Esc. 1/20

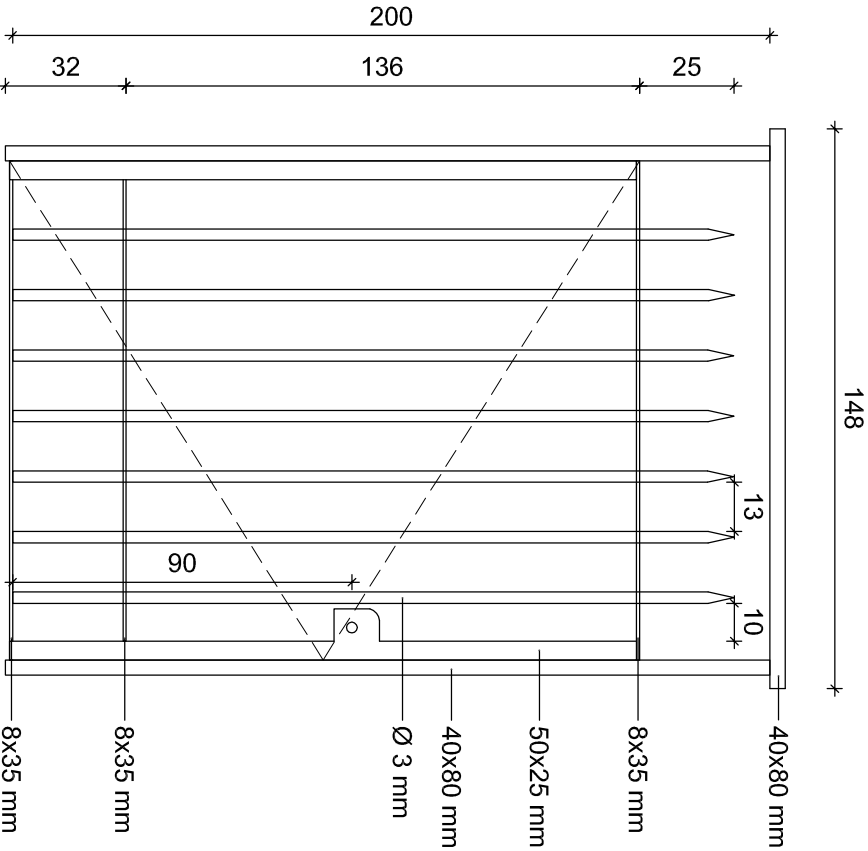


ELEVACIÓN Y PLANTA
Re 05 y 08
Esc. 1/20

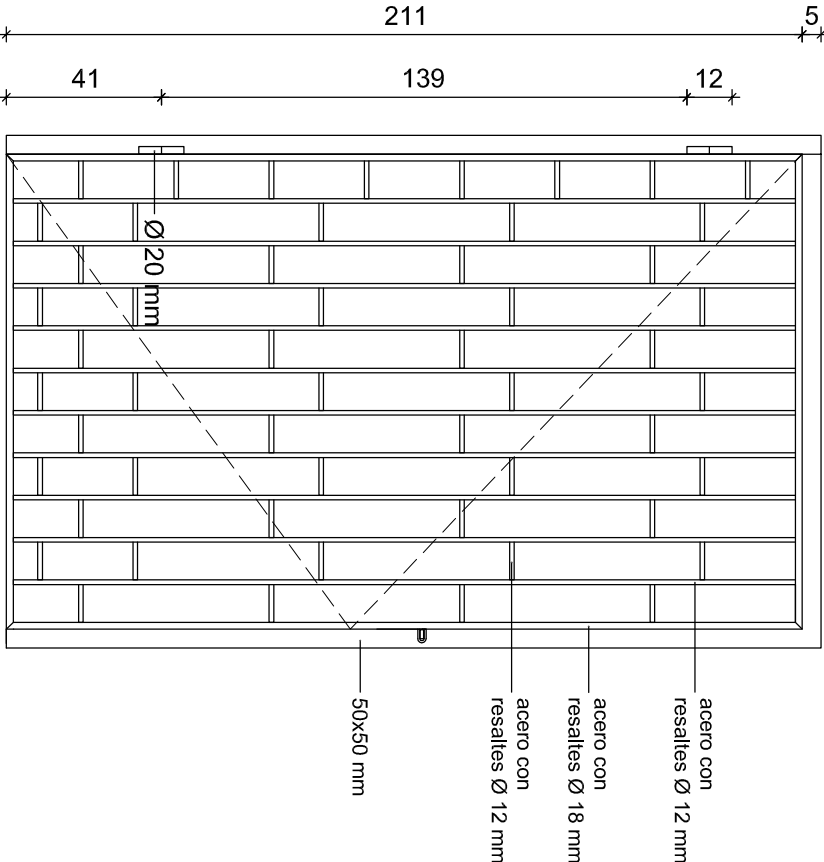


ELEVACIÓN Y PLANTA
Re 03 y 04
Esc. 1/20

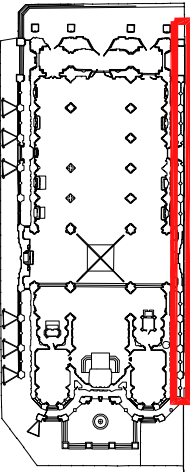
Ubicación					
DIRECCIÓN DE ARQUITECTURA DIRECCIÓN REGIONAL METROPOLITANA		PROYECTO			
PROYECTO: REPARACIÓN PARCIAL BASÍLICA DEL SALVADOR STGO					
BASÍLICA DEL SALVADOR		ES			
Huérfanos 1796 - Santiago		Re			
Región Metropolitana		02-08			
LEVANTAMIENTO		1/20		Ago. 13	
REJA TIPO 02-03-04-05-08		Escala		Fecha	
TD		LEV		DET	
Emisor		Proyecto		Zona	
Dibuj: RL		Control : VI		Índice	

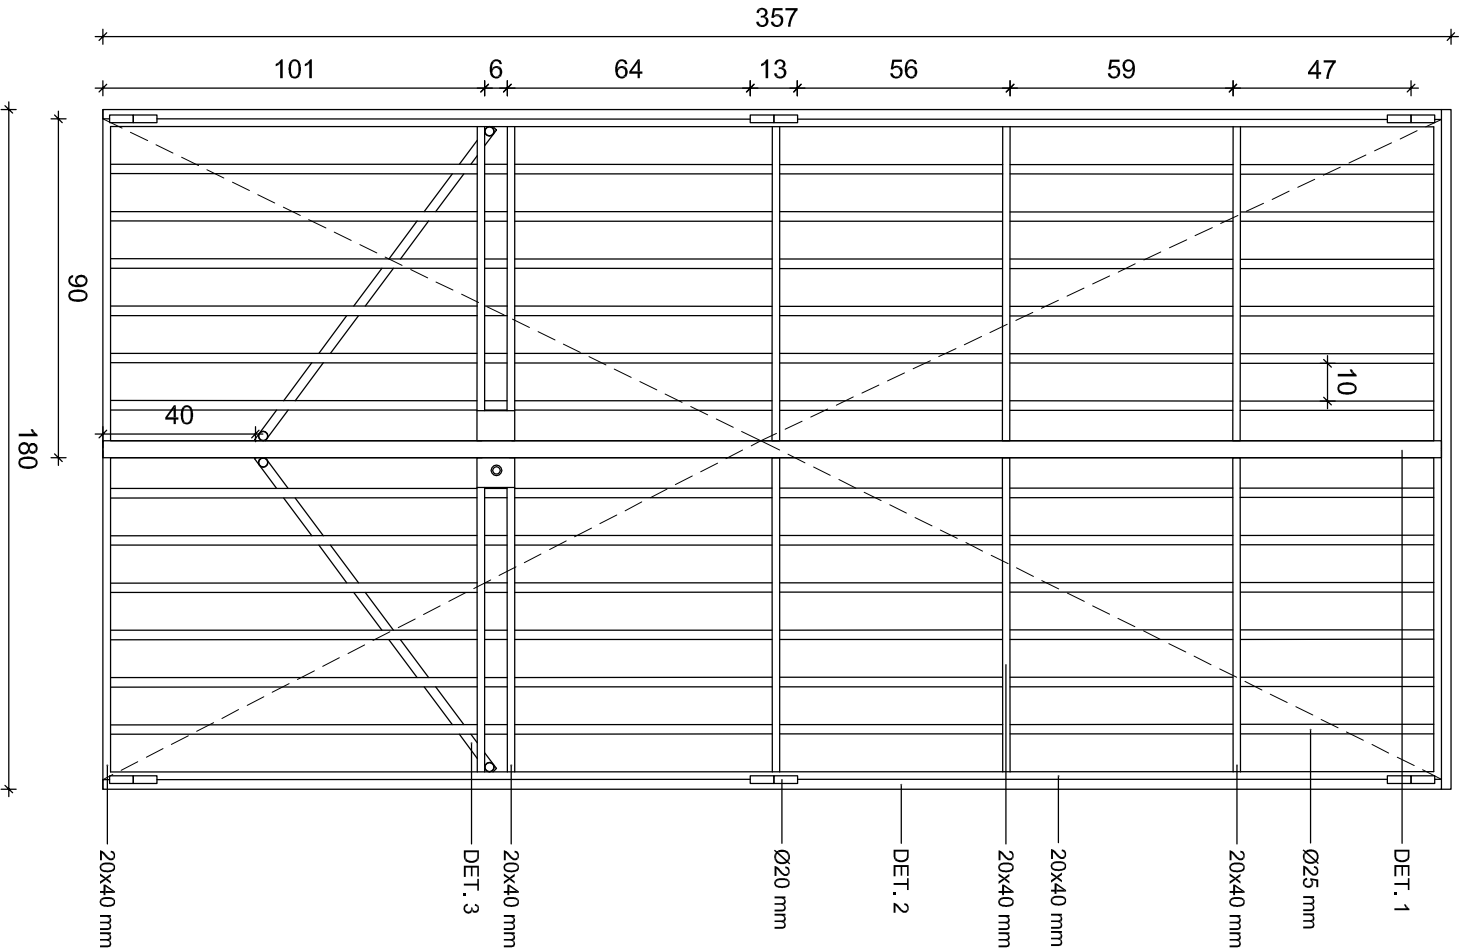


ELEVACIÓN
Esc. 1/20

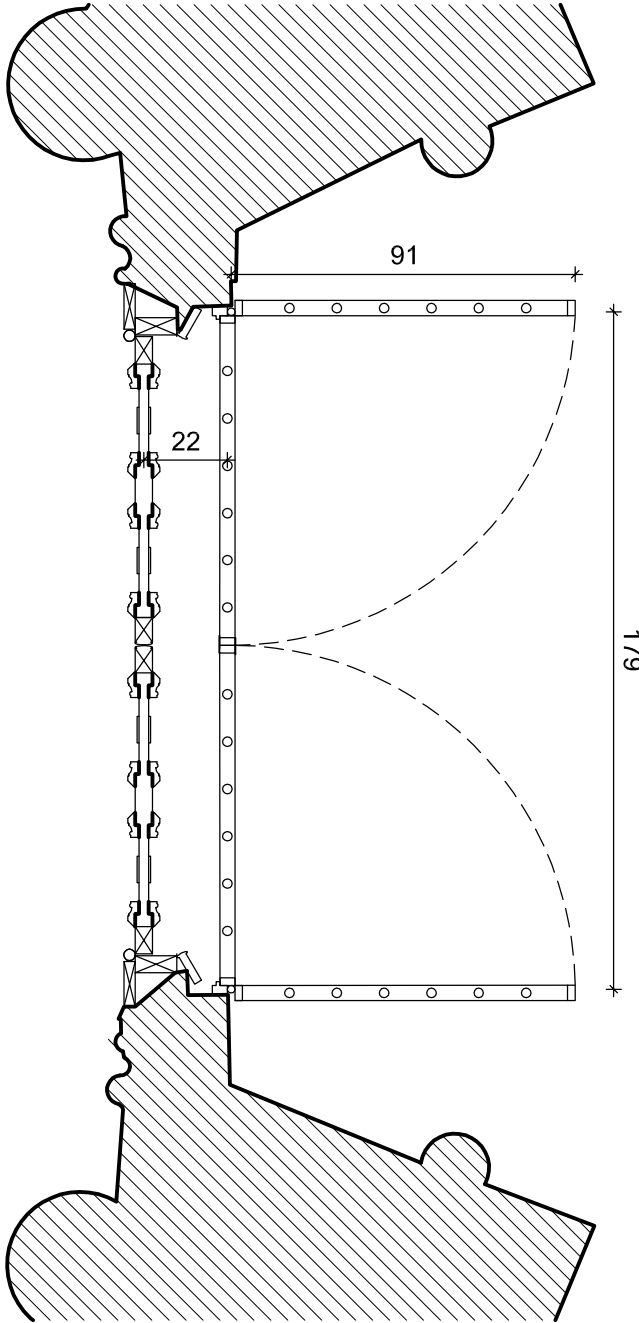


PLANTA
Esc. 1/20

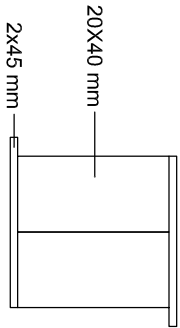


DETALLE 1
Esc. 1/5

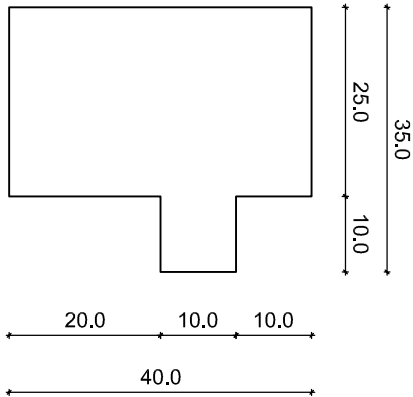


DETALLE 2
Esc. 1/10

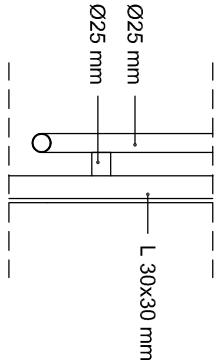


DETALLE 3
Esc. 1/10

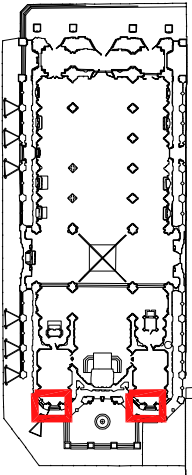
Ubicación														
														
PROYECTO					PROYECTO									
					Arqto. Dino Bozzi F. TÁNDEM Limitada contacto@tandemlimitada.cl									
DIRECCIÓN DE ARQUITECTURA DIRECCIÓN REGIONAL METROPOLITANA														
PROYECTO: REPARACIÓN PARCIAL BASÍLICA DEL SALVADOR STGO														
BASÍLICA DEL SALVADOR														
Huérfanos 1796 - Santiago Región Metropolitana					ES Re 06-10									
LEVANTAMIENTO					1/20		Ago. 13							
REJAS TIPO 06-10					Escala		Fecha							
TD	TD	LEV	DET		-	A								
Emisor	Proyecto	Fase	Tipo		Zona	Índice								
Dibujó: RL Control : VI Archivo de ref.: TD_1212_LEV_ES_Reading														

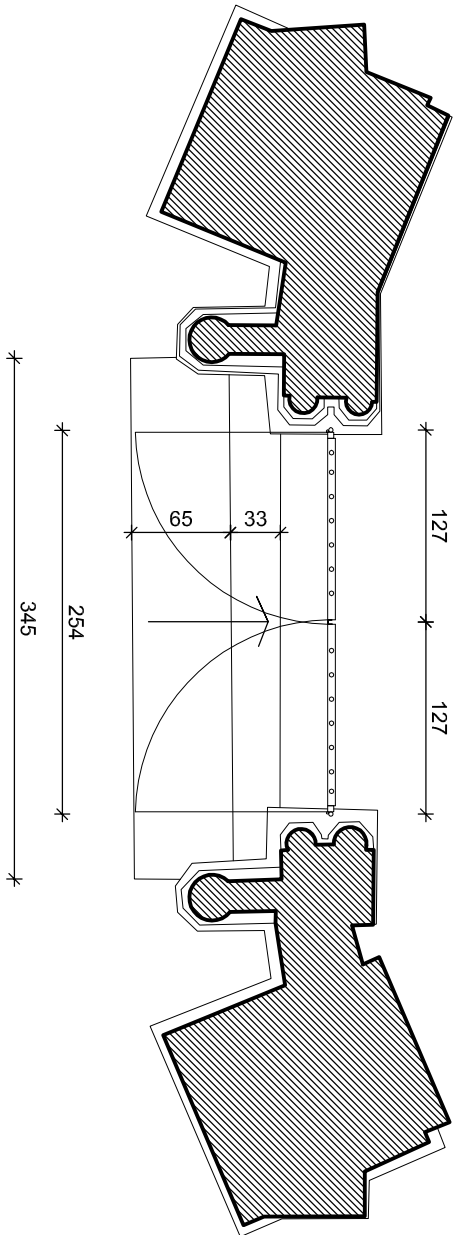

PLANTA CONTEXTO REJA
Esc. 1/50

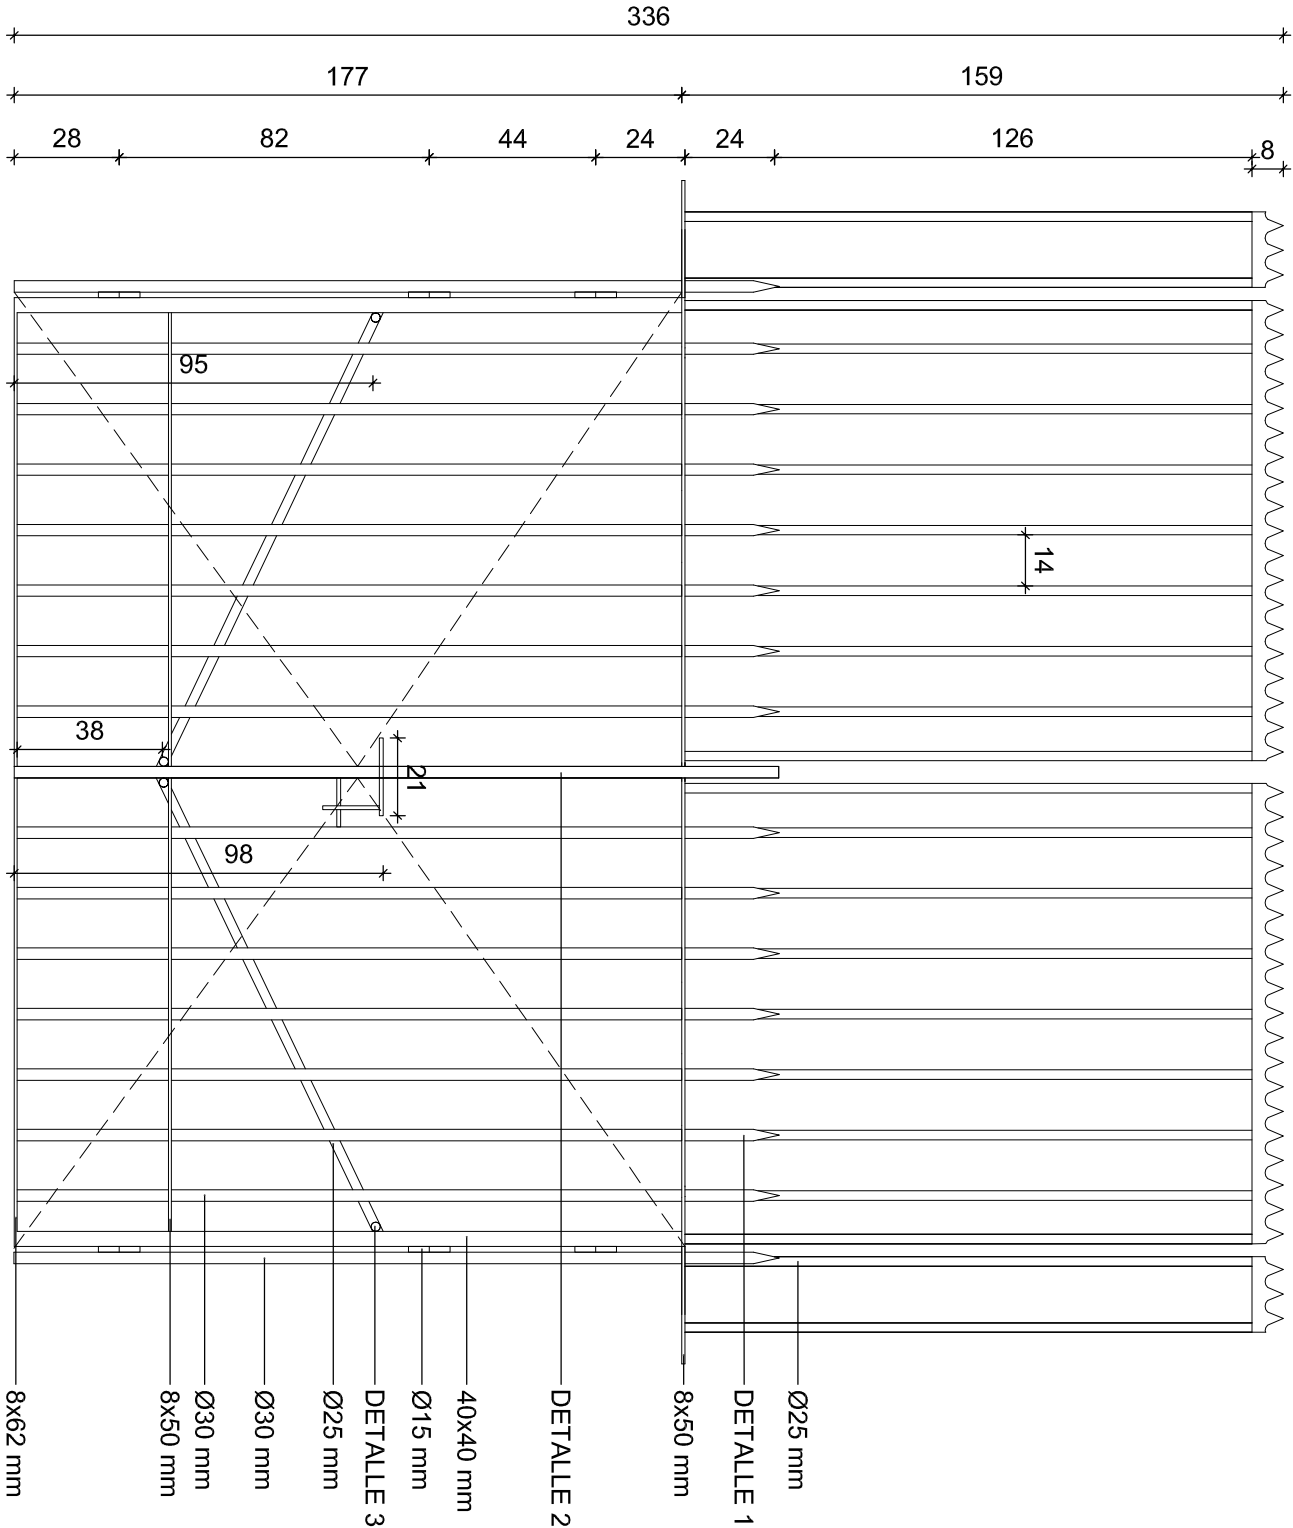


ELEVACIÓN
Esc. 1/20

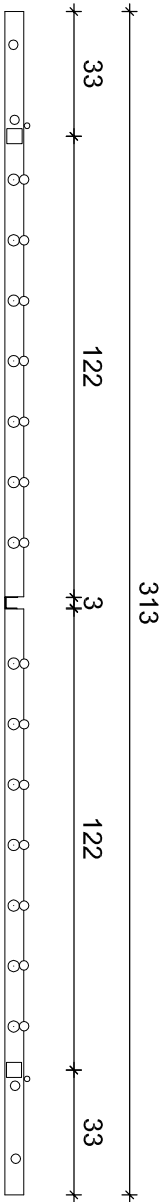


PLANTA
Esc. 1/20


DETALLE 1
Esc. 1/10

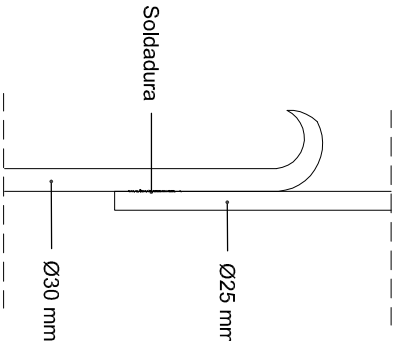



DETALLE 2
Esc. 1/20

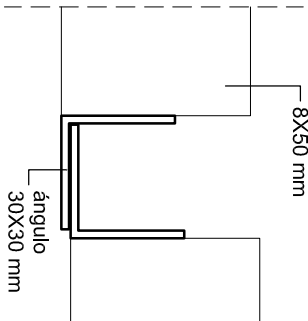

DETALLE 3
Esc. 1/10


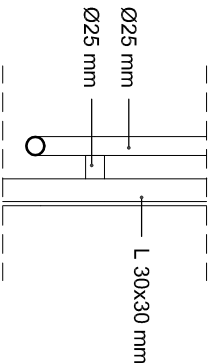


Ubicación					
DIRECCIÓN DE ARQUITECTURA DIRECCIÓN REGIONAL METROPOLITANA		PROYECTO			
PROYECTO: REPARACIÓN PARCIAL BASÍLICA DEL SALVADOR STGO					
BASÍLICA DEL SALVADOR					
Huérfanos 1796 - Santiago					
Región Metropolitana					
DIRECCIÓN DE ARQUITECTURA Ministerio de Obras Públicas		PROYECTO			
Gobierno de Chile					
Arqto. Dino Bozzi F. TÁNDEM Limitada contacto@tandemlimitada.cl					
LEVANTAMIENTO		1/20		Ago. 13	
REJA TIPO 07		Escala		Fecha	
TD		LEV		DET	
1305		Fase		-	
Emisor		Proyecto		Tipo	
Zona		Índice			
Dibuj: RL		Control : VI		Archivo de ref.: TD_1212_LEV_ES_Rev09	

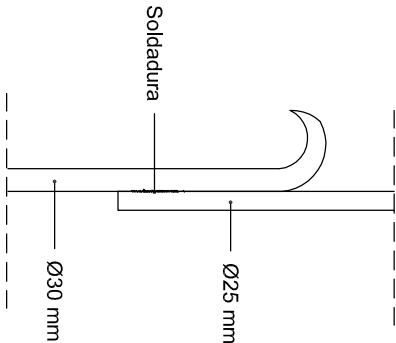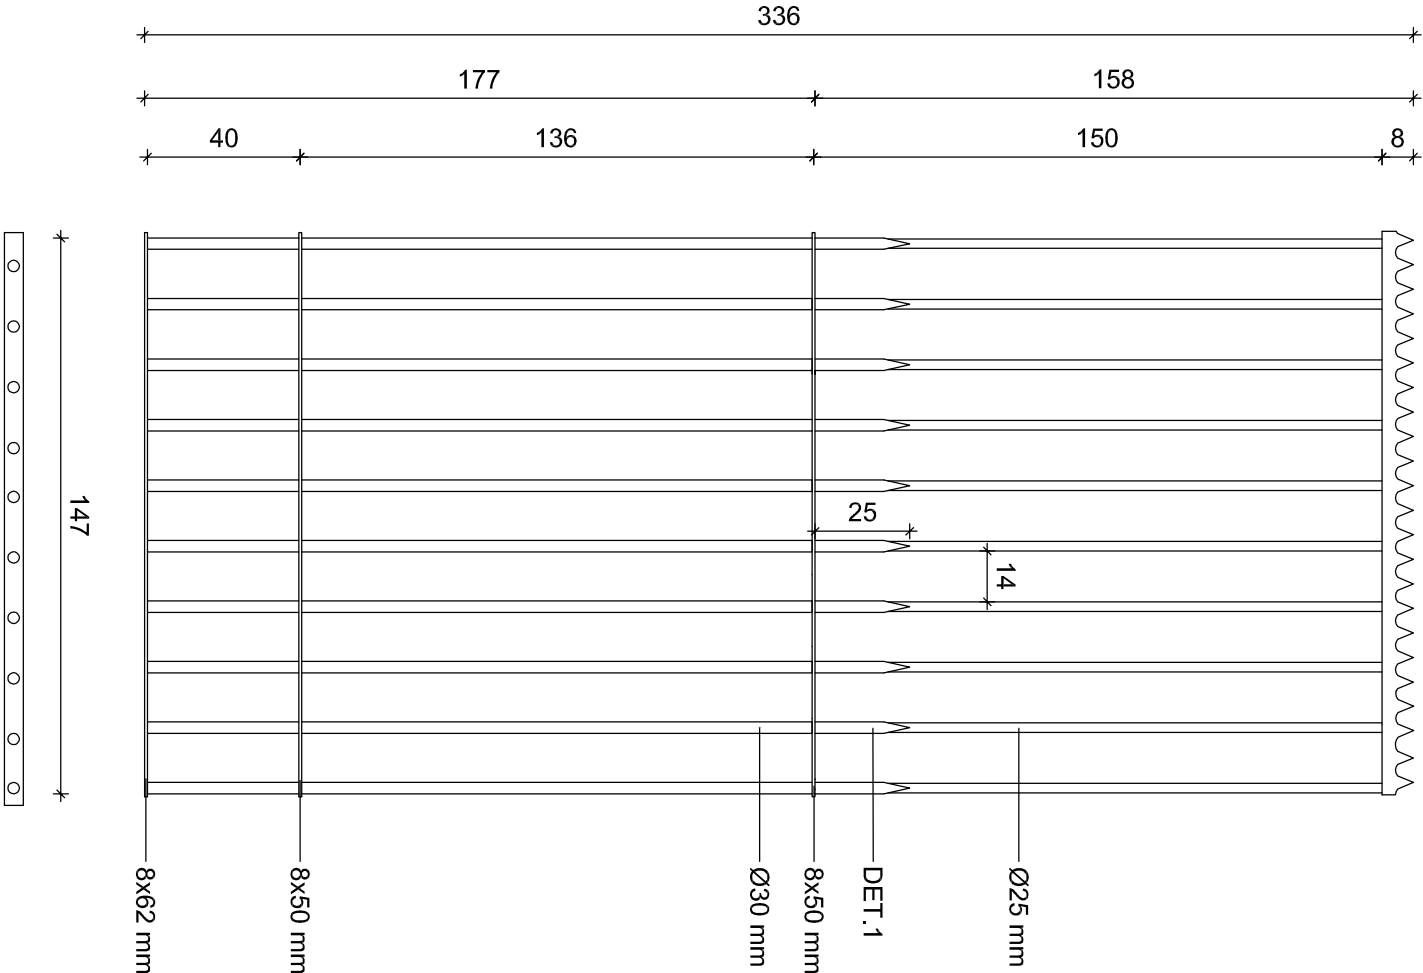


DETALLE 1
Esc. 1/10


Ubicación				
DIRECCIÓN DE ARQUITECTURA DIRECCIÓN REGIONAL METROPOLITANA		PROYECTO		
PROYECTO: REPARACIÓN PARCIAL BASÍLICA DEL SALVADOR STGO				
BASÍLICA DEL SALVADOR				
Huérfanos 1796 - Santiago Región Metropolitana				
LEVANTAMIENTO REJAS TIPO 09				
1/20		Ago. 13		
Escala		Fecha		
TD 1305		LEV DET - A		
Emisor Proyecto		Tipo Zona Índice		
Dibuj: RL Control: VI		Archivo de ref.: TD_1212_LEV_ES_Rev09		

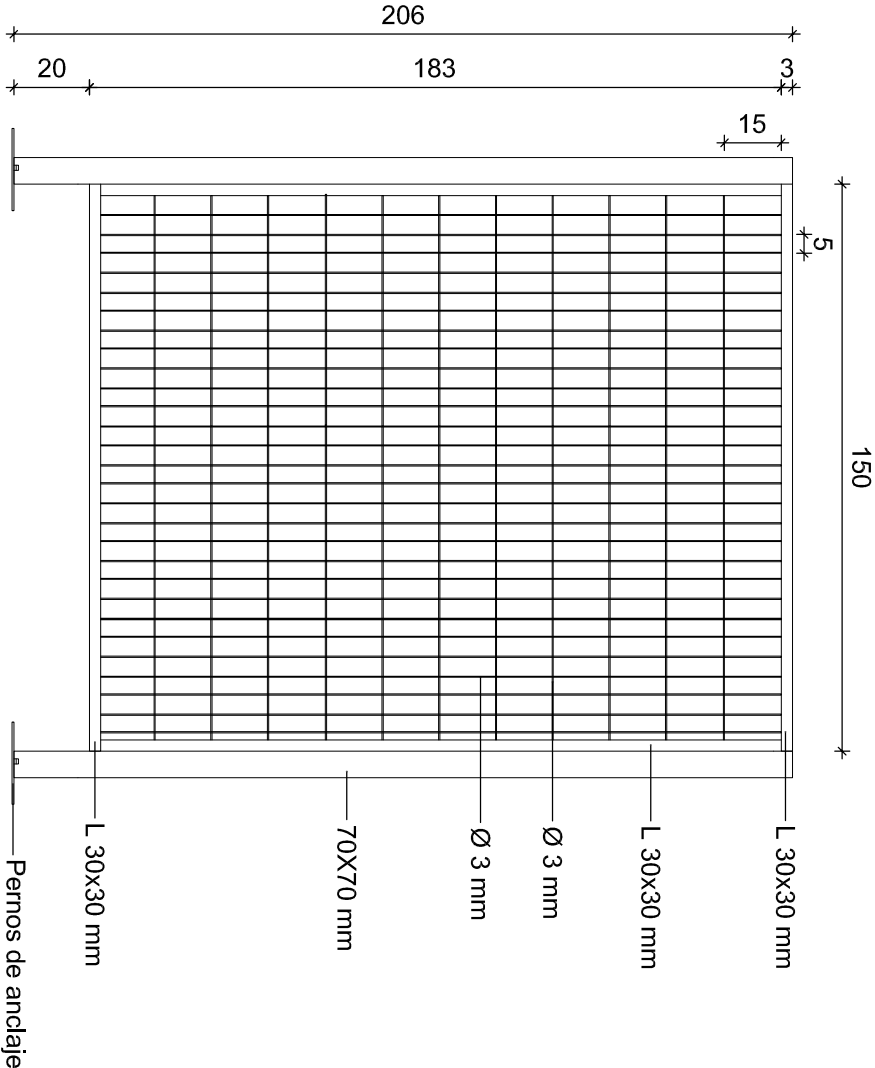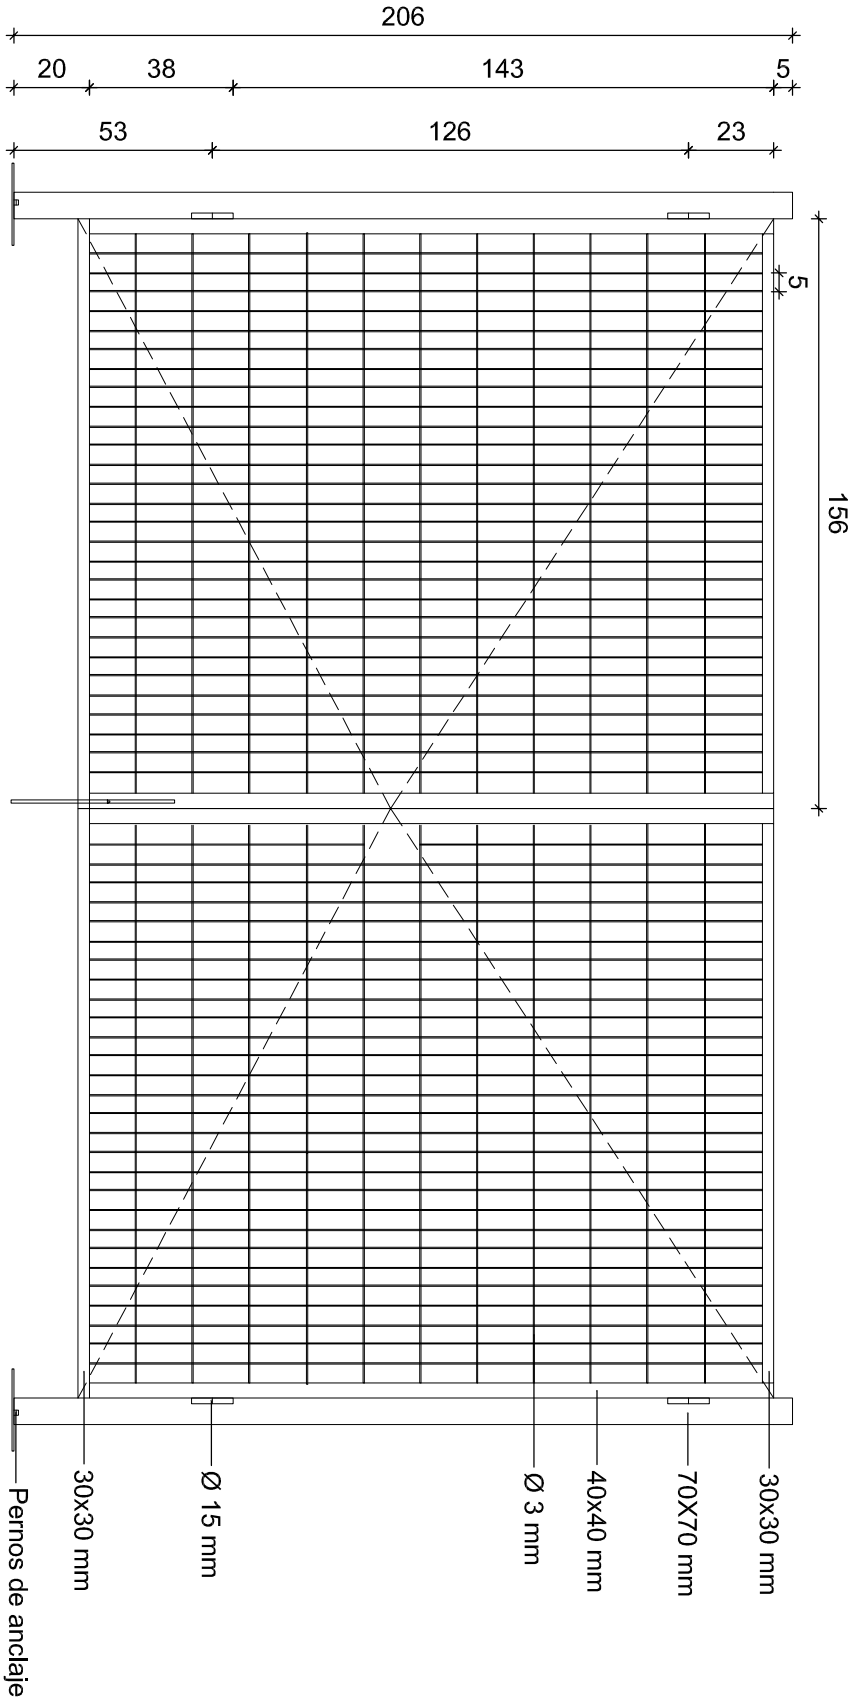

ELEVACIÓN PORTÓN ACCESO AGUSTINAS
Esc. 1/20

ELEVACIÓN MÓDULO TIPO
REJA CALLE AGUSTINAS Y A. BARROSO
Esc. 1/20

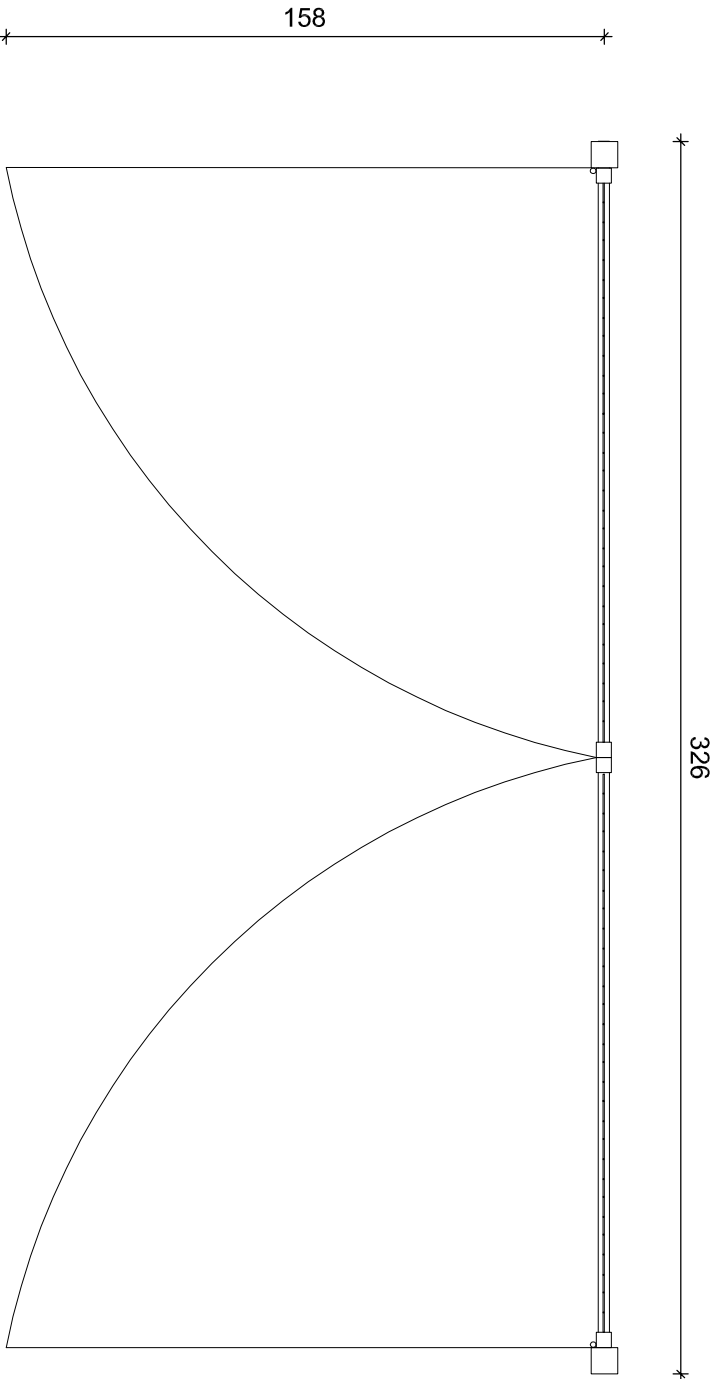

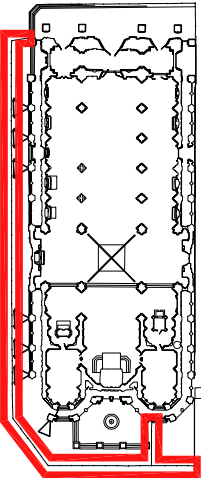Ubicación							
DIRECCIÓN DE ARQUITECTURA DIRECCIÓN REGIONAL METROPOLITANA					PROYECTO		
					Arqto. Dino Bozzi F. TÁNDEM Limitada contacto@tandemlimitada.cl		
PROYECTO: REPARACIÓN PARCIAL BASÍLICA DEL SALVADOR STGO							
BASÍLICA DEL SALVADOR					ES Re 11-12		
Huérfanos 1796 - Santiago Región Metropolitana							
LEVANTAMIENTO REJA TIPO 11-12 / AGUSTINAS Y A. BARR.					1/20	Ago. 13	
Escala					Fecha		
TD	TD	LEV	DET	-	A		
Emisor	Proyecto	Fase	Tipo	Zona	Índice		
Dibuj: RL Control : VI					Archivo de ref.: TD_1212_LEV_ES_Rev09		