



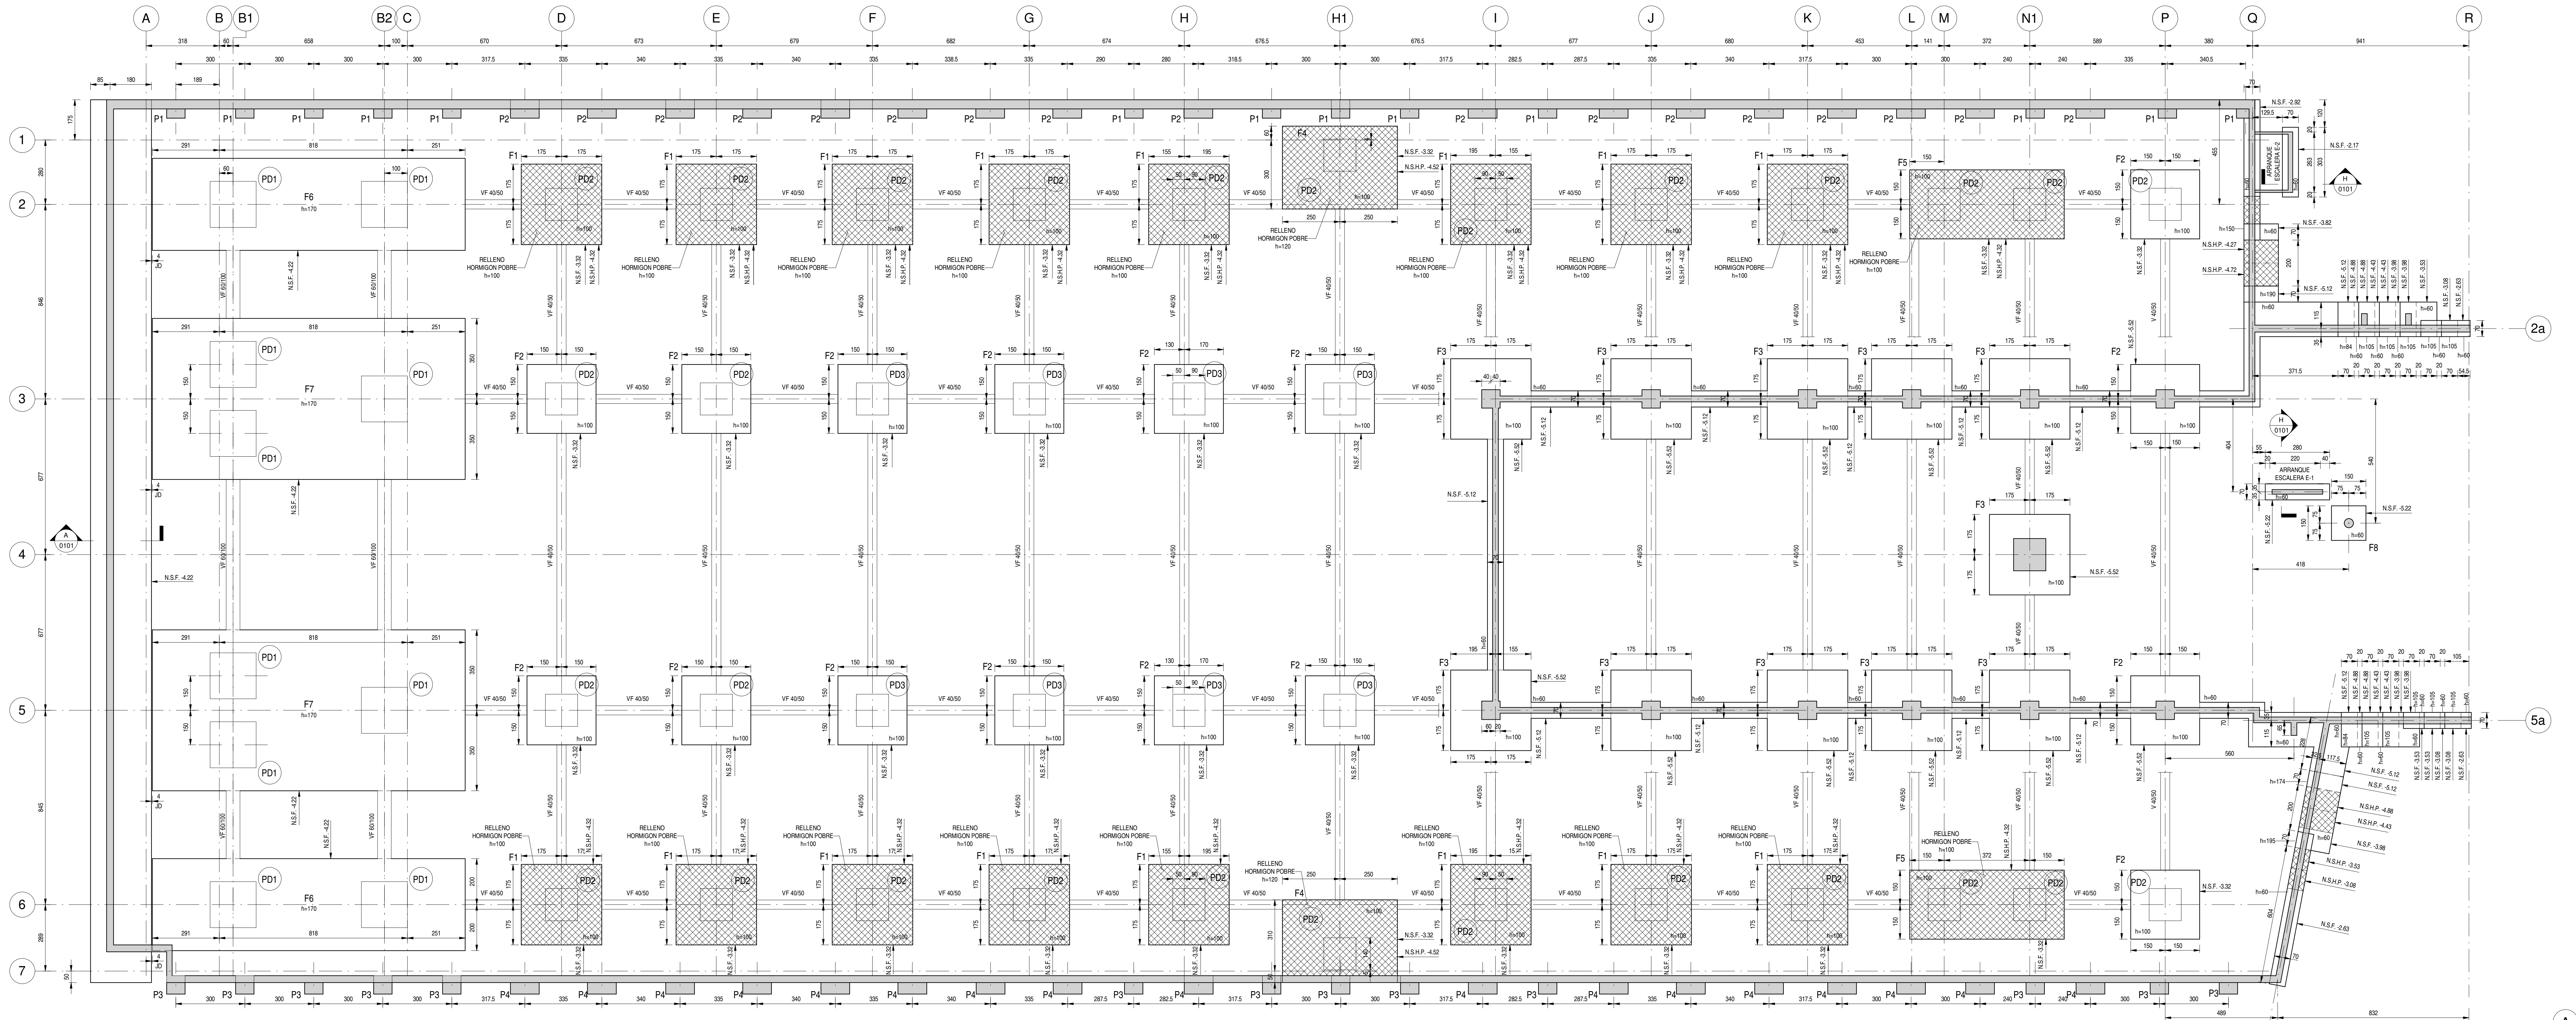

PLANTA DE FUNDACION

ESCALA 1 : 100

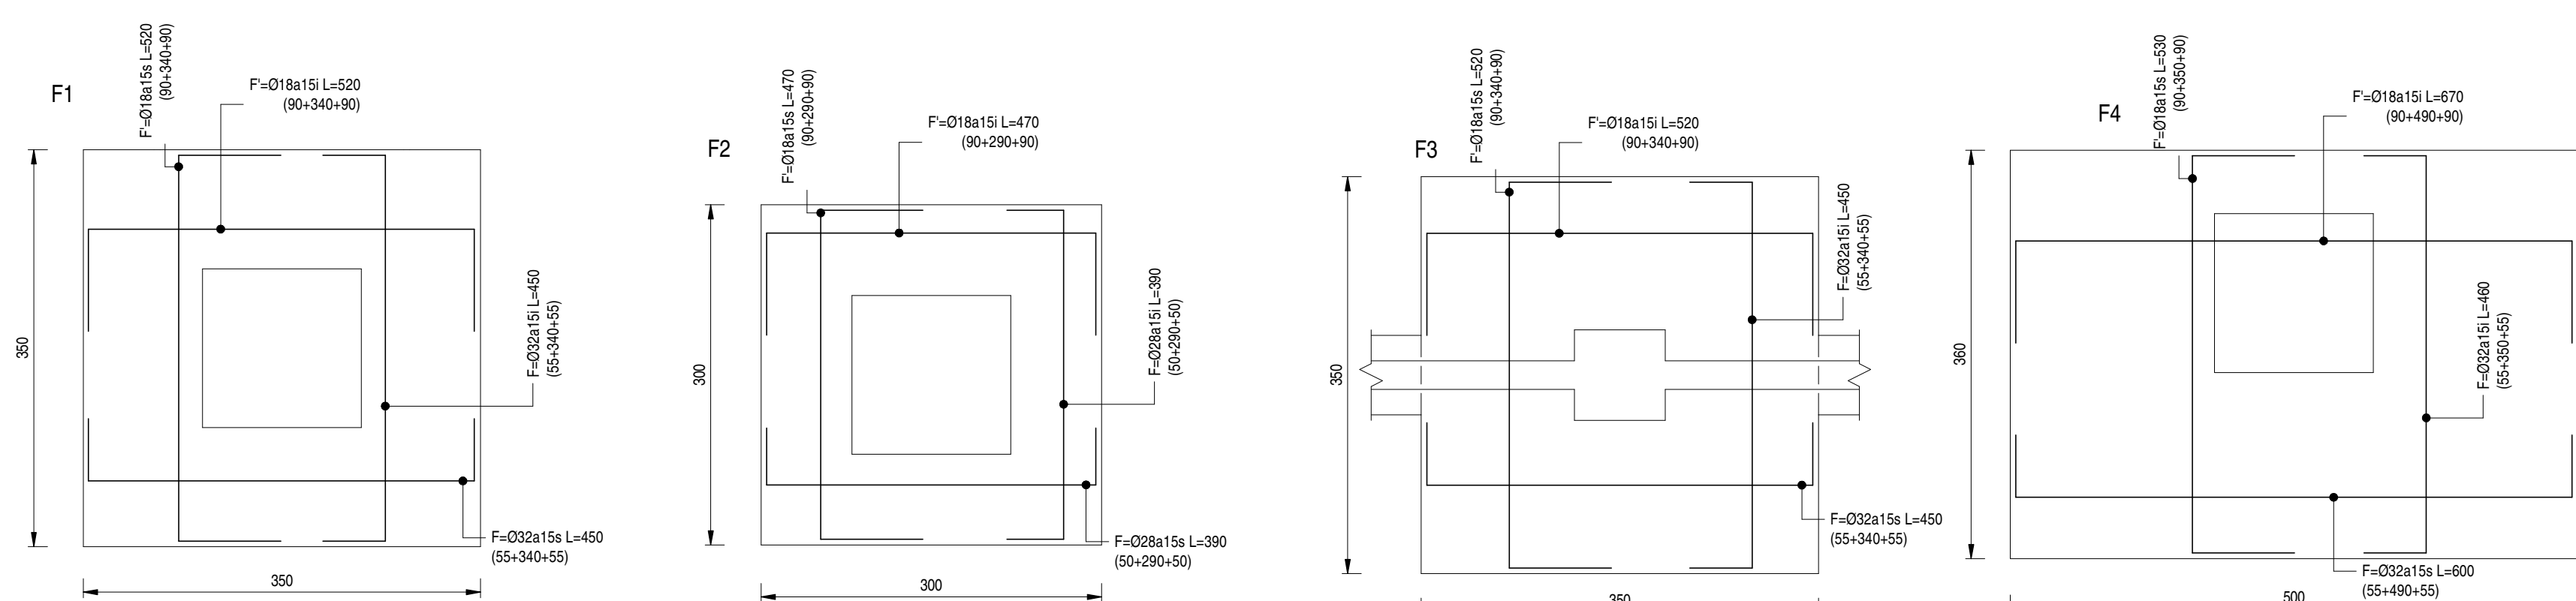


DETALLE TIPICO ARMADURA
ZAPATA F1
ESCALA 1 : 50

DETALLE TIPICO ARMADURA
ZAPATA F2
ESCALA 1 : 50


DETALLE TIPICO ARMADURA
ZAPATA F3
ESCALA 1 : 50

DETALLE TIPICO ARMADURA
ZAPATA F4
ESCALA 1 : 50


DETALLE TIPICO ARMADURA
ZAPATA F5
ESCALA 1 : 50

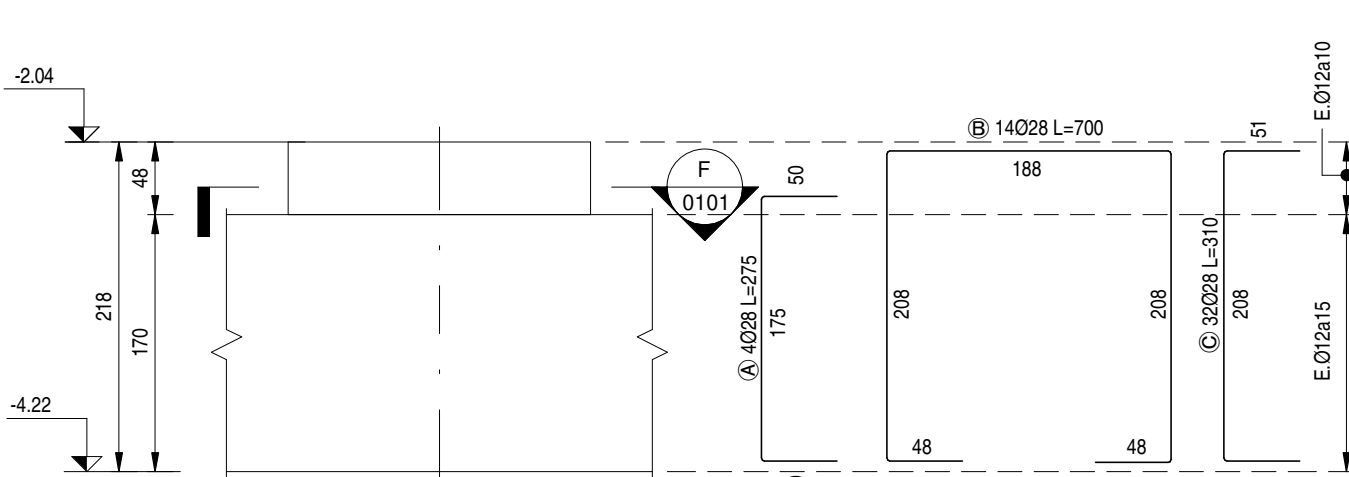


DETALLE TIPICO ARMADURA
PEDESTAL PD1
ESCALA 1 : 50

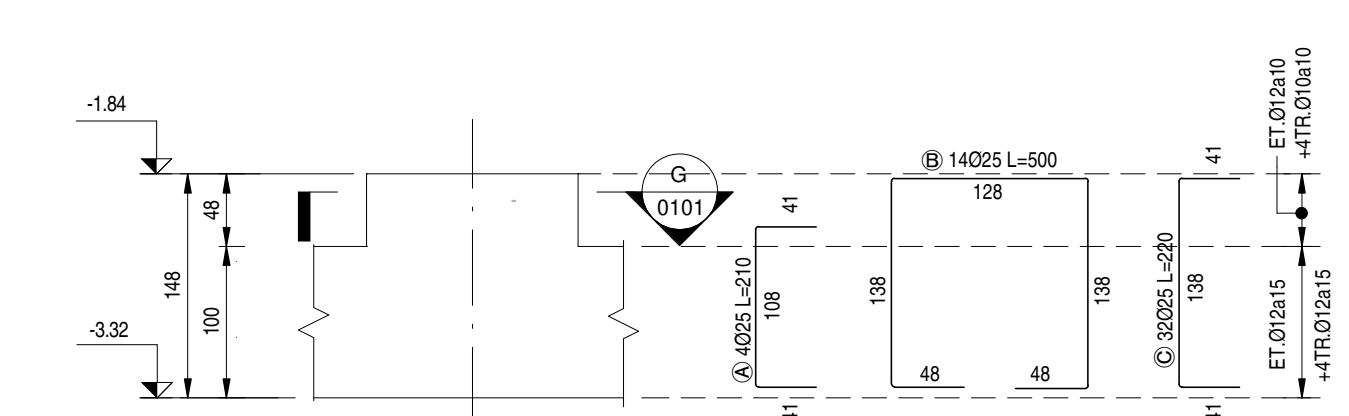


DETALLE TIPICO ARMADURA
PEDESTAL PD2
ESCALA 1 : 50

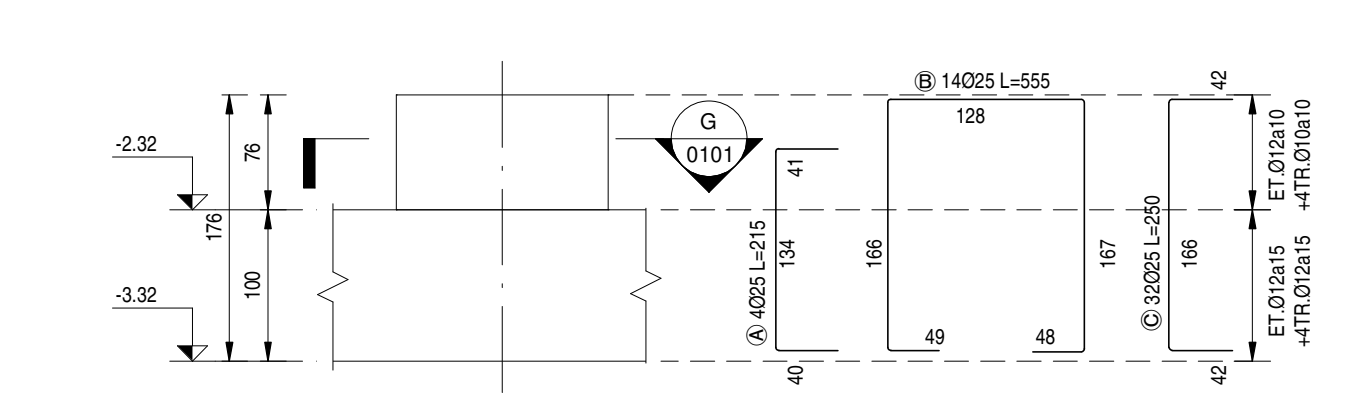


DETALLE TIPICO ARMADURA
PEDESTAL PD3
ESCALA 1 : 50

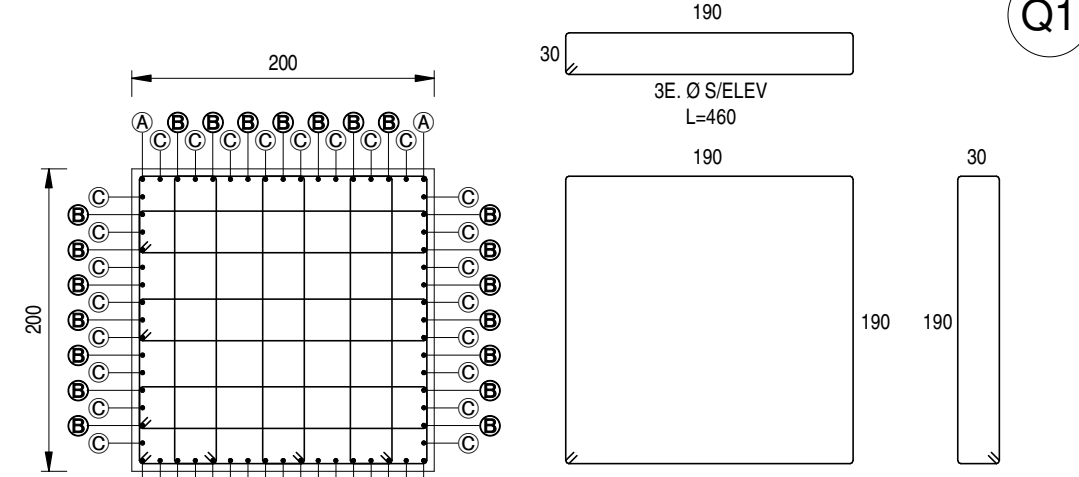


CORTE
ESC. 1 : 50

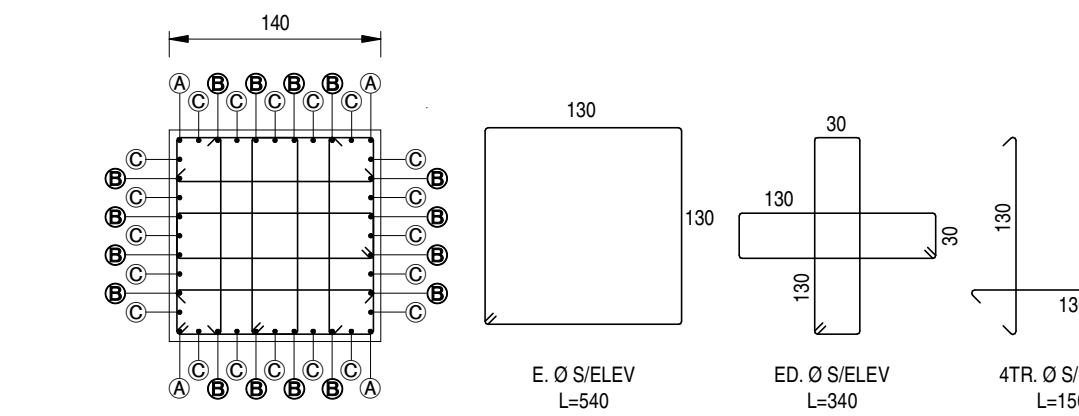


CORTE
ESC. 1 : 50

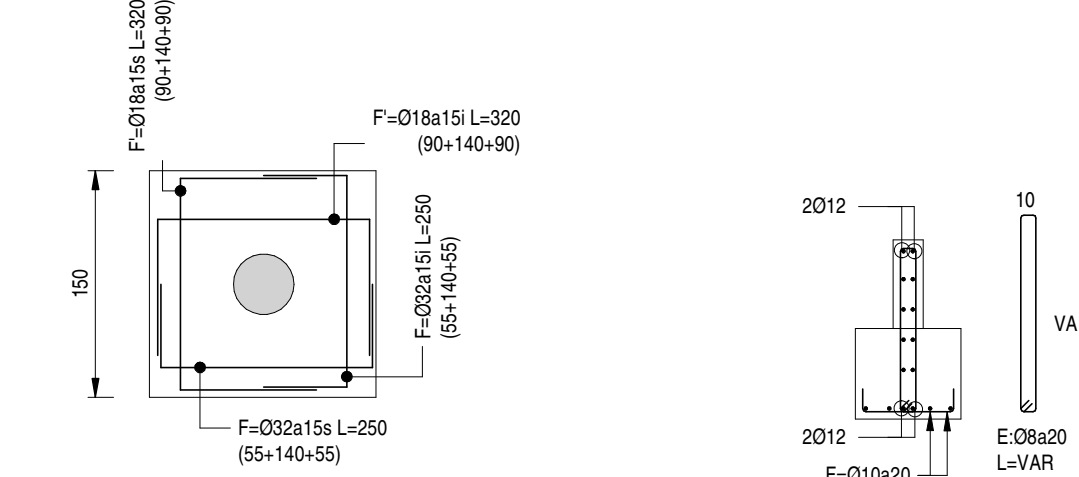


DETALLE TIPICO ARMADURA
ZAPATA F8
ESCALA 1 : 50

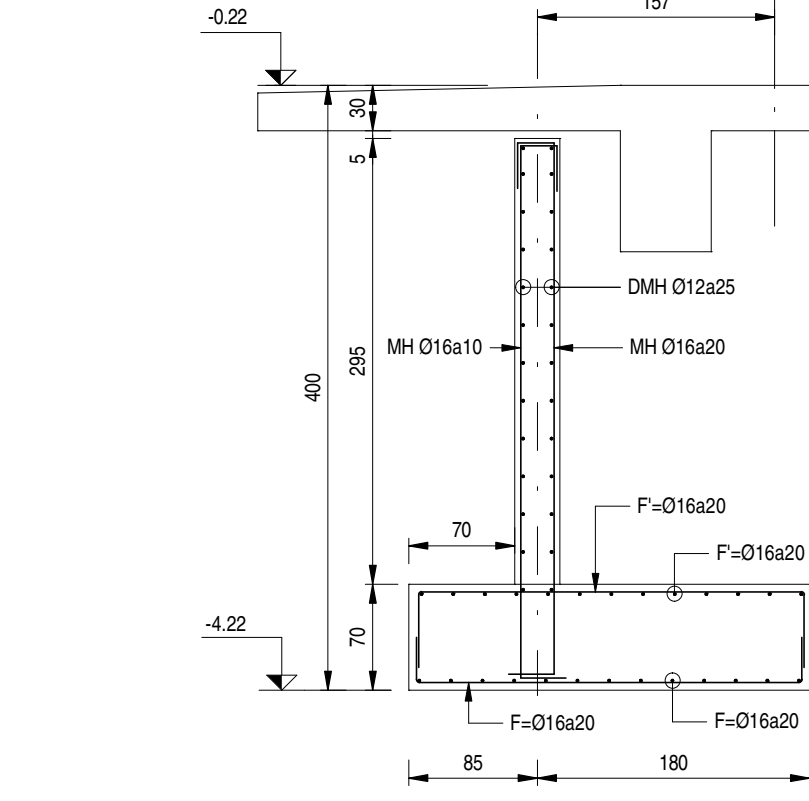


CORTE
ESC. 1 : 50

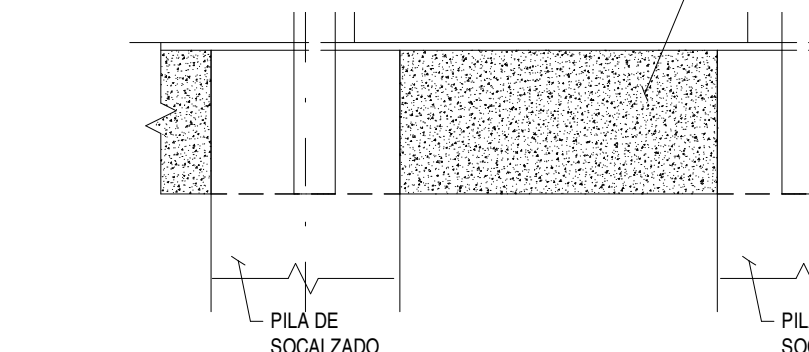

DETALLE TIPICO MURO DE
CONTENCIÓN ENTRE PILAS
ESCALA 1 : 50

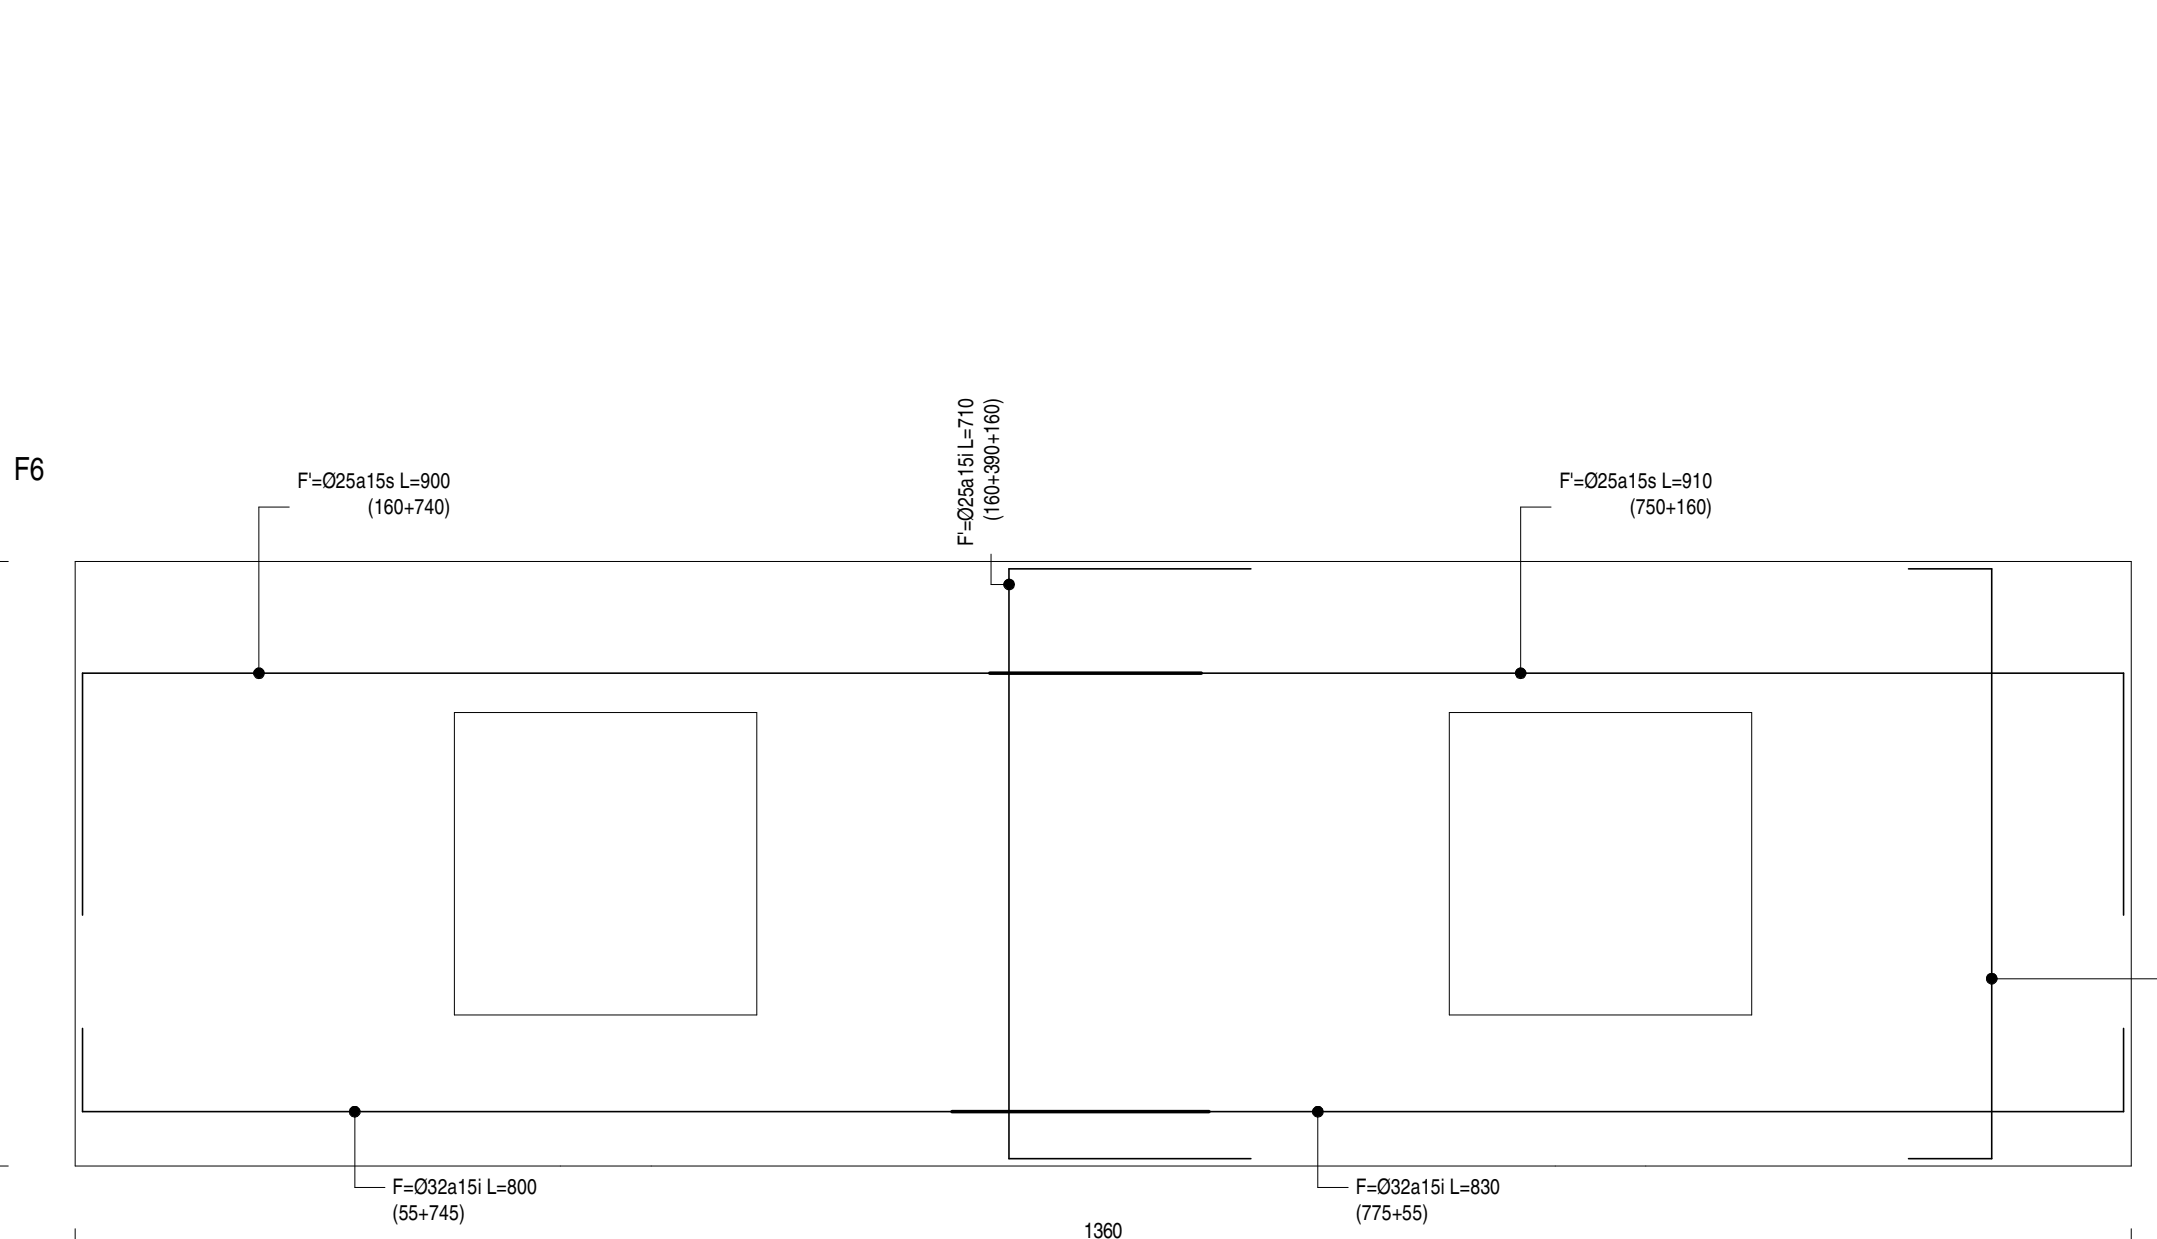

DETALLE TIPICO ARMADURA
ZAPATA F6
ESCALA 1 : 50

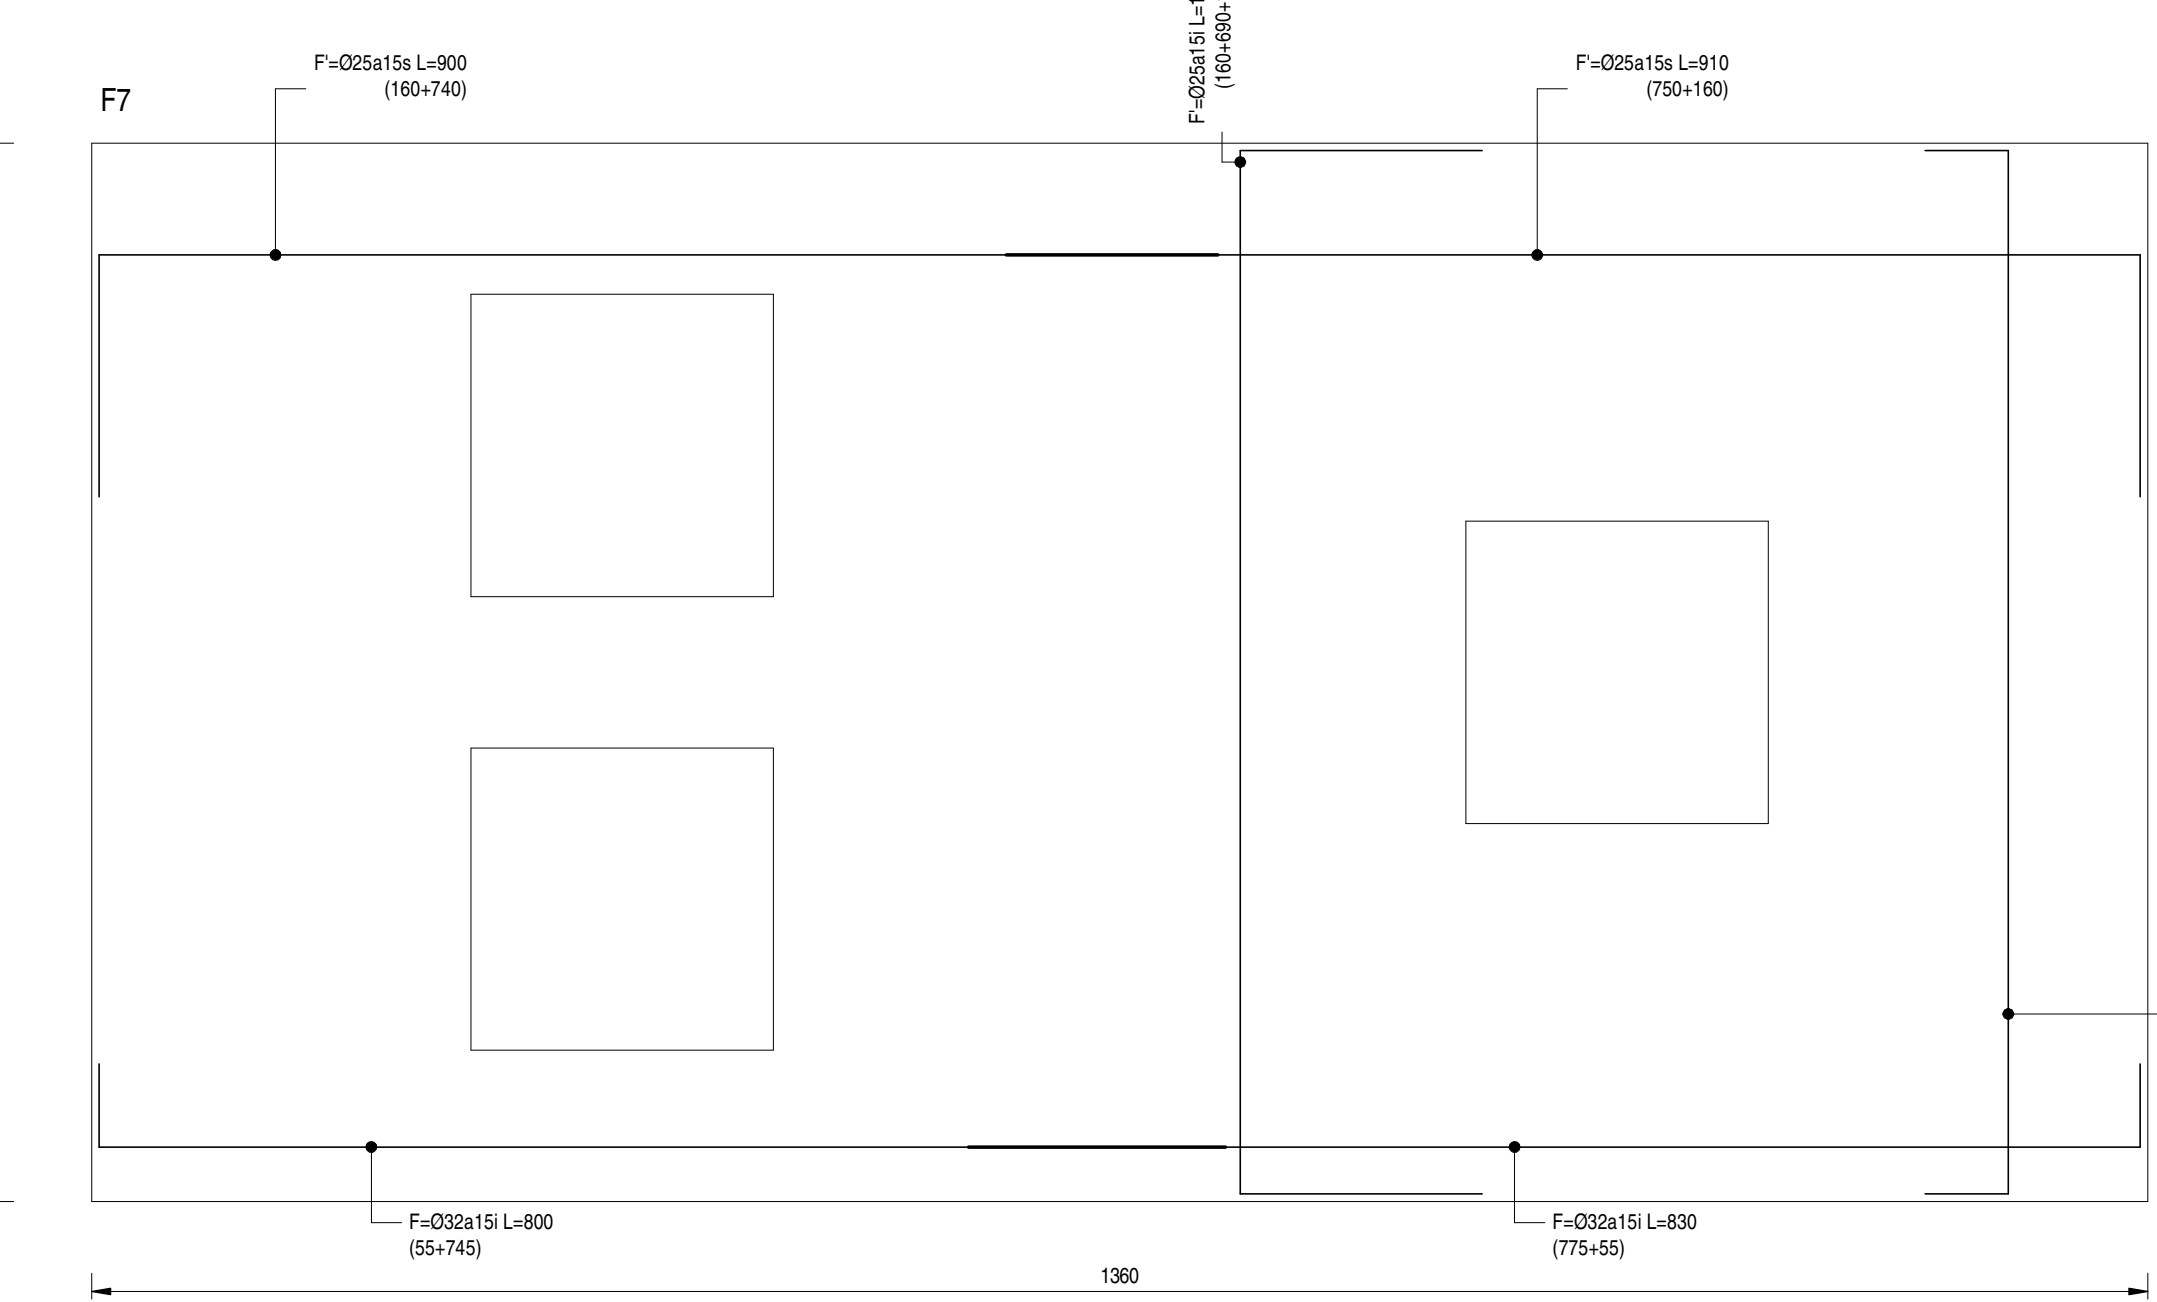

DETALLE TIPICO ARMADURA
ZAPATA F7
ESCALA 1 : 50

NOTA:
VER DETALLES DE PILAS P1, P2, P3 Y P4 EN
PLANO 18088-01-PL-EST-1101

FECHA	PROYECTO	CLIENTE	PROYECTO	FECHA
23.02.2020	RECUPERACION BASILICA DEL SALVADOR	CAR LUDERS	ENTREGA ETAPA DE DISEÑO	
12.06.2020	FUNDACIONES, LOSA BASE Y SISTEMA AISLAMIENTO SISMICO	CAR LUDERS	EMITIDO PARA REVISION DEL CLIENTE	
19.12.2019		CAR LUDERS	EMITIDO PARA REVISION DEL CLIENTE	
30.07.2019		CAR LUDERS	EMITIDO PARA PRESUPUESTO	
08.07.2019		CAR LUDERS	EMITIDO PARA PRESUPUESTO	
FECHA	DIBUJO/REVISOR	APROBADO	DETALLE	
18.08.01-PL-EST-0101				

SEISMIC PROTECTION TECHNOLOGIES

Estadío de Obras, Las Condes, Santiago - Chile
TELÉFONO: +56 2 2337 1100
CORREO: info@sirve.cl
WEB: www.sirve.cl

CAR LUDERS SCHWABENBERG
Ingeniero Civil E.C.

Dist. Ing. Technologic Hochschule Darmstadt
3.639.1723

PROYECTO	RECUPERACION BASILICA DEL SALVADOR	FECHA	23.02.2020
UBICACION	CALLE HUERFANOS 1796 - SANTIAGO	FECHA	23.02.2020
CLIENTE	FUNDACION BASILICA DEL SALVADOR	FECHA	23.02.2020
CONTENIDO	PLANTA DE FUNDACIONES y DETALLES DE ARMADURA DE FUNDACIONES	FECHA	23.02.2020