



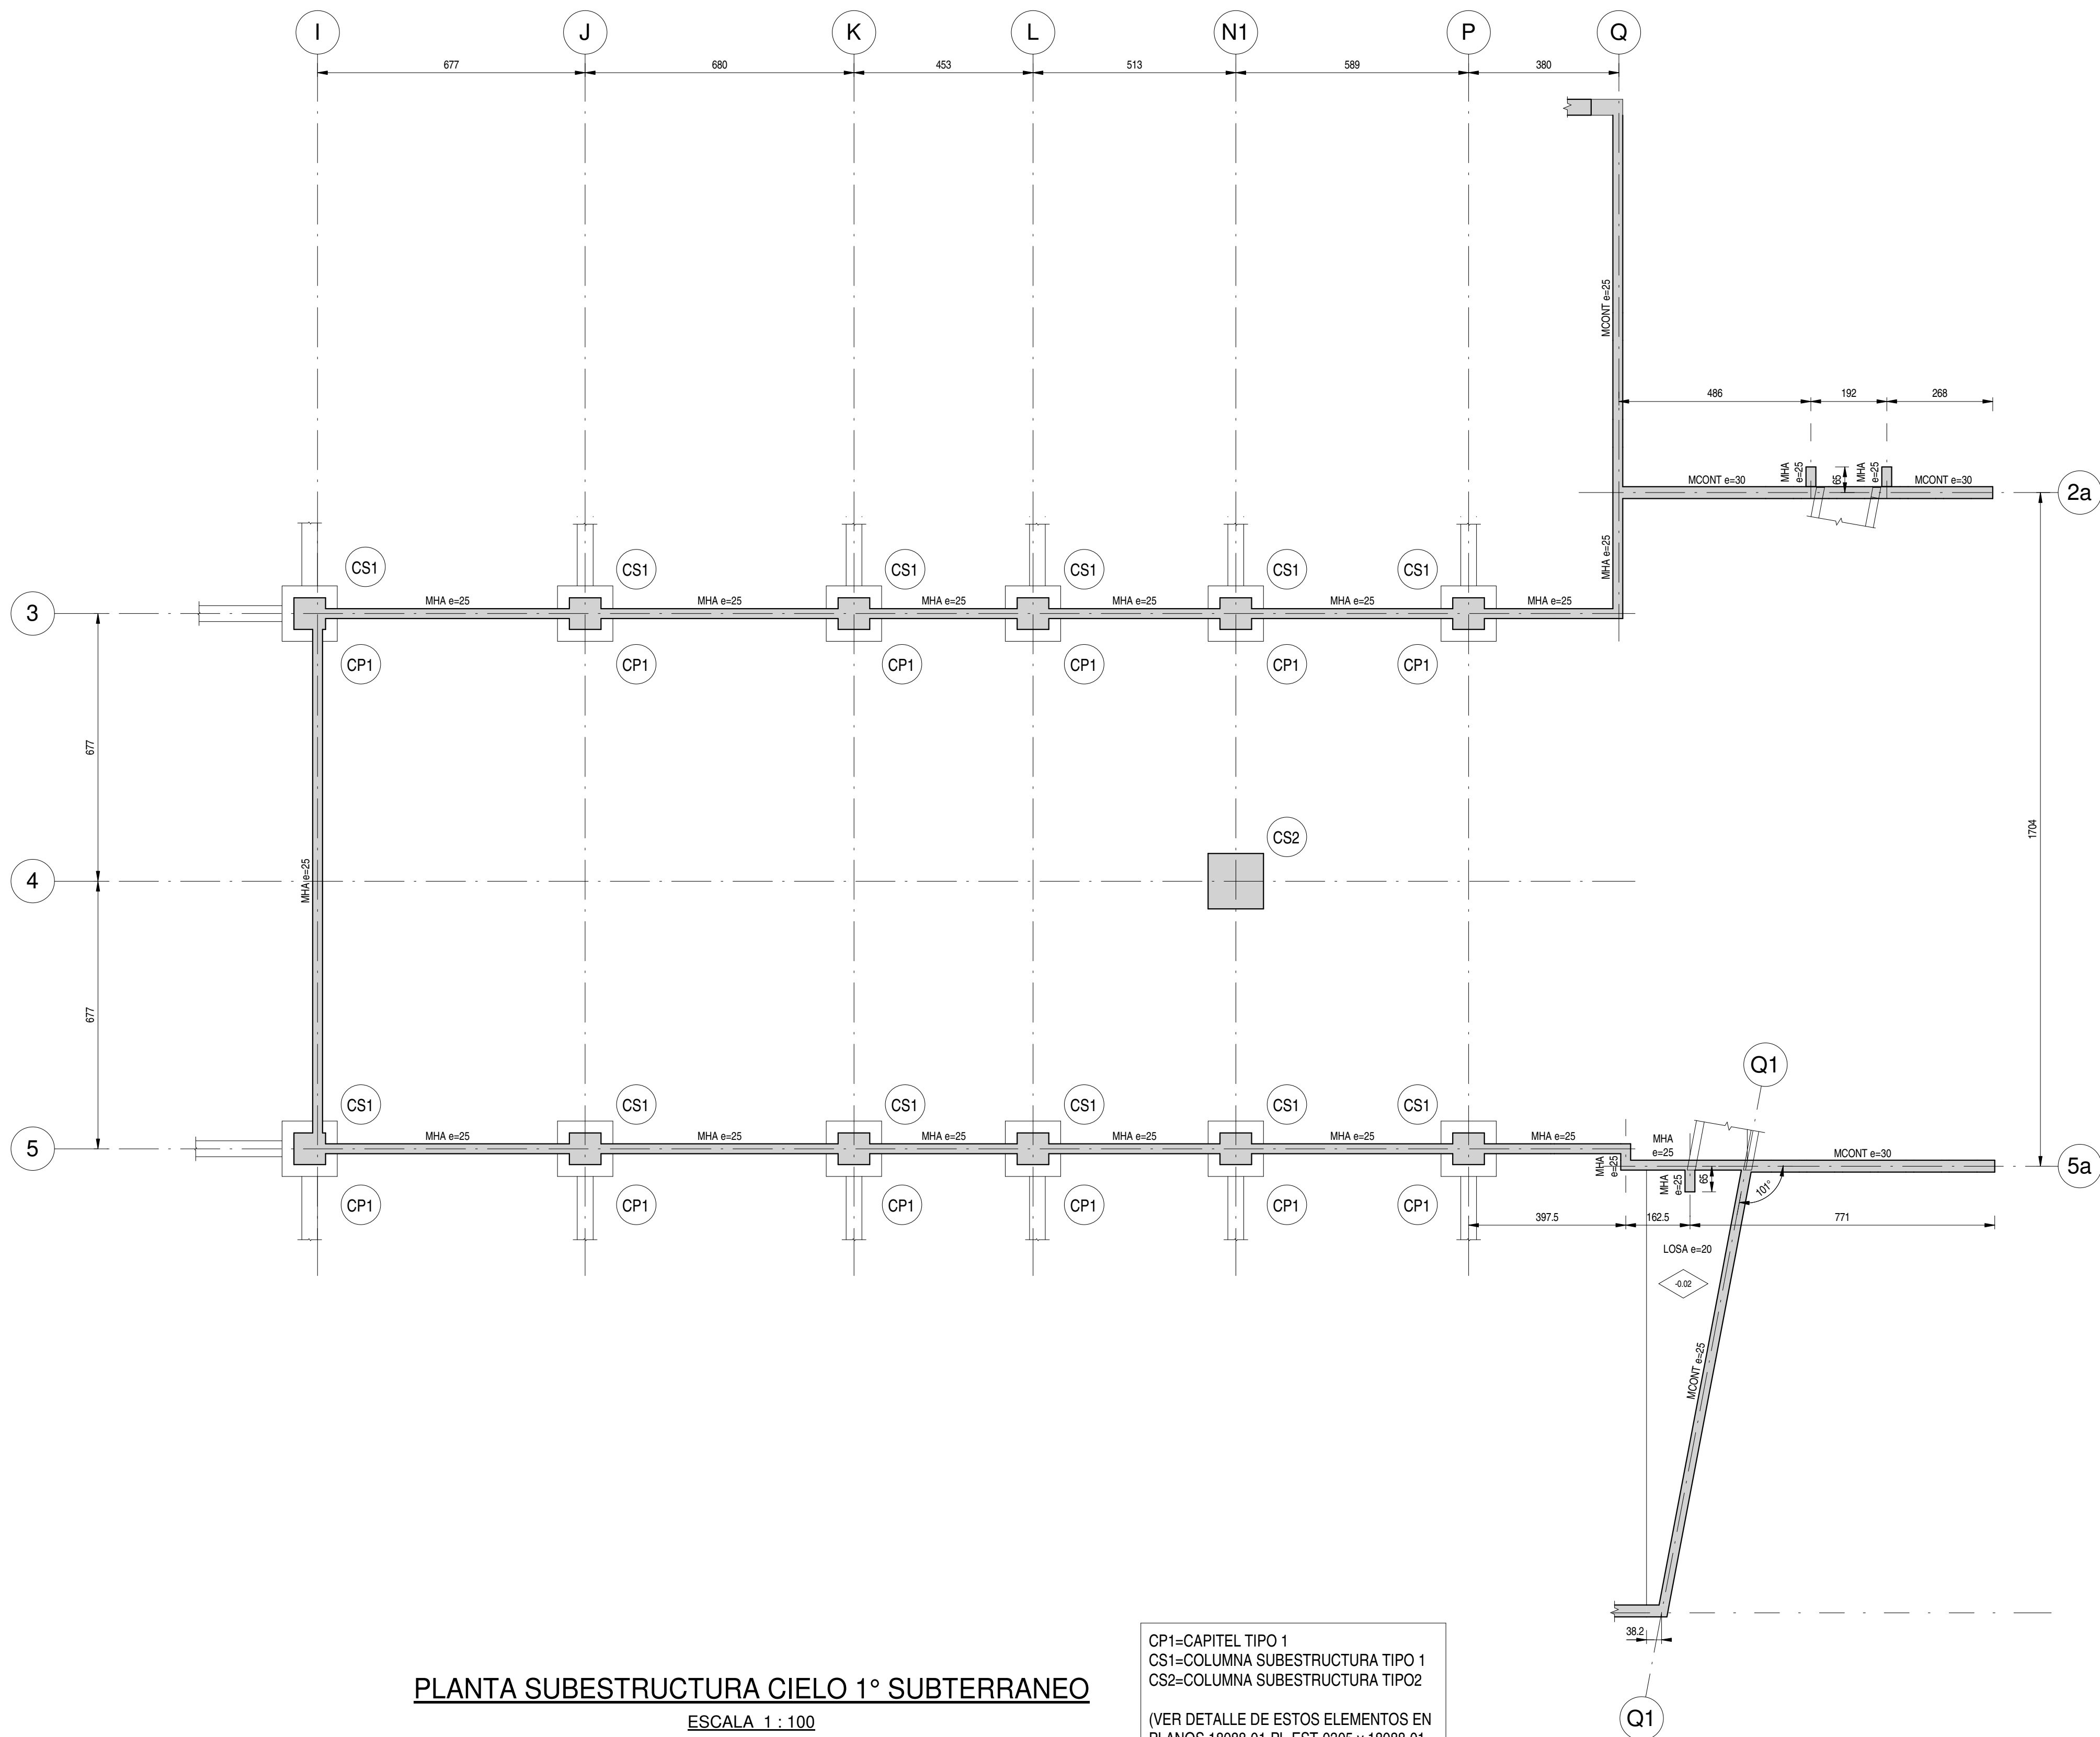

PLANTA SUBESTRUCTURA CIELO 1° SUBTERRANEO
ESCALA 1 : 100

CP1=CAPITEL TIPO 1
CS1=COLUMNA SUBESTRUCTURA TIPO 1
CS2=COLUMNA SUBESTRUCTURA TIPO 2
(VER DETALLE DE ESTOS ELEMENTOS EN PLANOS 18088-01-PL-EST-0305 y 18088-01-PL-EST-0306)

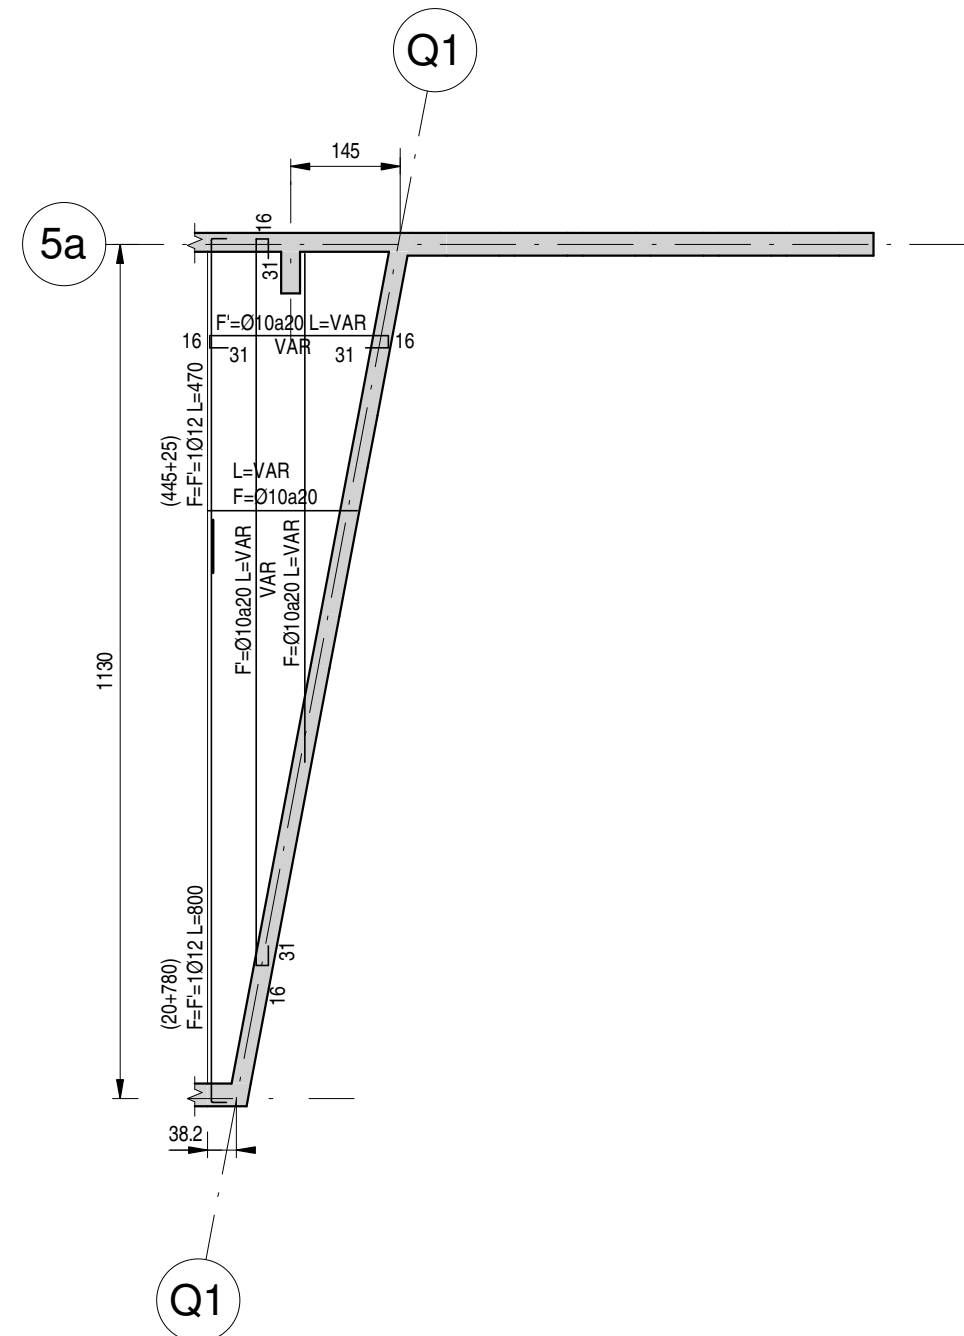

PLANTA ARMADURA DE LOSA NIVEL -0.02
ACCESO RAMPA PEATONAL
ESCALA 1 : 100

E	23.02.2020	L. SQUIBBA M. RENDIEL	CARL LUDERS	ENTREGA ETAPA DE DISEÑO
D	12.06.2020	L. SQUIBBA M. RENDIEL	CARL LUDERS	EMITIDO PARA REVISION DEL CLIENTE
C	19.12.2019	S. SAEZ M. RENDIEL	CARL LUDERS	EMITIDO PARA REVISION DEL CLIENTE
B	30.07.2019	S. SAEZ M. RENDIEL	CARL LUDERS	EMITIDO PARA PRESUPUESTO
A	08.07.2019	S. SAEZ M. RENDIEL	CARL LUDERS	EMITIDO PARA PRESUPUESTO
Nº	FECHA	DIBUJO/REVISO	APROBO	DETALLE
PROYECTO DE CÁLCULO ESTRUCTURAL				
 SEISMIC PROTECTION TECHNOLOGIES Estudio de Obras, Las Condes, Santiago - Chile TELÉFONO: +56 2 21071100 CONTACTO: info@sirve.cl WEB: www.sirve.cl  CARL LUDERS SCHWARZENBERG Ingeniero Civil Dipl. Ing. Technische Hochschule Darmstadt 5.6.79.1923				
PROYECTO RECUPERACION BASILICA DEL SALVADOR				
FUNDACIONES, LOSA BASE Y SISTEMA AISLAMIENTO SÍSMICO				
UBICACION CALLE HUERFANOS 1796 - SANTIAGO				
CLIENTE FUNDACION BASILICA DEL SALVADOR				
RUT: 65.148.985-6				
CONTENIDO PLANTA DE SUBESTRUCTURA CIELO 1° SUBTERRANEO				REVISION
				E
CODIGO DEL DOCUMENTO 18088-01-PL-EST-0102		FORMATO A3	ESCALA 1:100	FECHA 23.02.2020