




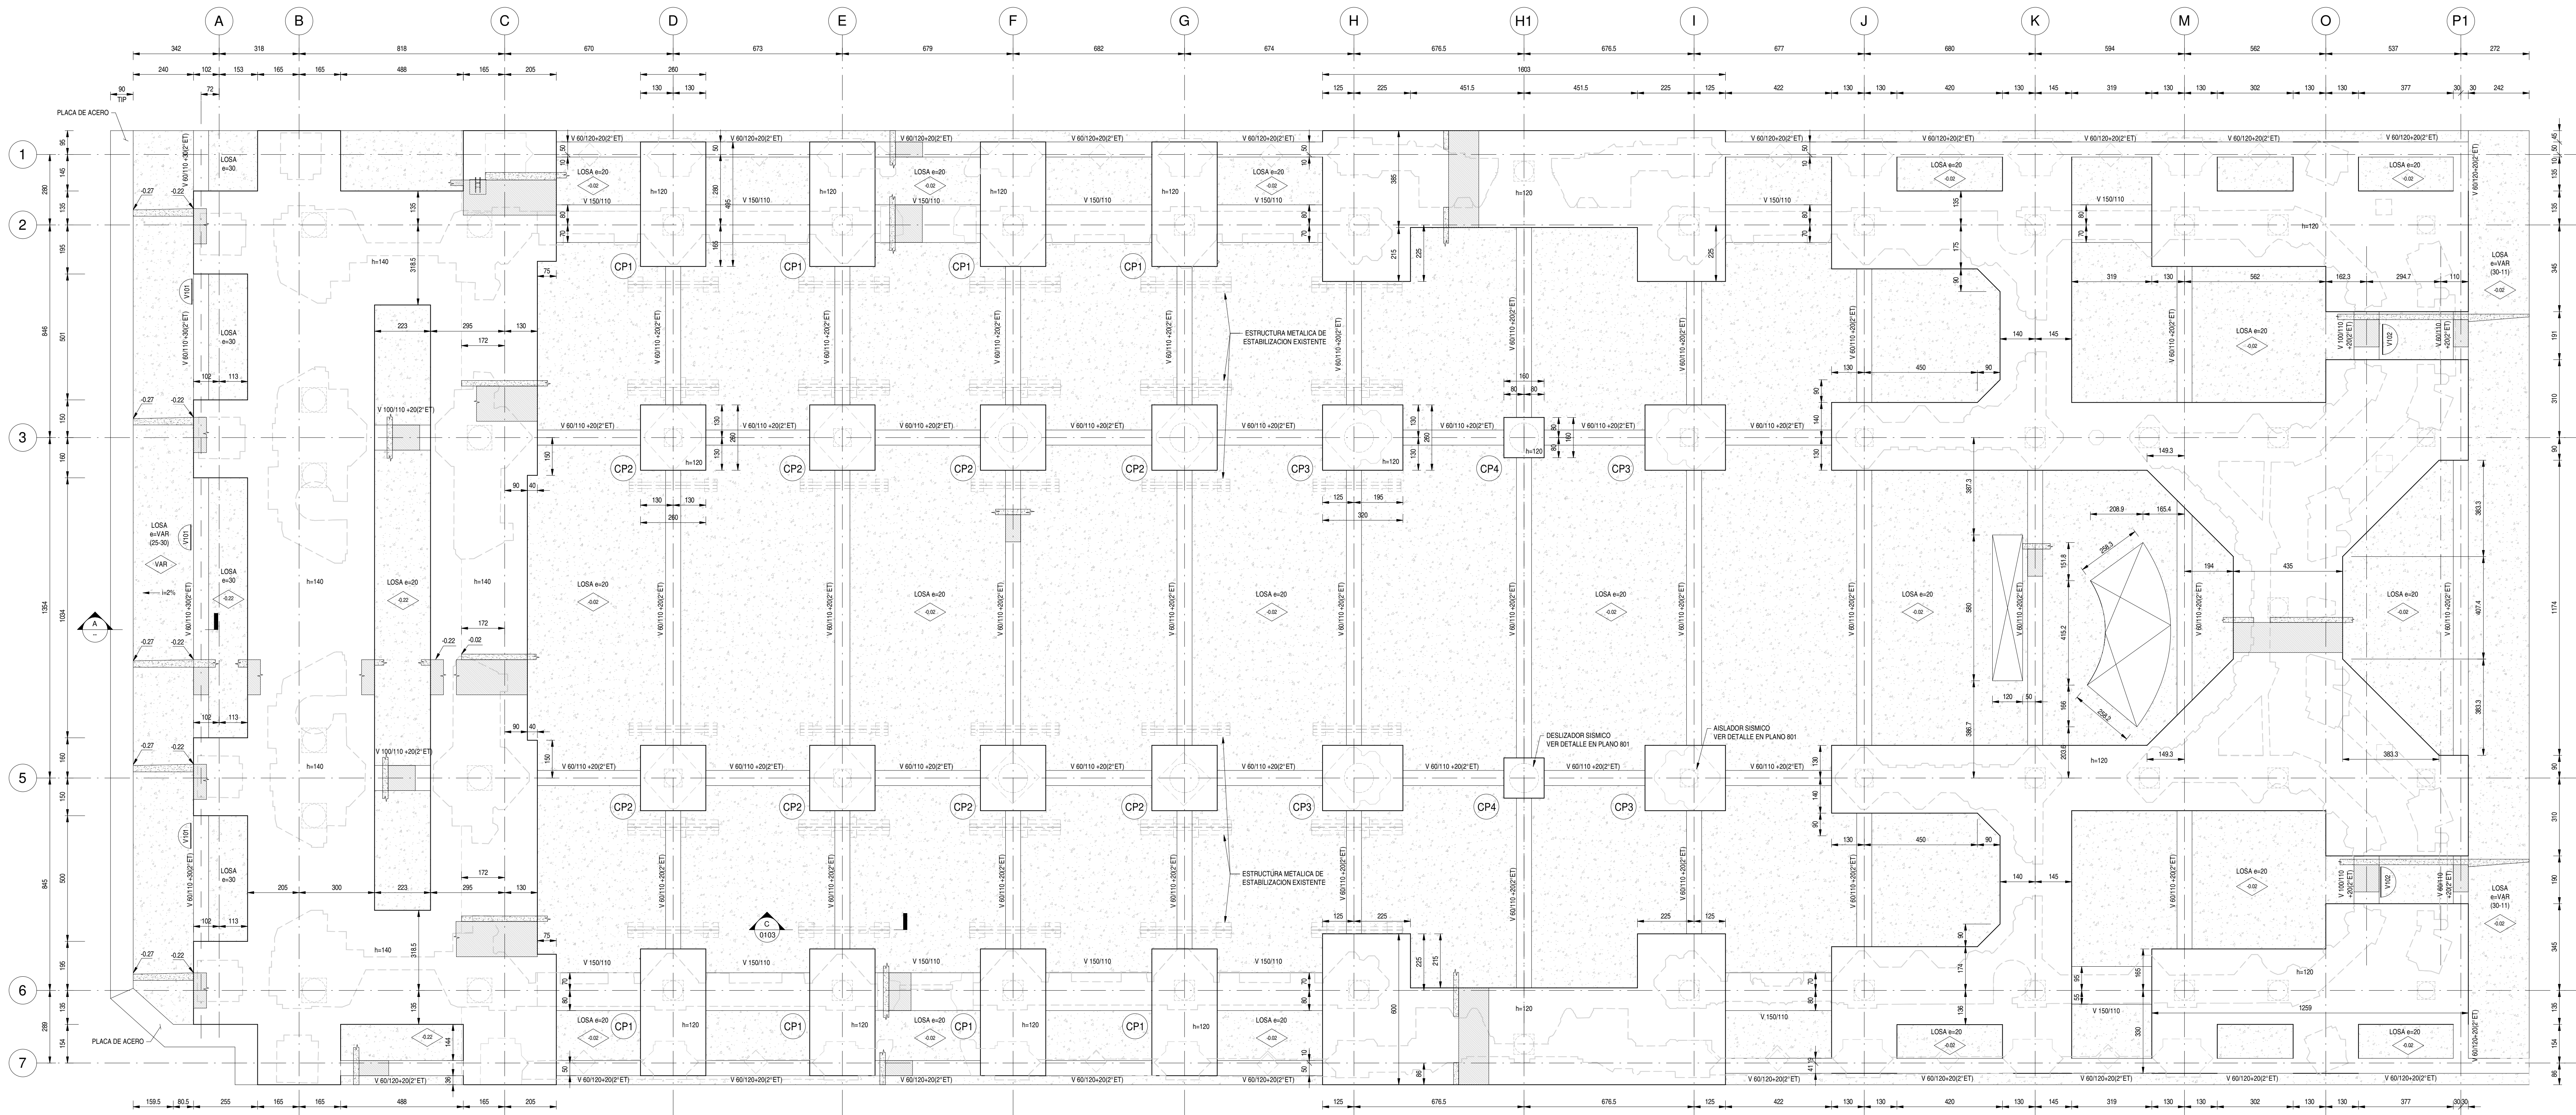

LOSA e=20 NIVEL SUPERIOR -0.02 (S.I.C.)
PLANTA DE ESTRUCTURA CIELO 1º SUBTERRANEO
ESCALA 1 : 100

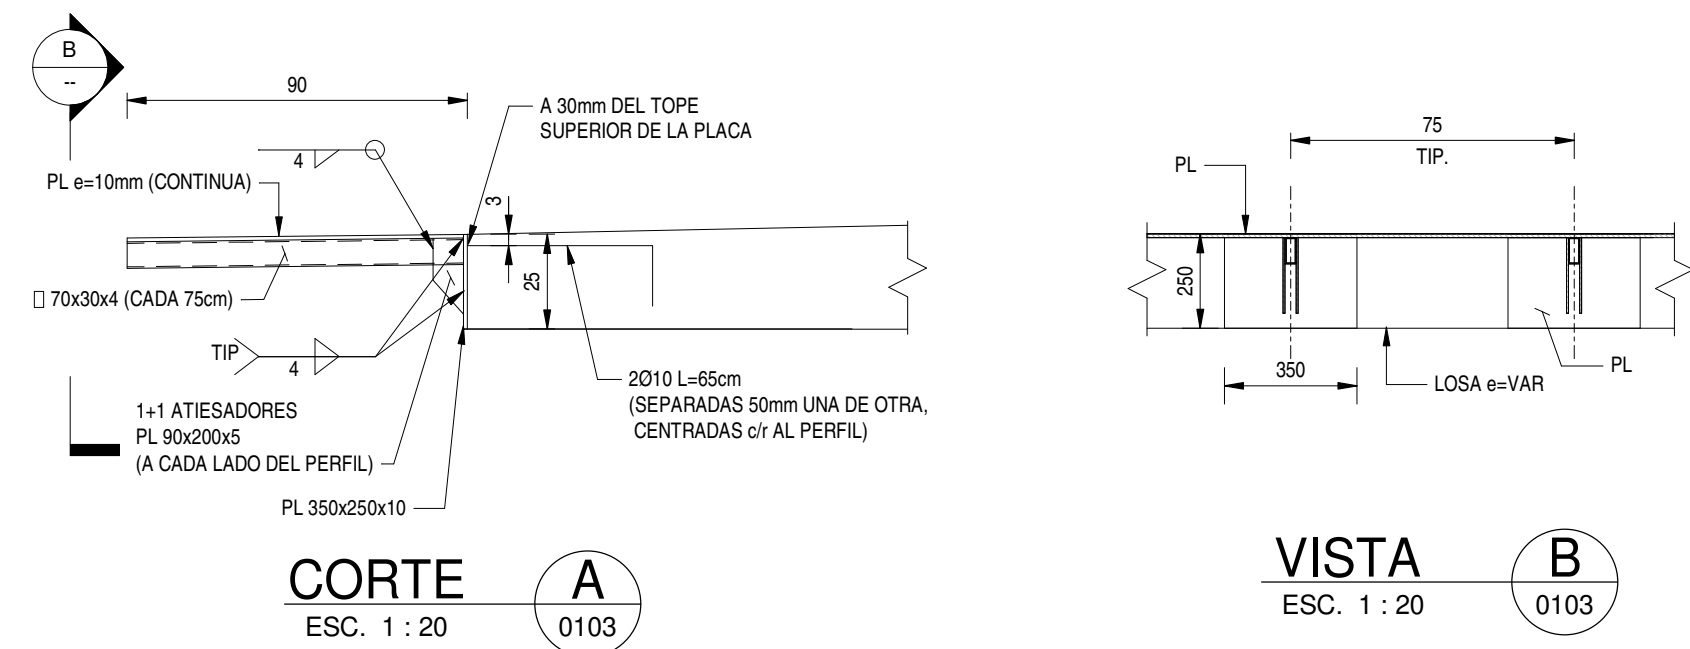

SECUENCIA CONSTRUCTIVA DE SOSTENIMIENTO DE ESTRUCTURA DE ESTABILIZACION EXISTENTE

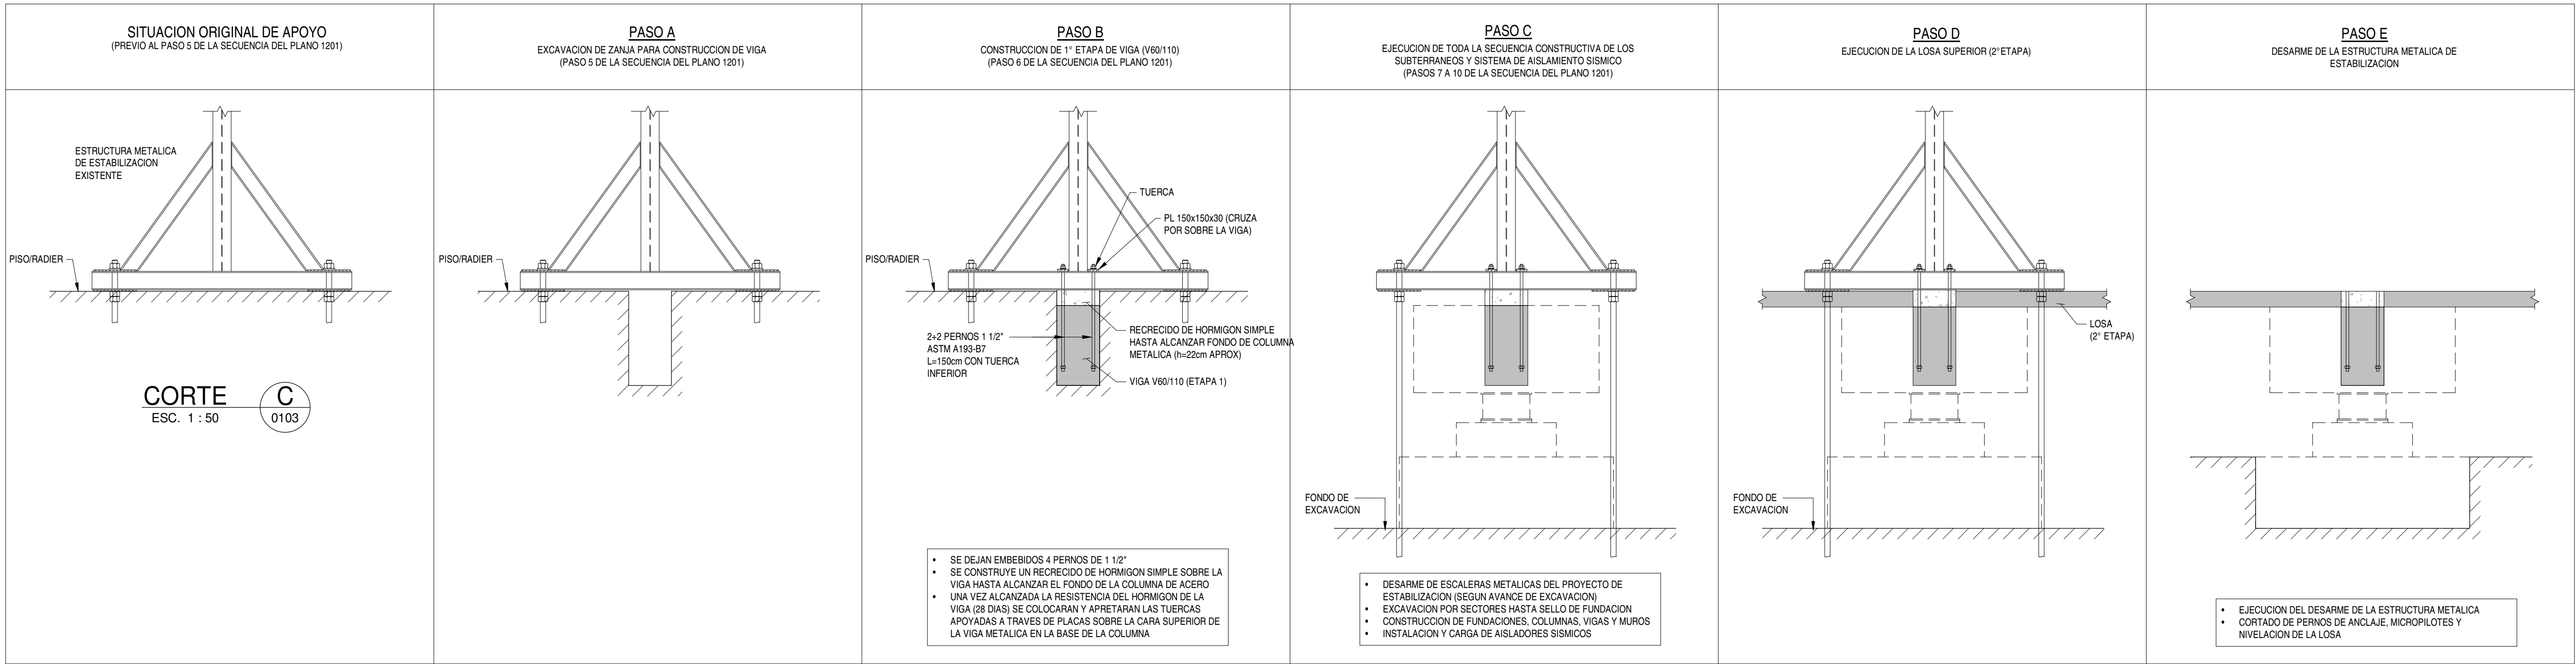

H	23.02.2020	L. SQUIERA M. RENDIL	CARL LUDERS	ENTREGA ETAPA DE DISEÑO
G	18.12.2020	L. SQUIERA M. RENDIL	CARL LUDERS	SE MODIFICA LO INDICADO
F	13.08.2020	L. SQUIERA M. RENDIL	CARL LUDERS	SE MODIFICA LO INDICADO
E	12.06.2020	L. SQUIERA M. RENDIL	CARL LUDERS	EMITIDO PARA REVISION DEL CLIENTE
D	19.12.2019	S. SAIZ M. RENDIL	CARL LUDERS	EMITIDO PARA REVISION DEL CLIENTE
Nº	FECHA	DIBUJO/REVISO	APROBÓ	DETALLE
PROYECTADO				
PROYECTO DE CÁLCULO ESTRUCTURAL				
PROYECTO RECUPERACION BASILICA DEL SALVADOR FUNDACIONES, LOSA BASE Y SISTEMA AISLAMIENTO SISMICO				
UBICACION CALLE HUERFANOS 1796 - SANITIAO				
CLIENTE FUNDACION BASICA DEL SALVADOR RUT: 65.165.980-A				
CONTENIDO PLANTA DE ESTRUCTURA CIELO 1º SUBTERRANEO				REVISION H
CODIGO DEL DOCUMENTO 18088-01-PL-EST-0103	FORMATO A0	ESCALA 1:100	FECHA 23.02.2020	