
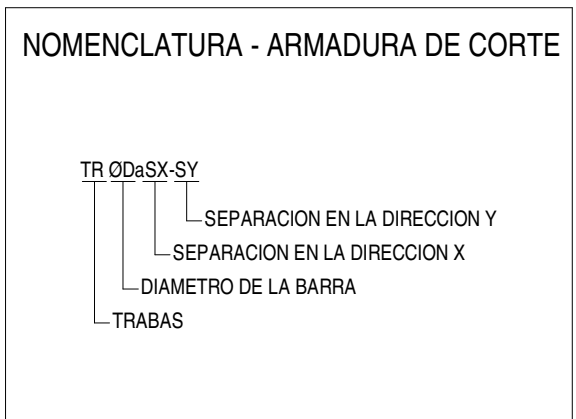
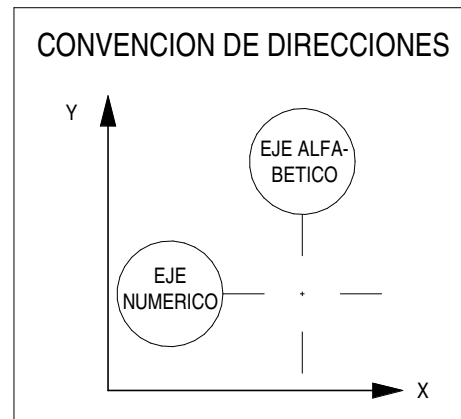


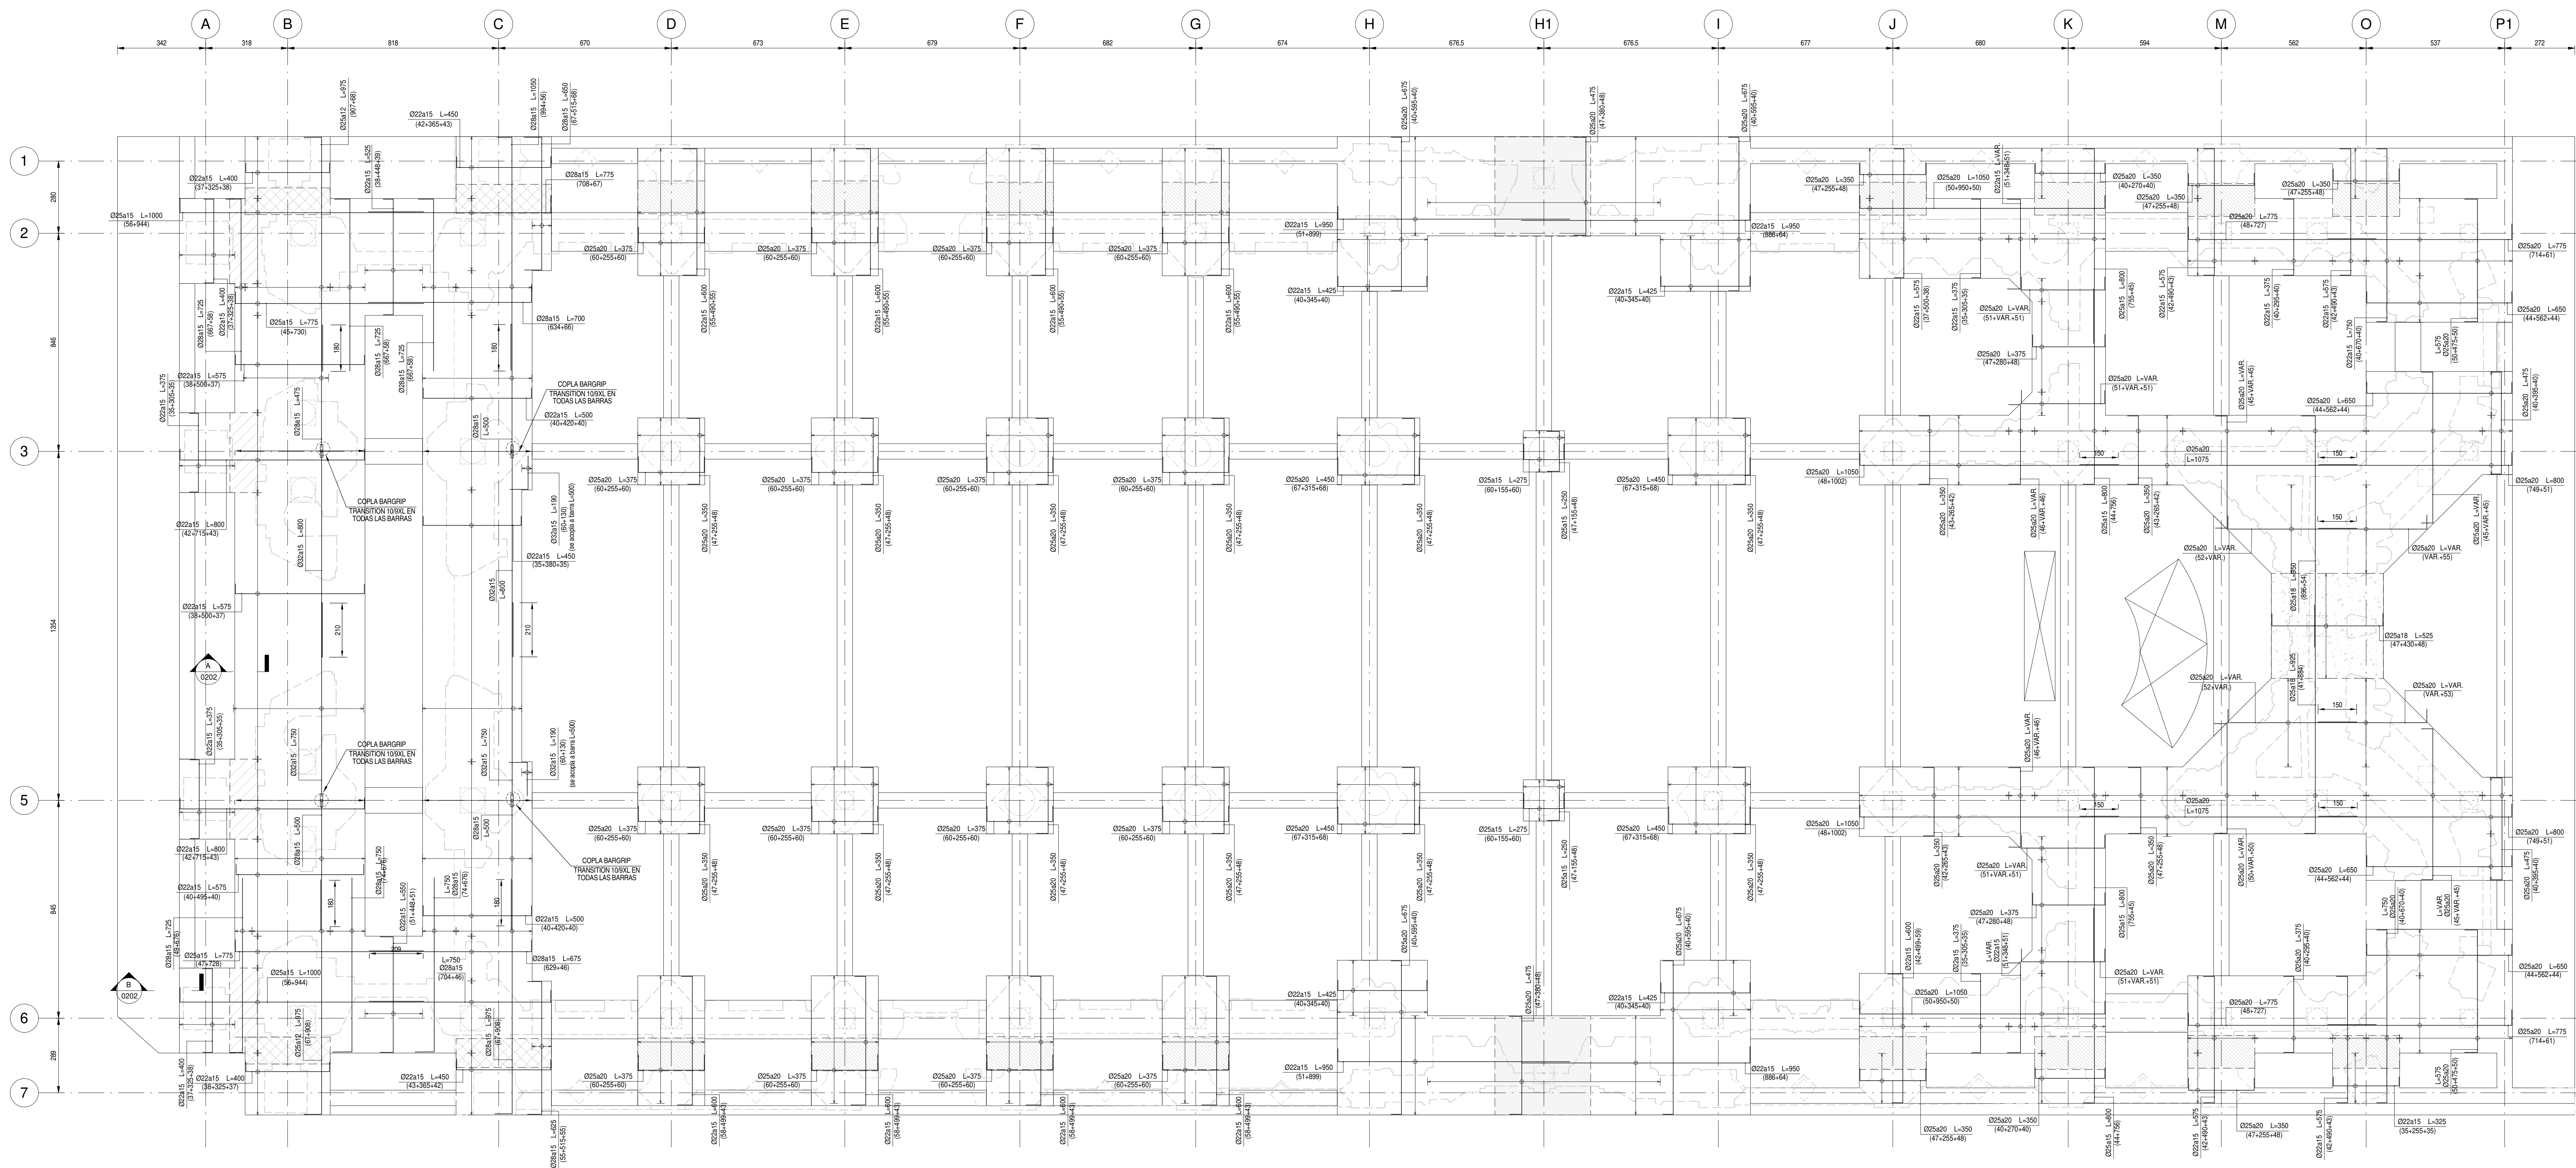

ETAPAS DE HORMIGONADO SEGUN DEFINIDO EN PLANO 103 Y CORTES

PLANTA ARMADURA INFERIOR Y DE CORTE DE LOSA
CIELO 1° SUBTERRANEO - 1° ETAPA
ESCALA 1 : 100

- NOTAS:
1. LAS COPLAS ESPECIFICADAS EN ESTE PLANO SERÁN TIPO 2 SEGÚN CLASIFICACIÓN ACI318-08, Y SERÁN DEL MODELO BARGRIP XL DE LA MARCA BARGRIP.
 2. LA INSTALACIÓN DE LAS COPLAS DEBERÁ REALIZARSE POR PERSONAL CALIFICADO, USANDO EL EQUIPAMIENTO Y PROCEDIMIENTOS ESPECIFICADOS POR EL PROVEEDOR.
 3. NO SE PODRÁ USAR OTRA MARCA O TIPO DE COPLAS, QUE NO HAYAN SIDO PREVIAMENTE AUTORIZADAS POR EL INGENIERO CALCULISTA DEL PROYECTO.

F	23.02.2020	L. SQUIERBA M. RENDIL	CARL LUDERS	ENTREGA ETAPA DE DISEÑO
E	18.12.2020	L. SQUIERBA M. RENDIL	CARL LUDERS	SE MODIFICA LO INDICADO
D	12.06.2020	L. SQUIERBA M. RENDIL	CARL LUDERS	EMITIDO PARA REVISIÓN DEL CLIENTE
C	19.12.2019	S. SÁEZ M. RENDIL	CARL LUDERS	EMITIDO PARA REVISIÓN DEL CLIENTE
B	05.09.2019	S. SÁEZ M. RENDIL	CARL LUDERS	EMITIDO PARA REVISIÓN DEL CLIENTE
Nº	FECHA	DIBUJO/REVISO	APROBÓ	DETALLE
PROYECTO DE CÁLCULO ESTRUCTURAL				
PROYECTO RECUPERACIÓN BASÍLICA DEL SALVADOR				
FUNDACIONES, LOSA BASE Y SISTEMA AISLAMIENTO SÍSMICO				
UBICACIÓN CALLE HUERFANOS 1796 - SAN TIAGO				
GIRTE FUNDACIÓN BASÍLICA DEL SALVADOR				
RUT 55, PAR 1005A				
CONTENIDO PLANTA ARMADURA INFERIOR DE LOSA CIELO 1° SUBTERRANEO - 1° ETAPA				
CÓDIGO DEL DOCUMENTO 18088-01-PL-EST-0201				REVISIÓN F
FORMATO AD				FECHA 23.02.2020
ESCALA 1:100				