


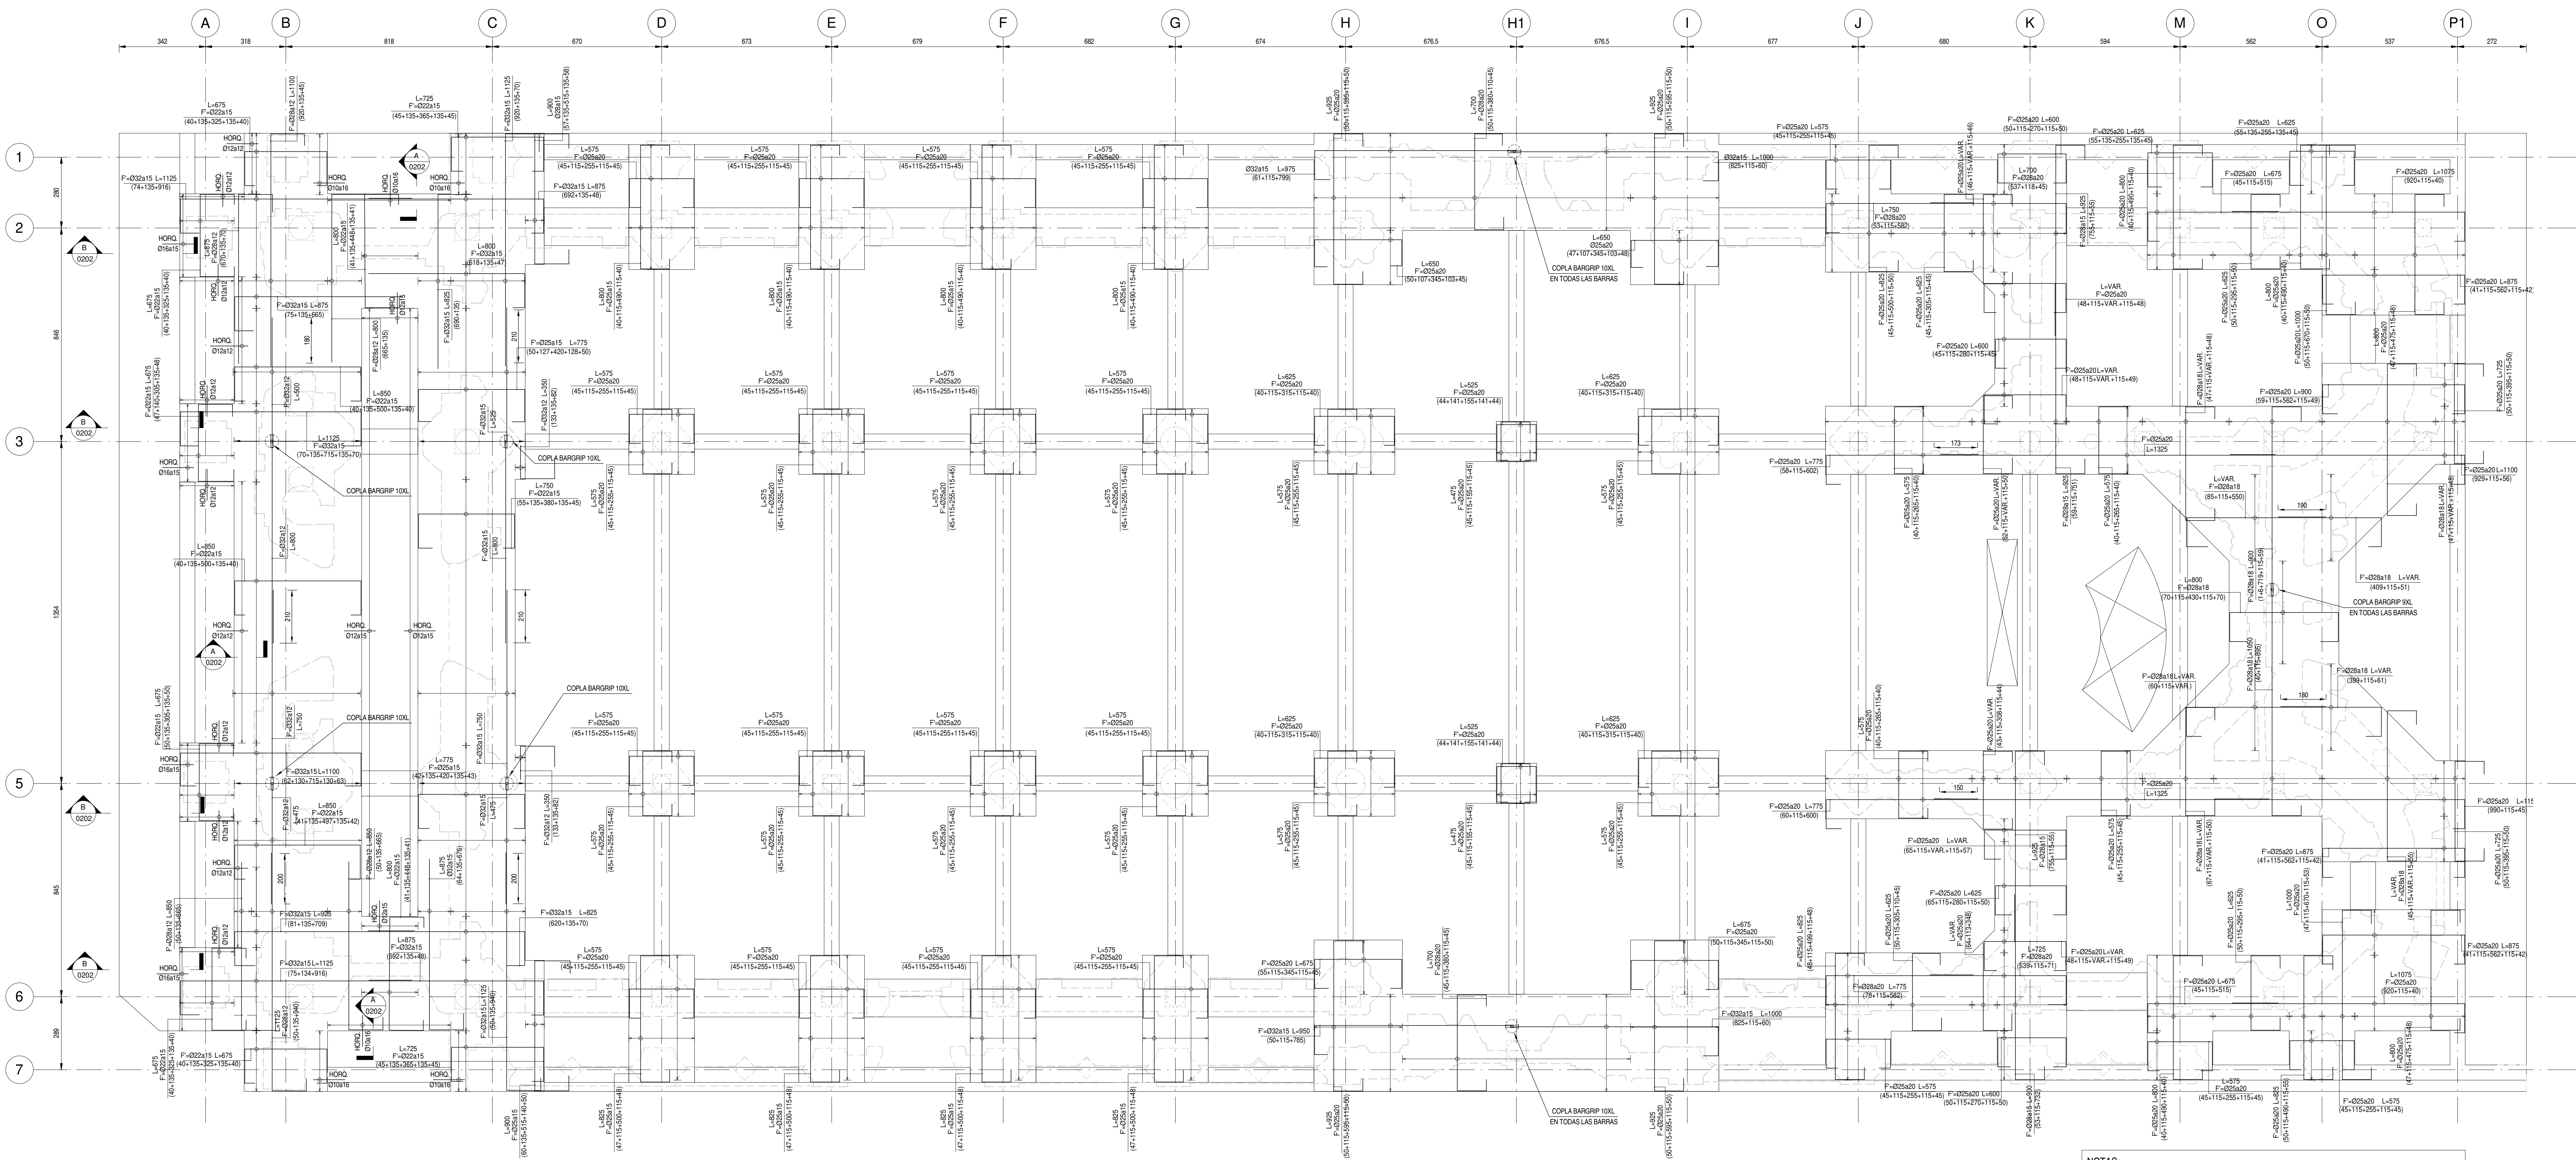


ETAPAS DE HORMIGONADO SEGUN DEFINIDO EN PLANO 103 Y CORTES

**PLANTA ARMADURA SUPERIOR DE LOSA CIELO 1° SUBTERRANEO - 1° ETAPA**


ESCALA 1 : 100

- NOTAS:
1. LAS COPLAS ESPECIFICADAS EN ESTE PLANO SERÁN TIPO 2 SEGUN CLASIFICACION ACI318-08, Y SERÁN DEL MODELO BARGRIP XL DE LA MARCA BARSPLICE.
  2. LA INSTALACION DE LAS COPLAS DEBERÁ REALIZARSE POR PERSONAL CALIFICADO, USANDO EL EQUIPAMIENTO Y PROCEDIMIENTOS ESPECIFICADOS POR EL PROVEEDOR.
  3. NO SE PODRÁ USAR OTRA MARCA O TIPO DE COPLAS, QUE NO HAYAN SIDO PREVIAMENTE AUTORIZADAS POR EL INGENIERO CALCULISTA DEL PROYECTO.

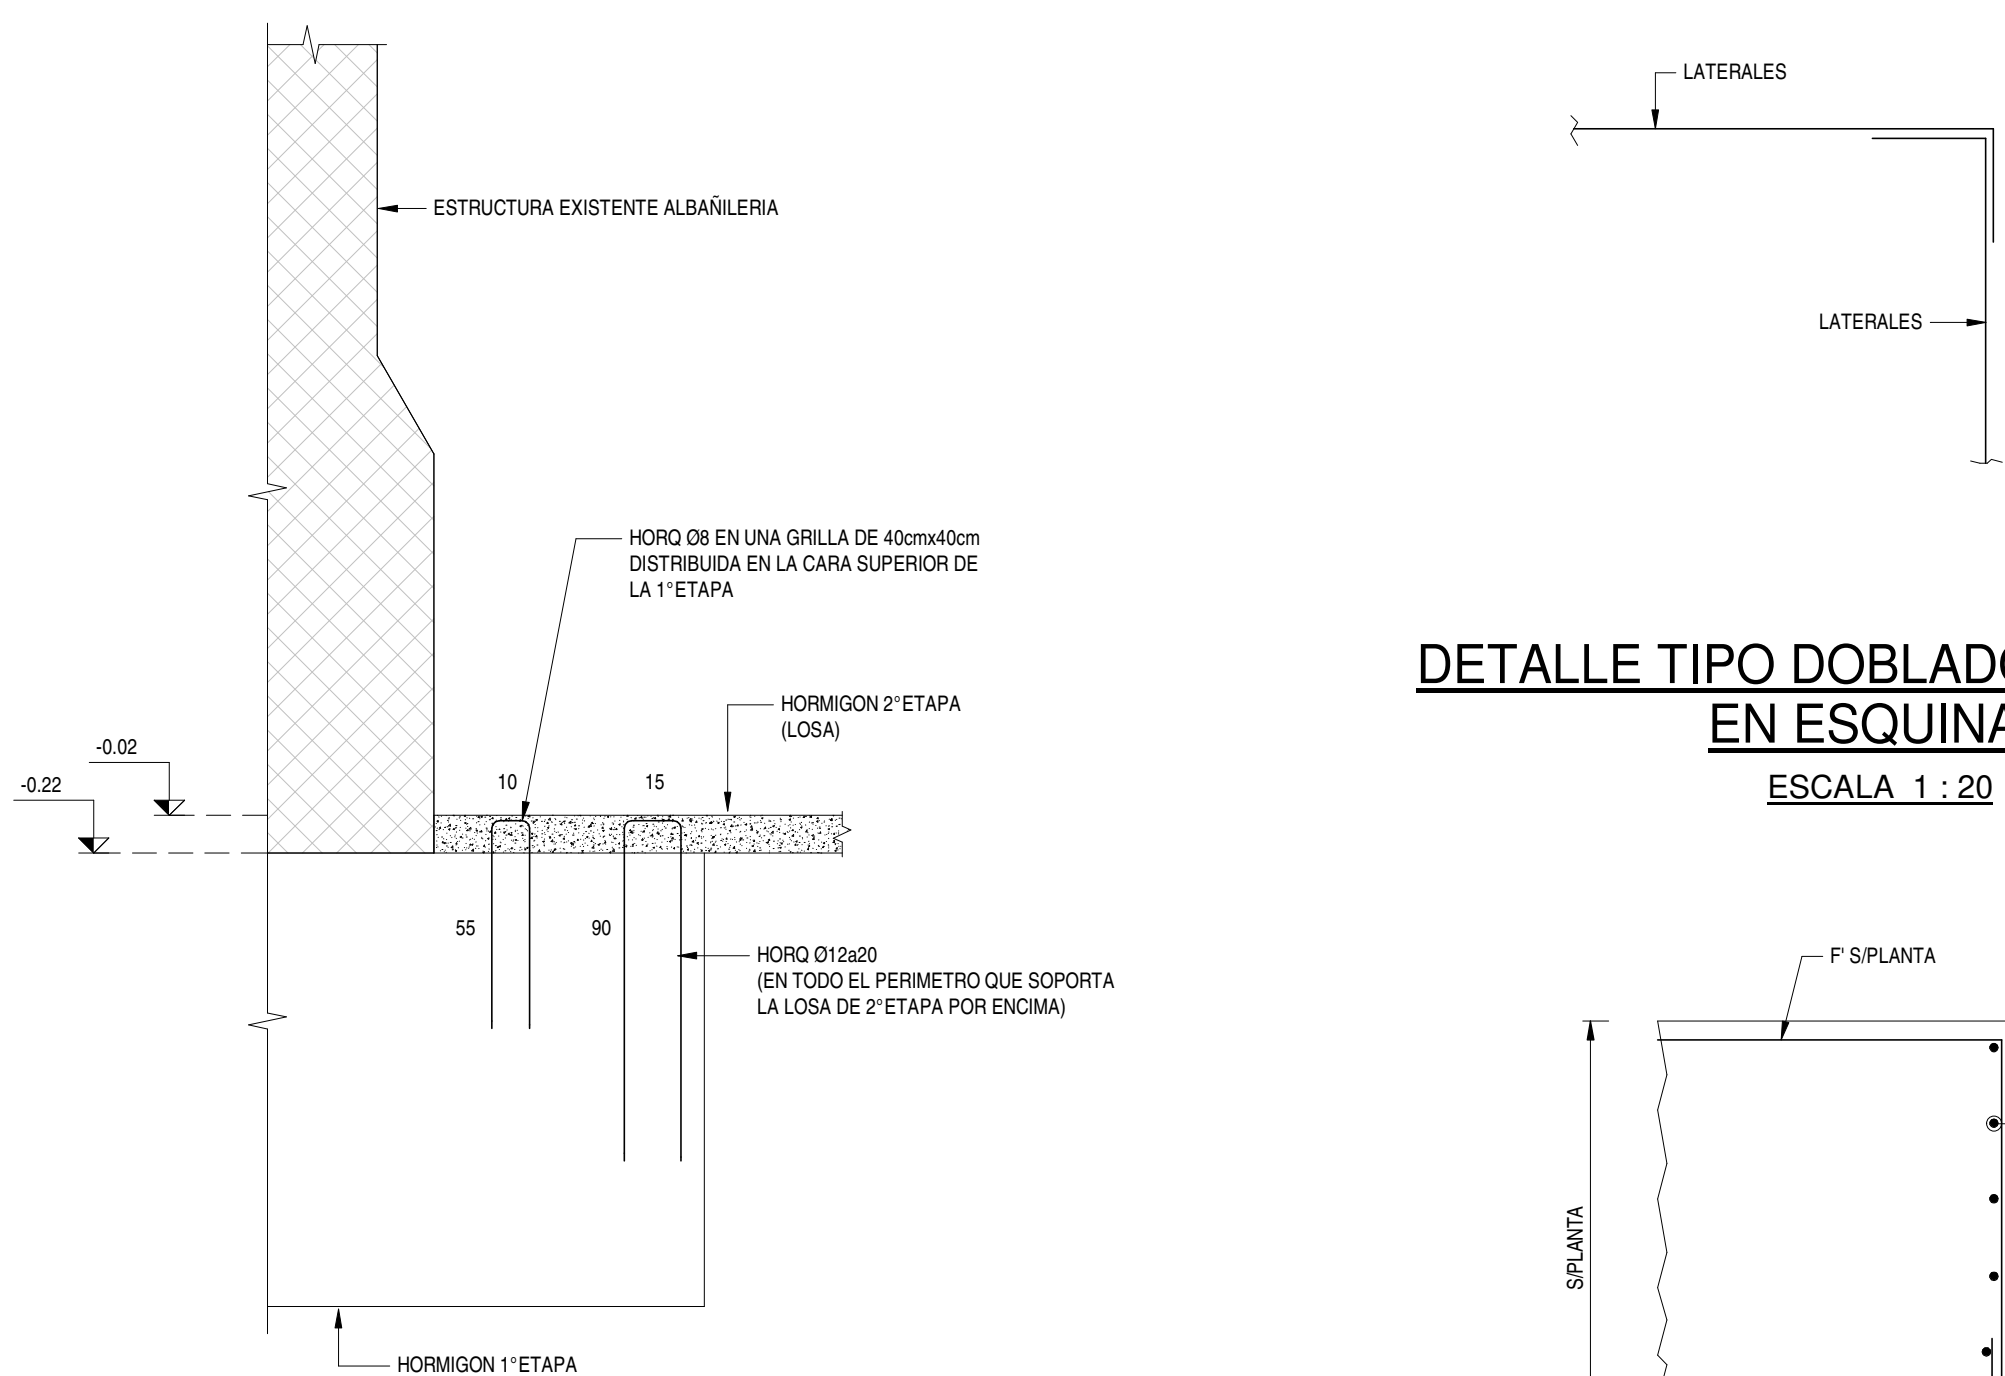


**DETALLE TIPO DOBLADO LATERALES EN ESQUINAS**

ESCALA 1 : 20

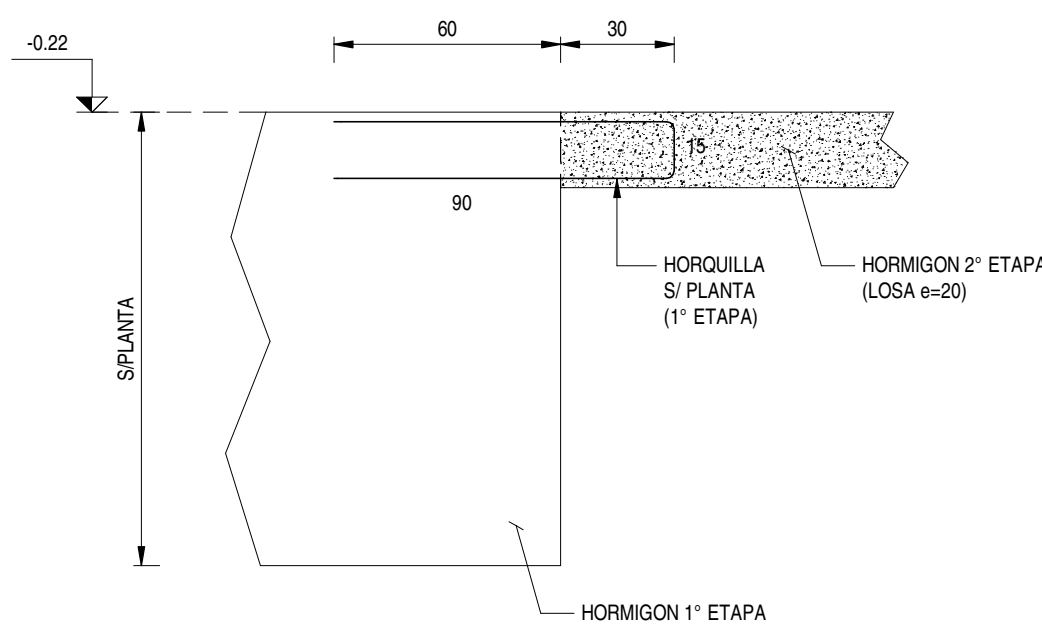

**CORTE A**

ESC. 1 : 20

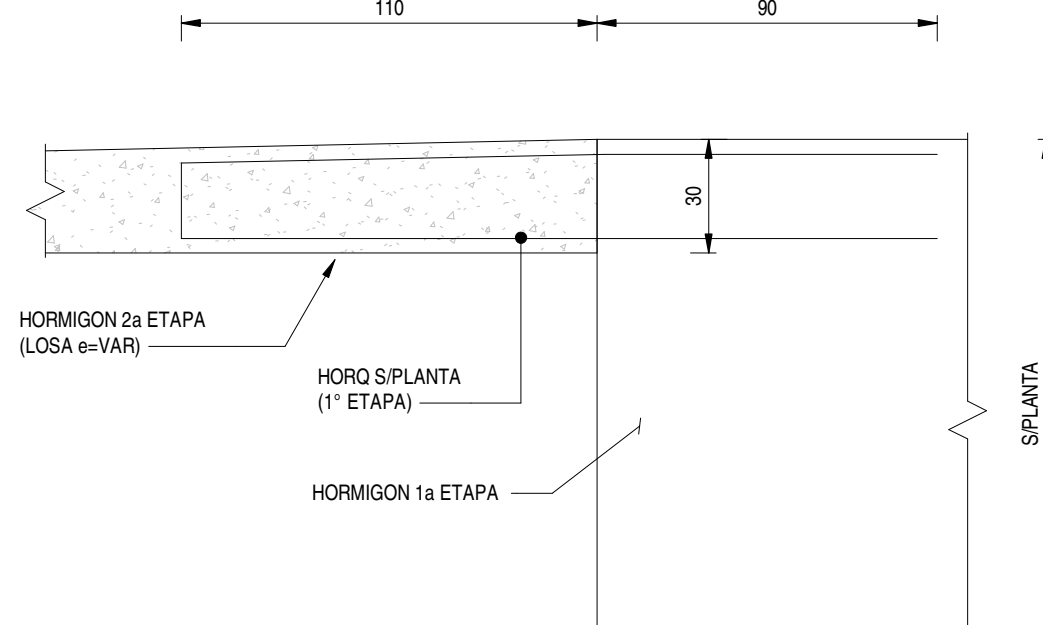

**CORTE B**

ESC. 1 : 20

**DETALLE TIPO HORQUILLAS DE UNION DE LOSA DE 2ª ETAPA COLOCADA SOBRE HORMIGON DE 1ª ETAPA**

ESCALA 1 : 20

**DETALLE TIPO ARMADURAS DE BORDE**

ESCALA 1 : 20

|                                                                                       |            |                      |              |                                   |
|---------------------------------------------------------------------------------------|------------|----------------------|--------------|-----------------------------------|
| F                                                                                     | 23.02.2020 | L. SQUIBBA M. RENDIL | CARL LUDERS  | ENTREGA ETAPA DE DISEÑO           |
| E                                                                                     | 18.12.2020 | L. SQUIBBA M. RENDIL | CARL LUDERS  | SE MODIFICA LO INDICADO           |
| D                                                                                     | 12.06.2020 | L. SQUIBBA M. RENDIL | CARL LUDERS  | EMITIDO PARA REVISION DEL CLIENTE |
| C                                                                                     | 19.12.2019 | S. SAEZ M. RENDIL    | CARL LUDERS  | EMITIDO PARA REVISION DEL CLIENTE |
| B                                                                                     | 05.09.2019 | S. SAEZ M. RENDIL    | CARL LUDERS  | EMITIDO PARA REVISION DEL CLIENTE |
| Nº                                                                                    | FECHA      | DIBUJO/REVISO        | APROBÓ       | DETALLE                           |
| PROYECTO DE CÁLCULO ESTRUCTURAL                                                       |            |                      |              |                                   |
|  |            |                      |              |                                   |
| PROYECTO RECUPERACION BASILICA DEL SALVADOR                                           |            |                      |              |                                   |
| FUNDACIONES, LOSA BASE Y SISTEMA AISLAMIENTO SISMICO                                  |            |                      |              |                                   |
| CALLE HUERFANOS 1796 -SANTIAGO                                                        |            |                      |              |                                   |
| FUNDACION BASICA DEL SALVADOR                                                         |            |                      |              |                                   |
| RUT 55, 146 900-A                                                                     |            |                      |              |                                   |
| CONTENIDO PLANTA ARMADURA SUPERIOR DE LOSA CIELO 1° SUBTERRANEO - 1° ETAPA            |            |                      |              | REVISION                          |
|                                                                                       |            |                      |              | <b>F</b>                          |
| CODIGO DEL DOCUMENTO 18088-01-PL-EST-0202                                             |            | FORMATO AD           | ESCALA 1:100 | FECHA 23.02.2020                  |