


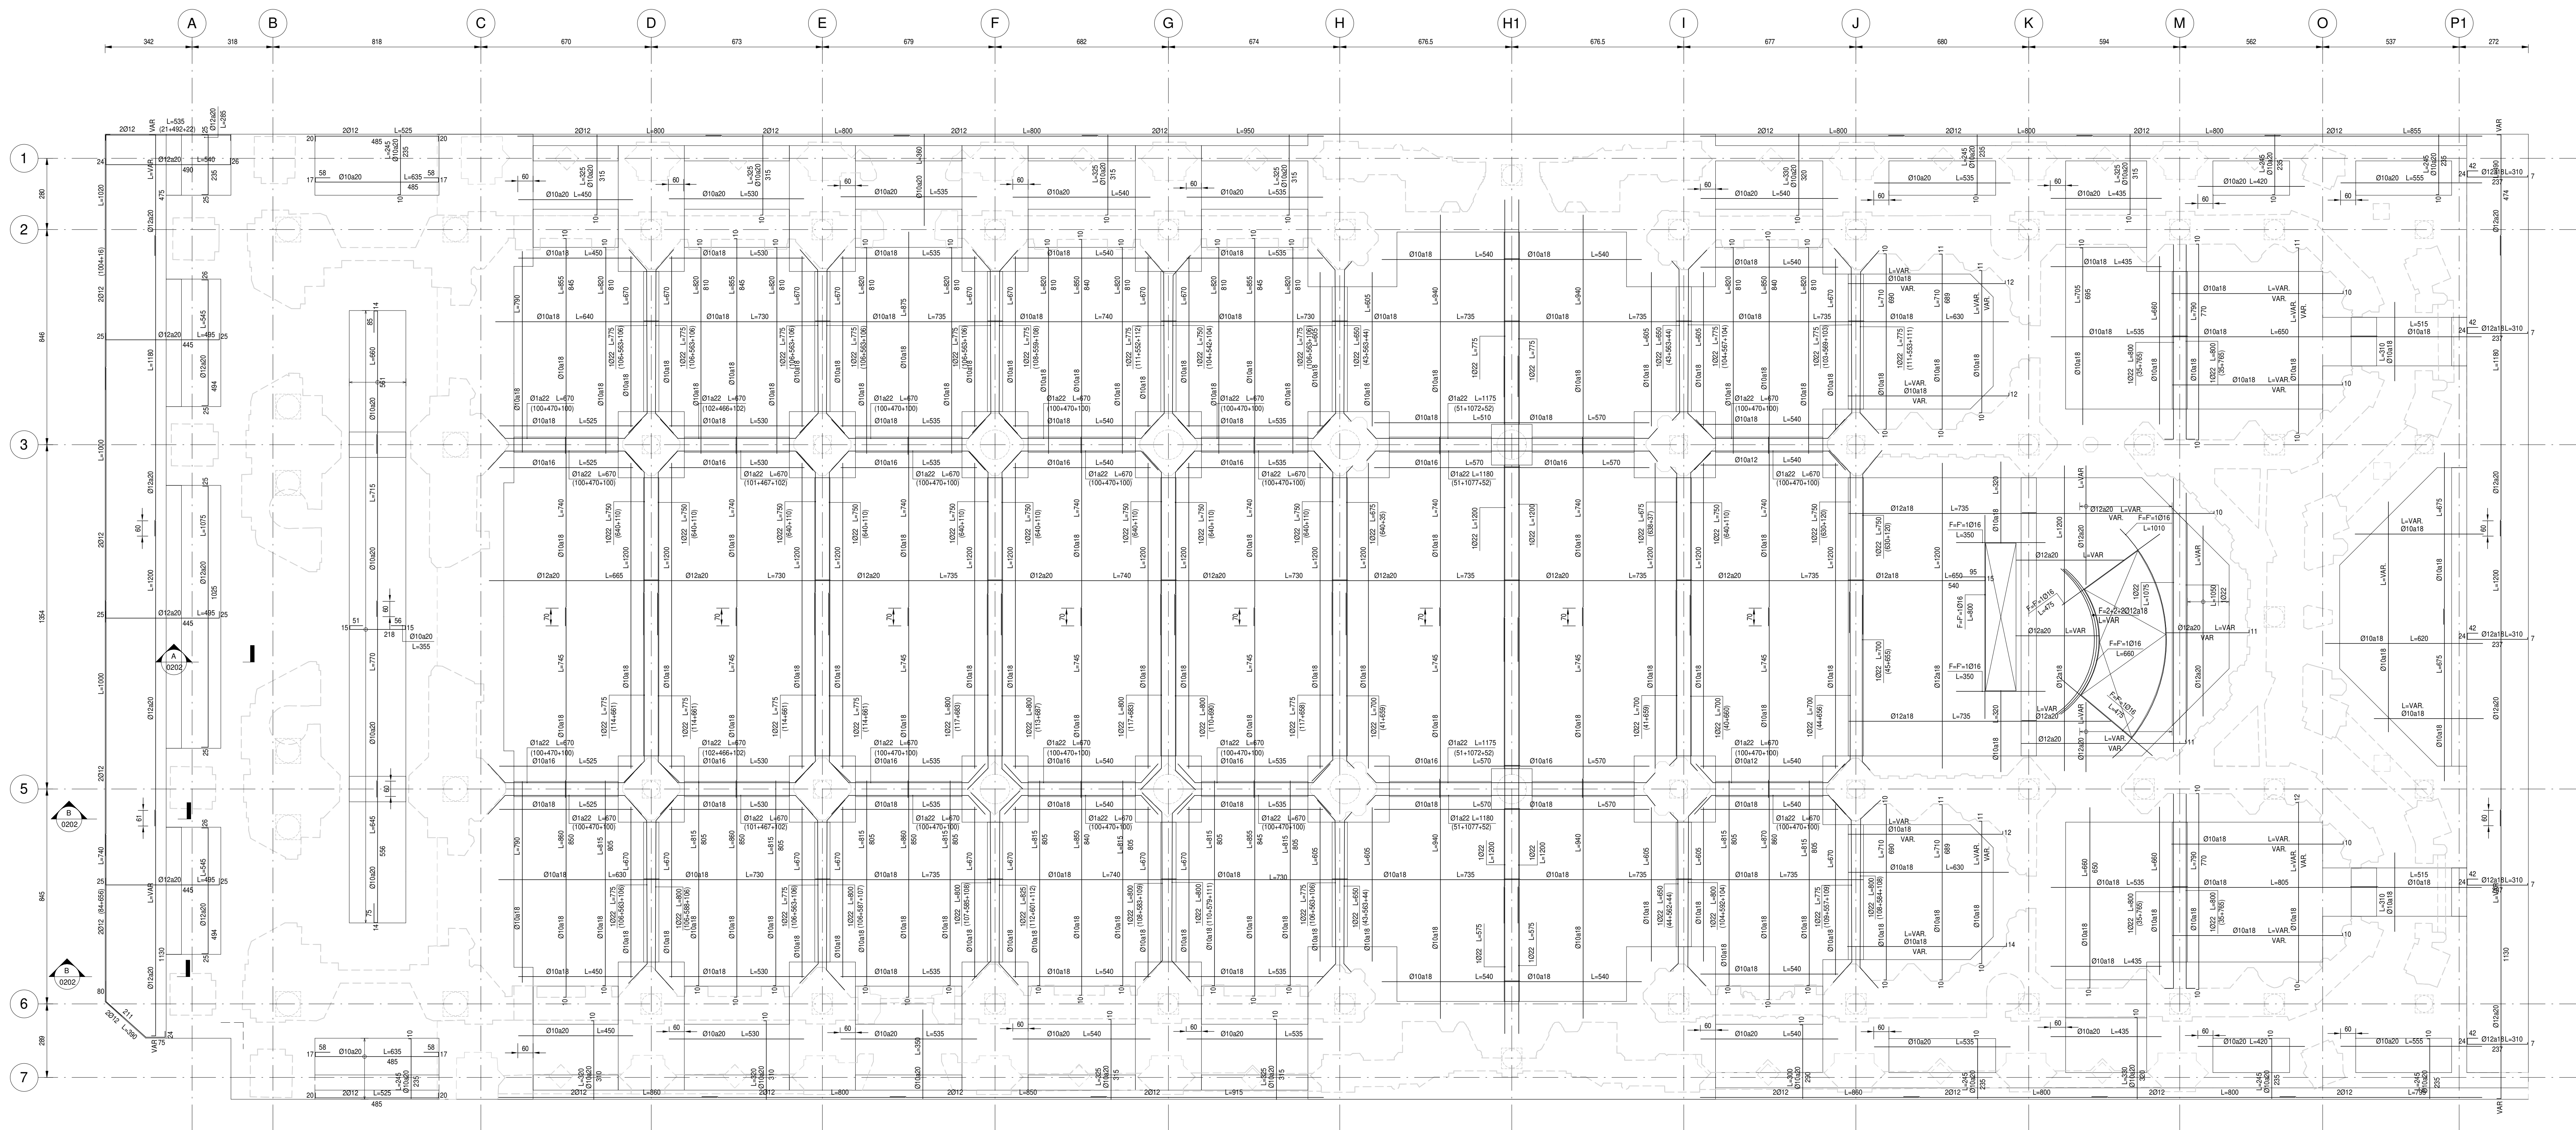

ETAPAS DE HORMIGONADO SEGUN DEFINIDO EN PLANO 103 Y CORTES

PLANTA ARMADURA INFERIOR DE LOSA CIELO 1°
SUBTERRANEO - 2° ETAPA
ESCALA 1:100

F	23.02.2020	L. SQUIBBA M. RENDIL	CARL LUDERS	ENTREGA ETAPA DE DISEÑO
E	18.12.2020	L. SQUIBBA M. RENDIL	CARL LUDERS	SE MODIFICA LO INDICADO
D	12.06.2020	L. SQUIBBA M. RENDIL	CARL LUDERS	EMITIDO PARA REVISION DEL CLIENTE
C	19.12.2019	S. SAIZ M. RENDIL	CARL LUDERS	EMITIDO PARA REVISION DEL CLIENTE
B	05.09.2019	S. SAIZ M. RENDIL	CARL LUDERS	EMITIDO PARA REVISION DEL CLIENTE
Nº			APROBÓ	DETALLE
PROYECTO DE CÁLCULO ESTRUCTURAL				
 sirve SEISMIC PROTECTION TECHNOLOGIES Estad 50 0089, Las Condes, Santiago - Chile TELÉFONO: +56 2 2337 1010 CORREO: info@sirve.cl WEB: www.sirve.cl				
PROYECTO RECUPERACION BASILICA DEL SALVADOR				
FUNDACIONES, LOSA BASE Y SISTEMA AISLAMIENTO SÍSMICO				
UBICACION CALLE HUERFANOS 1796 - SANTIAGO				
GIRITE FUNDACION BASILICA DEL SALVADOR				
RUT: 65.148.9064				
CONTENIDO PLANTA ARMADURA INFERIOR DE LOSA CIELO 1° SUBTERRANEO - 2° ETAPA				REVISION F
CODIGO DEL DOCUMENTO 18088-01-PL-EST-0203		FORMATO AD	ESCALA 1:100	FECHA 23.02.2020