




ELEVACION EJE 3 - ENTRE EJES A y H
ESCALA 1 : 50

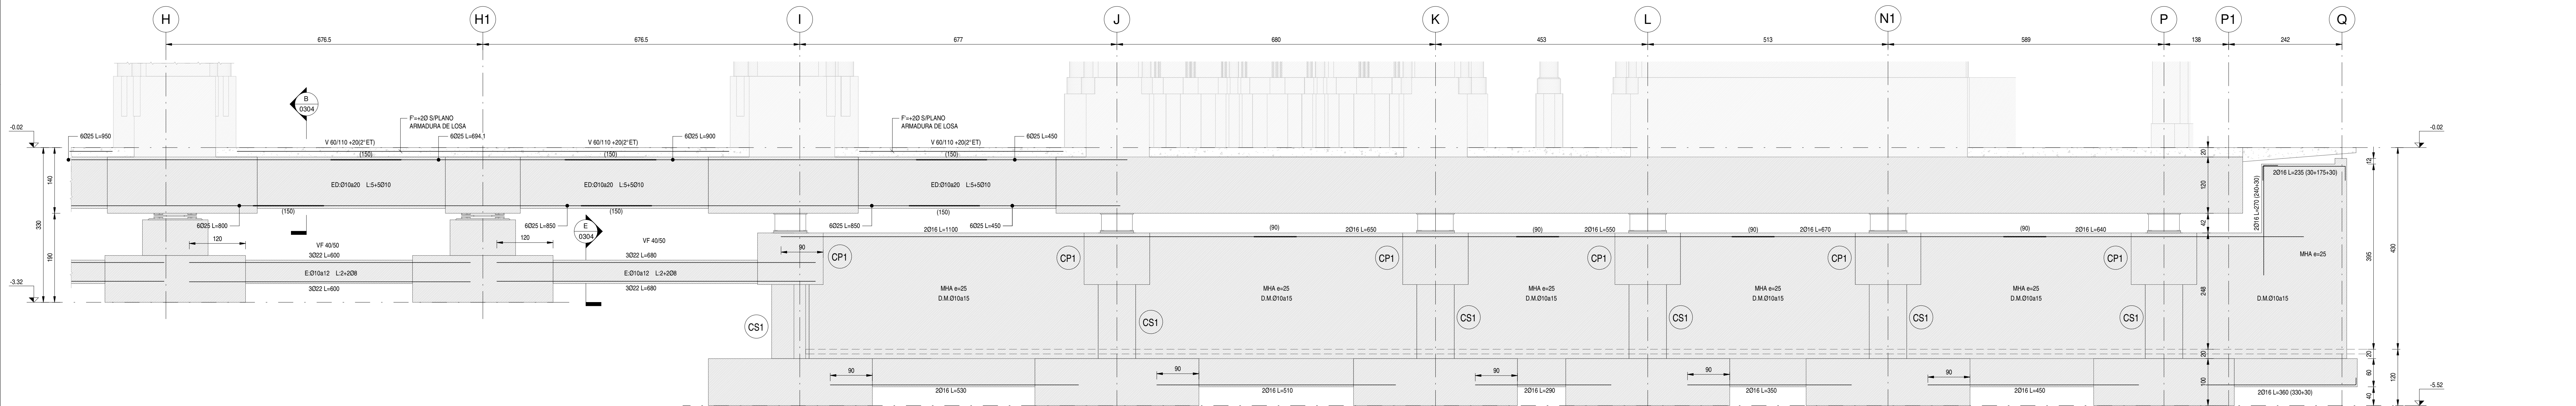

ELEVACION EJE 3 - ENTRE EJES H y P
ESCALA 1 : 50

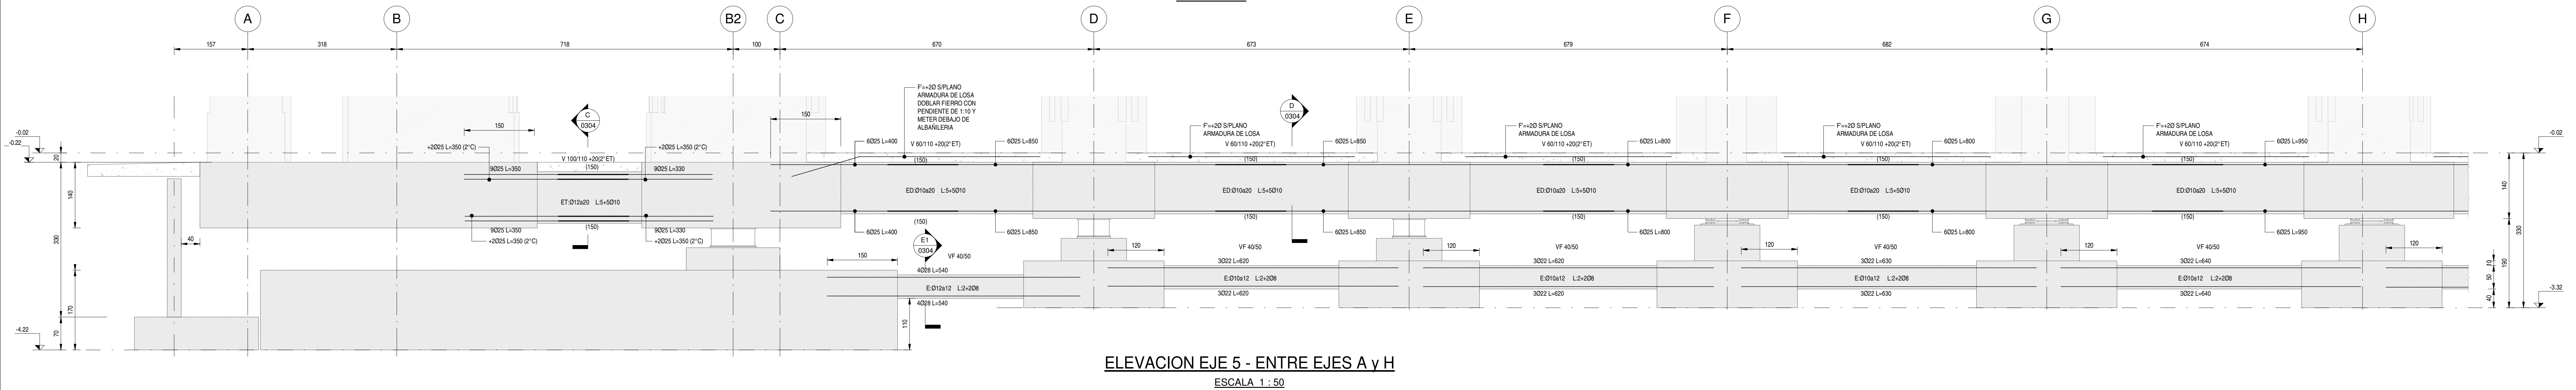

ELEVACION EJE 5 - ENTRE EJES A y H
ESCALA 1 : 50

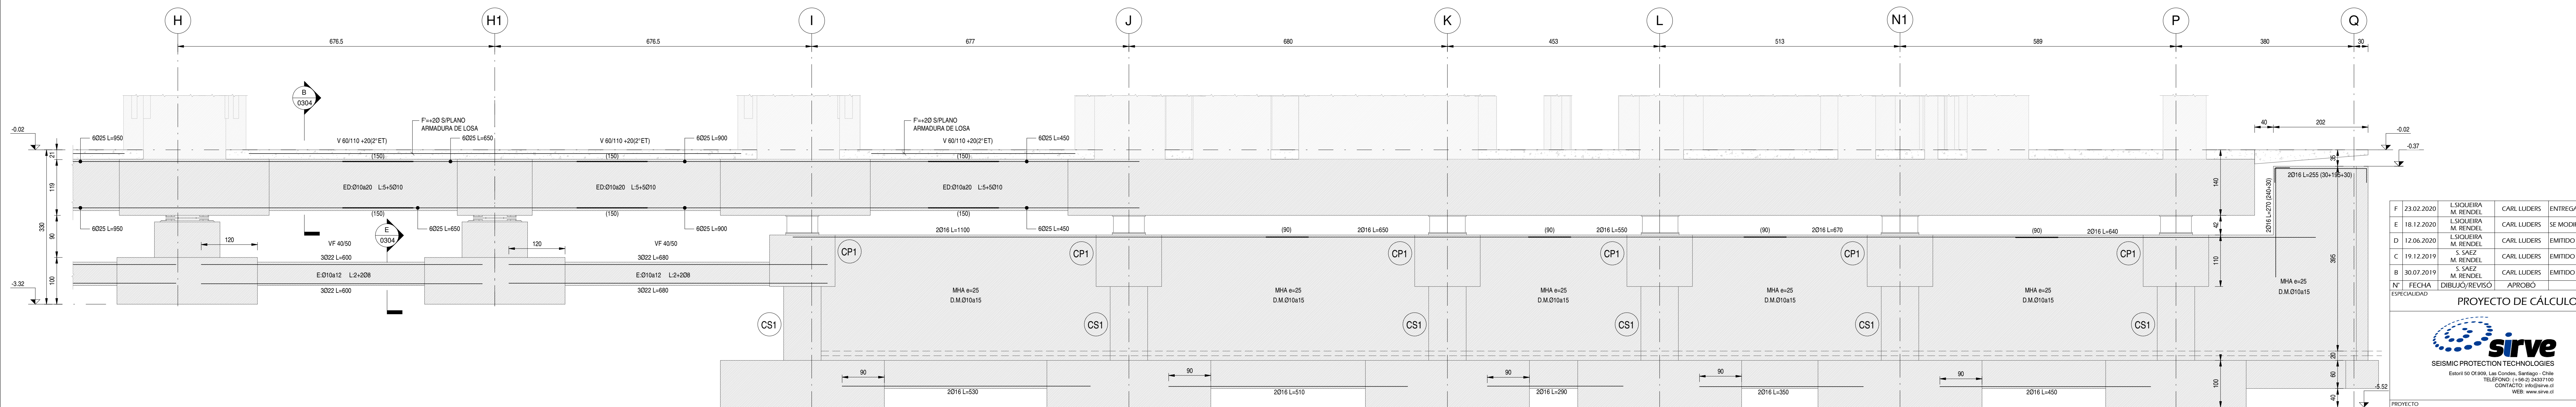

ELEVACION EJE 5 - ENTRE EJES H y P
ESCALA 1 : 50

SIMBOLOGIA	
	HORMIGON DE 1ª ETAPA
	HORMIGON DE 2ª ETAPA

F	23.02.2020	L. SQUIBBA M. RENDIL	CARL LUDERS	ENTREGA ETAPA DE DISEÑO
E	18.12.2020	L. SQUIBBA M. RENDIL	CARL LUDERS	SE MODIFICA LO INDICADO
D	12.06.2020	L. SQUIBBA M. RENDIL	CARL LUDERS	EMITIDO PARA REVISION DEL CLIENTE
C	19.12.2019	S. SAEZ M. RENDIL	CARL LUDERS	EMITIDO PARA REVISION DEL CLIENTE
B	30.07.2019	S. SAEZ M. RENDIL	CARL LUDERS	EMITIDO PARA PRESUPUESTO
Nº	FECHA	DIBUJO/REVISO	APROBÓ	DETALLE
PROYECTO DE CÁLCULO ESTRUCTURAL				
PROYECTO RECUPERACION BASILICA DEL SALVADOR				
UBICACION CALLE HUERFANOS 1796 - SANTIAGO				
GUBER FUNDACION BASILICA DEL SALVADOR				
CONTENIDO ELEVACIONES DE EJES 3 - 5				
CODIGO DEL DOCUMENTO 18088-01-PL-EST-0302				FECHA 23.02.2020