




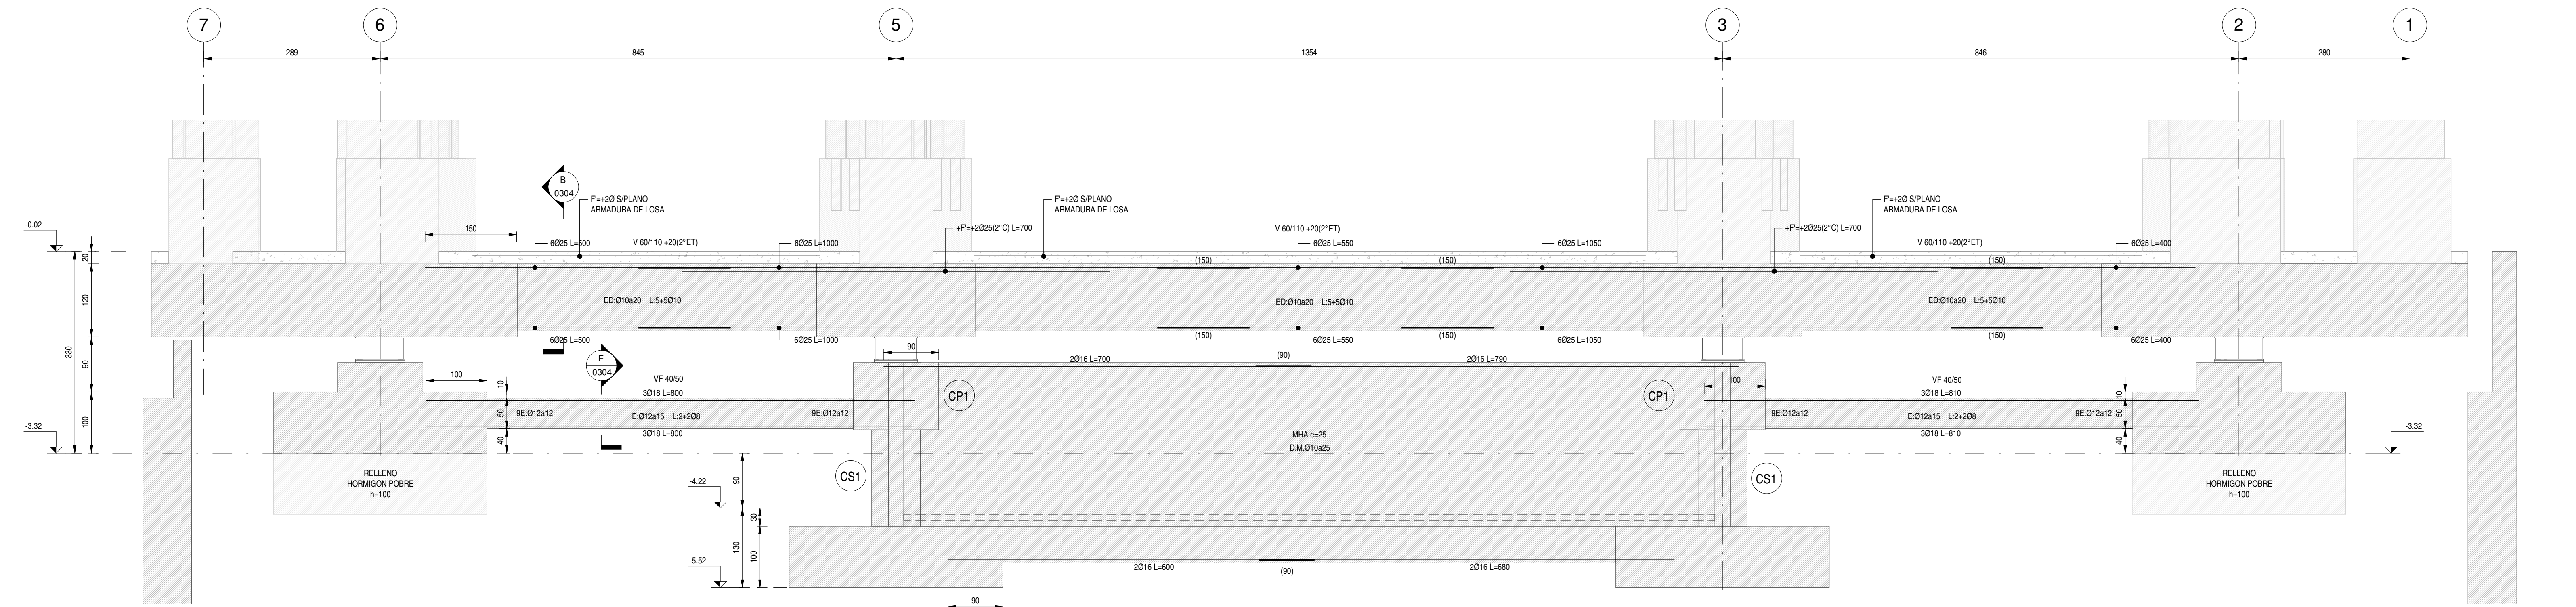


ELEVACION EJE I
ESCALA 1 : 50

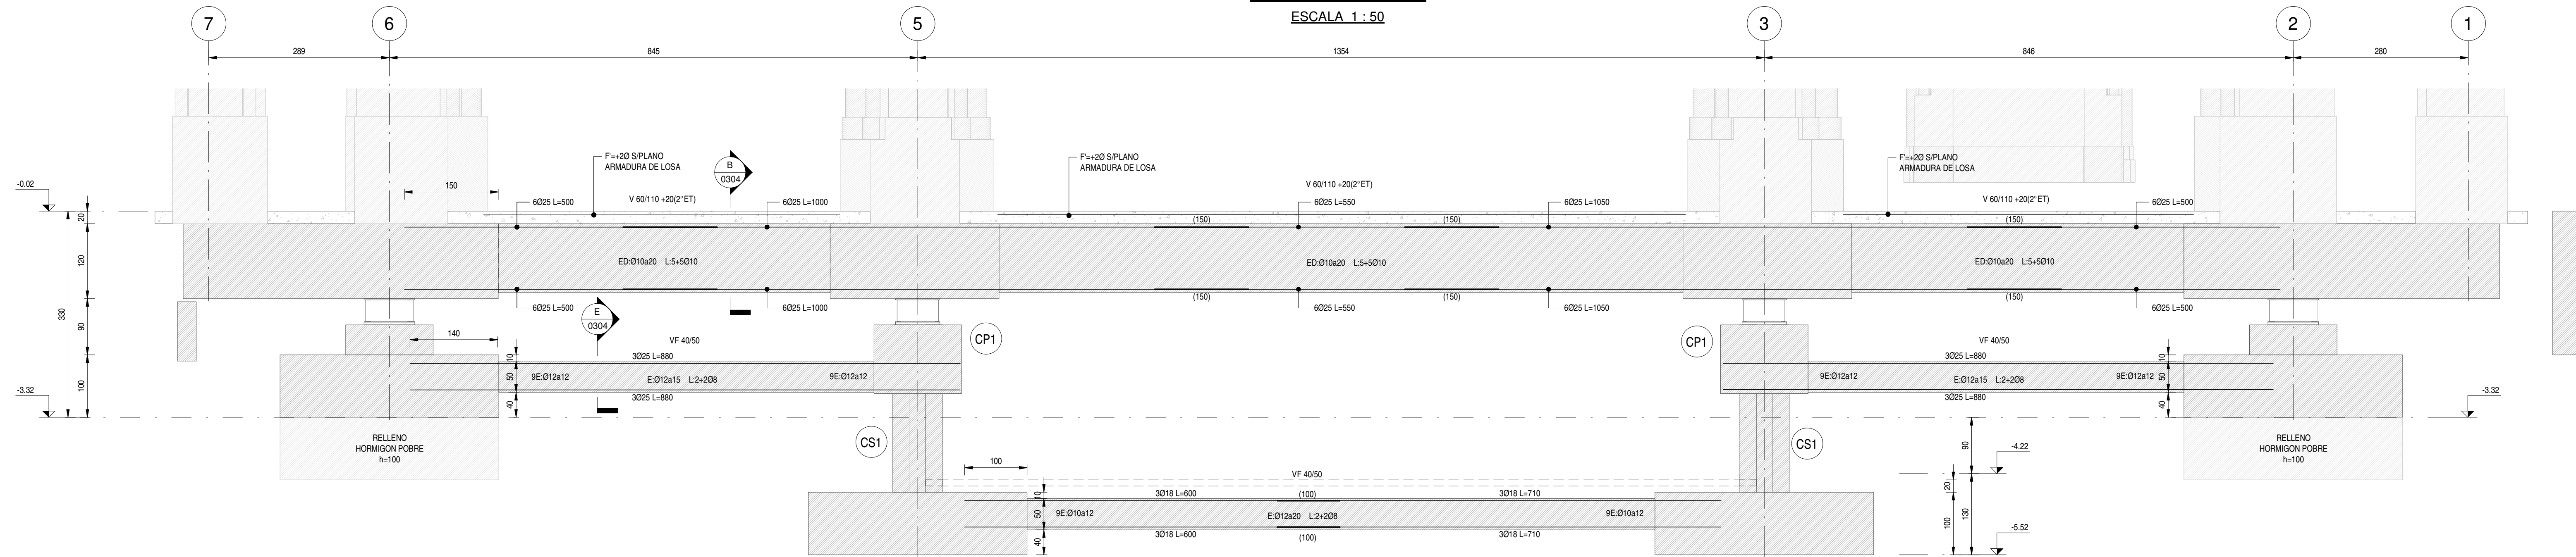


ELEVACION EJE J
ESCALA 1 : 50

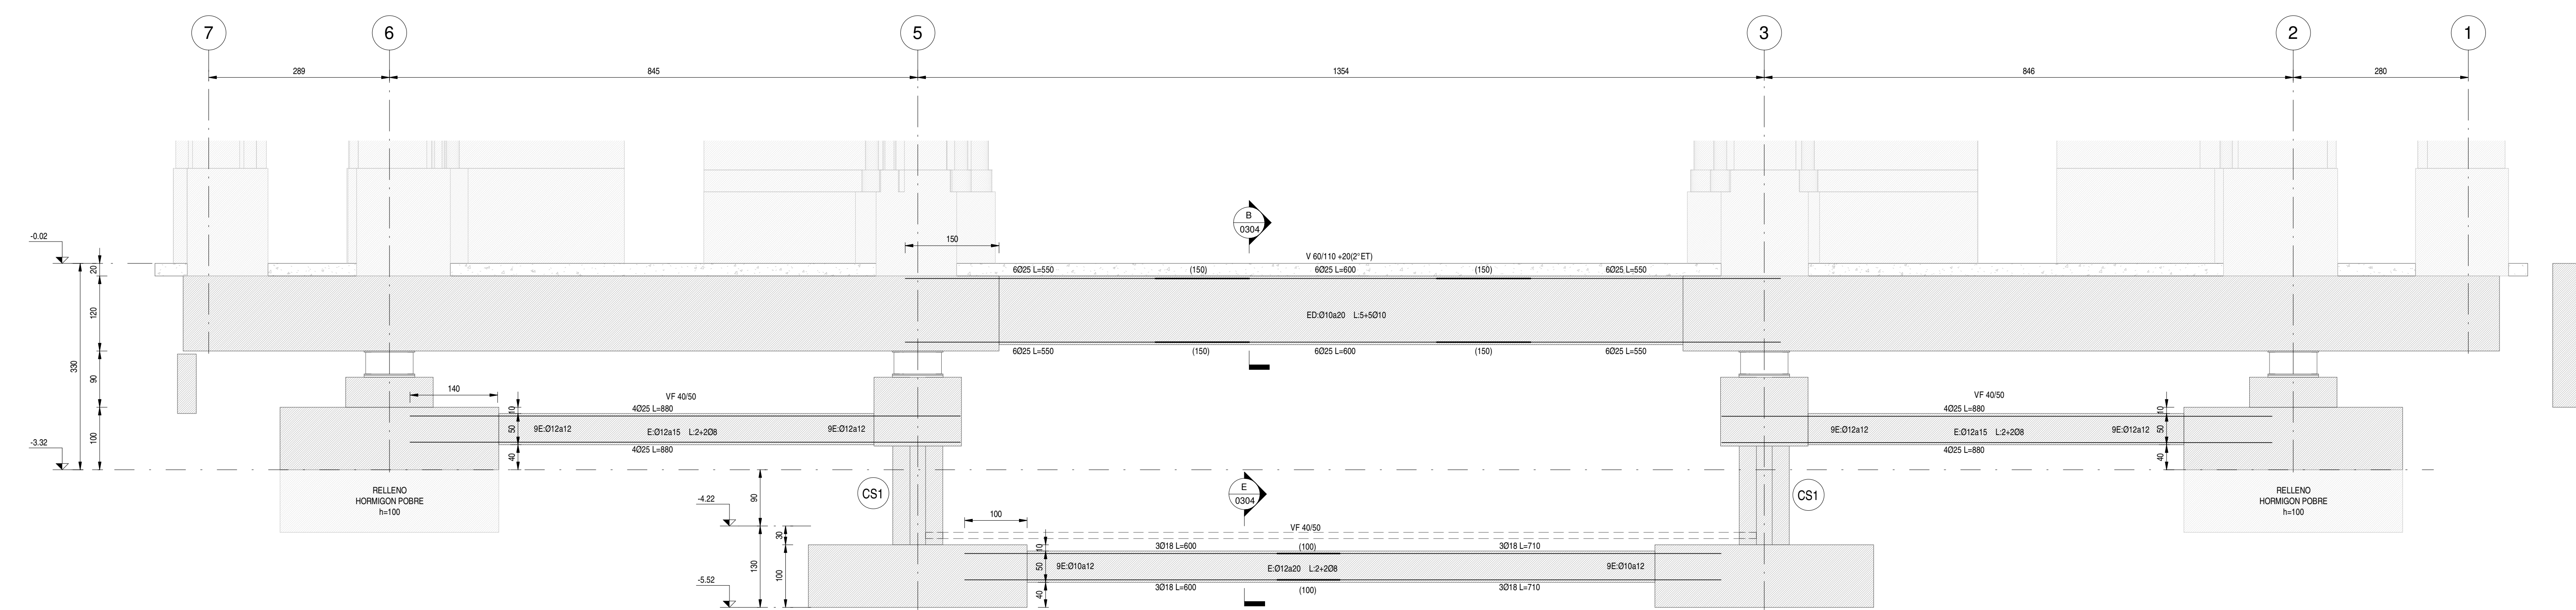


ELEVACION EJE K
ESCALA 1 : 50

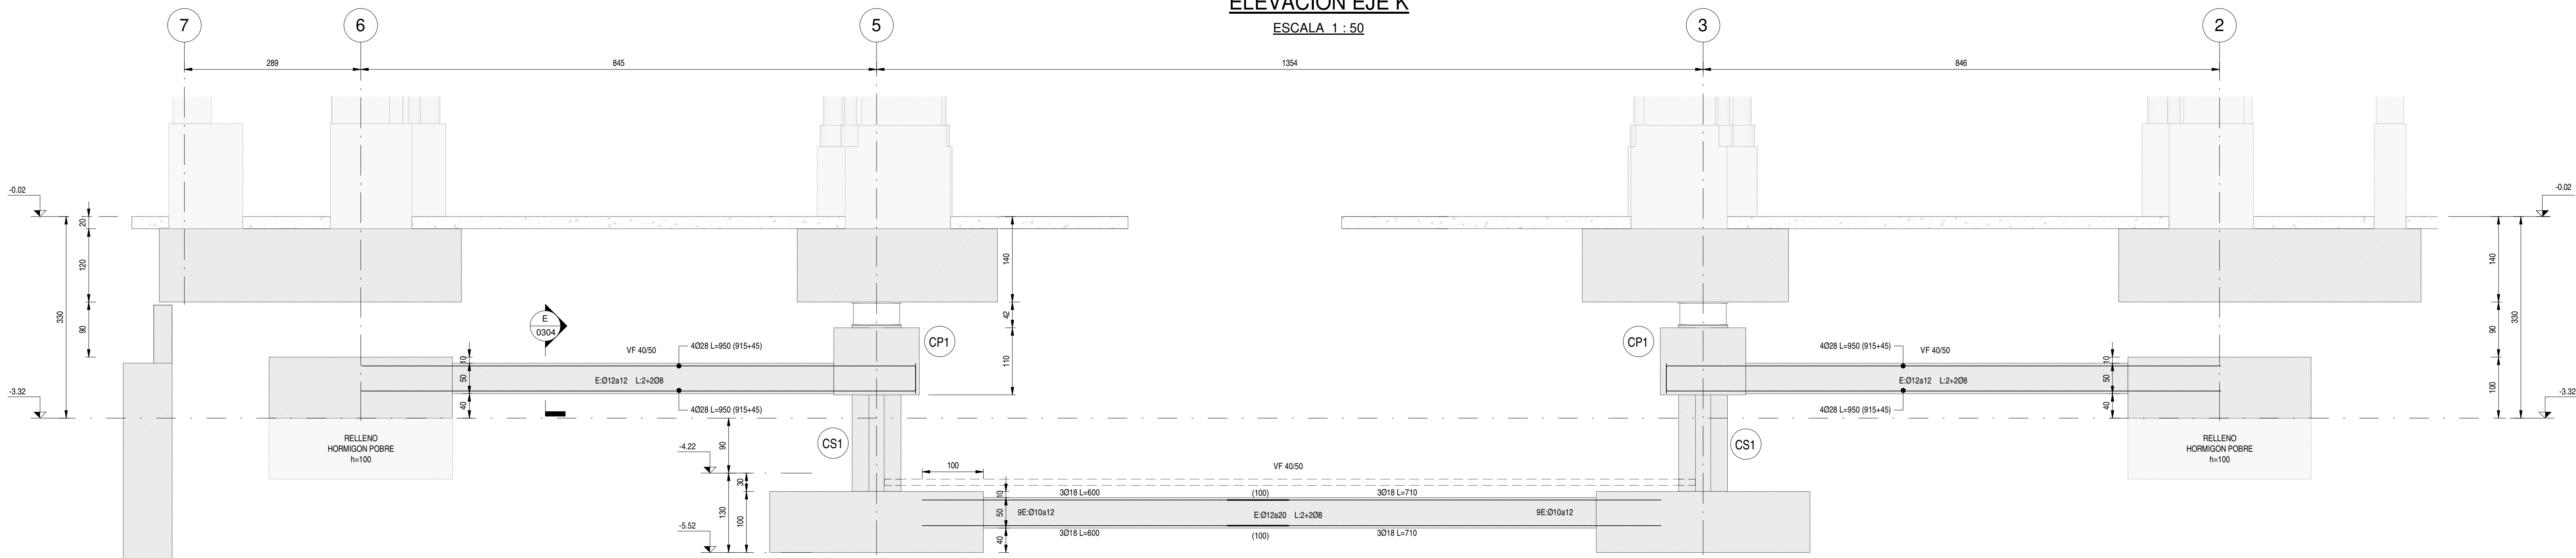


ELEVACION EJE L
ESCALA 1 : 50

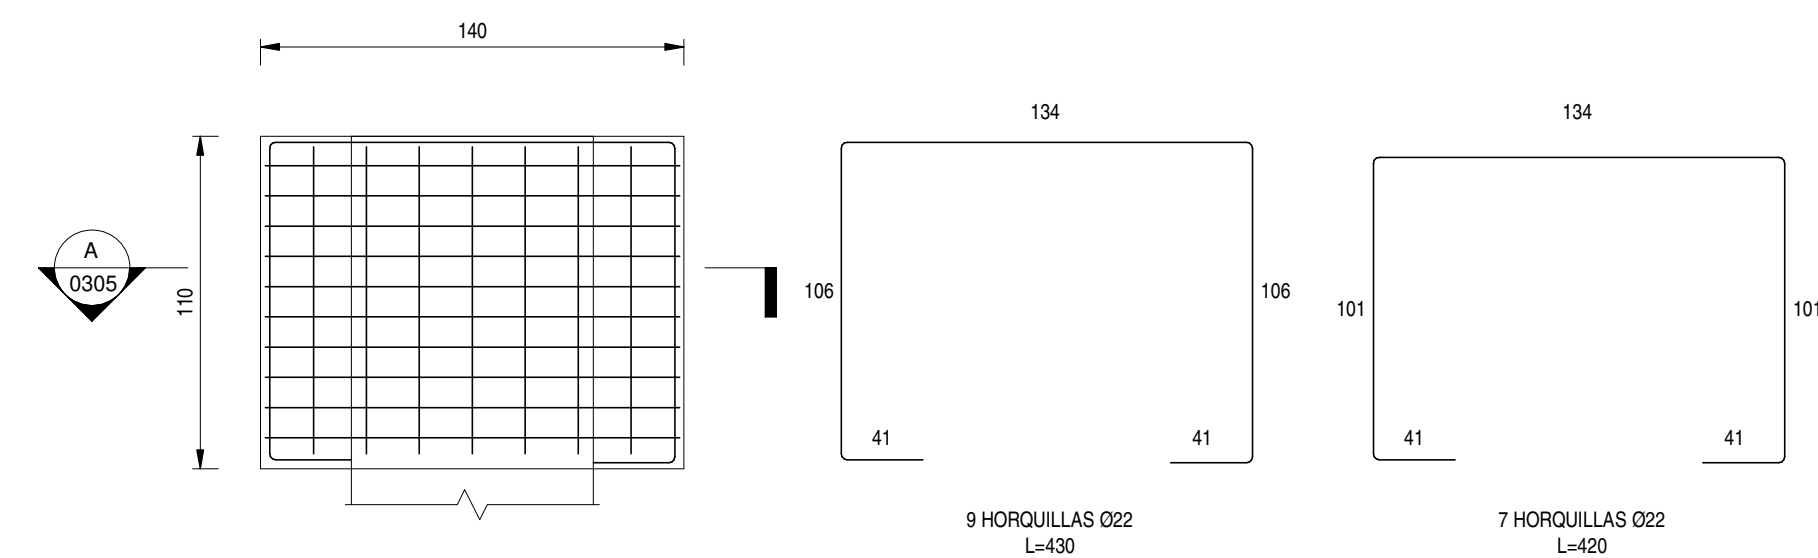


ARMADURA CAPITEL CP1
ESCALA 1 : 25

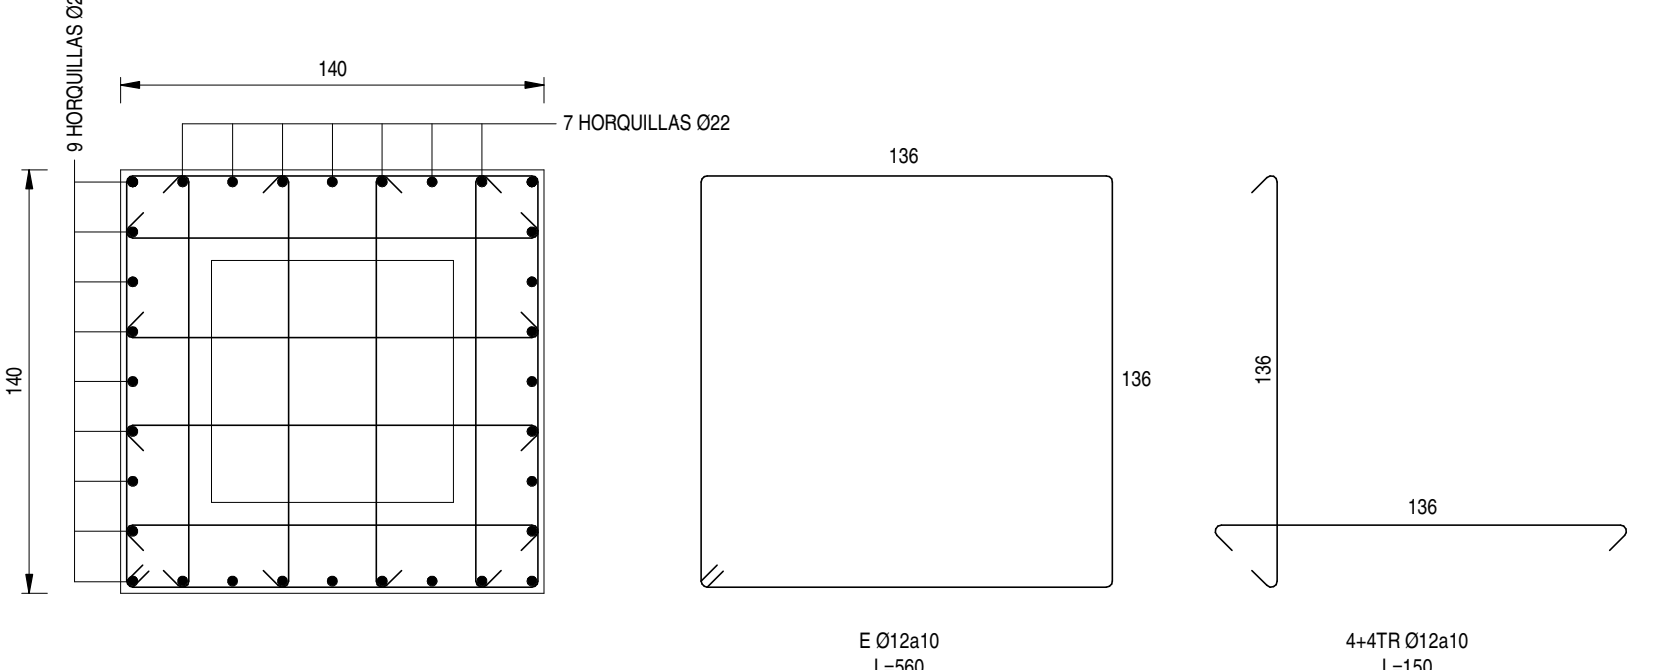

CORTE A
ESC. 1 : 25

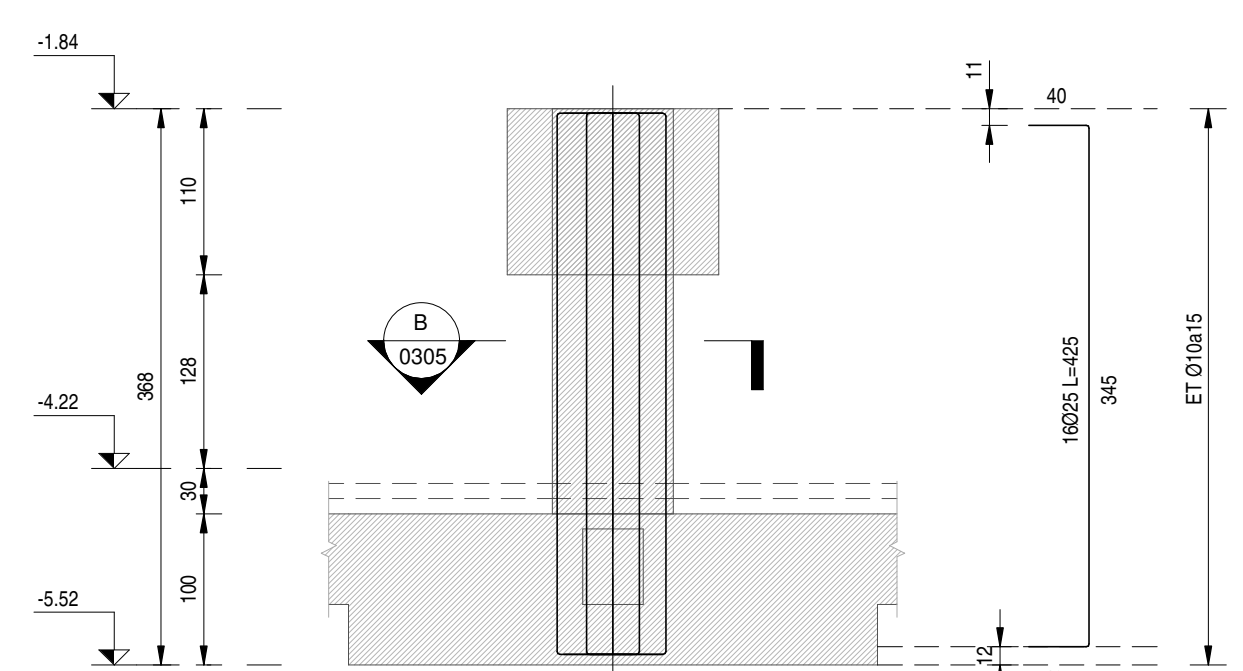

ELEVACION COLUMNA CS1
ESCALA 1 : 50

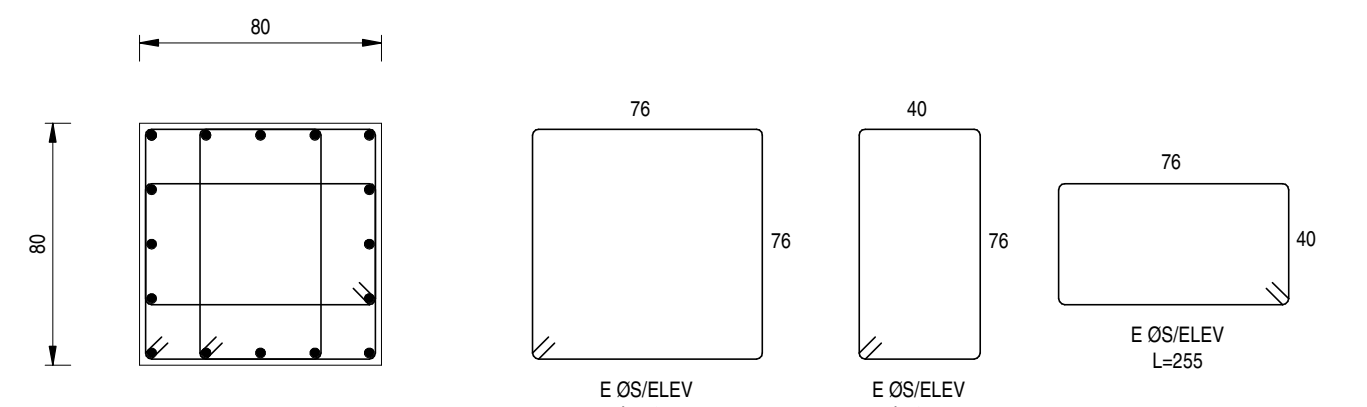

CORTE B
ESC. 1 : 25

F	23.02.2020	L. SQUIBBA M. RENDIEL	CARL LUDERS	ENTREGA ETAPA DE DISEÑO
E	18.12.2020	L. SQUIBBA M. RENDIEL	CARL LUDERS	SE MODIFICA LO INDICADO
D	12.06.2020	L. SQUIBBA M. RENDIEL	CARL LUDERS	EMITIDO PARA REVISION DEL CLIENTE
C	19.12.2019	L. SQUIBBA M. RENDIEL	CARL LUDERS	EMITIDO PARA REVISION DEL CLIENTE
B	30.07.2019	L. SQUIBBA M. RENDIEL	CARL LUDERS	EMITIDO PARA PRESUPUESTO
Nº	FECHA	DIBUJO/REVISO	APROBÓ	DETALLE
PROYECTO DE CÁLCULO ESTRUCTURAL				
				
PROYECTO RECUPERACION BASILICA DEL SALVADOR				
FUNDACIONES, LOSA BASE Y SISTEMA AISLAMIENTO SÍSMICO				
UBICACION CALLE HUERFANOS 1796 - SANTIAGO				
GIRITE FUNDACION BASILICA DEL SALVADOR				
RUT: 65.148.0834				
CONTENIDO ELEVACIONES DE EJES I - J - K - L				REVISION
				F
CODIGO DEL DOCUMENTO 18088-01-PL-EST-0305		FORMATO A4	ESCALA 1:50	FECHA 23.02.2020