


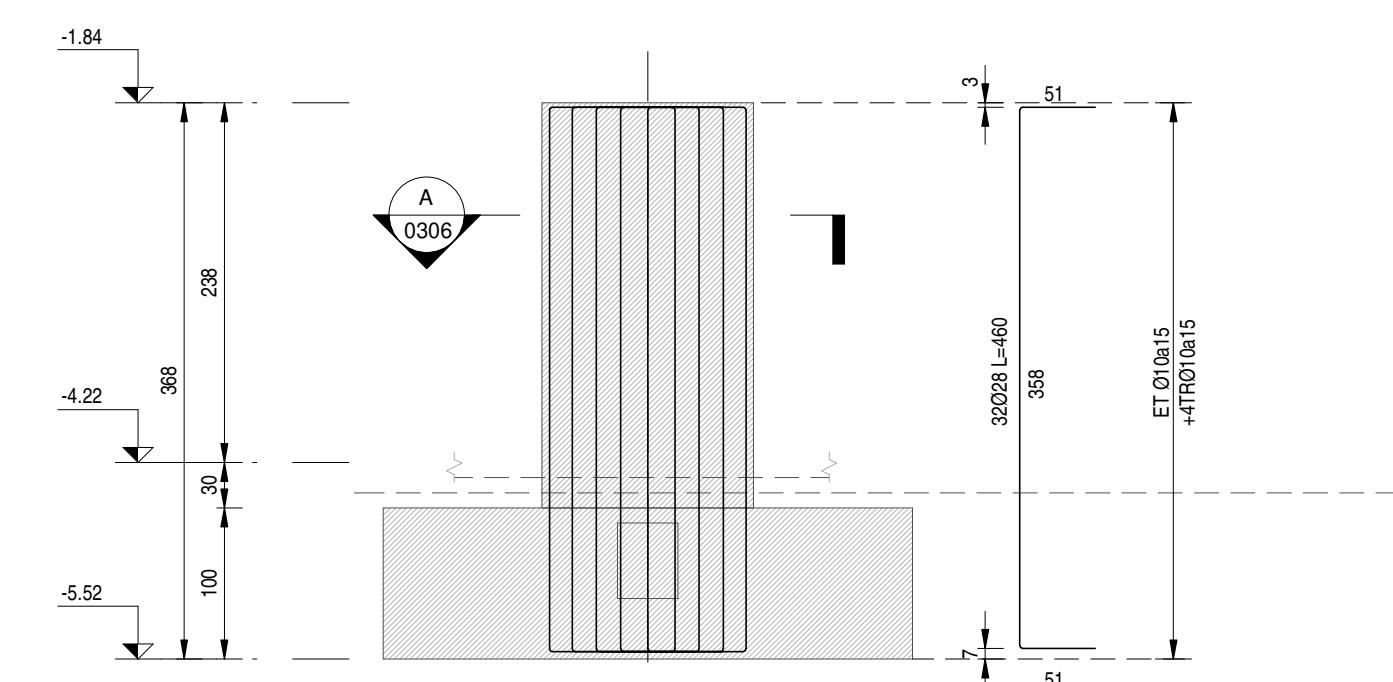
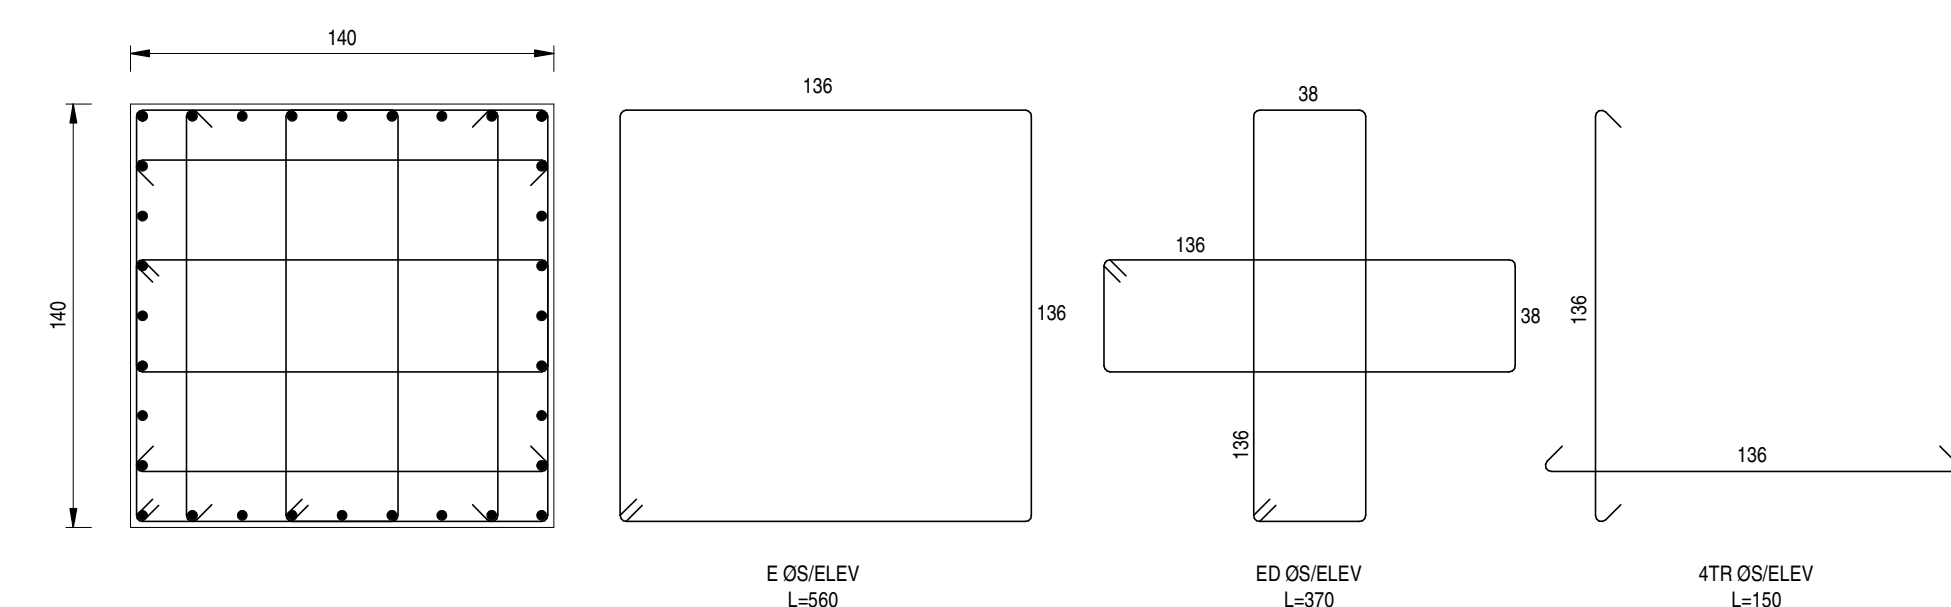


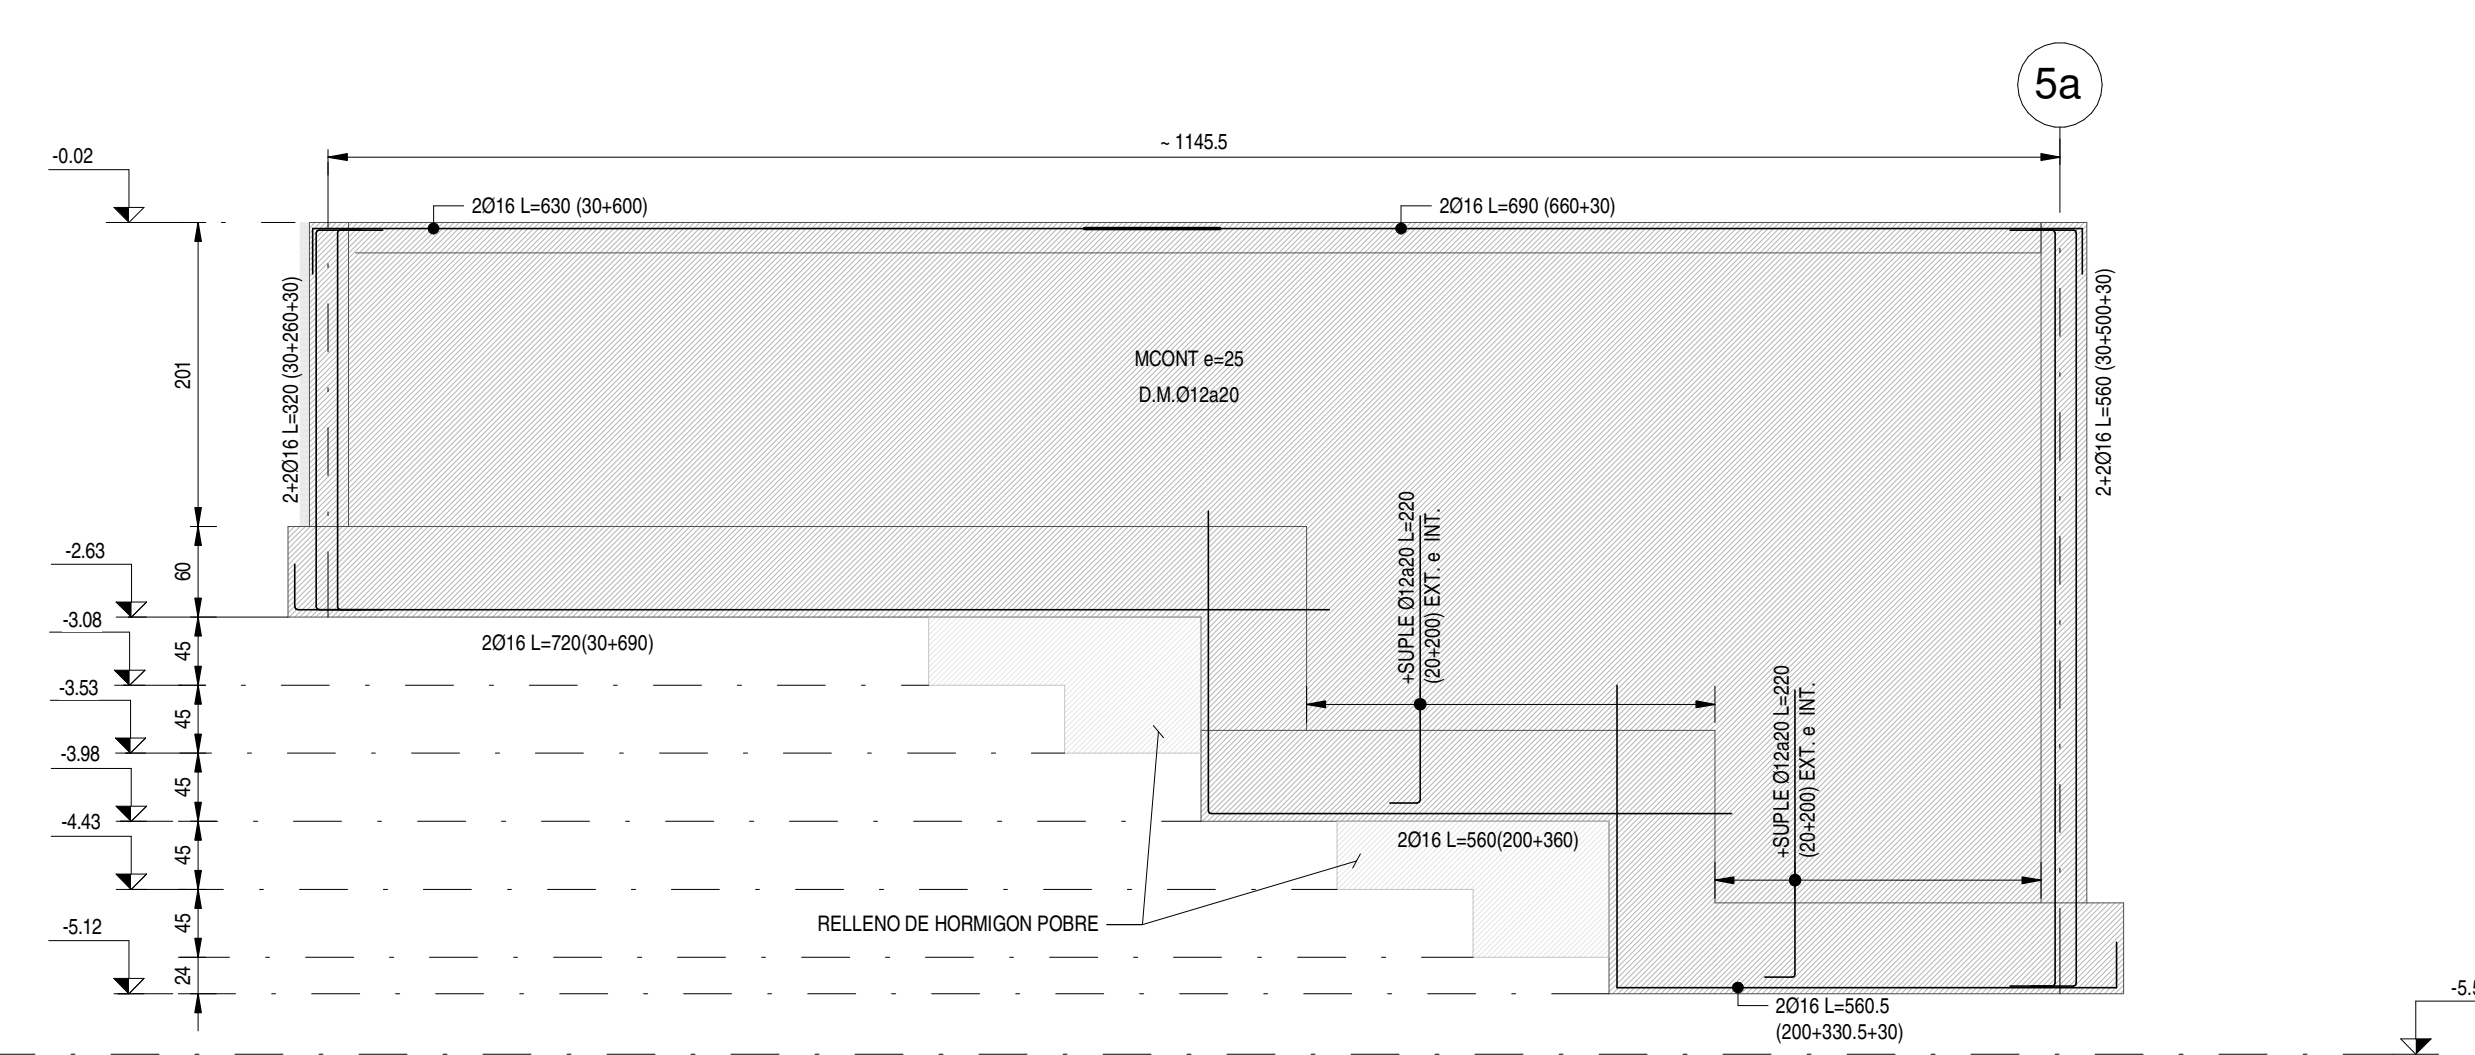

ELEVACION COLUMNA CS2
ESCALA 1 : 50

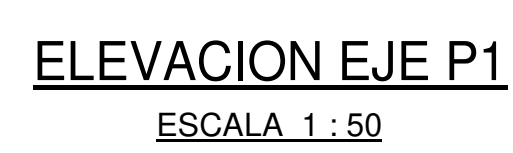

ELEVACION EJE M
ESCALA 1 : 50

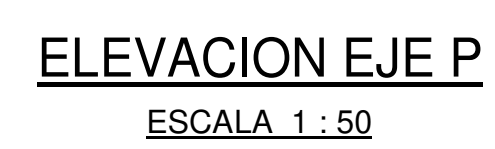

ELEVACION EJE Q1
ESCALA 1 : 50

F	23.02.2020	L. SQUERRA M. RENDIL	CARL LUDERS	ENTREGA ETAPA DE DISEÑO	
F	18.12.2020	L. SQUERRA M. RENDIL	CARL LUDERS	SE MODIFICA LO INDICADO	
D	12.06.2020	L. SQUERRA M. RENDIL	CARL LUDERS	EMITIDO PARA REVISIÓN DEL CLIENTE	
F	19.12.2019	L. SQUERRA M. RENDIL	CARL LUDERS	EMITIDO PARA REVISIÓN DEL CLIENTE	
B	30.07.2019	A. SÁEZ M. RENDIL	CARL LUDERS	EMITIDO PARA PRESUPUESTO	
N	FECHA DE CANCELACIÓN	DIBUJO	PROYECTO	APROBADO	DETALLE
PROYECTO DE CÁLULO ESTRUCTURAL					
 SEISMIC PROTECTION TECHNOLOGIES Baselstr. 20, 40511 Basel, Switzerland TELEFONO: +41 78 4343710 CONTACTO: info@sirve.ch WEB: www.sirve.ch CARL LUDERS SCHWENZMEIER Baselstr. 20, 40511 Basel, Switzerland Dipl. Ing. Technische Hochschule Darmstadt 3.67.13.17.2					
PROYECTO	RECUPERACION BASILICA DEL SALVADOR				
	FUNDACIONES, LOSA BASE Y SISTEMA AISLAMIENTO SISMICO				
UBICACION	CALLE HUERRANOS 1796 - SANTAGO				
CLIENTE	FUNDACION BASILICA DEL SALVADOR				
	RUT: 45.148.989-6				
CONTENIDO	ELEVACIONES DE EJES N1 - M - P - P1 - Q - O1				
					REVISION
CODIGO DEL DOCUMENTO	FIRMAS		ESCALA	FECHA	
10808-01-PL-EST-036	AD		-50	23.02.20	