




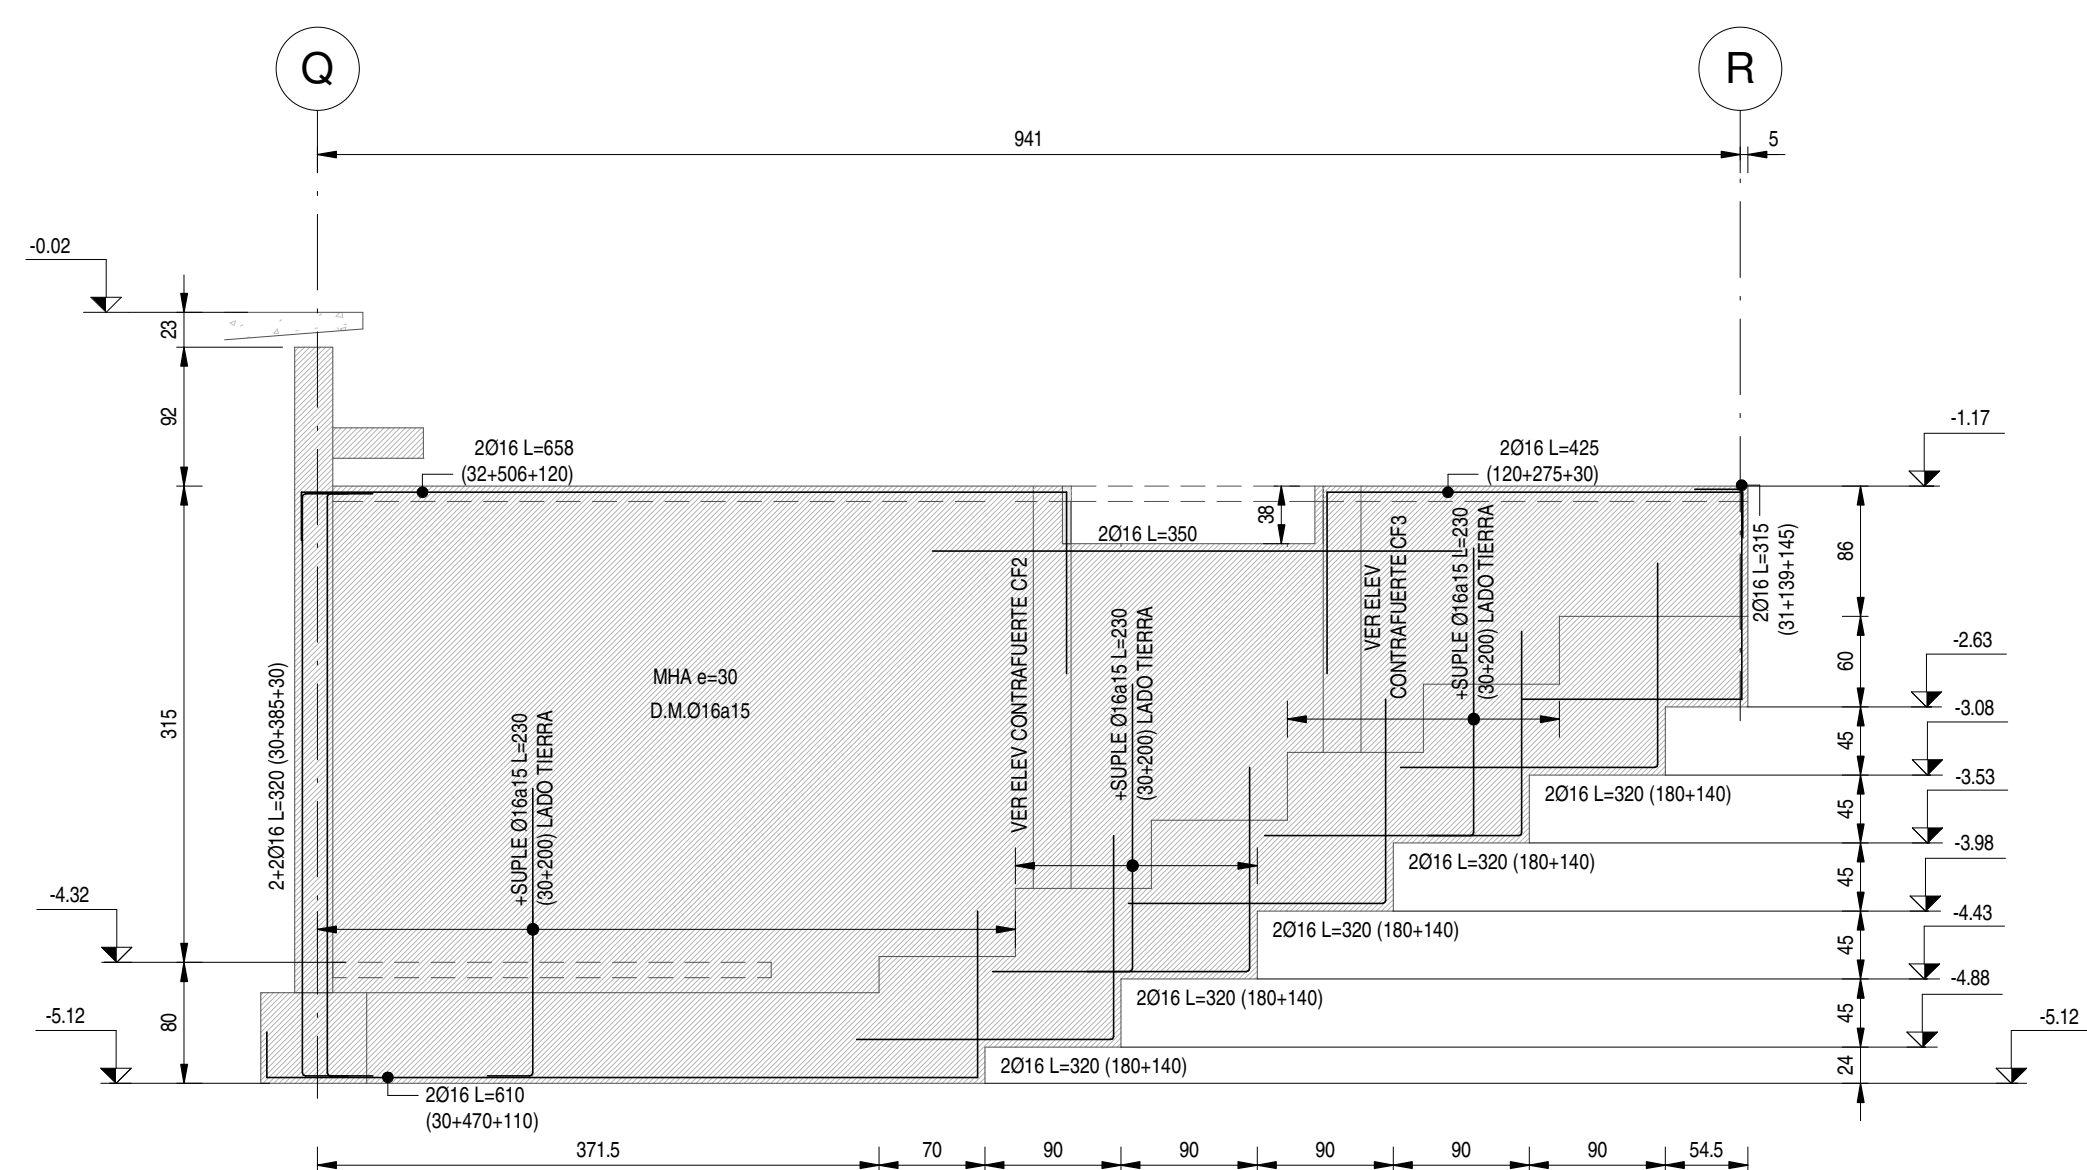


ELEVACION EJE 2a
ESCALA 1 : 50

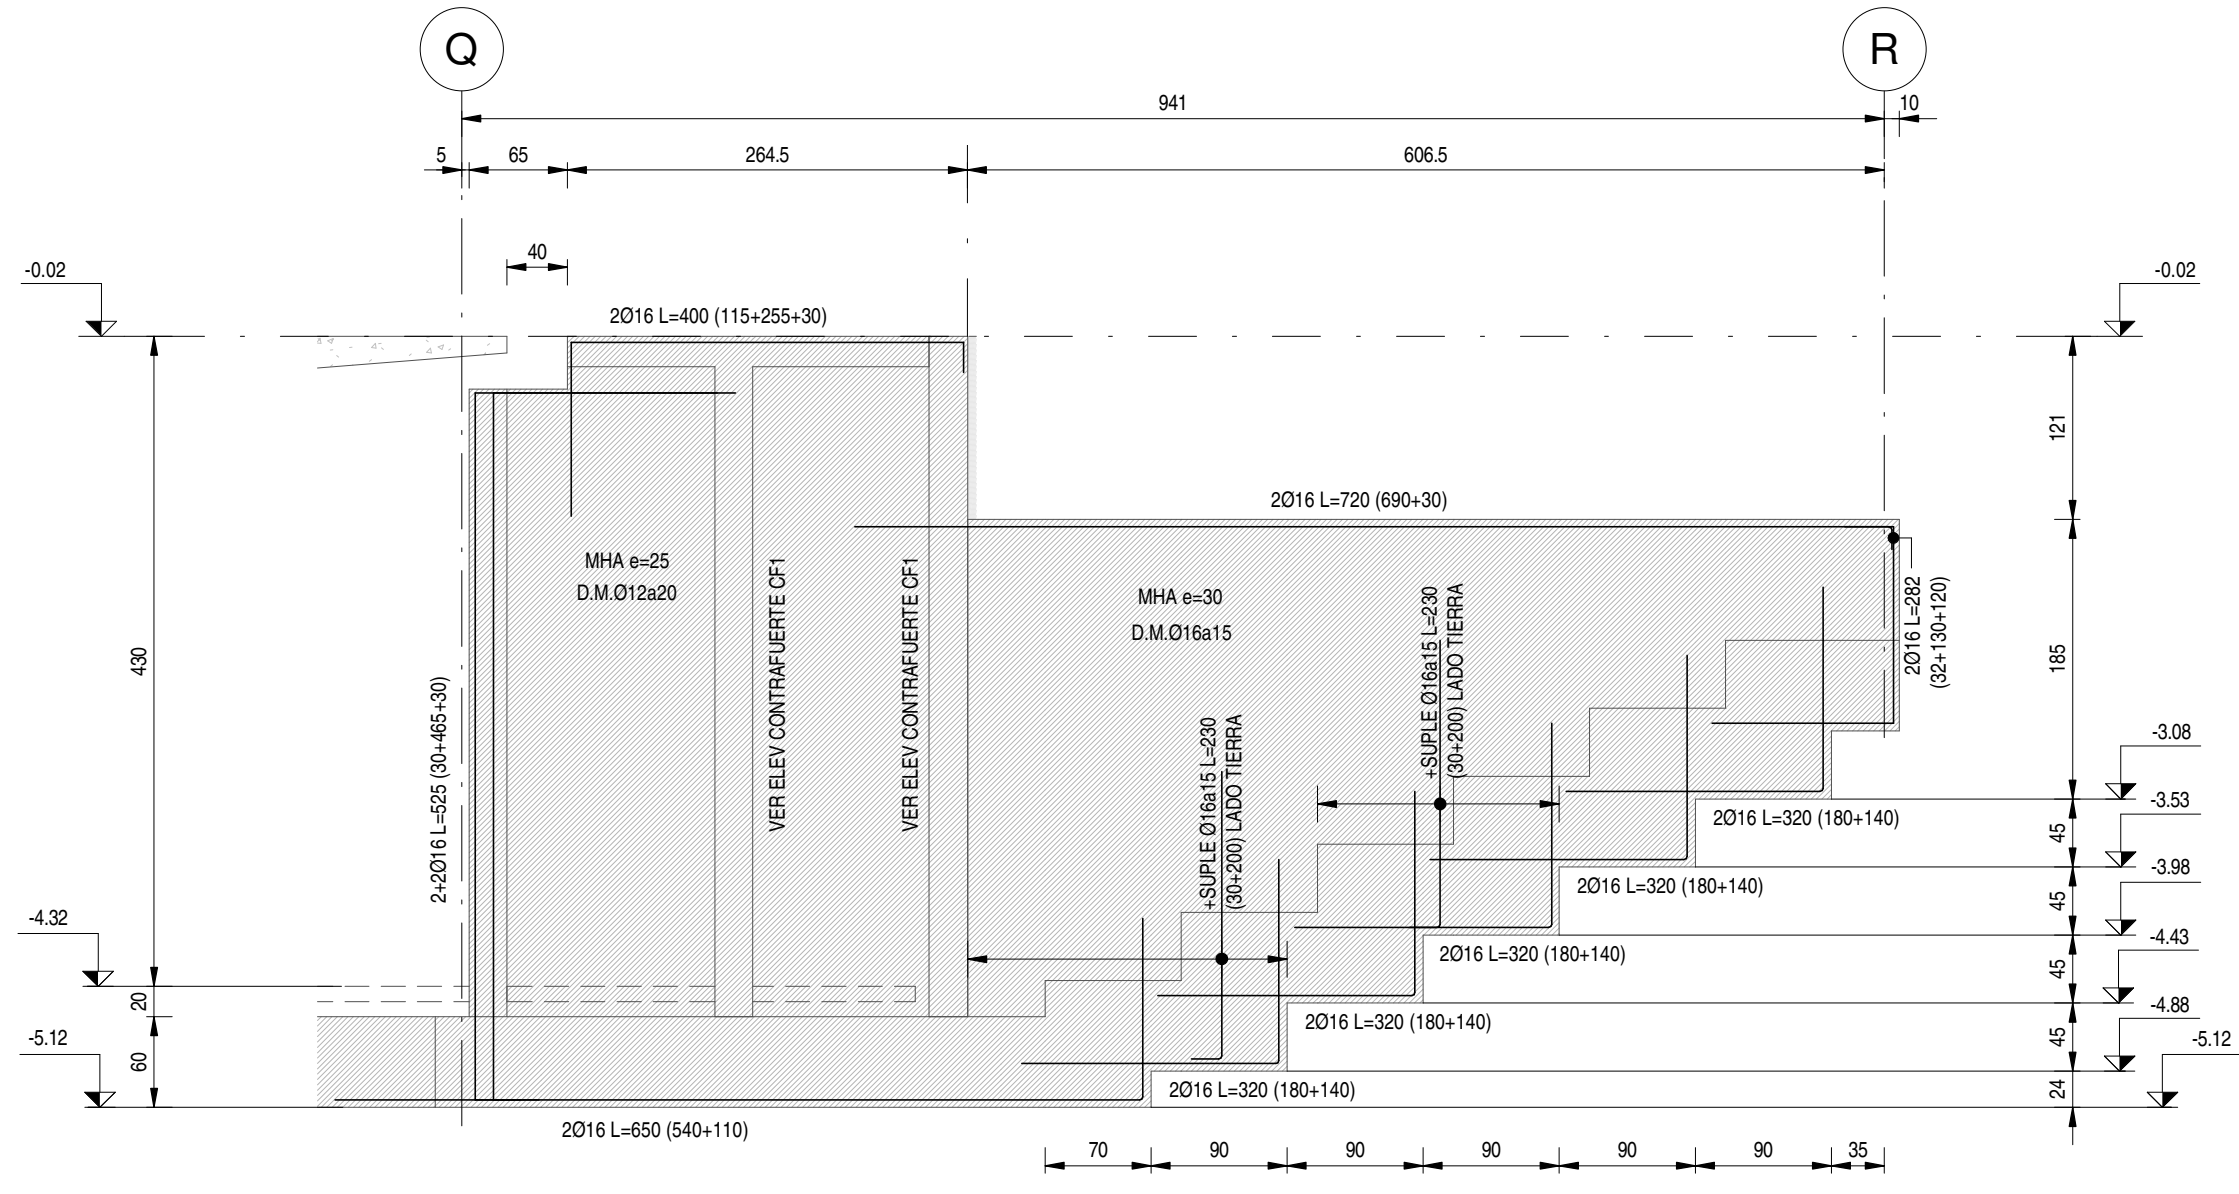


ELEVACION EJE 5a
ESCALA 1 : 50

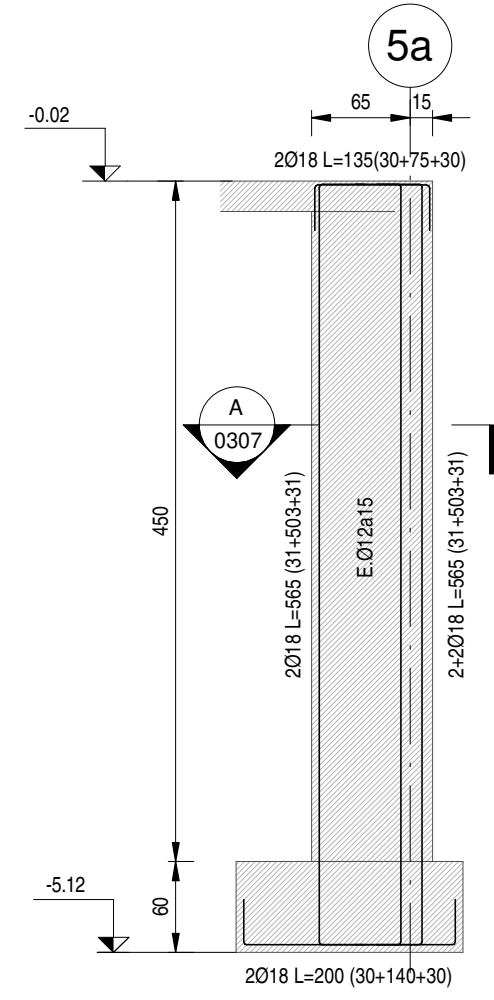


ELEVACION CONTRAFUERTE CF1
ESCALA 1 : 50

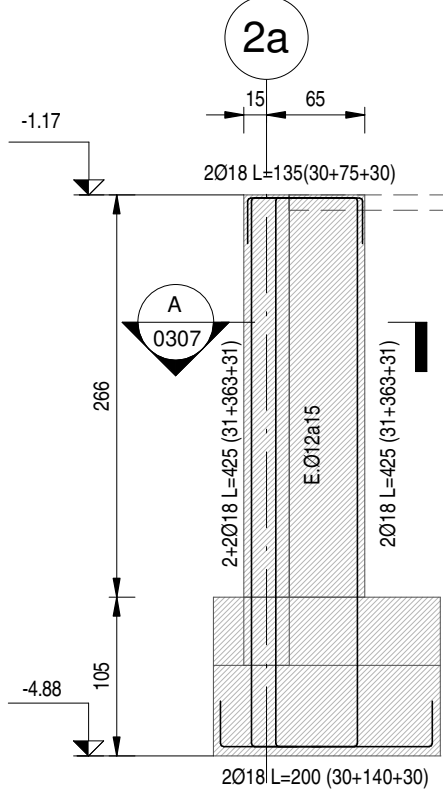


ELEVACION CONTRAFUERTE CF2
ESCALA 1 : 50

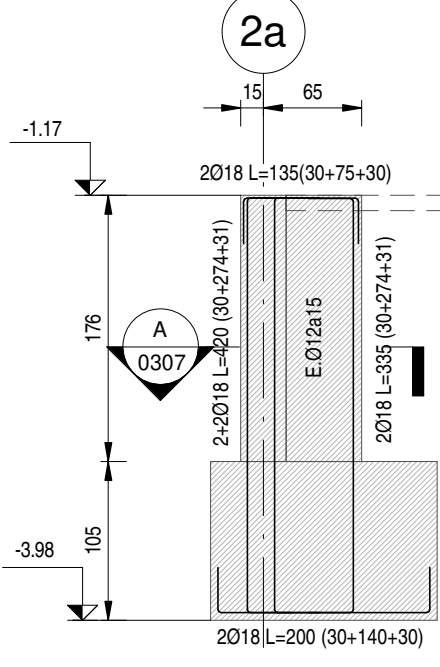


ELEVACION CONTRAFUERTE CF3
ESCALA 1 : 50

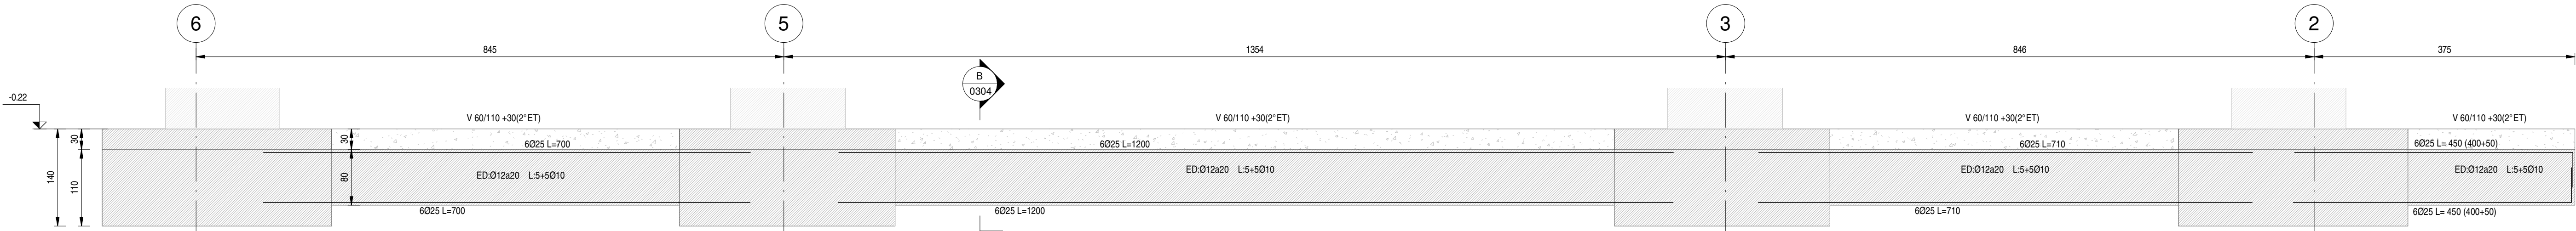


ELEVACION V101
ESCALA 1 : 50

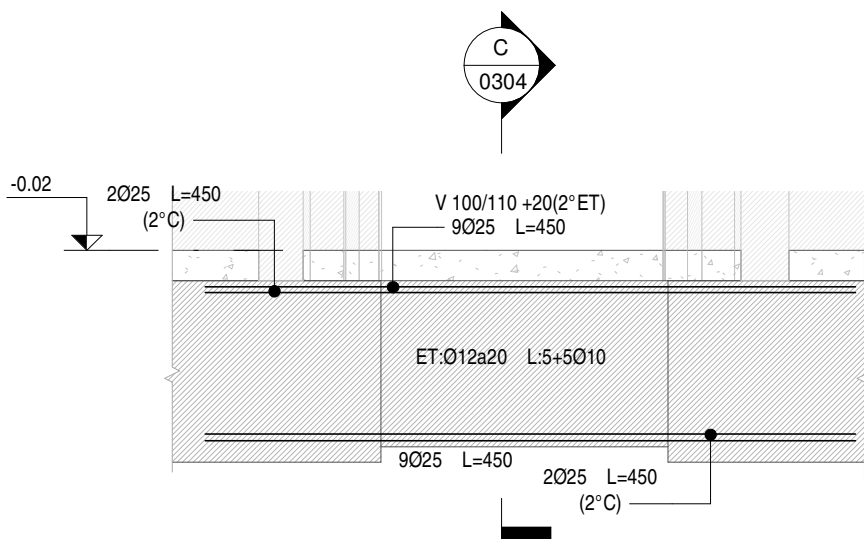

ELEVACION V102
ESCALA 1 : 50

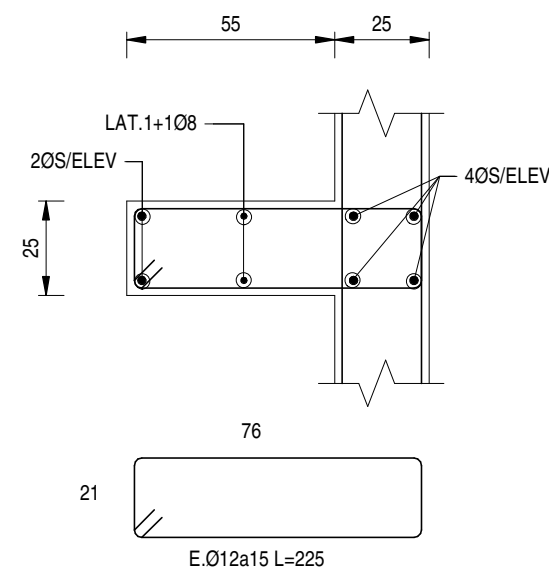

CORTE A
ESC. 1 : 20

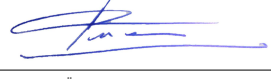E	23.02.2020	L. SQUIRRA M. RENDIEL	CARL LUDERS	ENTREGA ETAPA DE DISEÑO
D	12.02.2020	L. SQUIRRA M. RENDIEL	CARL LUDERS	SE MODIFICA LO INDICADO
C	18.12.2020	L. SQUIRRA M. RENDIEL	CARL LUDERS	SE MODIFICA LO INDICADO
B	12.06.2020	L. SQUIRRA M. RENDIEL	CARL LUDERS	EMITIDO PARA REVISION DEL CLIENTE
A	19.12.2019	S. SAEZ M. RENDIEL	CARL LUDERS	EMITIDO PARA REVISION DEL CLIENTE
Nº	FECHA	DIBUJO/REVISO	APROBO	DETALLE
PROYECTO DE CÁLCULO ESTRUCTURAL				
 SEISMIC PROTECTION TECHNOLOGIES Estadío de Obras, Las Condes, Santiago - Chile TELÉFONO: +56 2 2407 1100 CONTACTO: info@sirve.cl WEB: www.sirve.cl  CARL LUDERS SCHWARZENBERG Ingeniero Civil E.C. Dipl. Ing. Technisches Hochschule Darmstadt 3.639/1723				
PROYECTO RECUPERACION BASILICA DEL SALVADOR				
UBICACION FUNDACIONES, LOSA BASE Y SISTEMA AISLAMIENTO SISMICO				
GUBRNE CALLE HUERFANOS 1796 - SANTIAGO				
FUNDACION BASILICA DEL SALVADOR RUT: 65.148.985-6				
CONTENIDO ELEVACIONES EJES 2a - 5a y ELEVACIONES DE VIGAS				REVISION
				E
CODIGO DEL DOCUMENTO 18088-01-PL-EST-0307		FORMATO A3	ESCALA 1:50	FECHA 23.02.2020