



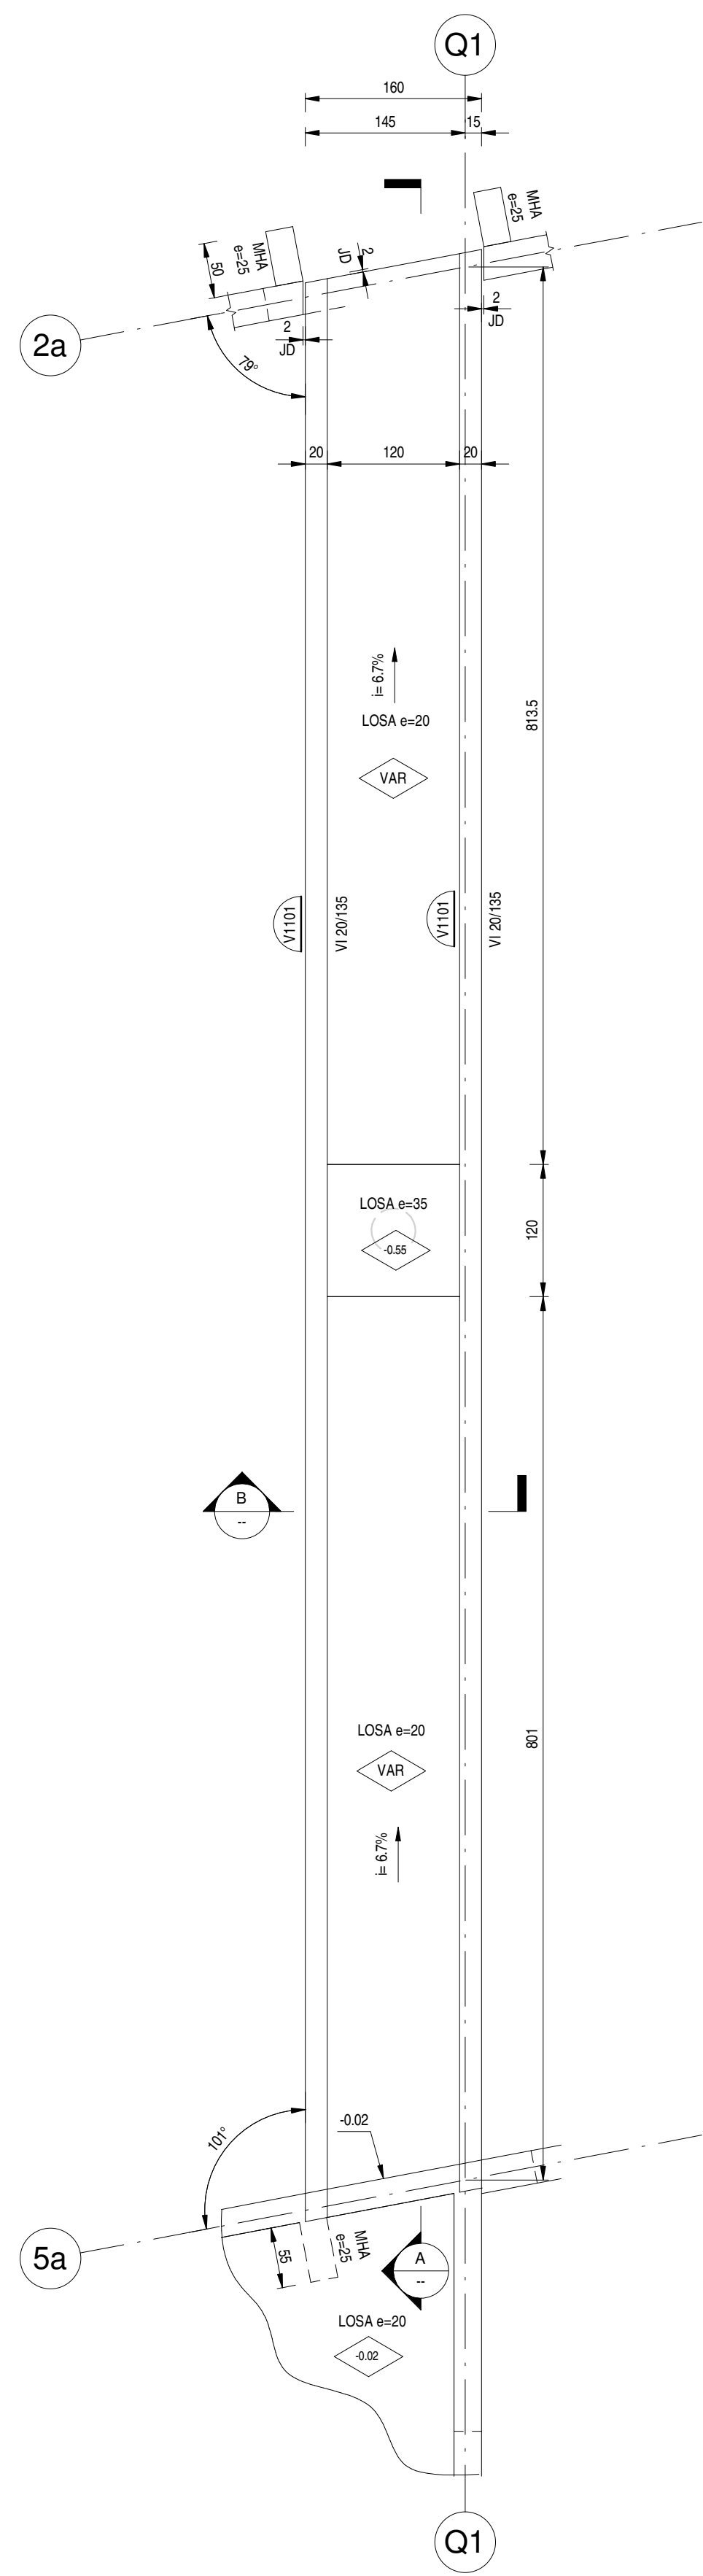


RAMPA  
PLANTA DE ESTRUCTURA  
ESCALA 1 : 50

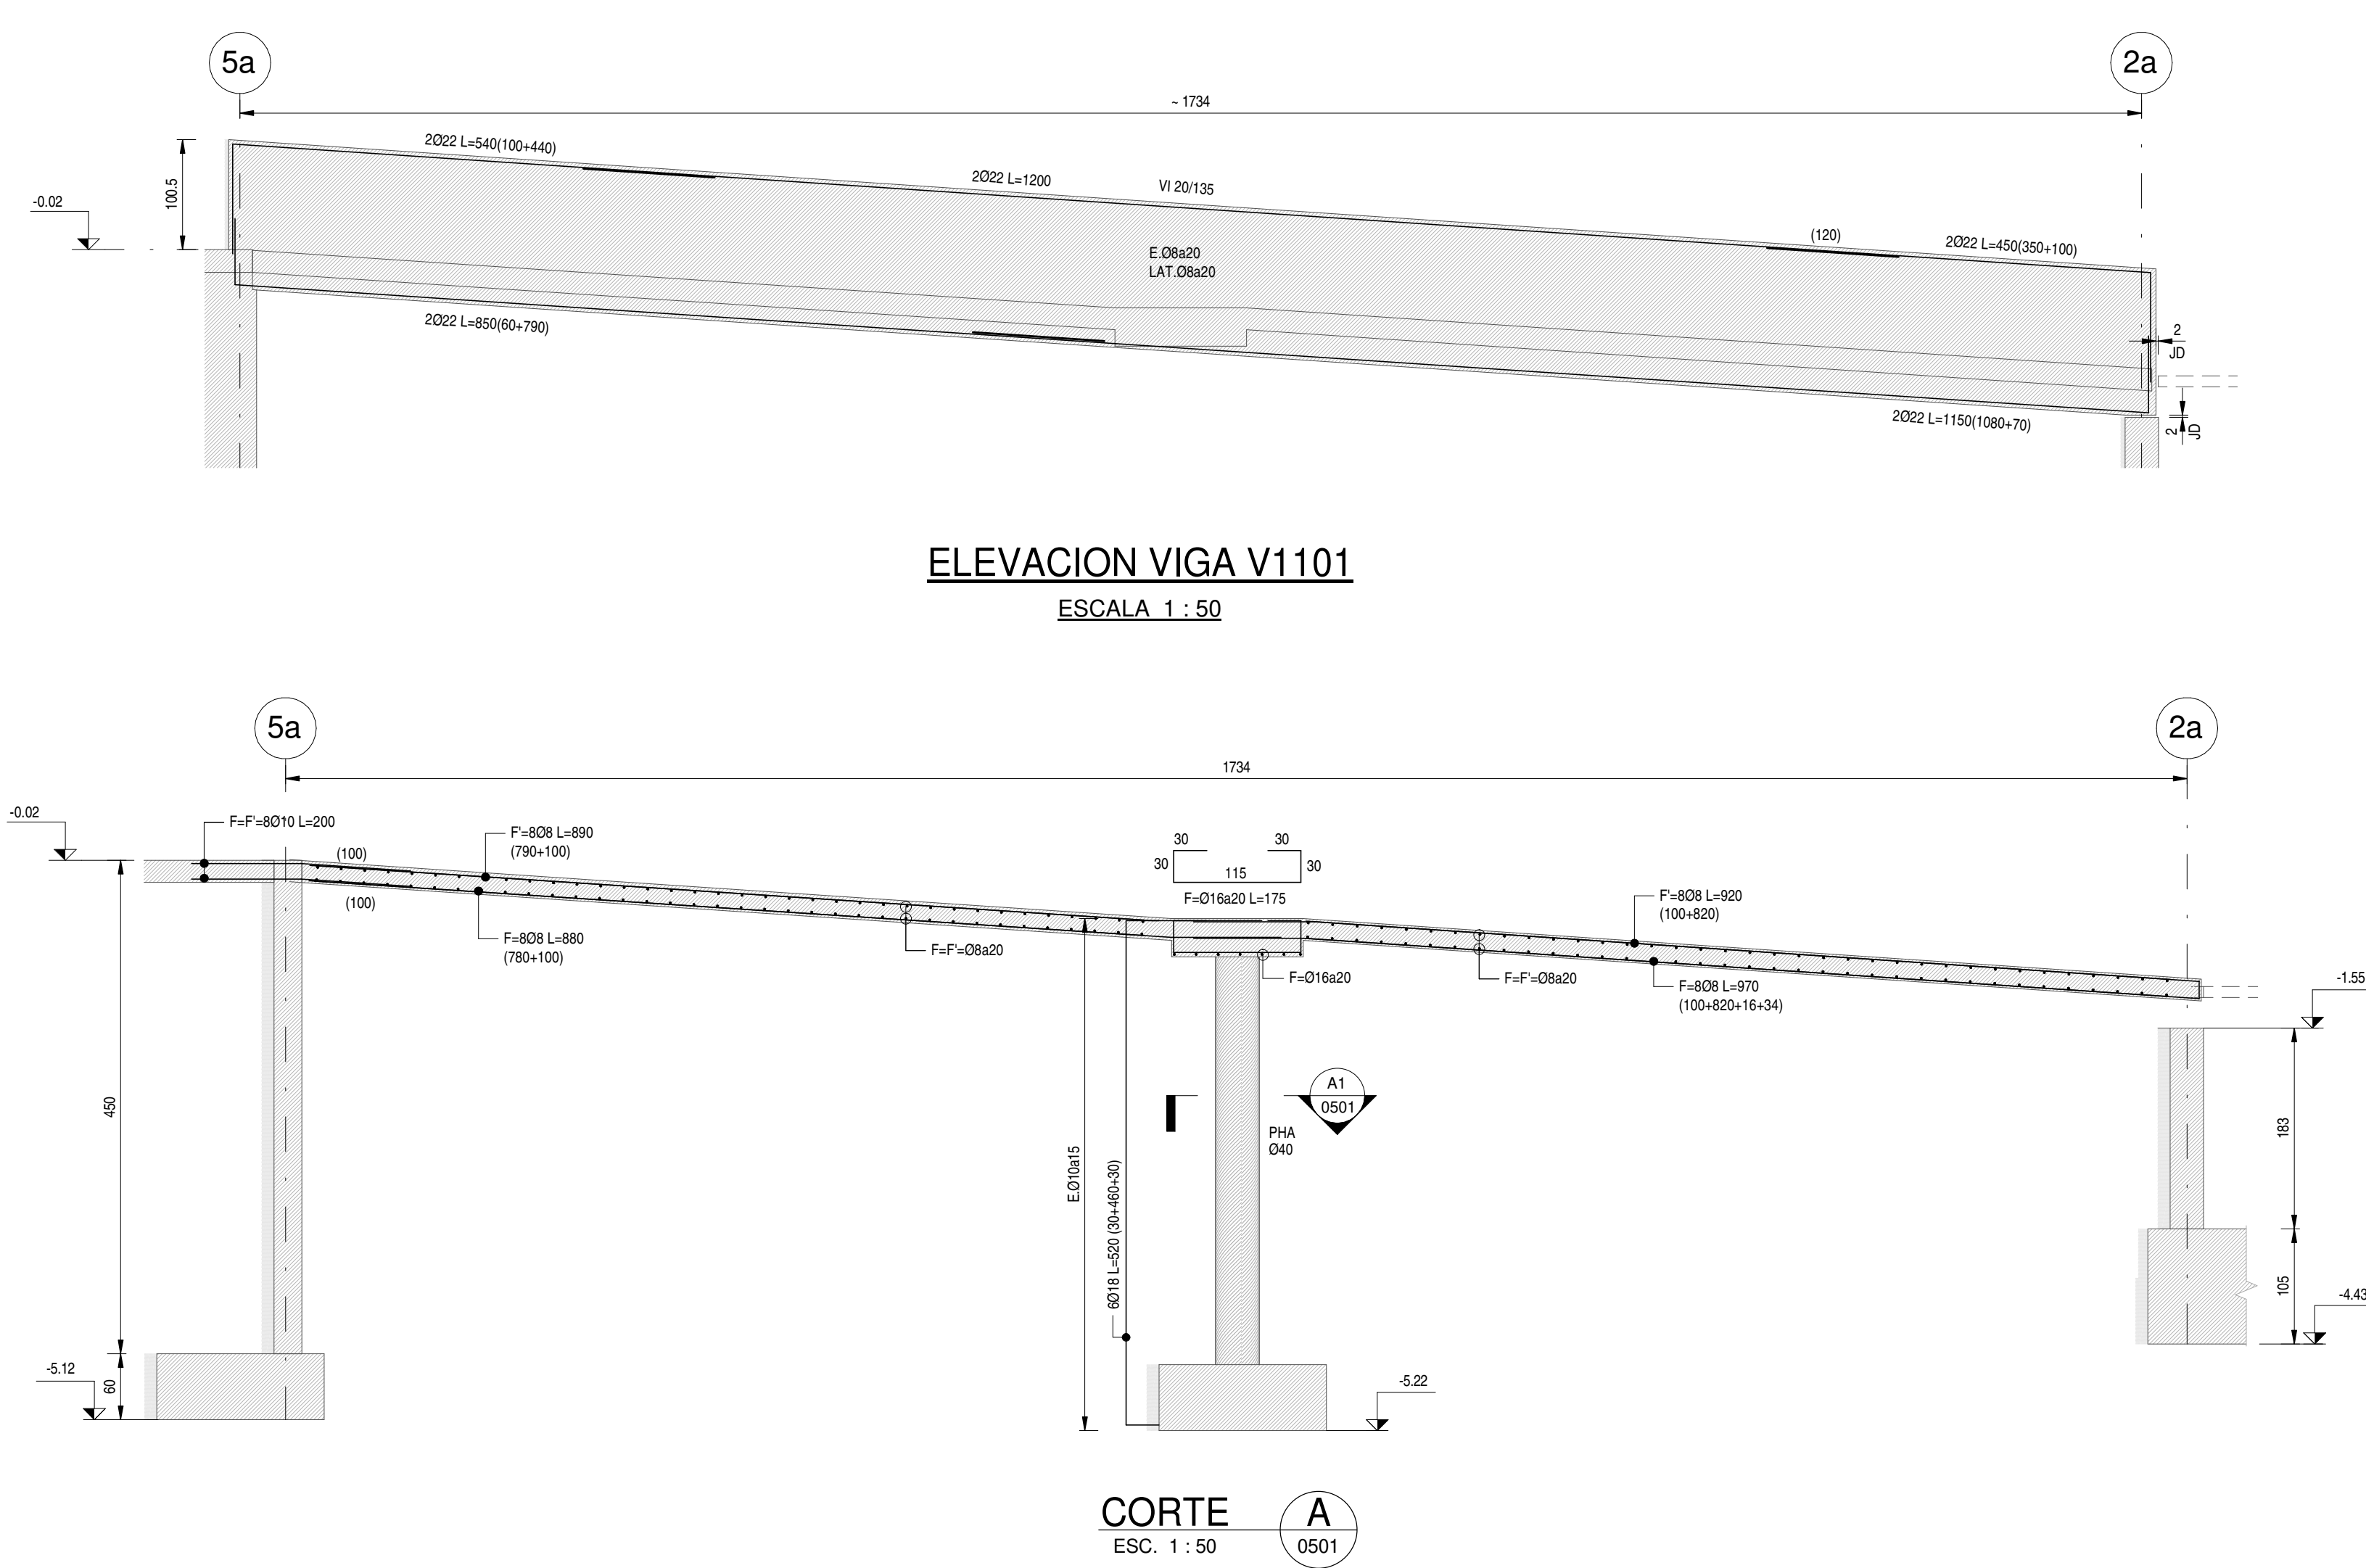


ELEVACION VIGA V1101  
ESCALA 1 : 50


CORTE A  
ESC. 1 : 50

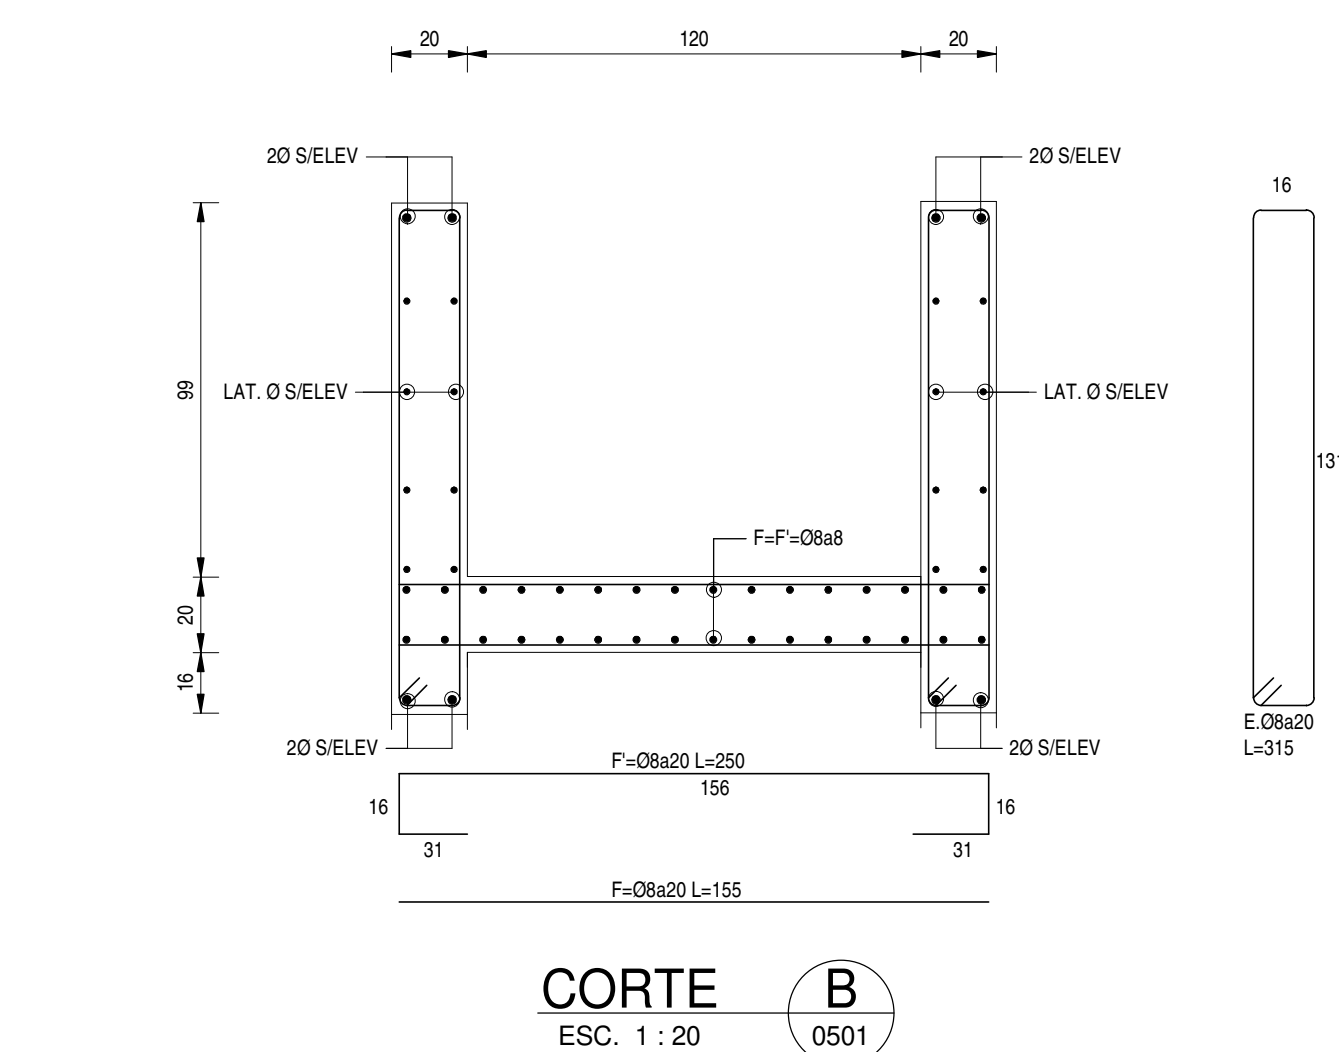


CORTE B  
ESC. 1 : 20

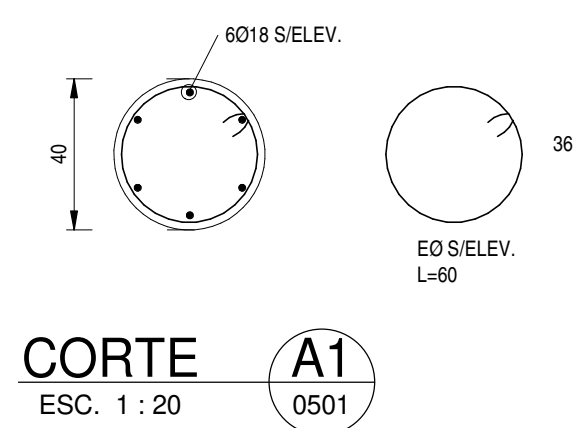


CORTE A1  
ESC. 1 : 20

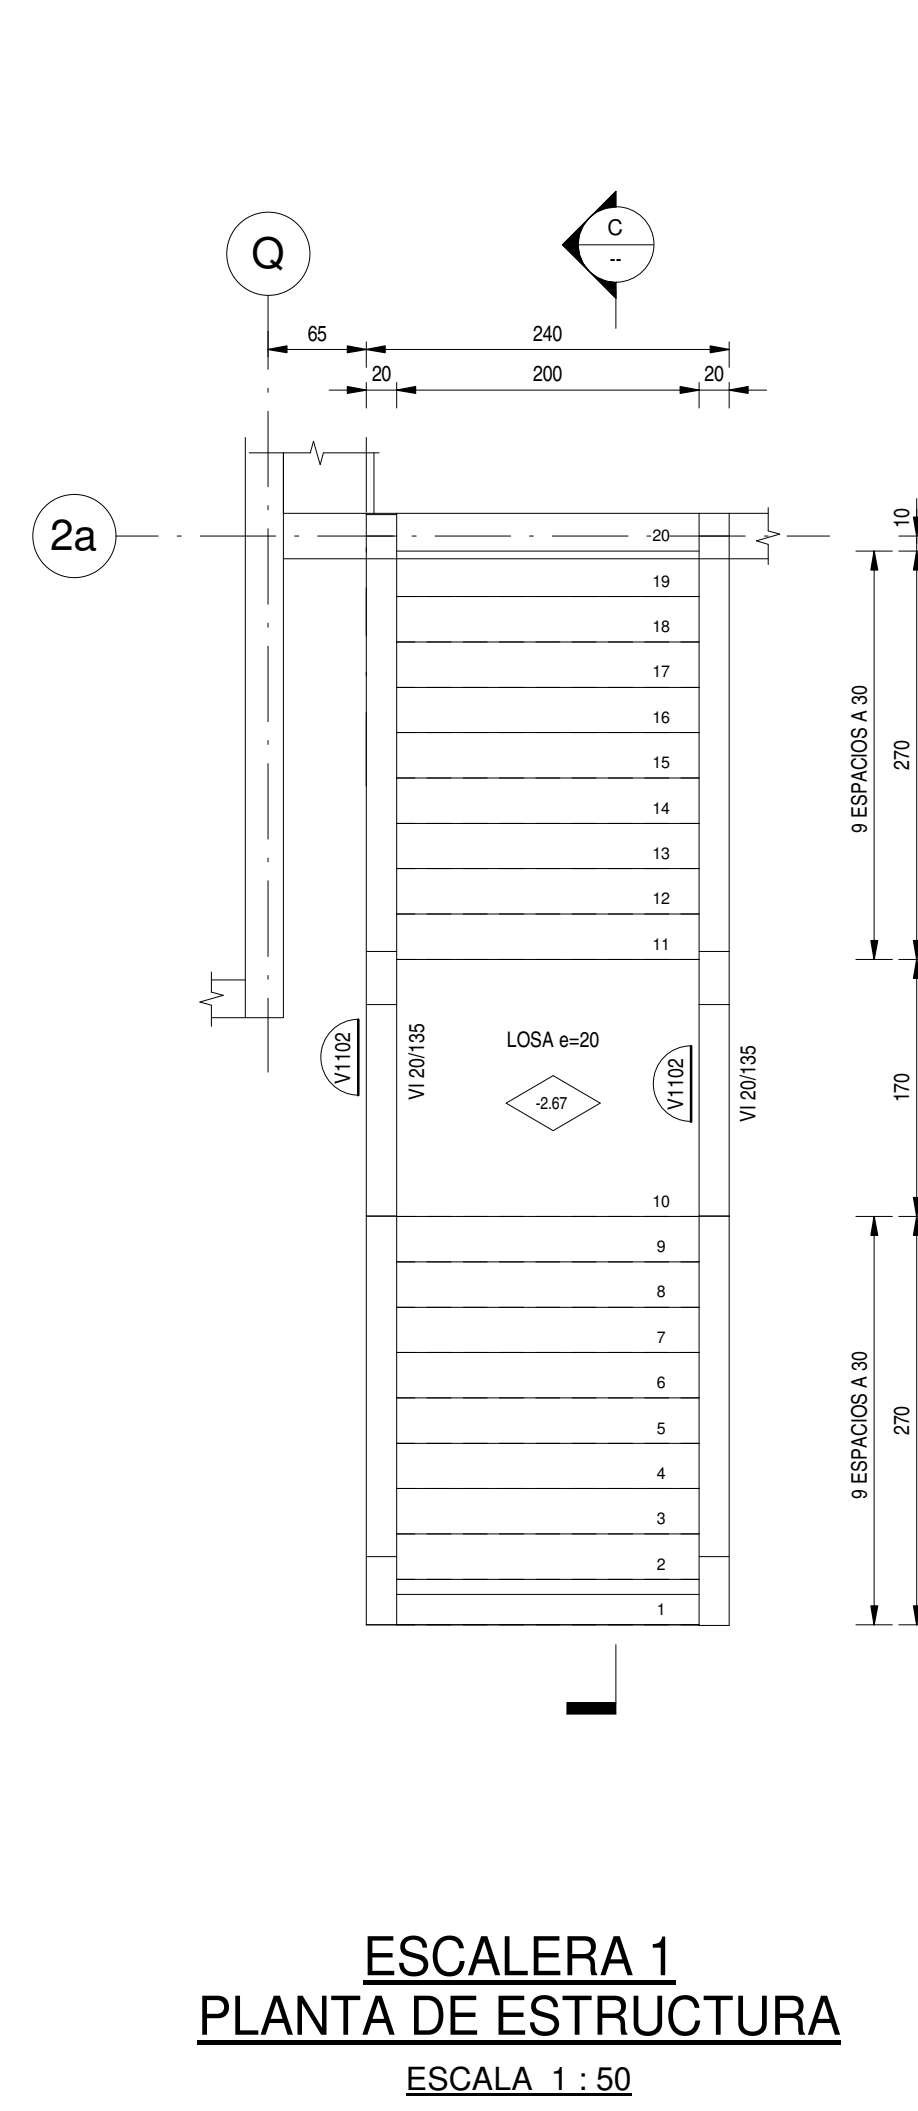


ESCALERA 1  
PLANTA DE ESTRUCTURA  
ESCALA 1 : 50

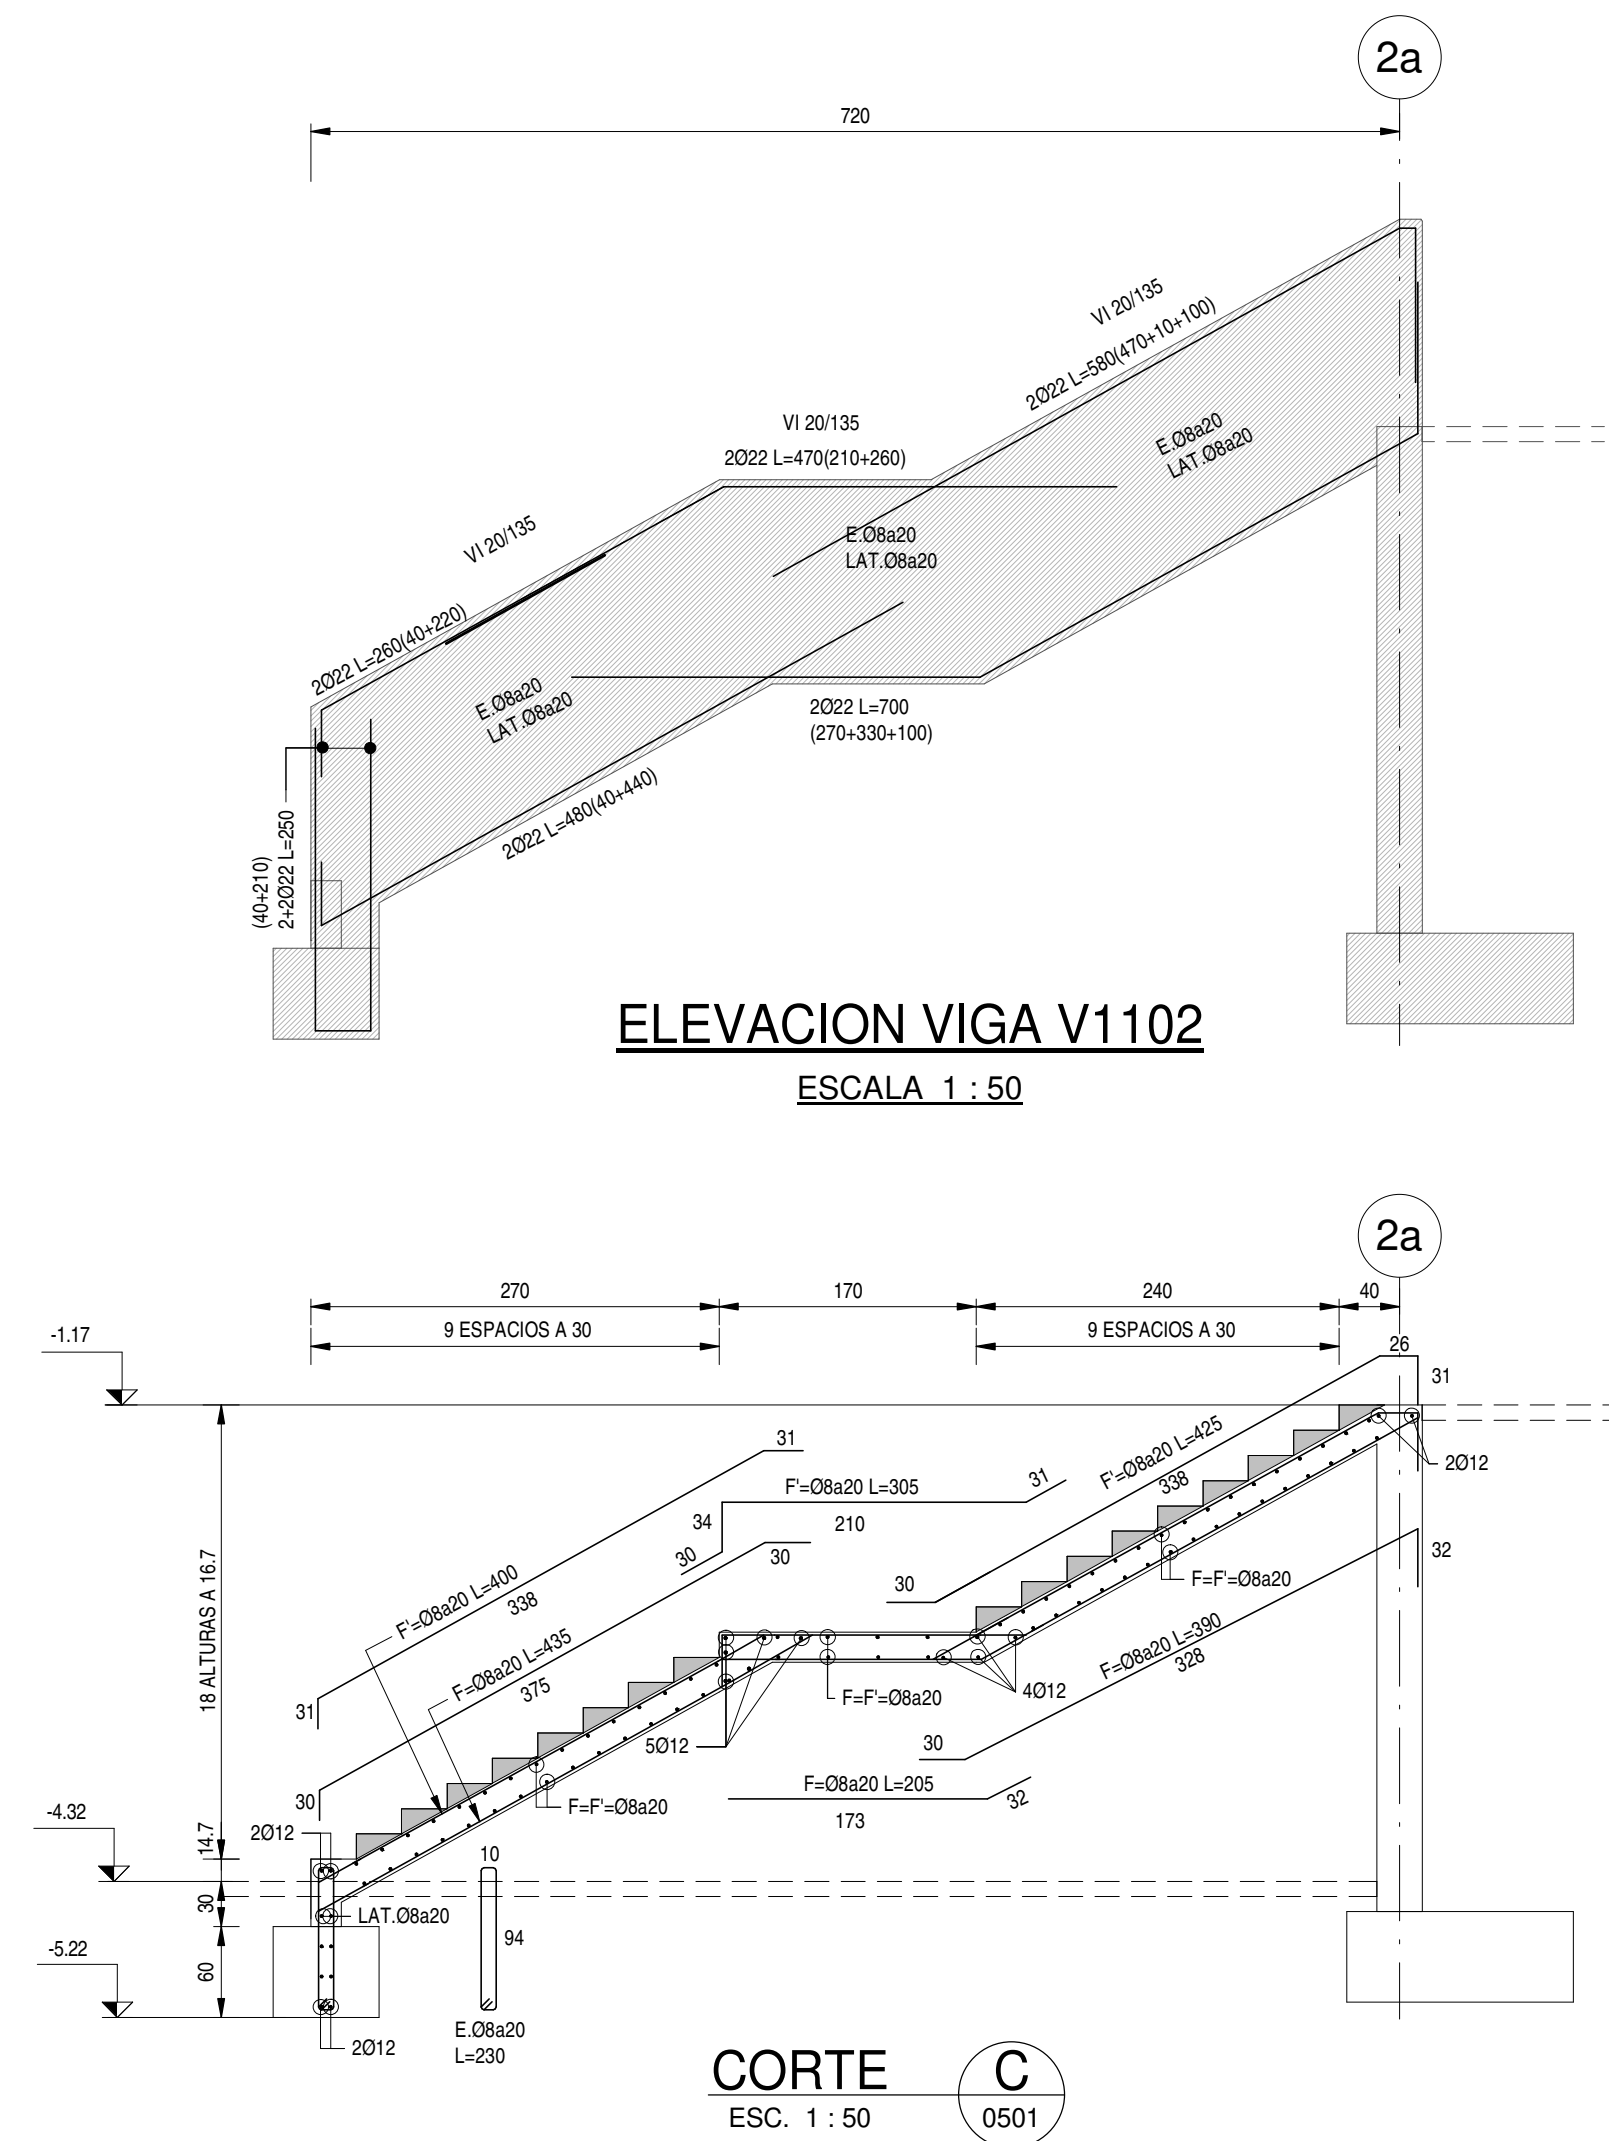


CORTE C  
ESC. 1 : 50

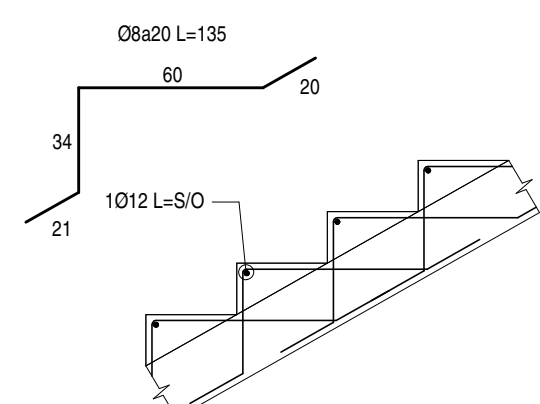


DETALLE DE GRADAS  
ESCALA 1 : 25

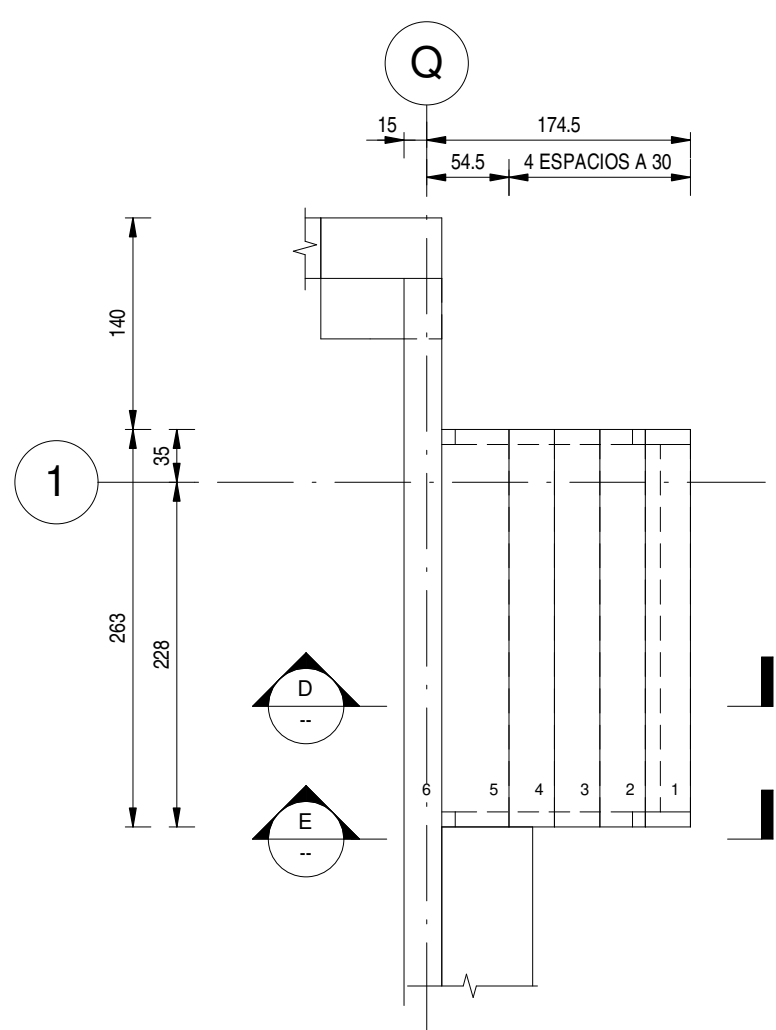

ESCALERA 2  
PLANTA DE ESTRUCTURA  
ESCALA 1 : 50

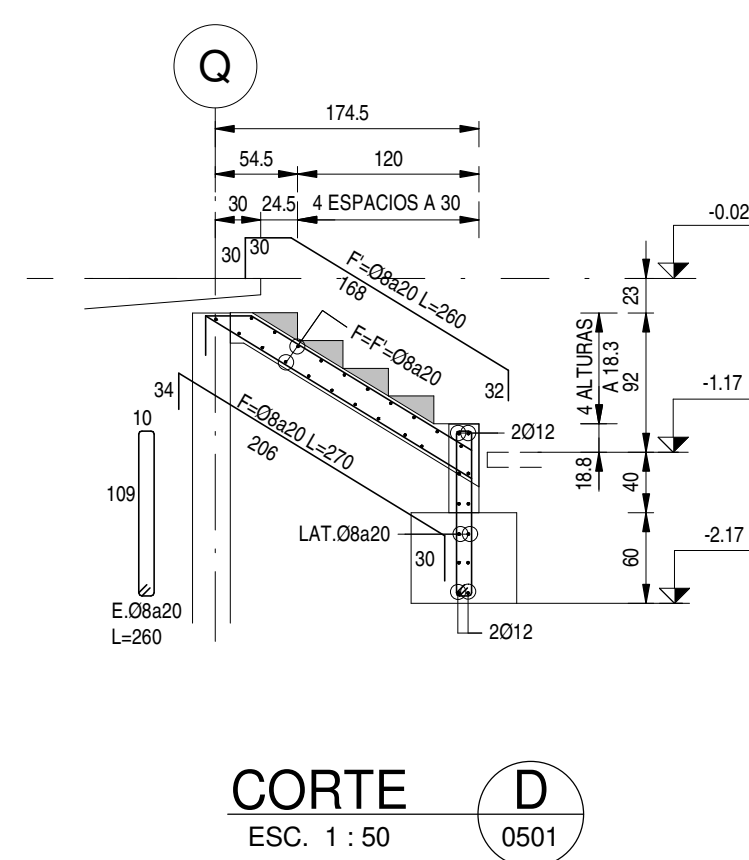

CORTE D  
ESC. 1 : 50

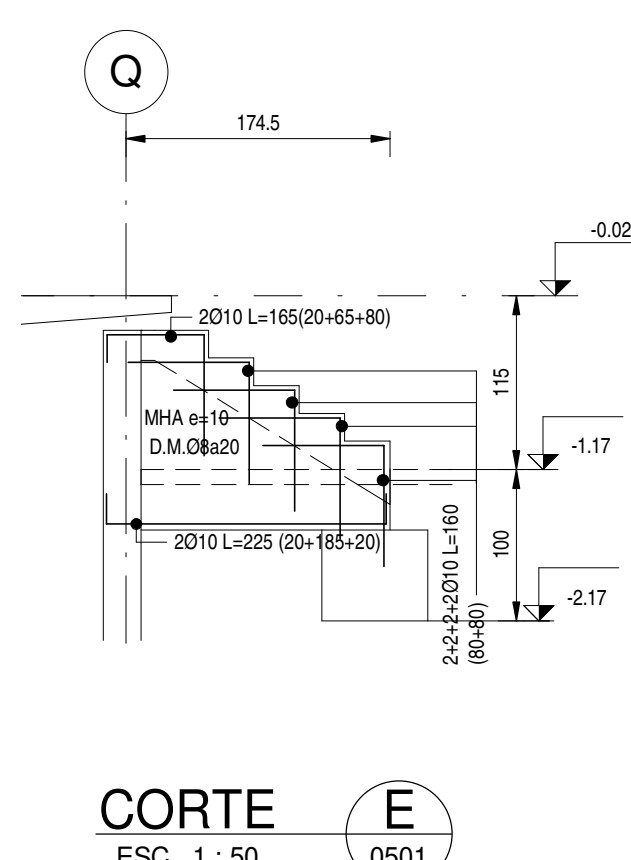

CORTE E  
ESC. 1 : 50

|                                                                                       |            |                       |             |                                   |                  |
|---------------------------------------------------------------------------------------|------------|-----------------------|-------------|-----------------------------------|------------------|
|                                                                                       |            |                       |             |                                   |                  |
| C                                                                                     | 23.02.2020 | ESQUERDA<br>M. RENDIL | CARL LUDERS | ENTREGA ETAPA DE DISEÑO           |                  |
| B                                                                                     | 12.06.2020 | ESQUERDA<br>M. RENDIL | CARL LUDERS | EMITIDO PARA REVISION DEL CLIENTE |                  |
| A                                                                                     | 19.12.2019 | S. SAEZ<br>M. RENDIL  | CARL LUDERS | EMITIDO PARA REVISION DEL CLIENTE |                  |
| Nº                                                                                    | FECHA      | DIBUJO/REVISO         | APROBÓ      | DETALLE                           |                  |
| PROYECTO DE CÁLCULO ESTRUCTURAL                                                       |            |                       |             |                                   |                  |
|  |            |                       |             |                                   |                  |
| PROYECTO RECUPERACION BASILICA DEL SALVADOR                                           |            |                       |             |                                   |                  |
| UBICACION FUNDACIONES, LOSA BASE y SISTEMA AISLAMIENTO SÍSMICO                        |            |                       |             |                                   |                  |
| GIRTE FUNDACION BASILICA DEL SALVADOR                                                 |            |                       |             |                                   |                  |
| CONTENIDO DETALLE DE ESCALERAS E-01, E-02 y RAMPA                                     |            |                       |             |                                   |                  |
| CÓDIGO DEL DOCUMENTO 18088-01-PL-EST-0501                                             |            |                       |             |                                   | FECHA 23.02.2020 |