
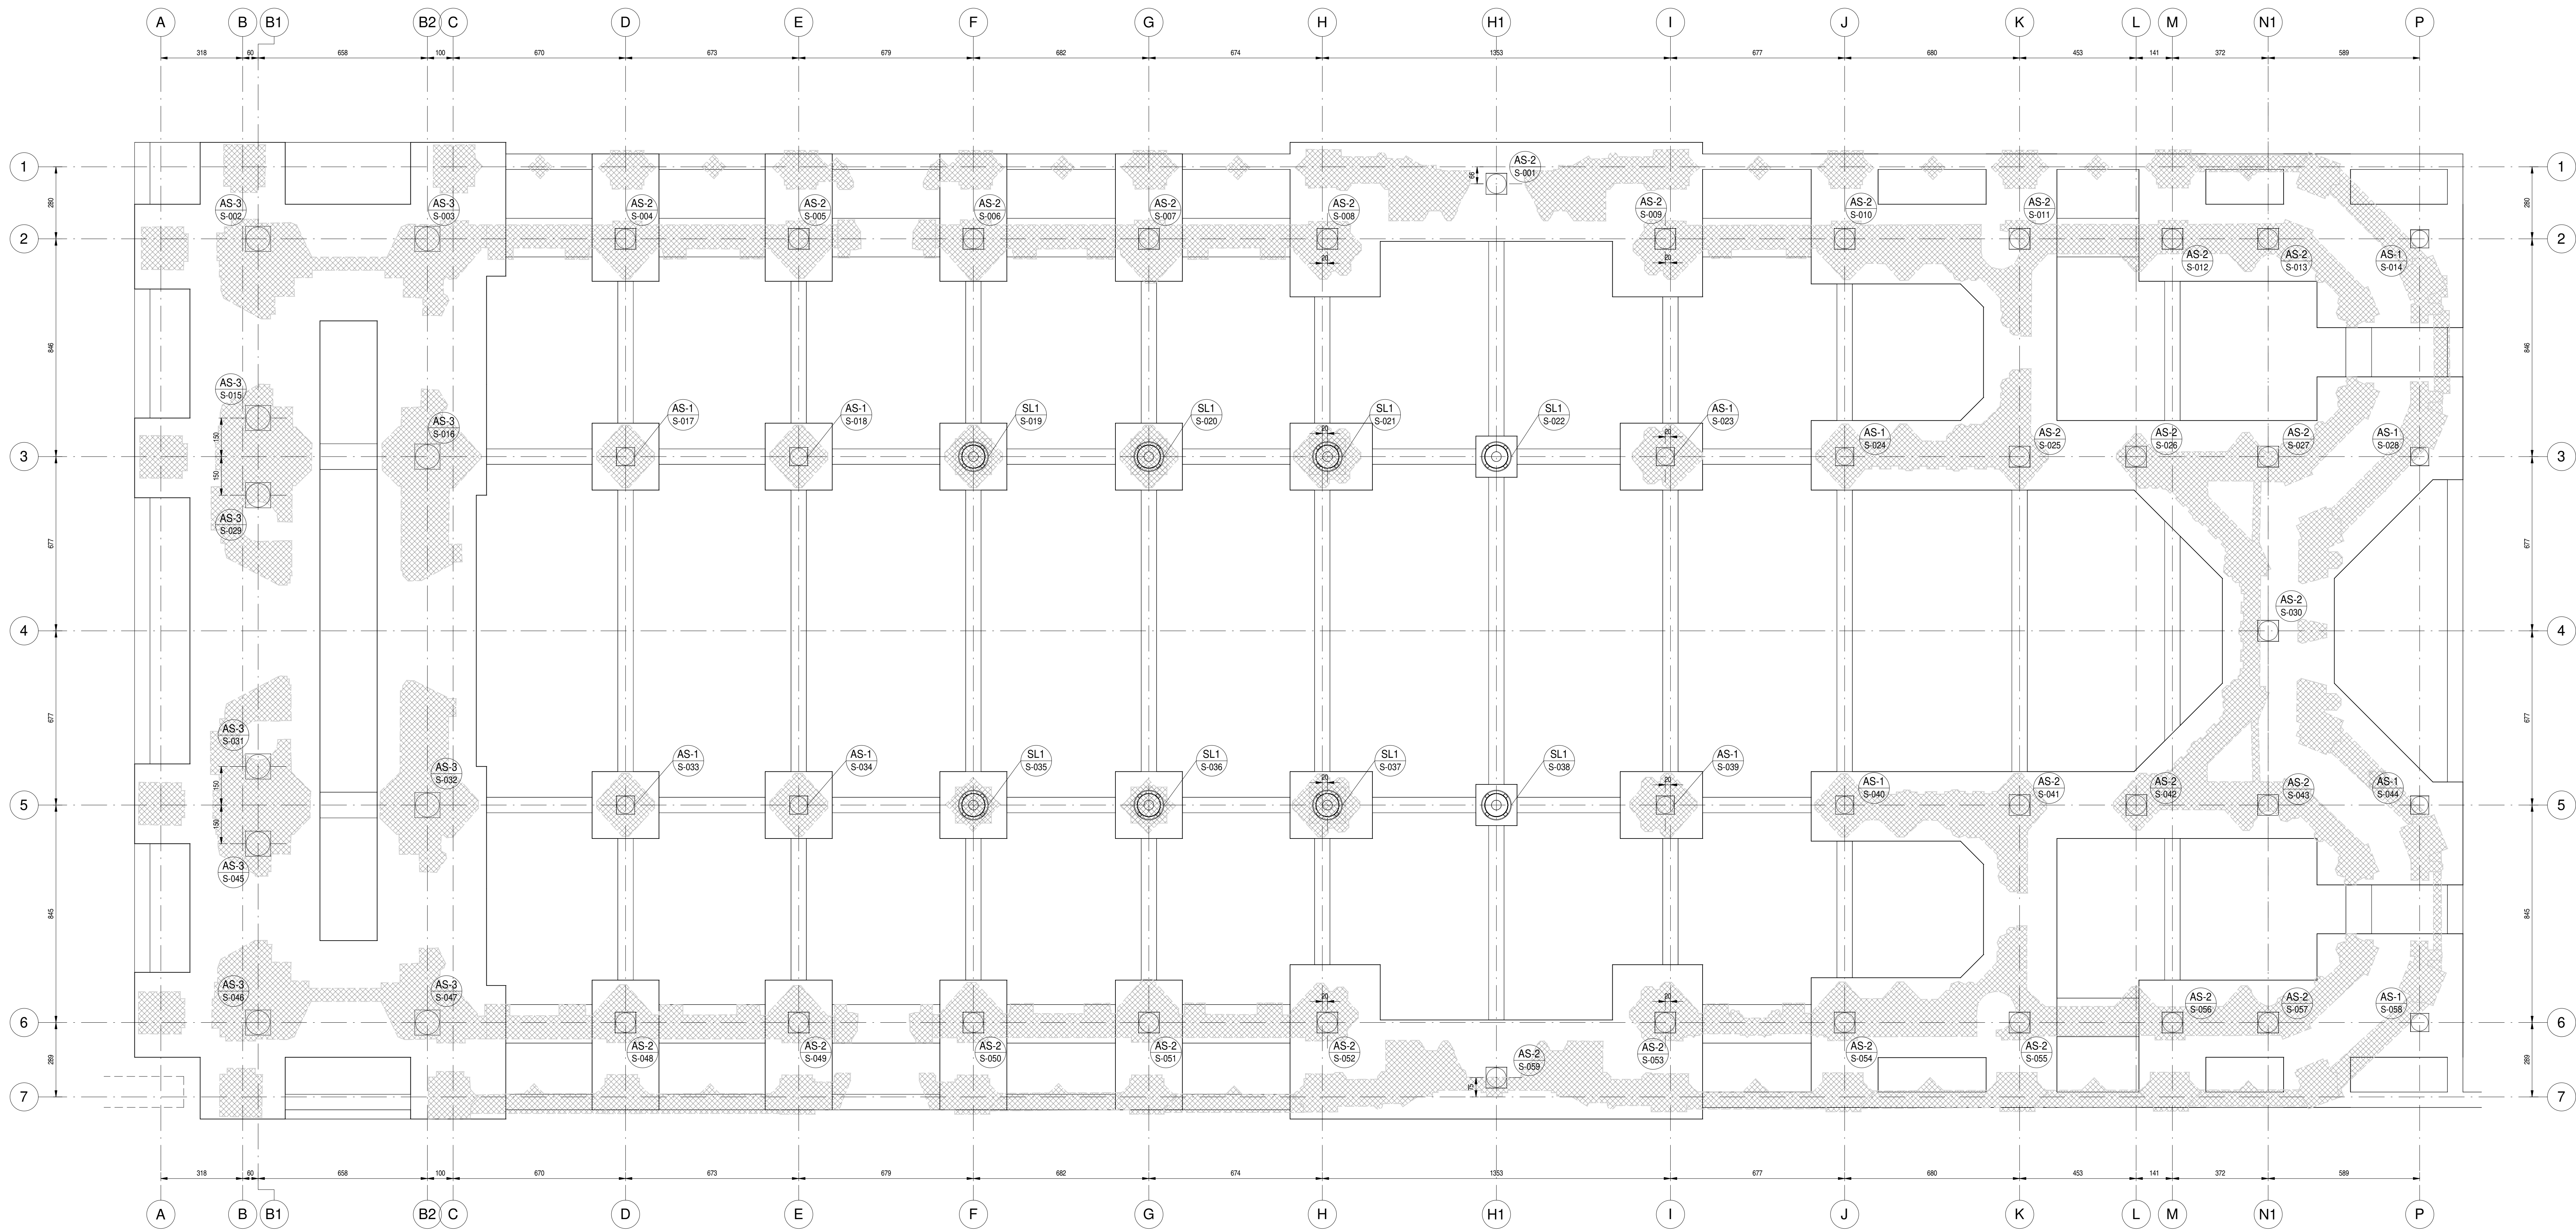


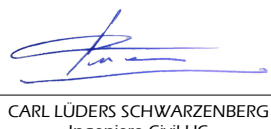

ELEMENTOS CENTRADOS A EJE (S.I.C.)
PLANTA DE DISTRIBUCION DE DISPOSITIVOS
ESCALA 1 : 100

TABLA DE DISPOSITIVOS		
TIPO	CANTIDAD*	ALTURA TOTAL** (mm)
AS-1	12	38.7
AS-2	29	38.7
AS-3	10	39.7
SL1	8	11.4
TOTAL	59	

*NO INCLUYE LOS PROTOTIPOS
**PUEDE VARIAR SEGUN FABRICANTE

E	23.02.2020	L. SQUIBBA M. RENDEL	CARL LUDERS	ENTREGA ETAPA DE DISEÑO
D	12.06.2020	L. SQUIBBA M. RENDEL	CARL LUDERS	EMITIDO PARA REVISION DEL CLIENTE
C	19.12.2019	S. SAEZ M. RENDEL	CARL LUDERS	EMITIDO PARA REVISION DEL CLIENTE
B	30.07.2019	S. SAEZ M. RENDEL	CARL LUDERS	EMITIDO PARA PRESUPUESTO
A	08.07.2019	S. SAEZ M. RENDEL	CARL LUDERS	EMITIDO PARA PRESUPUESTO
Nº	FECHA	DIBUJO/REVISO	APROBO	DETALLE
PROYECTO DE CÁLCULO ESTRUCTURAL				
 SEISMIC PROTECTION TECHNOLOGIES Estudio de Diseño, Ingeniería, Construcción y Mantenimiento de Estructuras y Equipos de Protección Sísmica  CARL LUDERS SCHWARZENBERG Ingeniero Civil Dipl. Ing. Technische Hochschule Darmstadt 3.639.1723				
PROYECTO RECUPERACION BASILICA DEL SALVADOR				
UBICACION FUNDACIONES, LOSA BASE Y SISTEMA AISLAMIENTO SISMICO				
CALLE HUERFANOS 1796 - SANTIAGO				
FUNDACION BASILICA DEL SALVADOR				
RUT: 65.168.985-6				
CONTENIDO PLANTA DE DISTRIBUCION DE DISPOSITIVOS				REVISION
				E
CODIGO DEL DOCUMENTO 18088-01-PL-EST-0801		FORMATO AD	ESCALA 1:100	FECHA 23.02.2020