



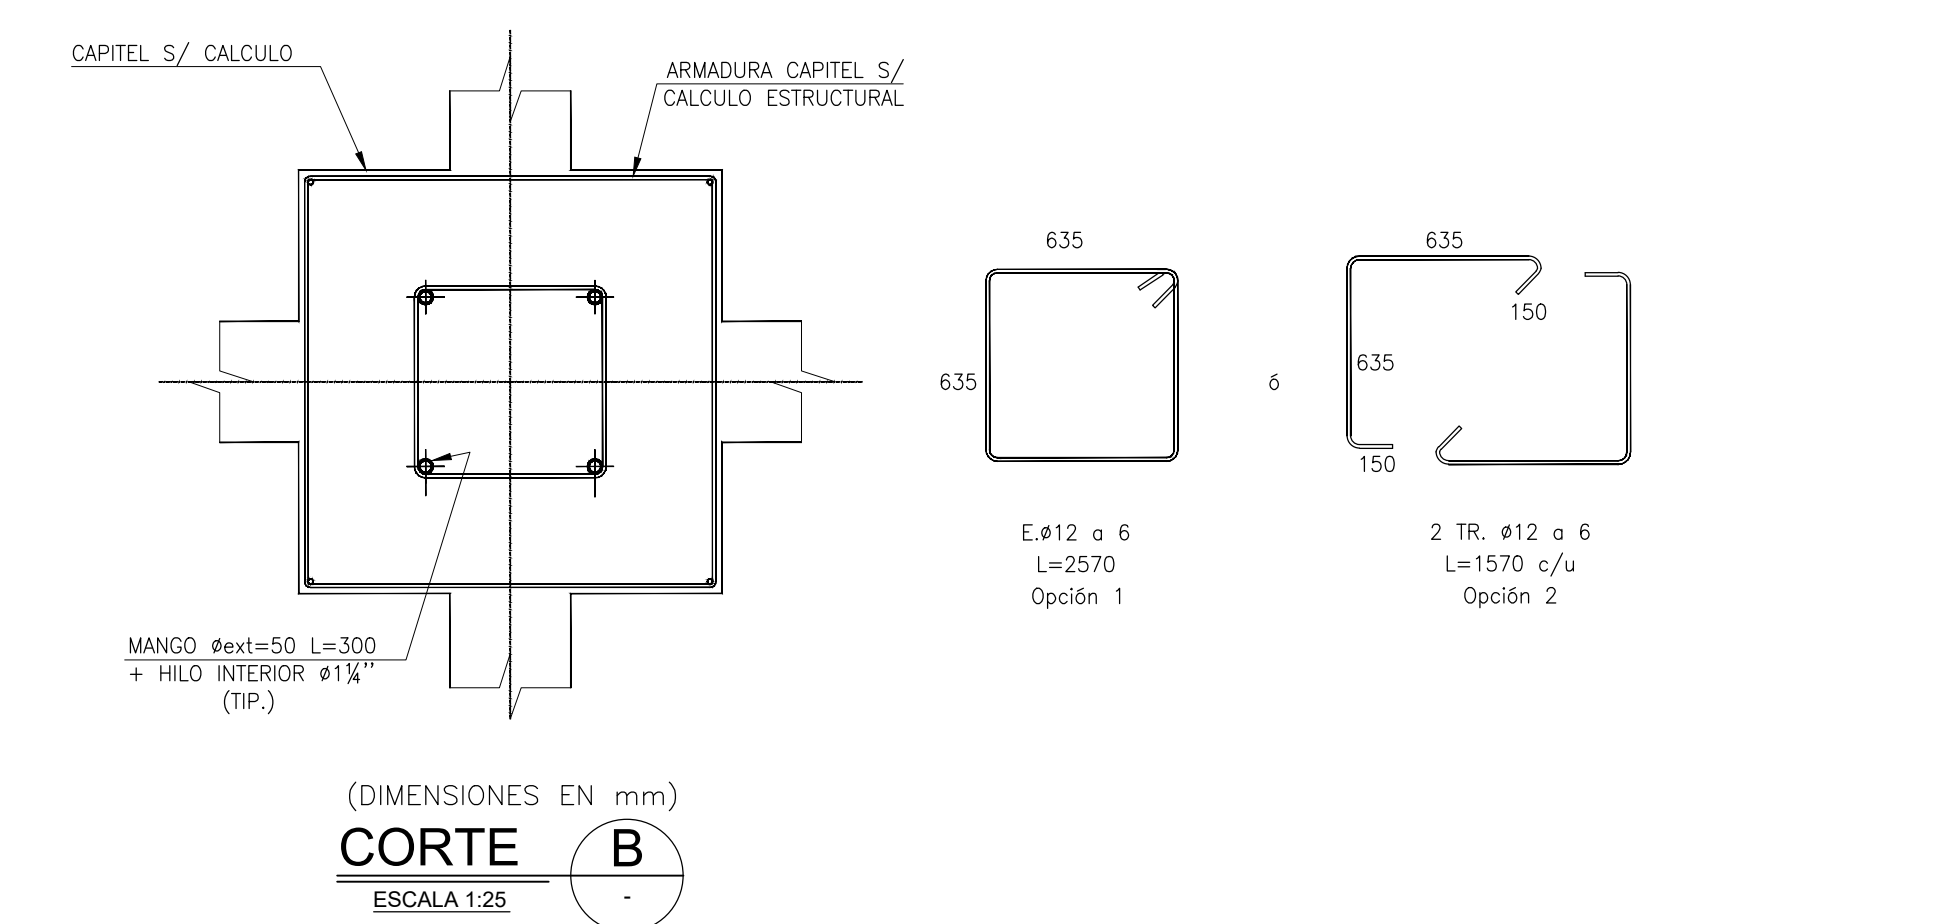


TIPO	CANTIDAD		D. ext. (cm)	REC. (cm)	D. int. (cm)	ts (cm)	nr	tr (cm)	Bf (cm)	tf (cm)	Hr (cm)	Ht (cm)	NUCLEO PLOMO
	OBRA	PROTOTIPOS											
AS1	12	2	66	0,5	5	0,3	35	0,7	71	2,0	24,5	38,7	SI

** DIMENSIONES PUEDEN VARIAR DE ACUERDO AL PROVEEDOR DE DISPOSITIVOS.

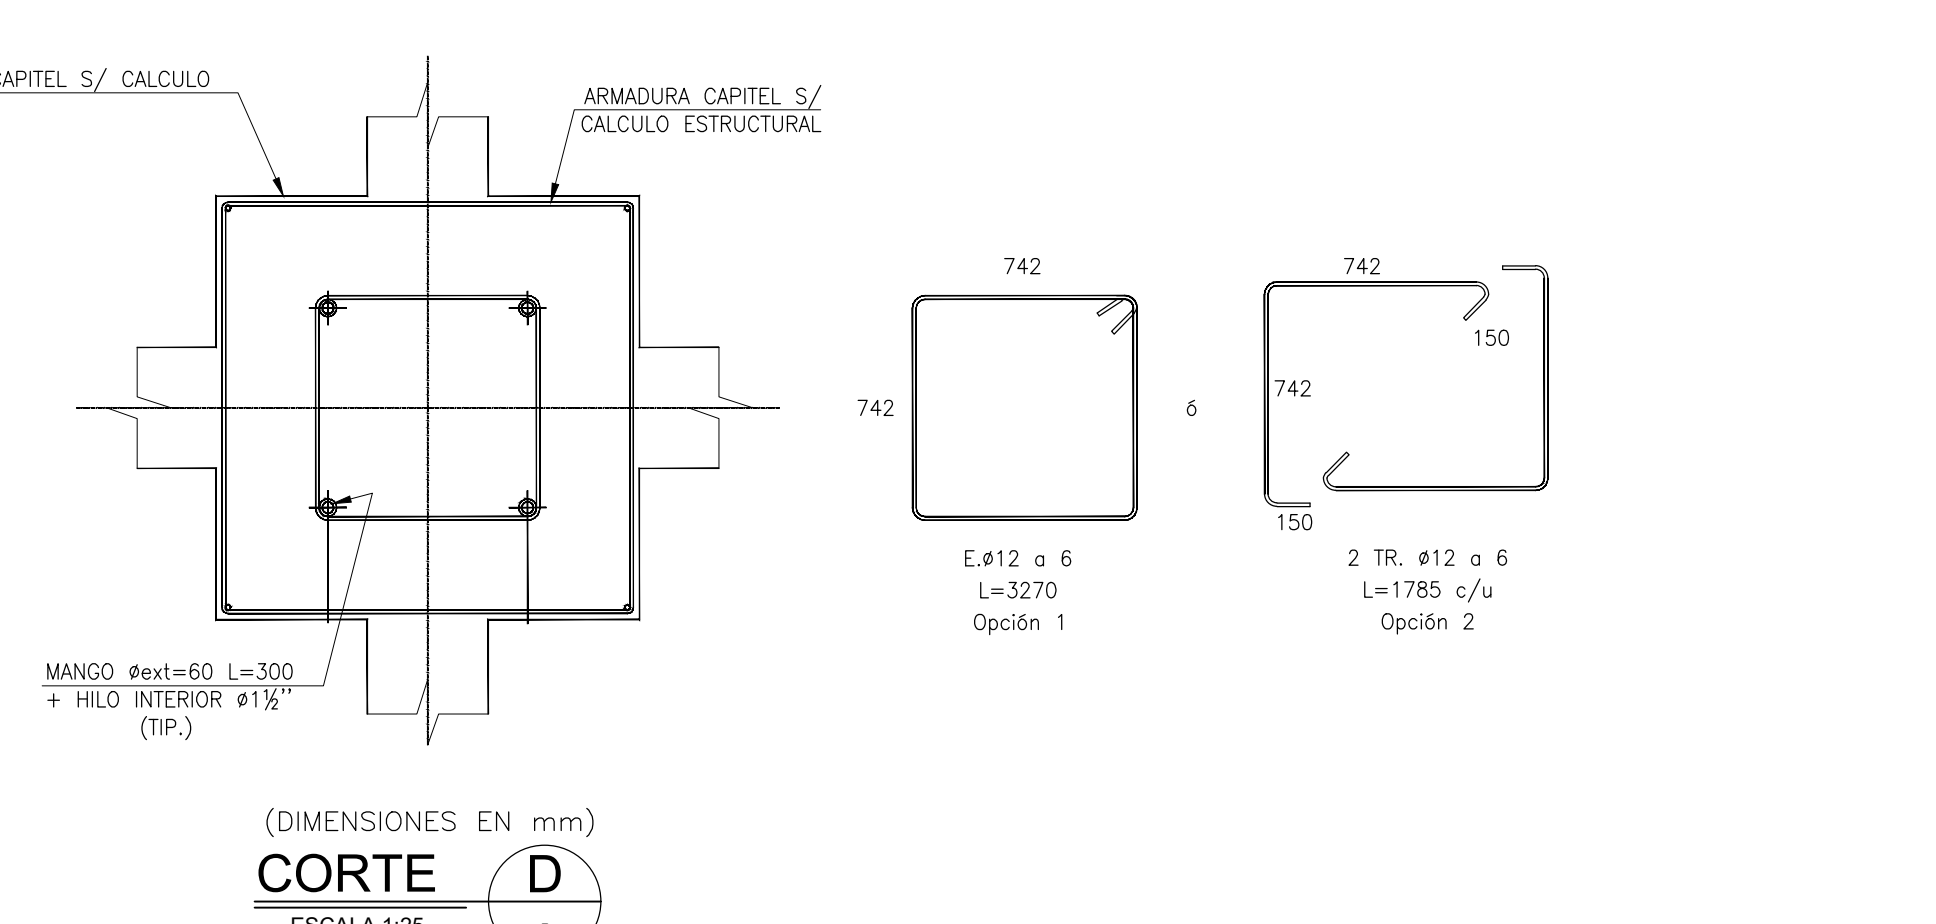

TIPO	CANTIDAD		D. ext. (cm)	REC. (cm)	D. int. (cm)	ts (cm)	re	tr (cm)	Bf (cm)	tf (cm)	Hr (cm)	Ht (cm)	NUCLEO PLOMO
	OBRA	PROTOTIPOS											
AS2	29	2	76	0.5	10	0.3	35	0.7	81	2.0	24.5	38.7	SI

** DIMENSIONES PUEDEN VARIAR DE ACUERDO AL PROVEEDOR DE DISPOSITIVOS.

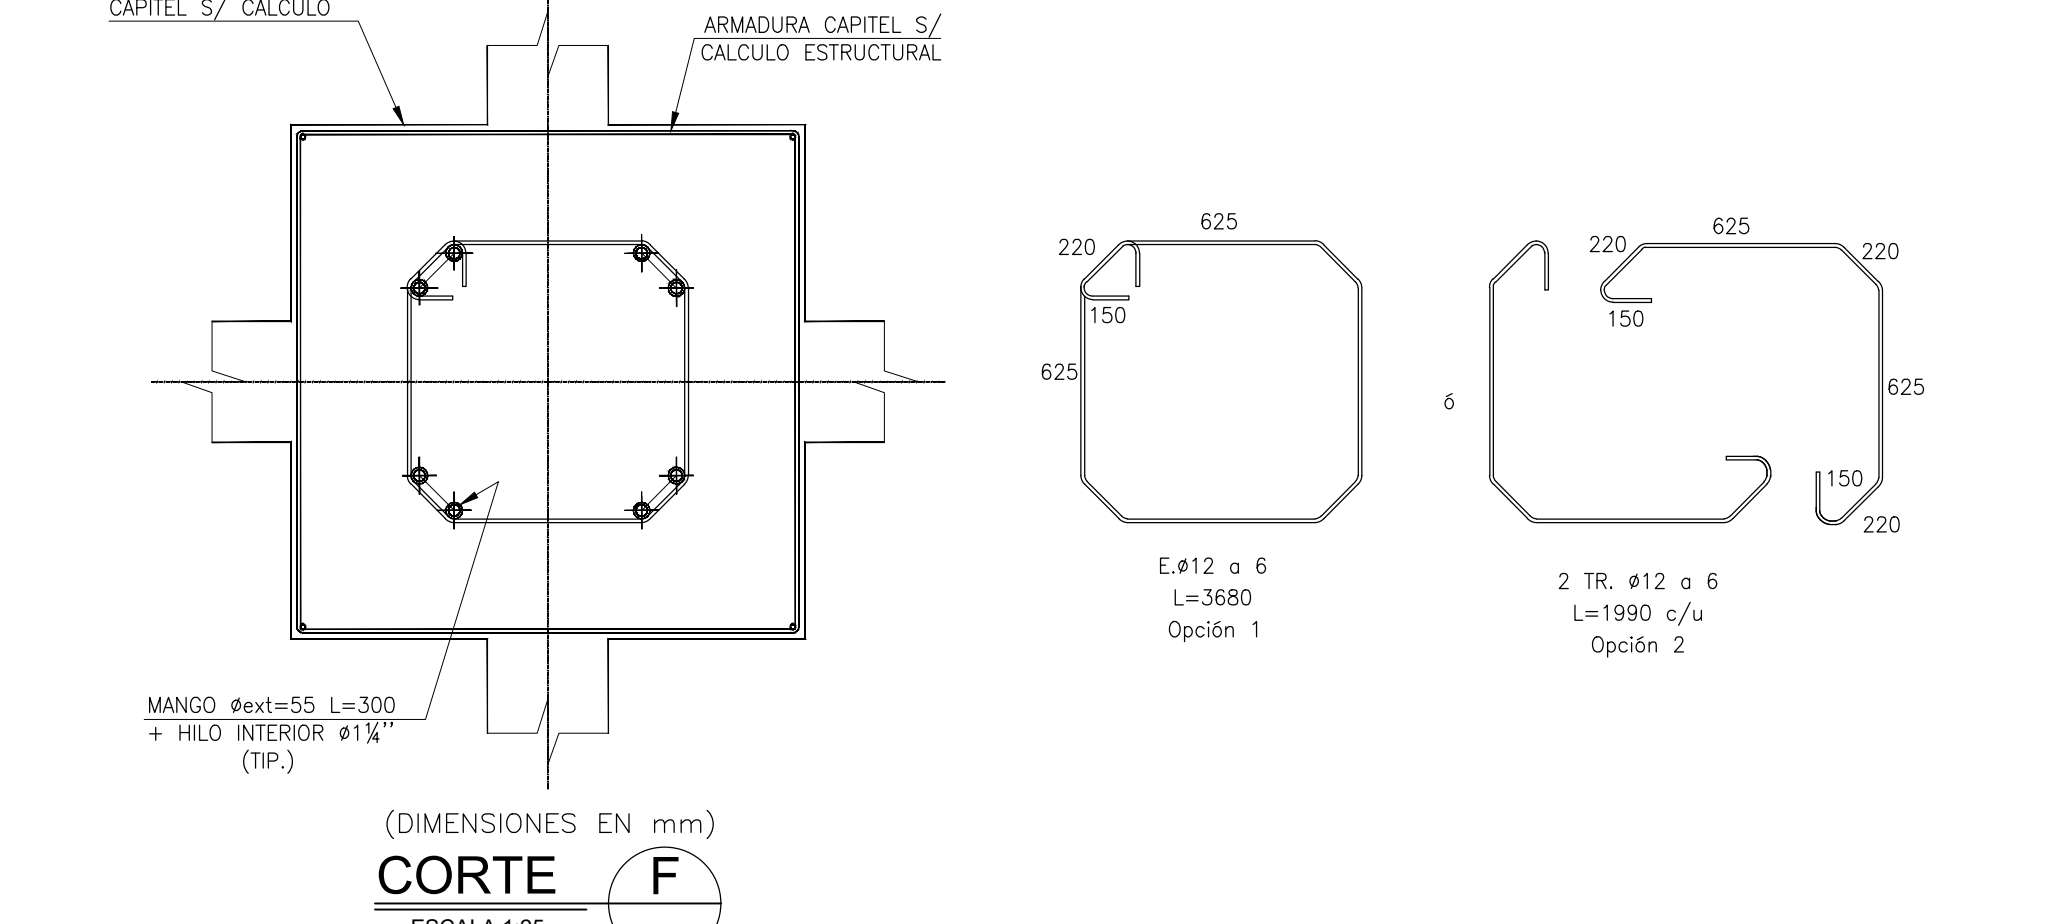

TIPO	CANTIDAD		D. ext. (cm)	REC. (cm)	D. int. (cm)	ts (cm)	nr	tr (cm)	Bf (cm)	tf (cm)	Hr (cm)	Hl (cm)	NUCLEO PLOMO
	OBRA	PROTOTIPOS											
AS3	10	2	93	0.5	15	0.3	35	0.7	98	2.5	24.5	39.7	SI

** DIMENSIONES PUEDEN VARIAR DE ACUERDO AL PROVEEDOR DE DISPOSITIVOS.

NOTAS:


1. ACERO PLACAS A36
2. ACERO PERFILES ASTM A325, ZINCADO
3. ACERO MANTENIDO A500 SAE 1020 CON CERTIFICADO $F_y \geq 250$ MPa
4. HORMIGÓN COMPACTO S/C CALCULO ESTRUCTURAL
5. SE DEBE CONSIDERAR MACHINA DE MONTE PARA PANGOS
6. EN CASO DE QUE EL PROYECTO REQUIERA UTILIZAR UN SISTEMA DE AISLAMIENTO QUE DIFERA AL ESPECIFICADO EN ESTOS PLANOS, DEBERA CONSULTAR CON EL INGENIERO EN LAS ESPECIFICACIONES TÉCNICAS DE LAS ABRIGOS
7. EN CASO DE QUE EL PROYECTO REQUIERA UTILIZAR EL PUNTO 6.1.3. ESTO DEBERA SER APROBADO POR SU SESA SEBA AL INICIO DE LA ABRIGACION
8. SE DEBE CONSIDERAR EL CULO DE AGUA POR CADA UNO DE LOS EQUIVALENTES
9. TORQUE PERFILES 700 lb-pie
10. LOS AISLADORES LLADEBOS DEBEN CONFORMAR CON LO REQUERIDO
11. LOS AISLADORES LLADEBOS DEBEN CONFORMAR CON EL SISTEMA DE AISLAMIENTO SISMO" QUE FORMA PARTE DEL PROYECTO DE ESTRUCTURAS
12. EL PROYECTO DEBERA DEBE CONFORMAR CON EL PROYECTO DE ESTRUCTURAS "PROCEDIMIENTO DE MONITOR DE AISLADORES SISMICOS" DEL PROYECTO DE CALCULO

E	23.02.2021	L. SIQUEIRA M. RENDEL	CARL LUDERS	ENTREGA ETAPA DE DISEÑO
D	18.12.2020	L. SIQUEIRA M. RENDEL	CARL LUDERS	SE MODIFICA LO INDICADO
C	12.06.2020	S. SAEZ M. RENDEL	CARL LUDERS	EMITIDO PARA REVISION DEL CUENTE
B	19.12.2019	S. SAEZ M. RENDEL	CARL LUDERS	EMITIDO PARA REVISION DEL CUENTE
A	30.07.2019	S. SAEZ M. RENDEL	CARL LUDERS	EMITIDO PARA PRESUPUESTO

ESPECIALIDAD	PROYECTO DE CÁLCULO ESTRUCTURAL
--------------	---------------------------------

 **sirve**
SEISMIC PROTECTION TECHNOLOGIES

Estado de Oaxaca, Las Condes, Santiago - Chile
TELÉFONO : (+52) 28257100
CONTACTO: info@sirve.cl

 
CARL LUDERS SCHWARZEN
Ingeniero Civil LC
Dipl. Ing. Technische Hochschule

PROYECTO	RECUPERACION BASILICA DEL SALVADOR FUNDACIONES, LOSA BASE y SISTEMA AISLAMIENTO S
----------	--

CALLE HUERFANOS 1796 - SANTIAGO

FUNDACION BASILICA DEL SALVADOR
RUT: 65.148.980-6

DETALLE DE AISLADORES SISMICOS

CÓDIGO DEL DOCUMENTO	FORMATO	ETIQUETA
----------------------	---------	----------

18088-01-PL-EST-0802	AD	INDICAD
----------------------	----	---------