




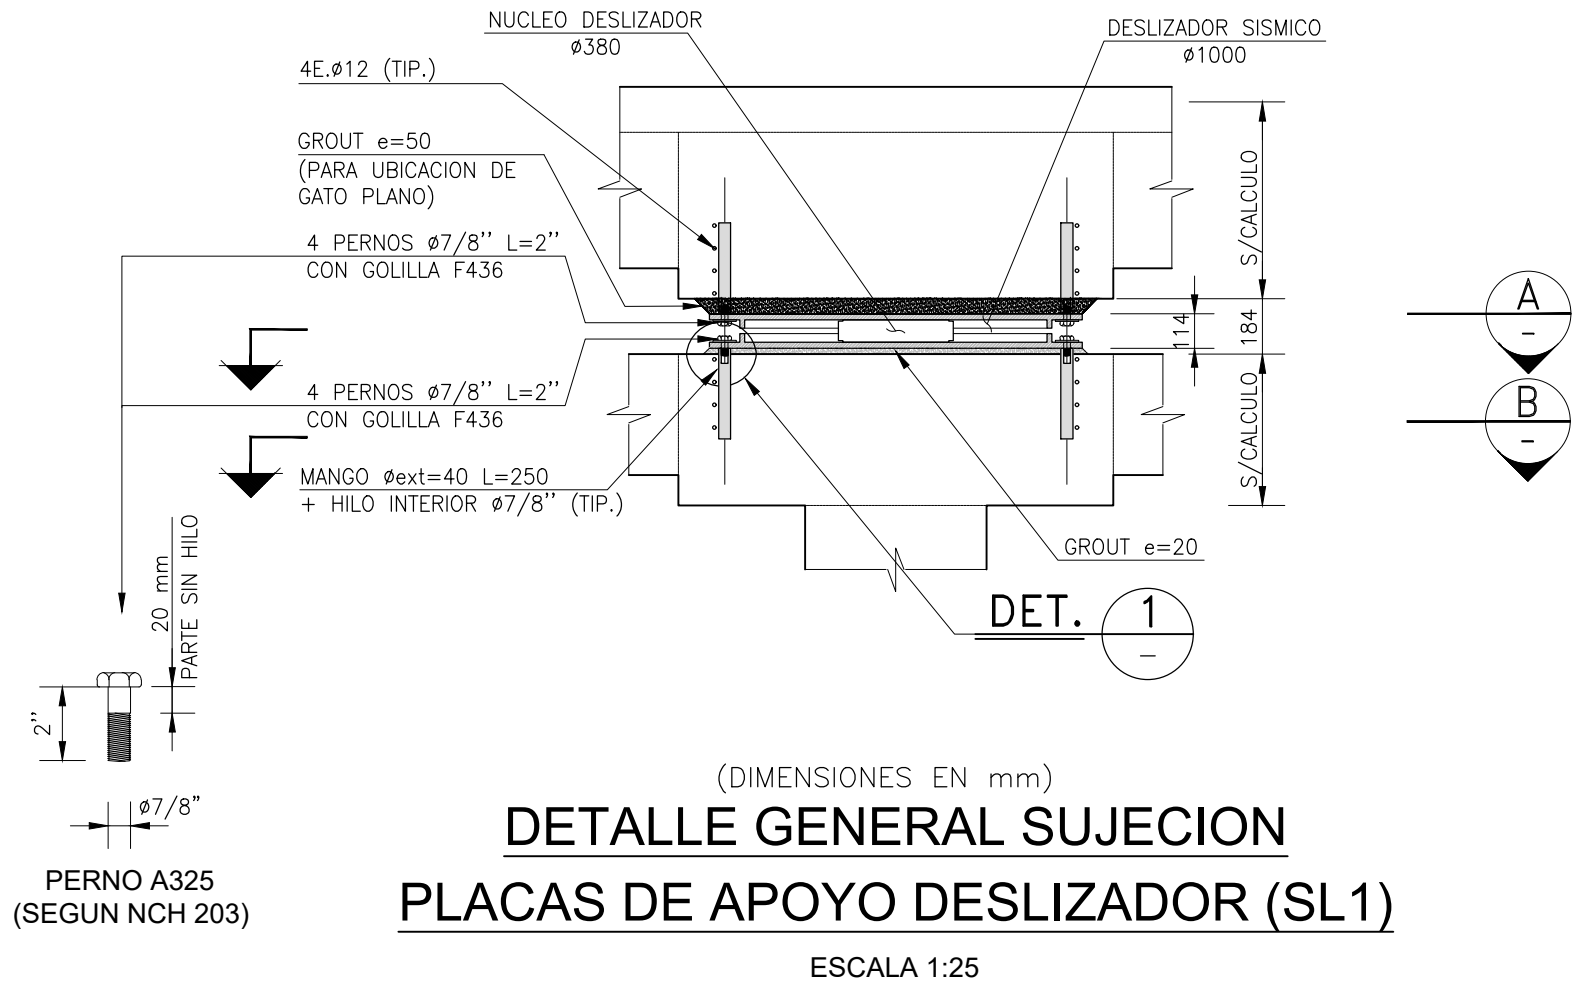


(DIMENSIONES EN mm.)
DETALLE GENERAL SUJECION
PLACAS DE APOYO DESLIZADOR (SL1)
ESCALA 1:25

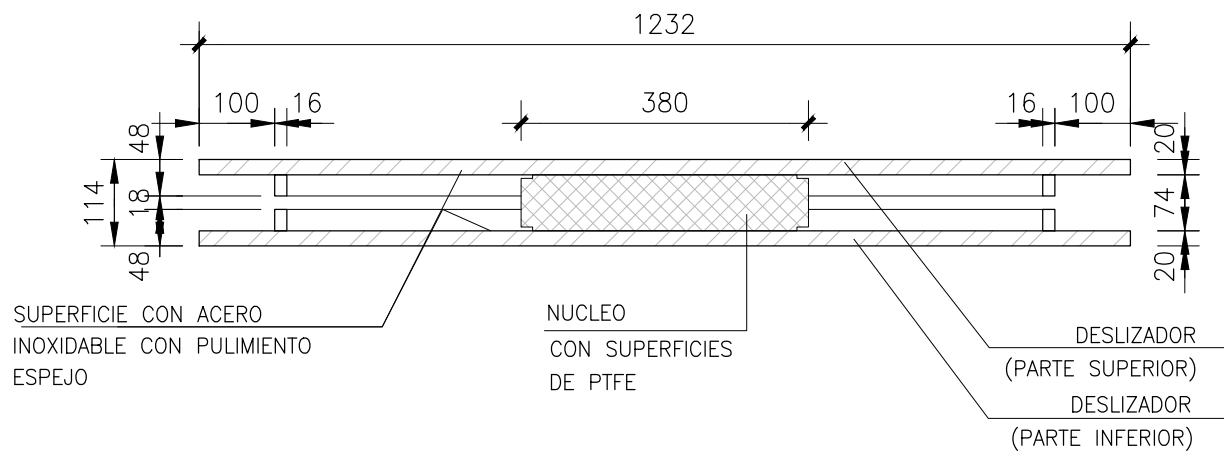


(DIMENSIONES EN mm.)
SECCION DESLIZADOR (SL1)
CORTE 1
ESCALA 1:10

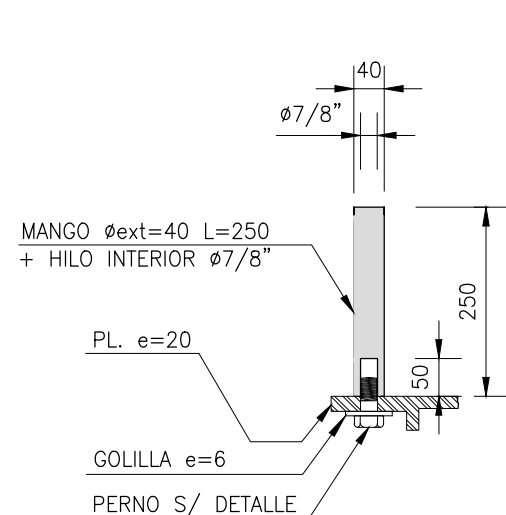


(DIMENSIONES EN mm.)
DETALLE EMPALME
PERNO Ø7/8" EN MANGO
ESCALA 1:10

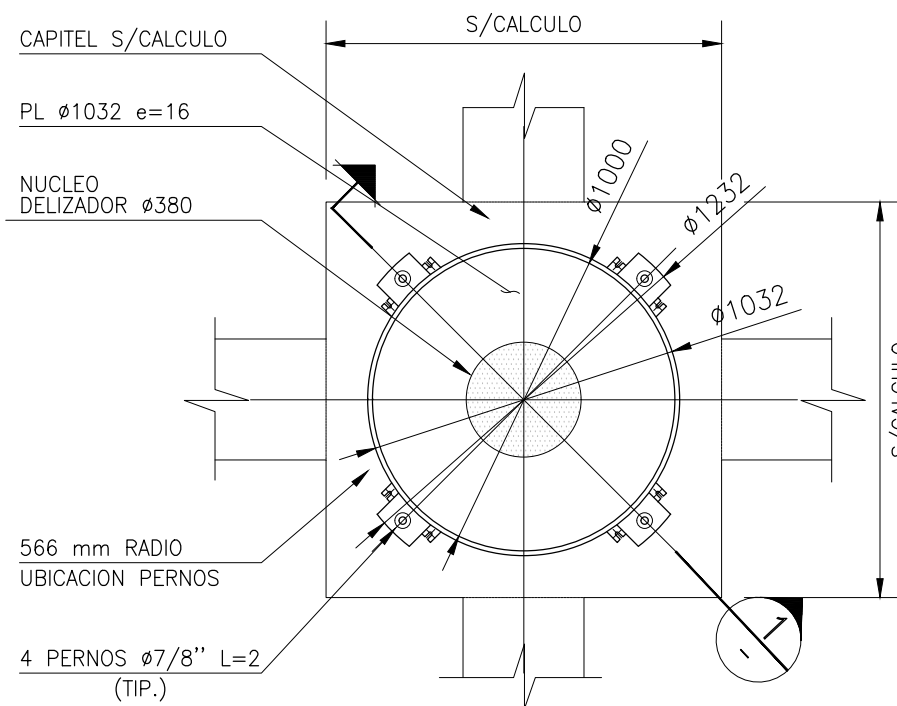


(DIMENSIONES EN mm.)
CORTE A
ESCALA 1:25

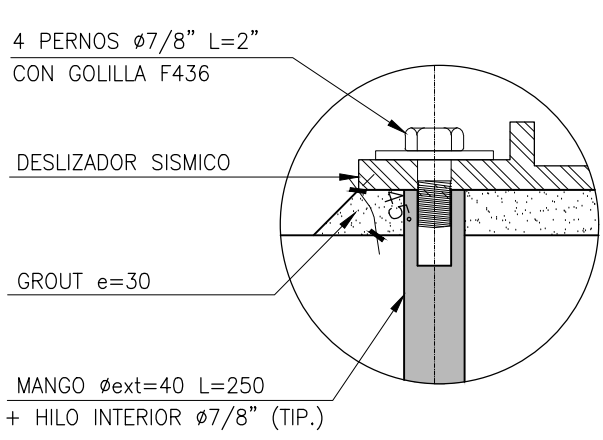

DETALLE 1
ESCALA 1:5

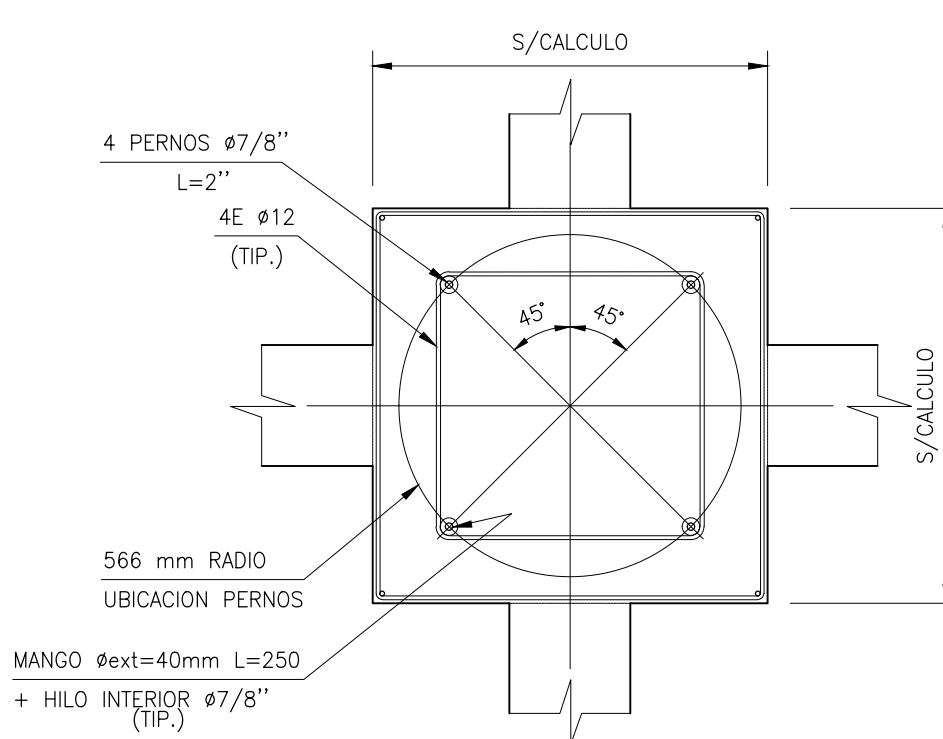

(DIMENSIONES EN mm.)
CORTE B
ESCALA 1:25

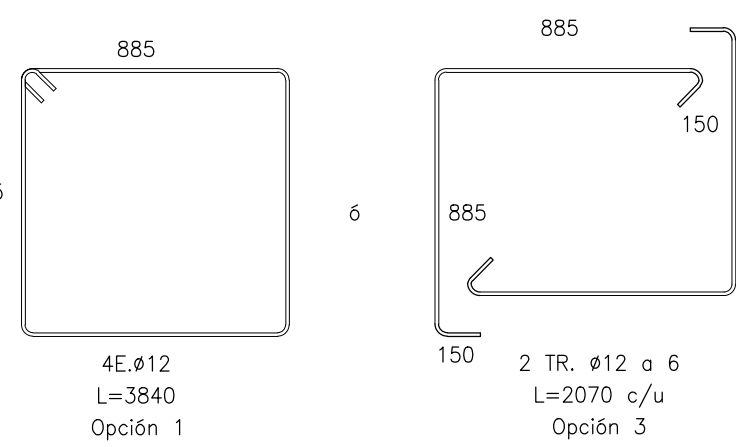

CANTIDAD DE DESLIZADORES

TIPO	CANT.
SL1	8

- TOLERANCIAS:**
- PLANITUD DE LA SUPERFICIE DE HORMIGÓN QUE RECIBE AL AISLADOR: NO DEBEN EXISTIR DESVIACIONES FUERA DEL PLANO DE LA SUPERFICIE DE HORMIGÓN QUE RECIBE AL AISLADOR, MAYORES A 1,5 mm.
 - HORIZONTALIDAD DEL AISLADOR UNA VEZ CONECTADO AL ANCLAJE EN EL HORMIGÓN: LAS PLACAS EXTERNAS AL AISLADOR NO DEBEN PRESENTAR UN CERO CON RESPECTO A LA HORIZONTAL MAYOR A 0,0000 mm.
 - DEBEN EXISTIR UNA DIFERENCIA EN LA POSICION VERTICAL MAYOR A 0,96mm ENTRE SUS EXTREMOS.
 - SE DEBERÁN TOMAR TODAS LAS PRECAUCIONES NECESARIAS TANTO PARA LA POSICION VERTICAL DE LOS MANGOS COMO EN EL ACABADO SUPERFICIAL DEL HORMIGÓN PARA QUE SE CUMPLA CON ESTA RESTRICCIÓN.

- NOTAS:**
- ACERO PLACAS A36
 - ACERO PERNOS ASTM A325 ZINCADO
 - ACERO MANGO RECTO A36 O SAE 1020 CON CERTIFICADO $F_y \geq 250$ MPa.
 - HORMIGÓN CAPITELES S/C CALCULO ESTRUCTURAL
 - SE DEBE CONSIDERAR MÁQUINA DE MONTAJE PARA MANGO
 - EN CASO QUE EL FABRICANTE DE AISLADORES PROPONGA UTILIZAR UN SISTEMA DE AISLAMIENTO QUE DIFERA AL ESPECIFICADO EN ESTOS PLANOS, DEBERÁ CUMPLIR CON LO INDICADO EN LAS ESPECIFICACIONES TÉCNICAS DE AISLADORES EN SISTEMA DE AISLAMIENTO* EN PARTICULAR CON EL PUNTO 6.1.3. ESTO DEBERÁ SER APROBADO POR SIRVE LA PREVIAMENTE AL INICIO DE LA FABRICACIÓN.
 - GROUT: Sika 328 CL (5,5 LITROS DE AGUA POR CADA 30kg) O EQUIVALENTE.
 - TORQUE PERNOS 700 Nm-pie
 - LOS AISLADORES ELASTOMÉRICOS DEBEN CUMPLIR CON LO REQUERIDO EN EL DOCUMENTO "ESPECIFICACIONES TÉCNICAS DE AISLADORES EN SISTEMA DE AISLAMIENTO SÍSMICO" QUE FORMA PARTE DEL PROYECTO DE ESTRUCTURAS.
 - LOS AISLADORES DEBEN SER INSTALADOS EN OBRA DE ACUERDO CON EL DOCUMENTO "PROCEDIMIENTO DE MONTAJE DE AISLADORES SÍSMICOS" DEL PROYECTO DE CÁLCULO.

FECHA	REVISIÓN	APROBADO	DETALLE
23.02.2021	L. SIQUIRA M. RENDEL	CAR. LUJERS	ENTREGA ETAPA DE DISEÑO
18.12.2020	L. SIQUIRA M. RENDEL	CAR. LUJERS	SE MODIFICA LO INDICADO
12.06.2020	S. SAEZ M. RENDEL	CAR. LUJERS	EMITEO PARA REVISIÓN DEL CLIENTE
Nº	FECHA	DIAGRAMA/REVISIÓN	APROBADO

PROYECTO DE CÁLCULO ESTRUCTURAL			
PROYECTO: RECUPERACION BASILICA DEL SALVADOR			
UBICACION: FUNDACIONES, LOSA BASE y SISTEMA AISLAMIENTO SISMICO			
CLIENTE: CALLE HUERFANOS 1796 - SANTIAGO			
CONTENIDO: FUNDACION BASILICA DEL SALVADOR			
DETALLE DE DESLIZADORES SISMICOS			
FECHA: 23.02.2021			
REVISIÓN: C			
CODIGO DEL DOCUMENTO: 18088-01-PL-EST-0803			
FORMATO: A4			
ESCALA: INDICADAS			