


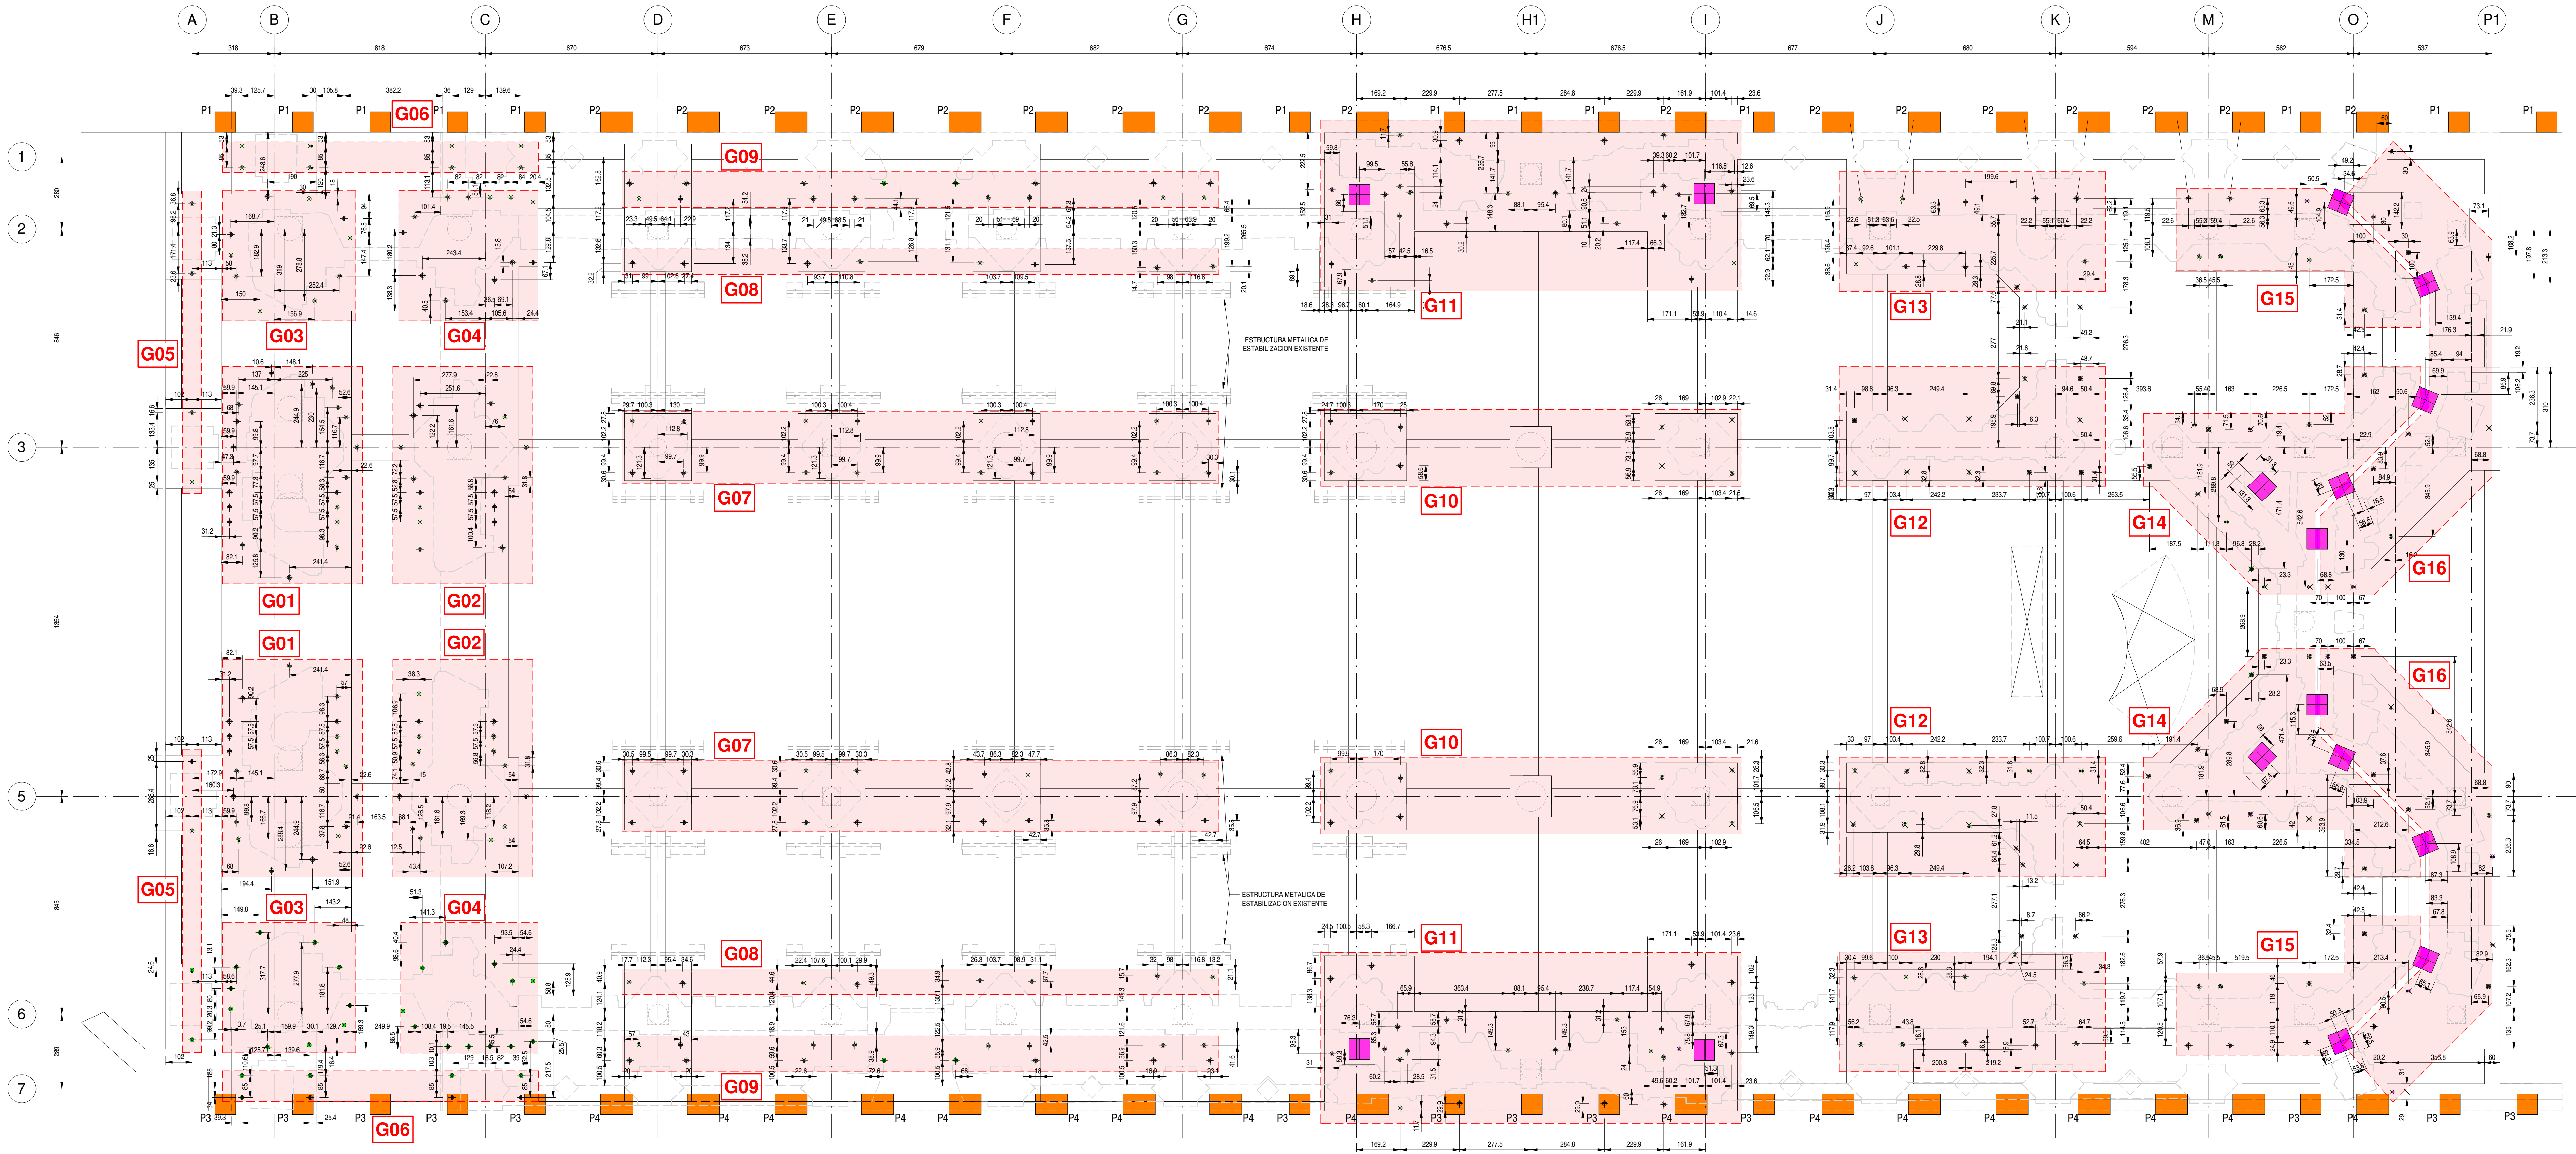

PLANTA DE DISPOSICION DE MICROPILOTES Y GRUPOS DE MICROPILOTES

ESCALA 1 : 100

TABLA DE CARGAS MÁXIMAS Y PROMEDIO POR GRUPOS DE MICROPILOTES (Tonf)

GRUPO	CANTIDAD ELEMENTOS	ETAPA A DE EXCAVACION				ETAPA B DE EXCAVACION			
		Q	Q	Q	Q	Q	Q	Q	Q
GRUPO 1	19	47.98	43.11	47.46	55.73	63.19	19	58.11	5.84
GRUPO 2	15	44.09	37.68	44.04	12.27	63.31	15	55.46	5.82
GRUPO 3	10	49.72	43.25	49.72	13.54	63.26	10	53.90	5.89
GRUPO 4	12	49.77	42.95	49.70	10.89	59.89	12	50.77	5.82
GRUPO 5	4	47.53	44.40	46.03	16.81	62.83	4	56.58	5.90
GRUPO 6	8	41.83	39.83	39.84	19.89	59.14	8	46.51	5.89
GRUPO 7	16	37.48	29.64	37.48	3.48	40.36	16	55.19	5.84
GRUPO 8	6	50.93	46.63	46.63	3.75	53.13	6	51.31	5.84
GRUPO 9	16	47.59	42.54	46.68	8.03	54.92	16	44.79	5.82
GRUPO 10	8	36.49	27.33	36.49	5.06	41.54	8	42.36	5.89
GRUPO 11	18	42.03	38.98	34.90	22.57	57.16	22	50.17	5.84
GRUPO 12	12	36.18	35.19	34.28	14.44	44.52	12	55.17	5.75
GRUPO 13	12	51.87	43.94	51.52	12.91	64.44	12	50.08	5.89
GRUPO 14	10	36.36	44.52	36.36	5.37	65.73	11	58.59	5.89
GRUPO 15	8	47.00	43.12	47.00	7.01	54.01	7	53.88	5.81
GRUPO 16	3	48.90	48.37	48.28	5.27	51.55	12	61.01	5.82
GRUPO 17	8	55.14	42.31	48.82	5.56	54.42	8	57.97	5.82
GRUPO 18	17	49.26	28.78	49.26	11.05	60.31	17	64.02	5.82
TOTAL PILAS	25						17		

NOTA: LAS CANTIDADES INDICADAS CORRESPONDEN A 1 GRUPO DE CADA NUMERACION, COMO CADA GRUPO ESTA PRESENTE 2 VECES EN LA PLANTA DEL EDIFICIO, LAS CANTIDADES TOTALES DE ELEMENTOS CORRESPONDEN AL DOBLE DE LAS INDICADAS.


SIMBOLOGIA

- PILA TEMPORAL DE HA - FUNCIONAL SOLO EN ETAPA A
- PILA DE CONTENCIÓN DE HA - FUNCIONAL EN ETAPAS A, B Y EN LA CONDICIÓN DEFINITIVA DEL EDIFICIO
- MICROPILETO 078MM L=10M - FUNCIONAL EN ETAPAS A Y B
- MICROPILETO 078MM L=11M - FUNCIONAL EN ETAPAS A Y B
- MICROPILETO 078MM L=10M - FUNCIONAL SOLO EN ETAPA B
- MICROPILETO 078MM L=11M - FUNCIONAL SOLO EN ETAPA B


DESCRIPCION GENERAL DE ETAPAS DE FUNCIONAMIENTO DE MICROPILOTES Y PILAS

ETAPA A: LOS ELEMENTOS EXISTENTES DE ALBAÑILERIA SON SOSTENIDOS POR MICROPILOTES Y PILAS DE HORMIGÓN, VINCULADOS POR MEDIO DE PIEZAS ESPECIALES DE ESTRUCTURA METALICA. SE DESMARRILLA LA PRIMERA FASE DE EXCAVACION A LA PROFUNDIDAD REQUERIDA PARA LA CONSTRUCCION DE LAS VIGAS Y CAPITELES DEL NIVEL SOBRE AISLADORES SISMICOS.

ETAPA B: LOS ELEMENTOS EXISTENTES DE ALBAÑILERIA SON SOSTENIDOS POR MICROPILOTES Y PILAS DE HORMIGÓN, VINCULADOS POR MEDIO DE LOS CAPITELES DE HORMIGON ARMADO CONSTRUIDOS AL FINAL DE LA ETAPA A. SE DESMARRILLA LA SEGUNDA FASE DE EXCAVACION A LA PROFUNDIDAD REQUERIDA PARA LA CONSTRUCCION DE LAS FUNDACIONES, COLUMNAS Y VIGAS BAJO AISLADORES SISMICOS. FINALIZADO CON LA INSTALACION DE LOS AISLADORES SISMICOS Y LA ELIMINACION DE LOS MICROPILOTES Y ELEMENTOS TEMPORALES DE SOPORTE.

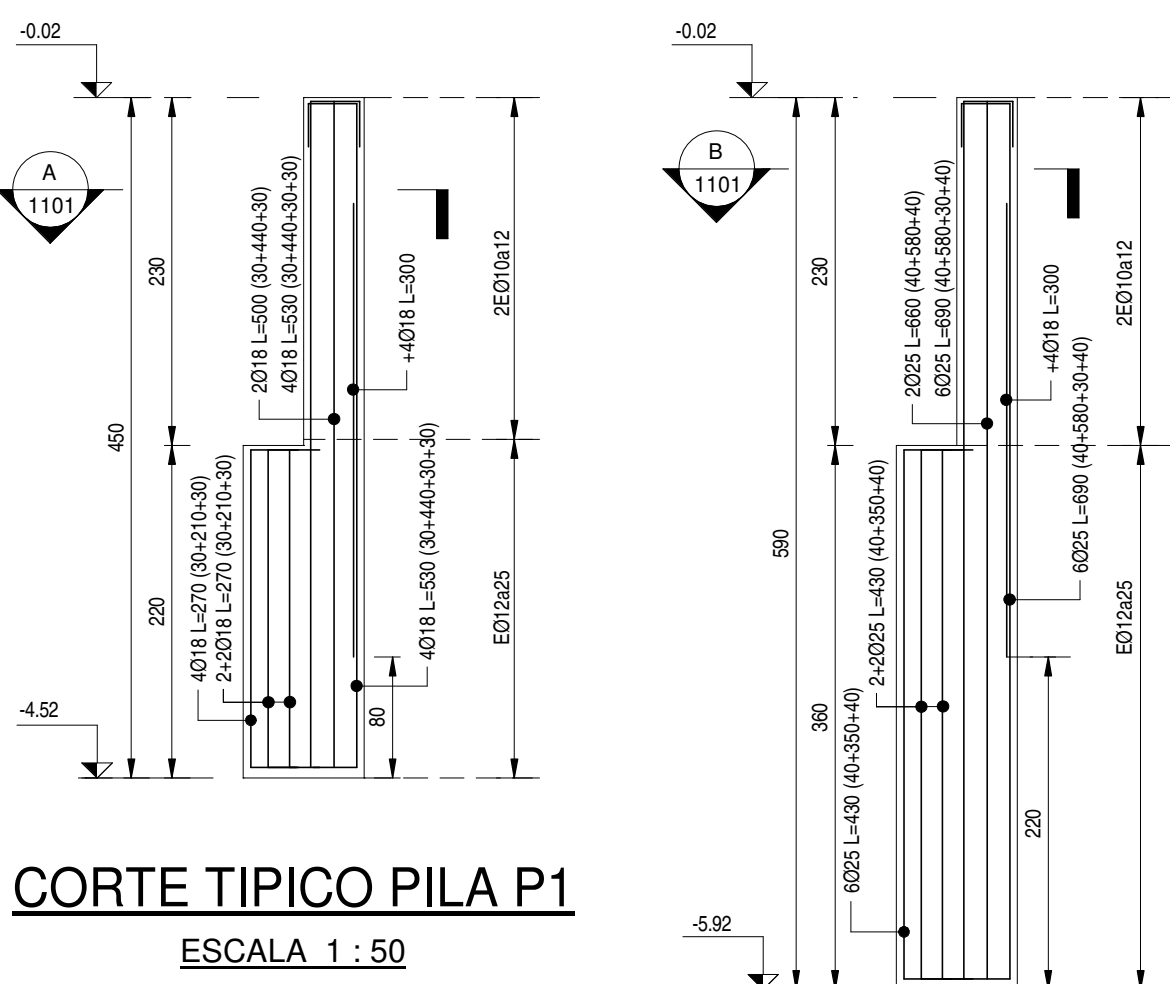


CORTE TIPOICO PILA P1

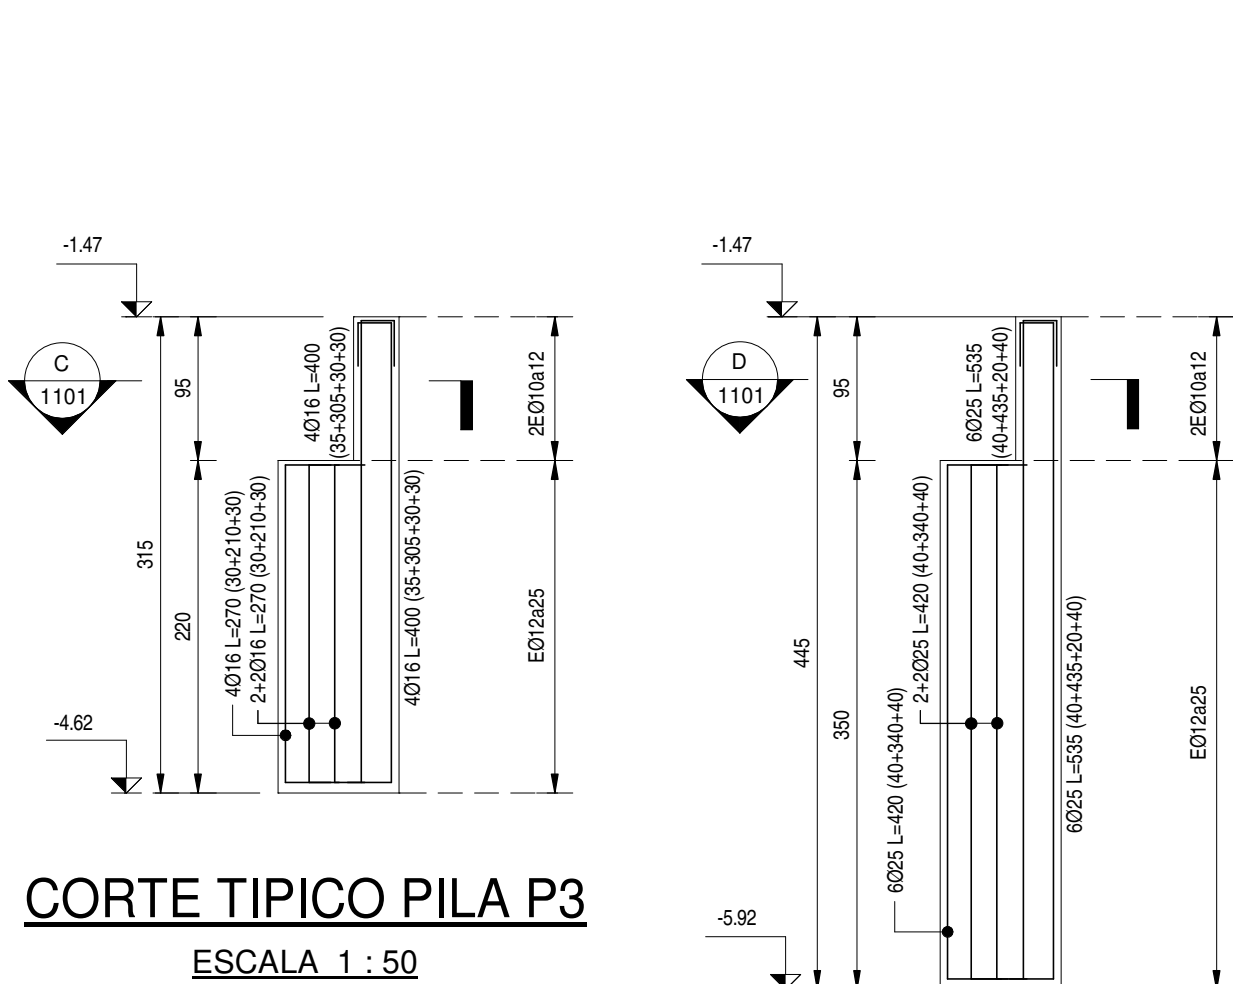

CORTE TIPOICO PILA P3





CORTE TIPOICO PILA P2

CORTE TIPOICO PILA P4

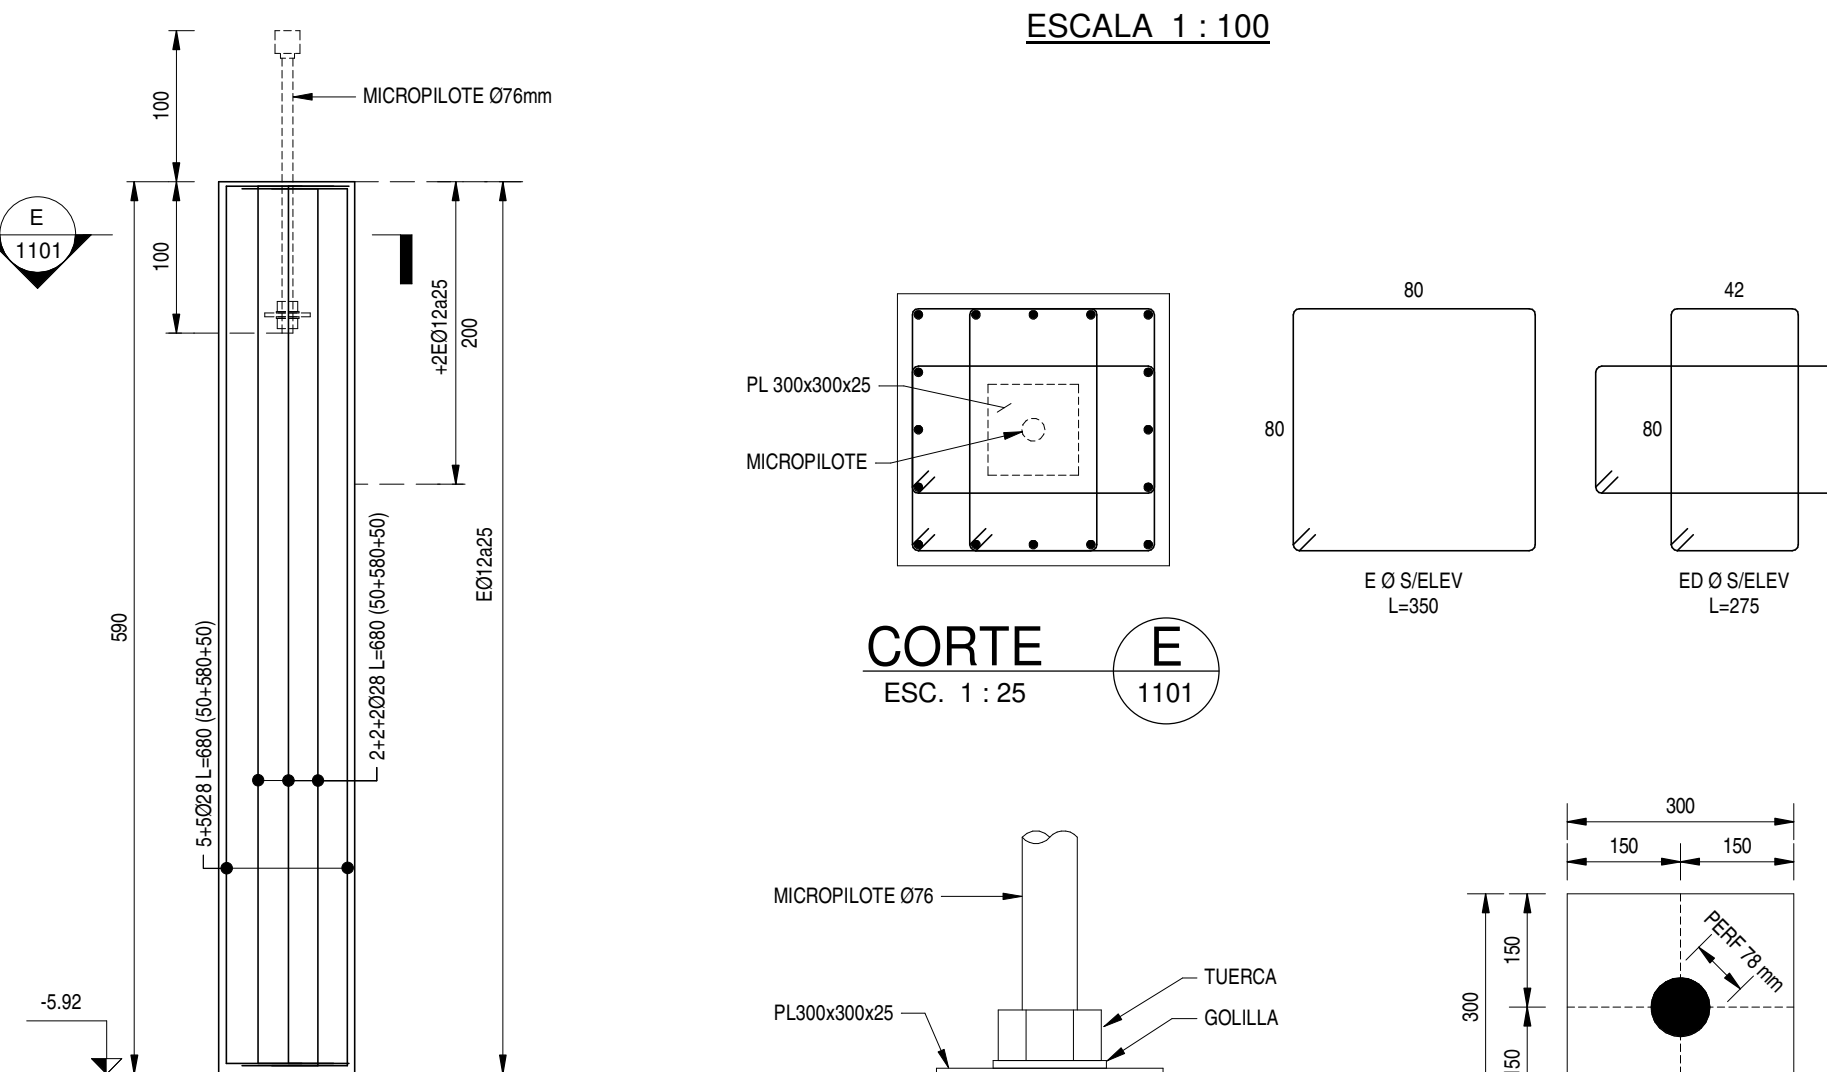

DETALLE TIPO DE PILA TEMPORAL DE HA

DETALLE ANCLAJE MICROPILETO

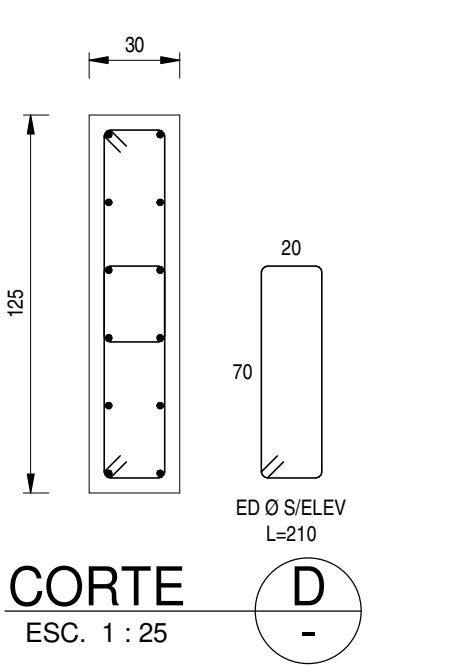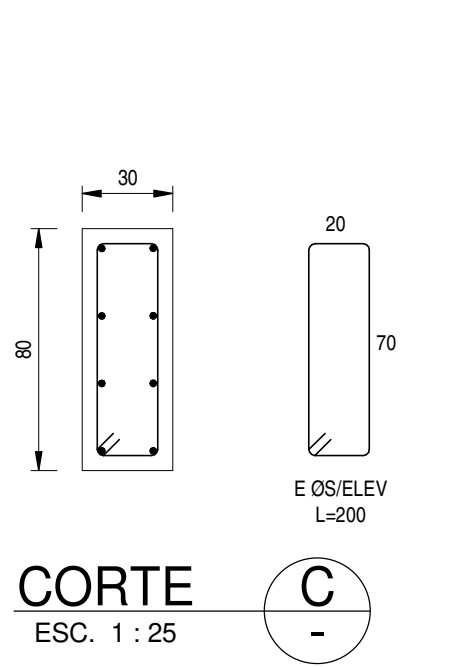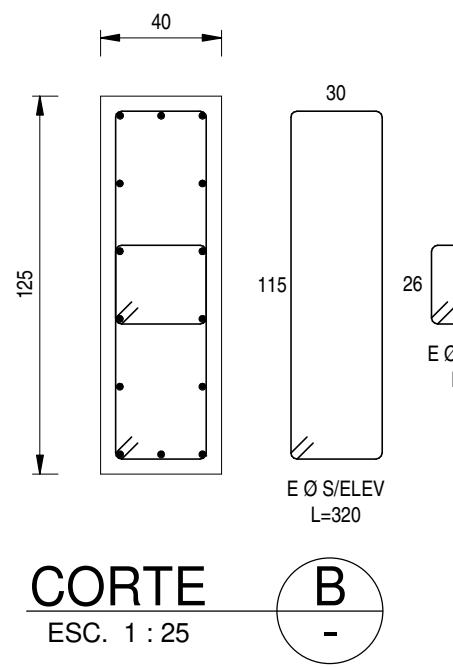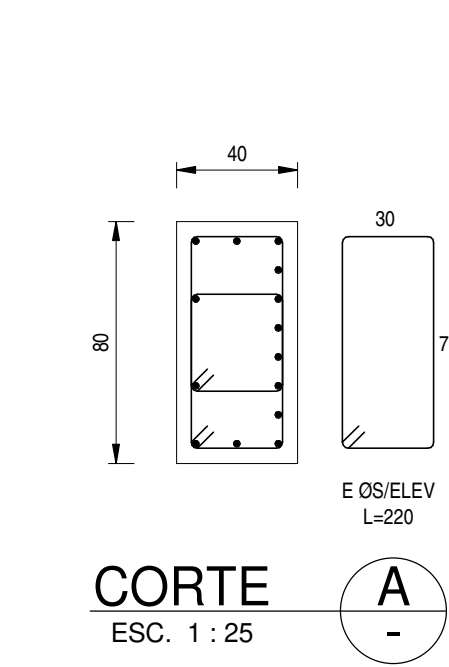

NOTAS:

- LOS MICROPILOTES QUE POR ACCESIBILIDAD NO PUEDAN SER EJECUTADOS EN EL DIAMETRO ESPECIFICADO, PODRAN SUSTITUIRSE POR 2 O MAS MICROPILOTES DE MENOR TAMAÑO.
- EL DISEÑO DEFINITIVO DE LOS MICROPILOTES DEBERÁ SER REALIZADO POR LA EMPRESA SELECCIONADA PARA SU EJECUCIÓN Y DEPENDERÁ DEL TIPO DE MICROPILETO ESPECÍFICO A CONSIDERAR. ESTE DISEÑO DEBERÁ SER VALIDADO POR EL INGENIERO CALCULISTA Y EL REVISOR INDEPENDIENTE DEL PROYECTO.
- EL DISEÑO DE CADA TIPO DE MICROPILETO DEBERÁ CONSIDERAR LAS CARGAS INDICADAS EN LA TABLA CONTENIDA EN ESTE PLANO, Y UN SISTEMA DE ARRIOSTRAMIENTO ENTRE ELLOS QUE GARANTICE SU ESTABILIDAD PERMITIENDO ALCANZAR LA PROFUNDIDAD DE EXCAVACION REQUERIDA POR EL PROYECTO DURANTE AMBAS ETAPAS DE EXCAVACION A Y B (VER PASOS 5 Y 7 EN PLANO 1201).

G	23.02.2020	L. SQUIRRA M. RENDIL	CARL LUDERS	ENTREGA ETAPA DE DISEÑO
F	12.02.2020	L. SQUIRRA M. RENDIL	CARL LUDERS	SE MODIFICA LO INDICADO
E	18.12.2020	L. SQUIRRA M. RENDIL	CARL LUDERS	SE MODIFICA LO INDICADO
D	13.08.2020	L. SQUIRRA M. RENDIL	CARL LUDERS	SE MODIFICA LO INDICADO
C	19.12.2019	M. SAIZ M. RENDIL	CARL LUDERS	EMPEZO PARA REVISION DEL CLIENTE
Nº	FECHA	DIBUJO/REVISO	APROBÓ	DETALLE
PROYECTADO				
PROYECTO DE CÁLCULO ESTRUCTURAL				
PROYECTO: RECUPERACION BASILICA DEL SALVADOR				
UBICACION: FUNDACIONES, LOSA BASE Y SISTEMA AISLAMIENTO SISMICO				
CALLE HUERFANOS 1796 - SANTIAGO				
FUNDACION BASILICA DEL SALVADOR				
RUT: 65.145.980-6				
CONTENIDO: PLANTA DE MICROPILOTES Y DETALLES DE PILAS				
REVISION: G				
CODIGO DEL DOCUMENTO: 18088-01-PL-EST-1101				
FORMATO: A4				
ESCALA: 1:100				
FECHA: 23.02.2020				