



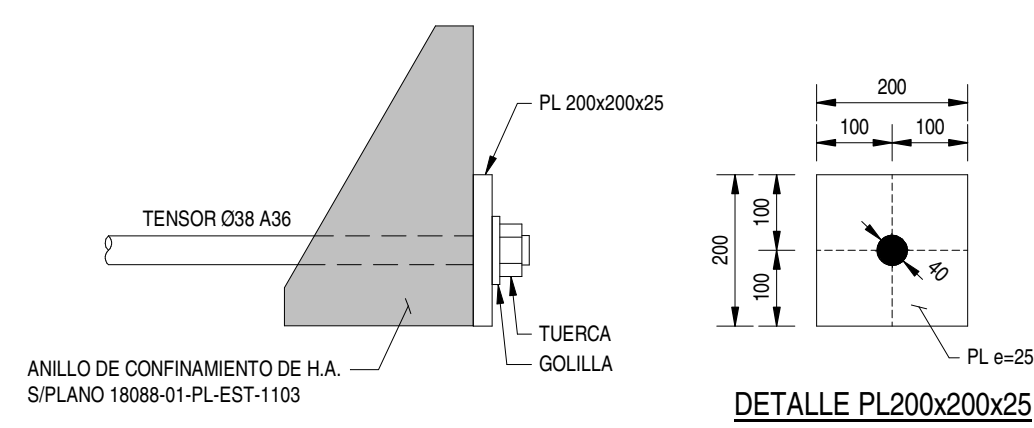

DETALLE TIPO DE TENSORES
TERMINADOS EN PLACA
ESCALA 1 : 10

F	23.02.2020	L.SIQUEIRA M. RENDEL	CARL LUDERS	ENTREGA ETAPA DE DISEÑO
E	12.02.2020	L.SIQUEIRA M. RENDEL	CARL LUDERS	SE MODIFICA LO INDICADO
D	18.12.2020	L.SIQUEIRA M. RENDEL	CARL LUDERS	SE MODIFICA LO INDICADO
C	13.08.2020	L.SIQUEIRA M. RENDEL	CARL LUDERS	SE MODIFICA LO INDICADO
B	19.07.2019	S. SAEZ M. RENDEL	CARL LUDERS	EMITIDO PARA REVISION DEL CLIENTE
Nº	FECHA	DIBUJO/REVISO	APROBO	DETALLE

PROYECTO DE CÁLCULO ESTRUCTURAL

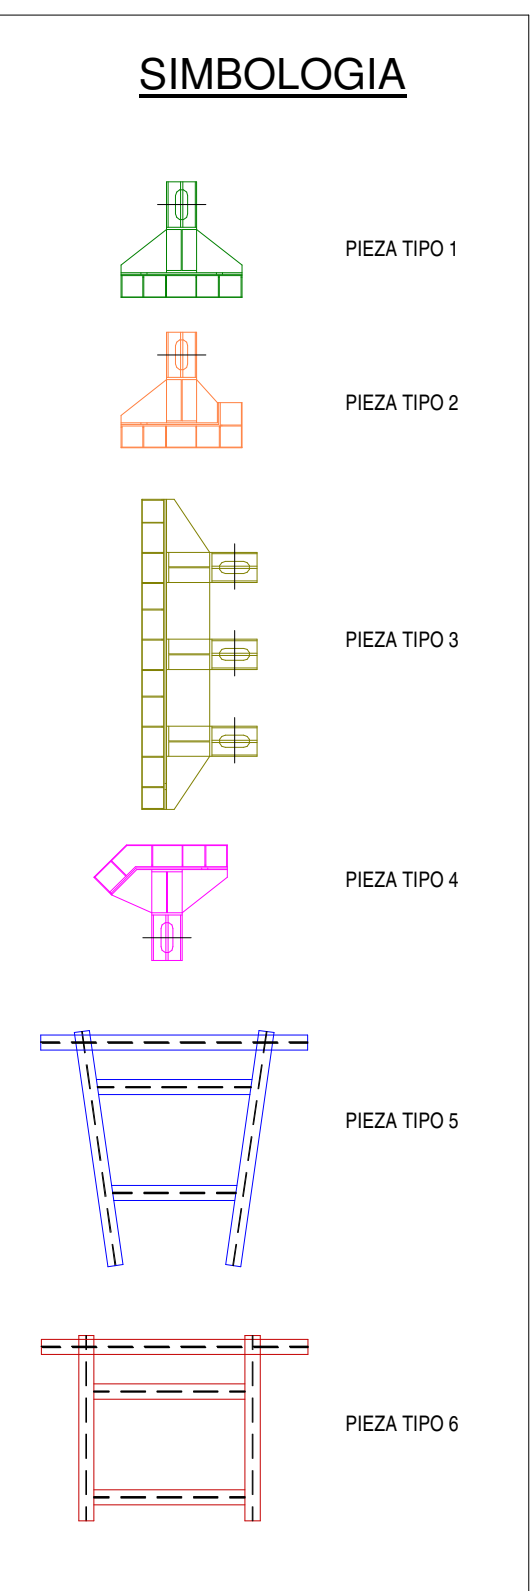

TELÉFONO: (+56-2) 24337100

CARL LÜDERS SCHWARZENBERG
Ingenieur Civil LLC
Hochschule Darmstadt
3.639.172-3

PROYECTO	RECUPERACION BASILICA DEL SALVADOR FUNDACIONES, LOSA BASE y SISTEMA AISLAMIENTO SISMICO
----------	--

UBICACIÓN	CALLE HUERFANOS 1796 - SANTIAGO
CLIENTE	FUNDACION BASILICA DEL SALVADOR

RUT: 65.148.980-6		REVISIÓN
CONTENIDO	PLANTA DE DISTRIBUCION DE PIEZAS DE SOPORTE	E

CÓDIGO DEL DOCUMENTO	FORMATO	ESCALA	FECHA
18088-01-PL-EST-1102	A0	1:100	23.02.2020