



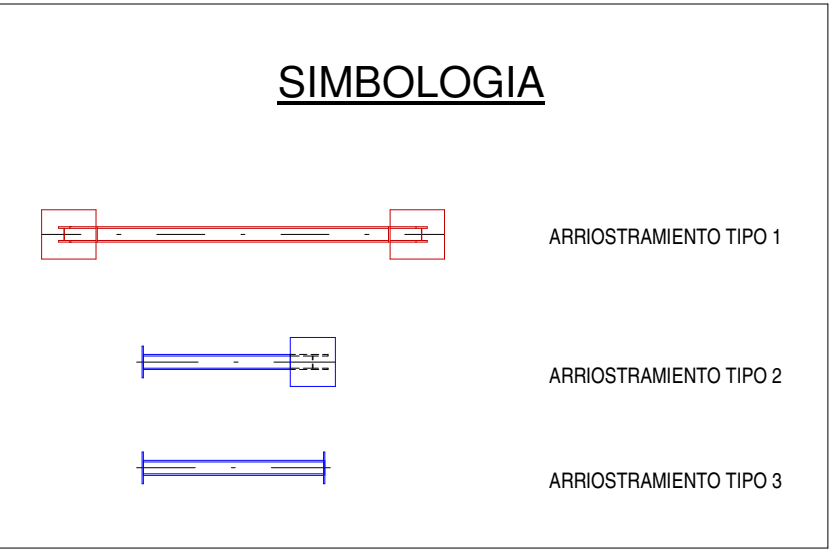






ESCALA 1 : 100

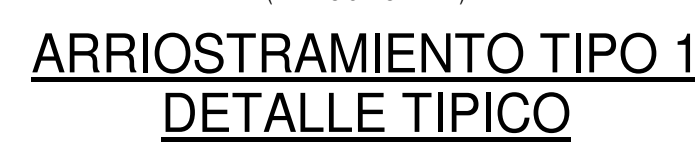

ESCALA 1 : 50



ESCALA 1 : 20

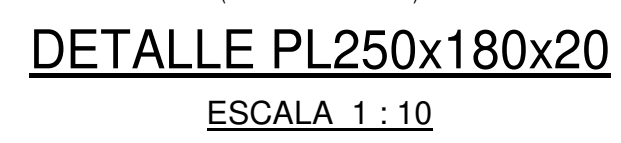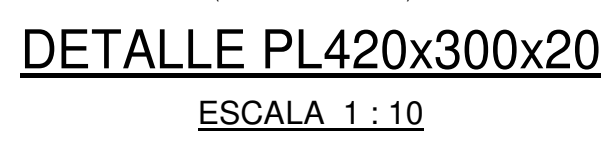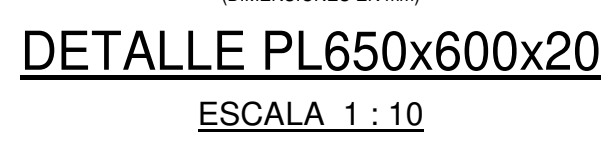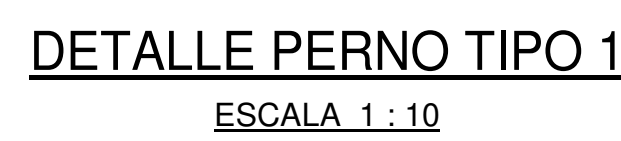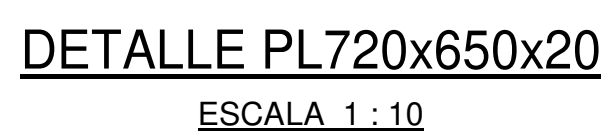

ESCALA 1 : 50



ESCALA 1 : 20



ESCALA 1 : 30



ESCALA 1 : 50

EN NINGUN CASO SE PODRA INICIAR LA FASE DE EXCAVACION EN LA ZONA COMPREDIDA ENTRE LOS EJES J y P1, SIN HABER ANTES TERMINADO LA INSTALACION DE TODOS LOS ARRIOSTRAMIENTOS ENTRE LOS EJES A y J.

NOTAS:

- LOS ARRIOSTRAMIENTOS EN ESTE PLANO SERÁN INSTALADOS TAN PRONTO SEA POSIBLE SEGUN EL AVANCE DE OBRA.
- EN NINGUN CASO SE PODRA INICIAR LA FASE B DE EXCAVACION EN LA ZONA COMPROMENIDA ENTRE LOS EJES J Y P1, SIN HABER ANTES TERMINADO LA INSTALACION DE TODOS LOS ARRIOSTRAMIENTOS ENTRE LOS EJES A Y J.
- TODAS LAS DIMENSIONES SERAN CONFIRMADAS EN OBRA.
- LOS ANCLAJES POSTINSTALADOS INDICADOS EN ESTE PLANO PODRAN SER REEMPLAZADOS POR UN SISTEMA PREINSTALADO, PREVIA APROBACION DEL INGENIERO CALIFICISTA DEL PROYECTO.

MATERIALES:

- ACERO PERFILES y PLACAS A36
- ACERO PERNOS A325
- ACERO ANCLAJES SINDICADO
- SOLDADURA E70XX

[illegible]