

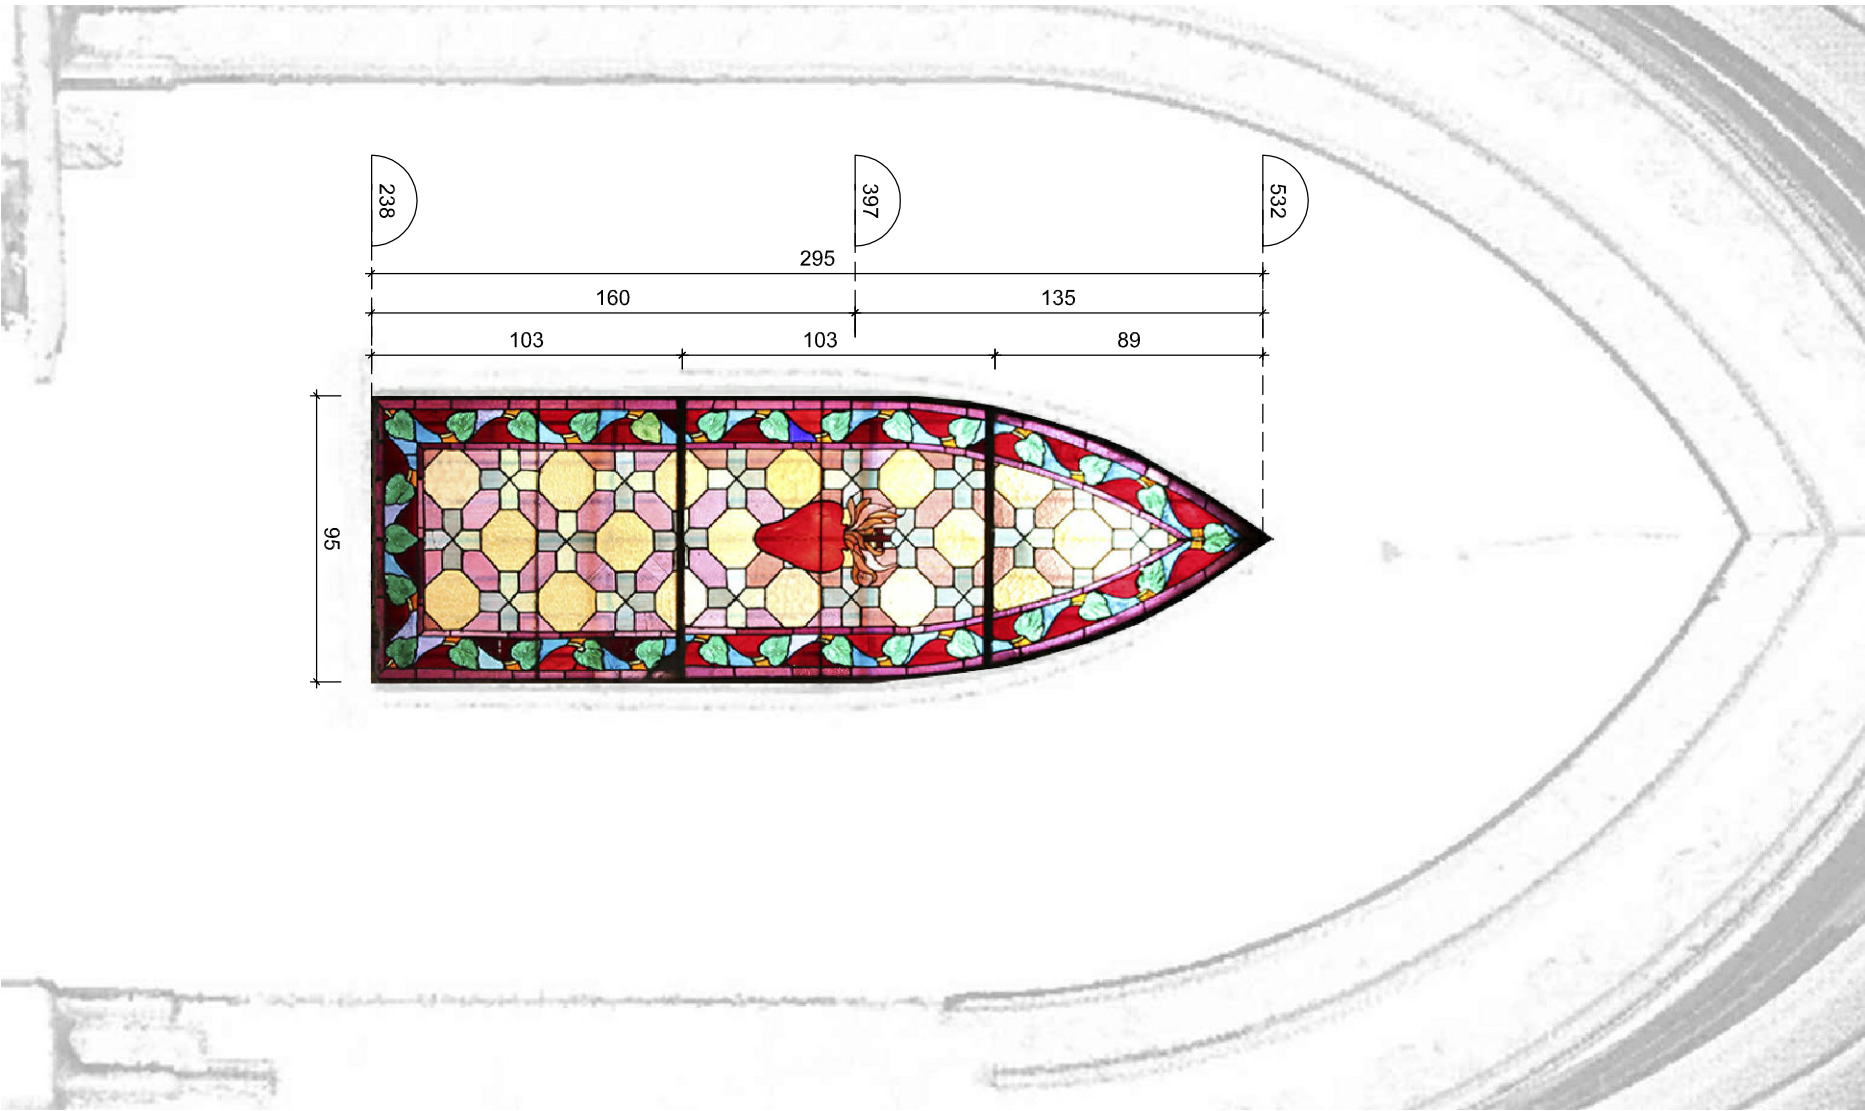


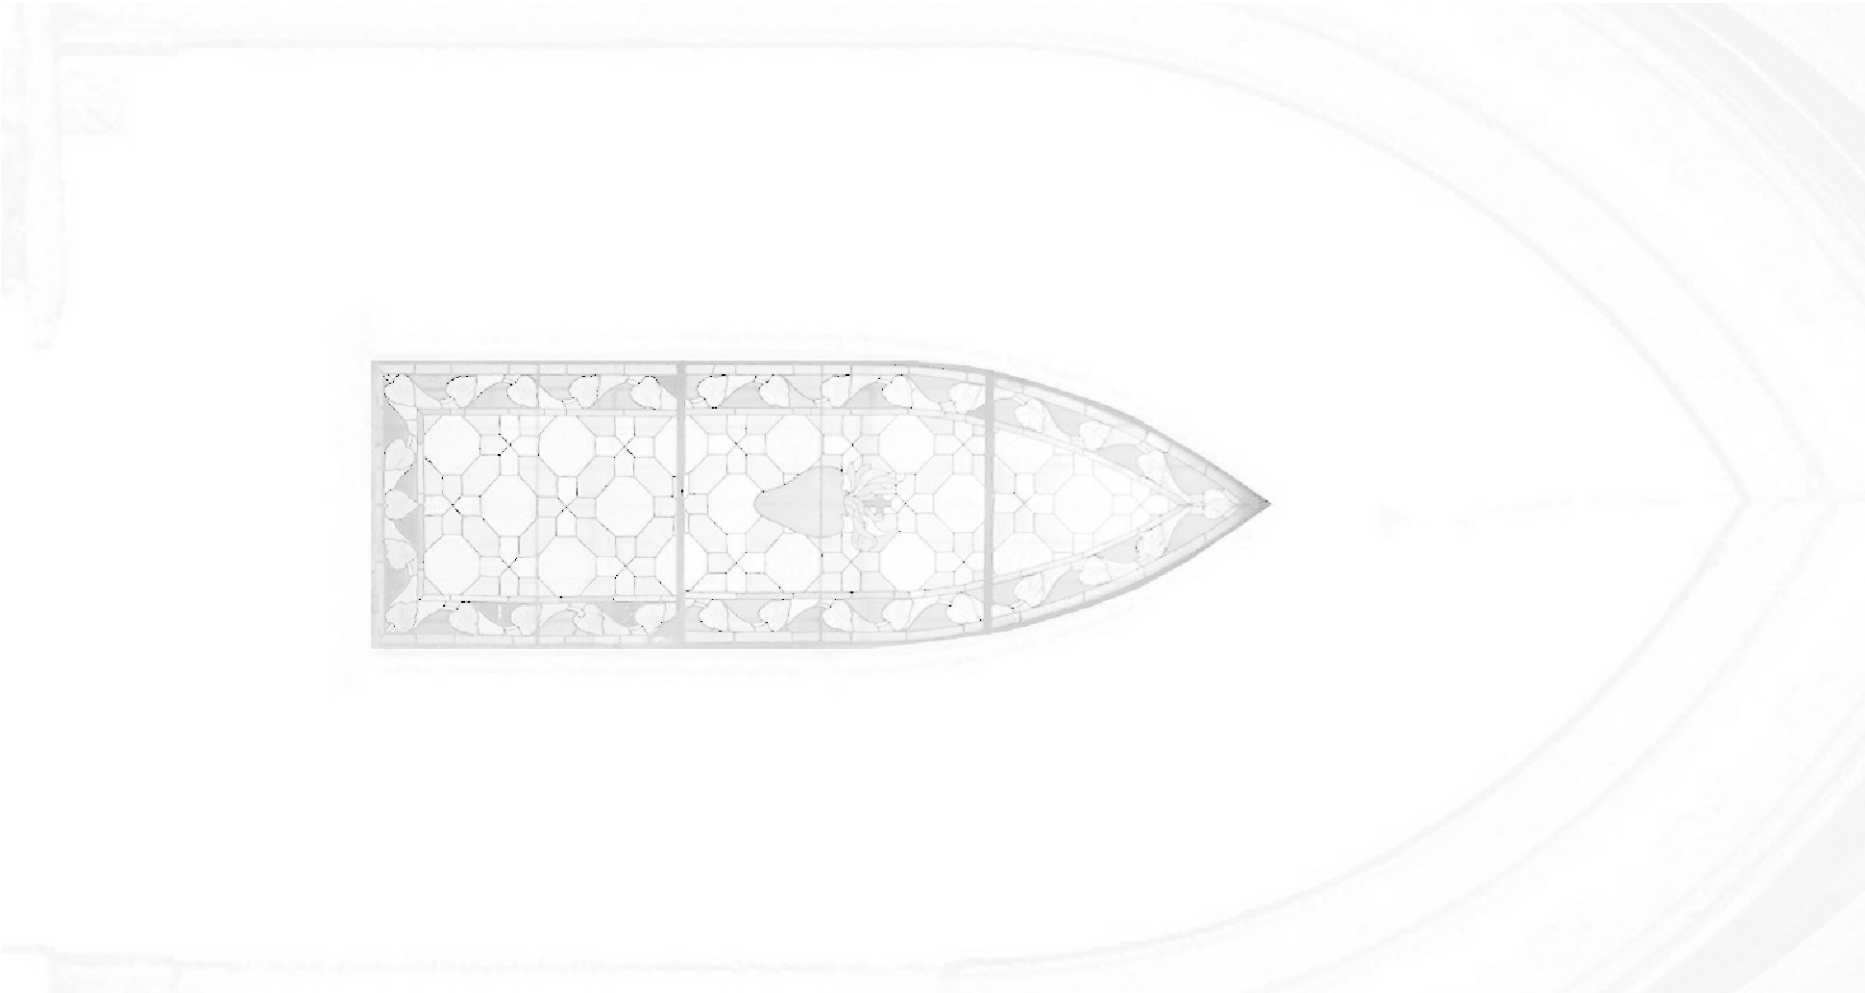

Elevación - Esc. 1/25

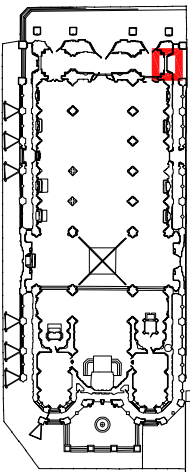

Levantamiento de Daños - Esc. 1/25

Ubicación					
					
				PROYECTO	
DIRECCIÓN DE ARQUITECTURA DIRECCIÓN REGIONAL METROPOLITANA				Arqto. Dino Bozzi F. TÁNDEM Limitada contacto@tandemlimitada.cl	
PROYECTO: REPARACIÓN PARCIAL BASÍLICA DEL SALVADOR STGO					
BASÍLICA DEL SALVADOR				ES	
Huérfanos 1796 - Santiago Región Metropolitana				Vi-01	
LEVANTAMIENTO VITRAL 01 "Sagrado Corazón" en nártex				1/25	Ago.13
				Escala	Fecha
TD	TD	LEV	DET	-	A
1305					
Emisor	Proyecto	Fase	Tipo	Zona	Índice
Dibujó: RM	Controló: VI	Archivo de ref.: TD_1212_LEV_ES_V401-05.dwg			