

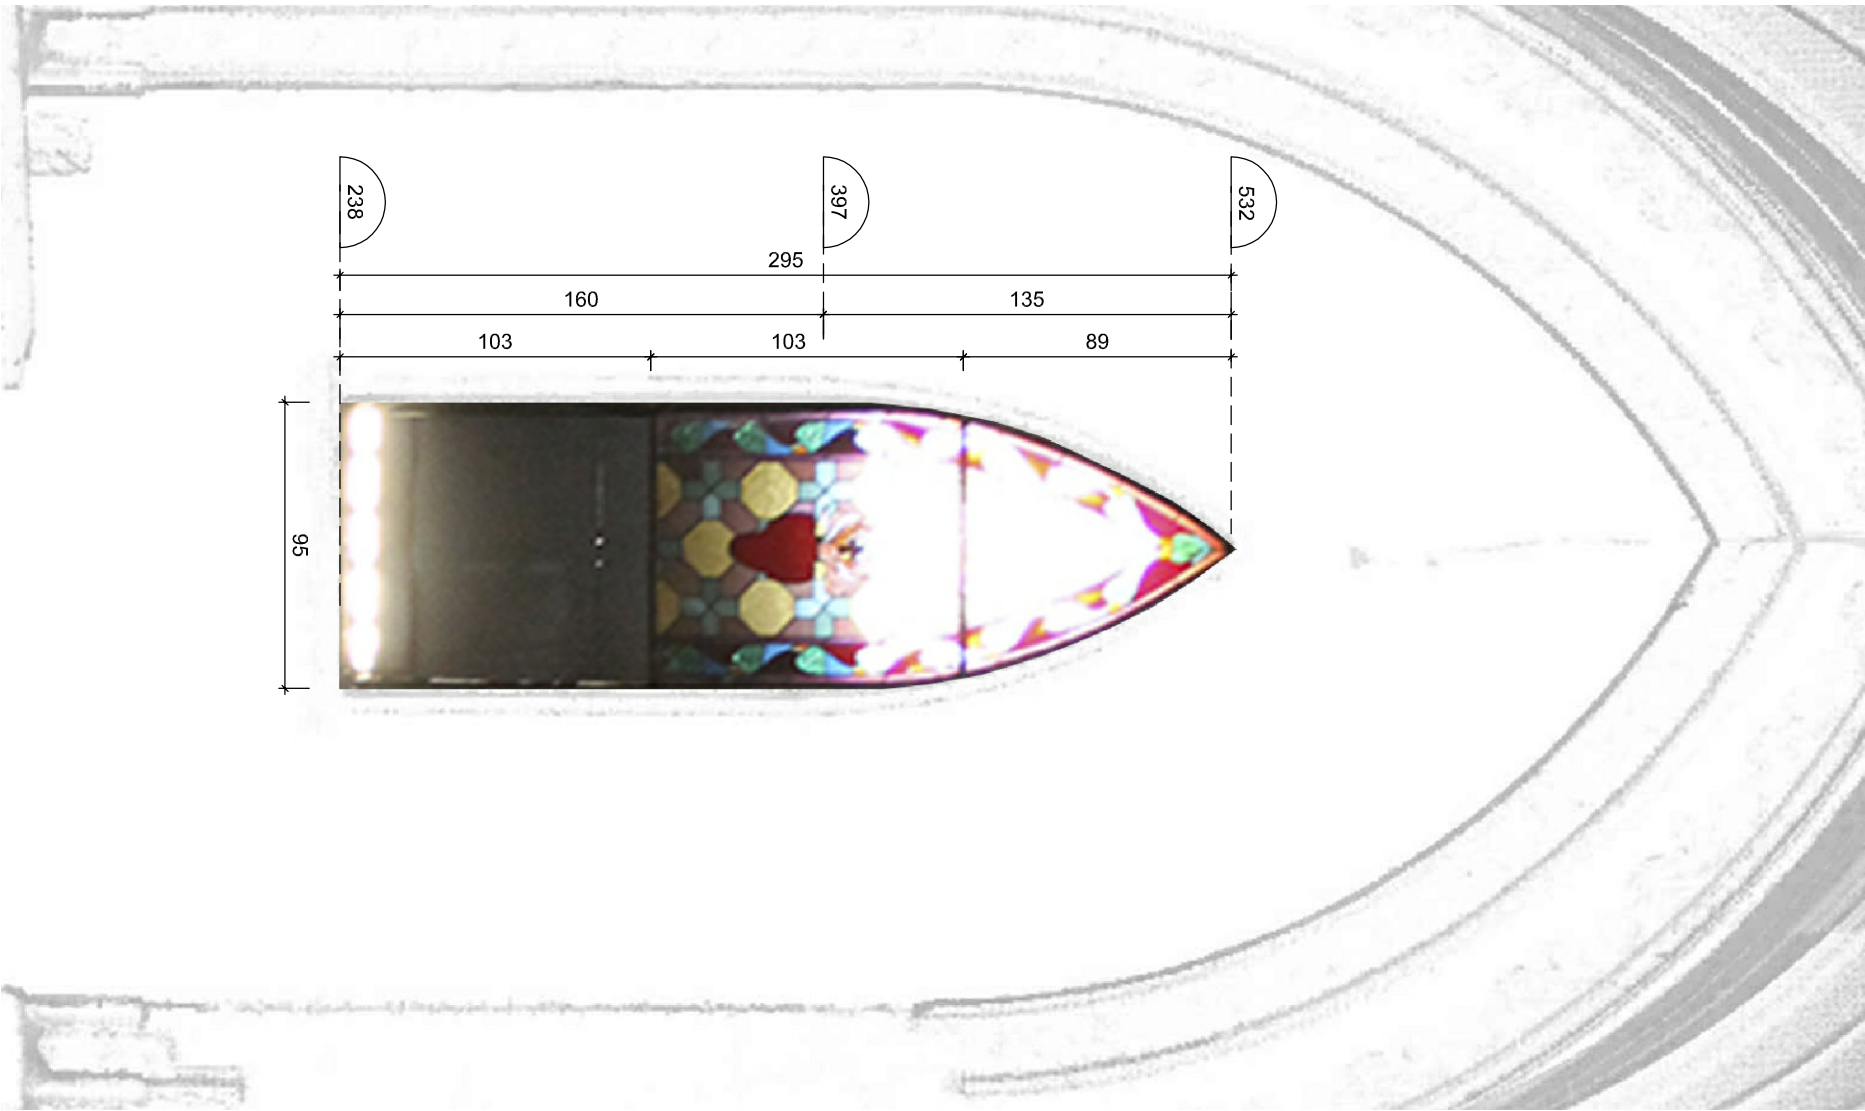


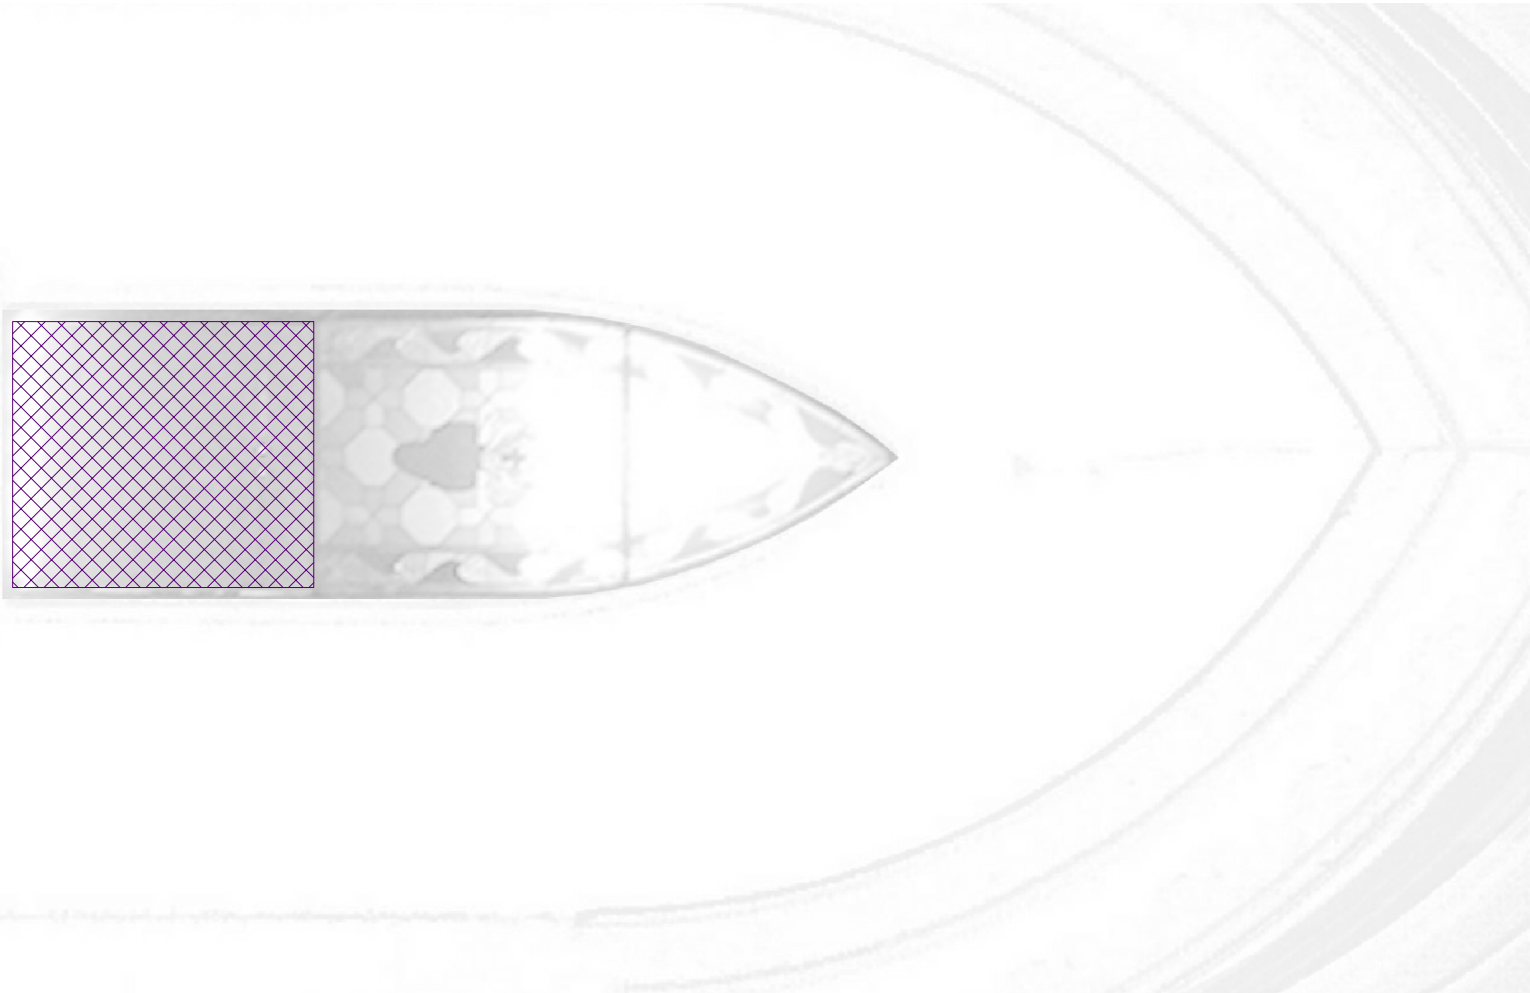

Elevación - Esc. 1/25

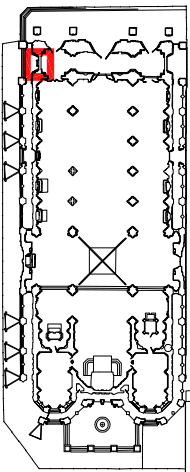

Levantamiento de Daños - Esc. 1/25

Ubicación					
					
			PROYECTO		
DIRECCIÓN DE ARQUITECTURA DIRECCIÓN REGIONAL METROPOLITANA			Arqto. Dino Bozzi F. TÁNDEM Limitada contacto@tandemlimitada.cl		
PROYECTO: REPARACIÓN PARCIAL BASÍLICA DEL SALVADOR STGO					
BASÍLICA DEL SALVADOR				ES	
Huérfanos 1796 - Santiago				Vi-02	
Región Metropolitana					
LEVANTAMIENTO VITRAL 02			1/25	Ago. 13	
"Sagrado Corazón" en nártex			Escala	Fecha	
TD	TD	LEV	DET	-	A
Emisor	Proyecto	Fase	Tipo	Zona	Índice
Dibujó: RM			Controló: VI		
Archivo de ref.: TD_1212_LEV_ES_V401-05.dwg					