



Elevación - Esc. 1/25

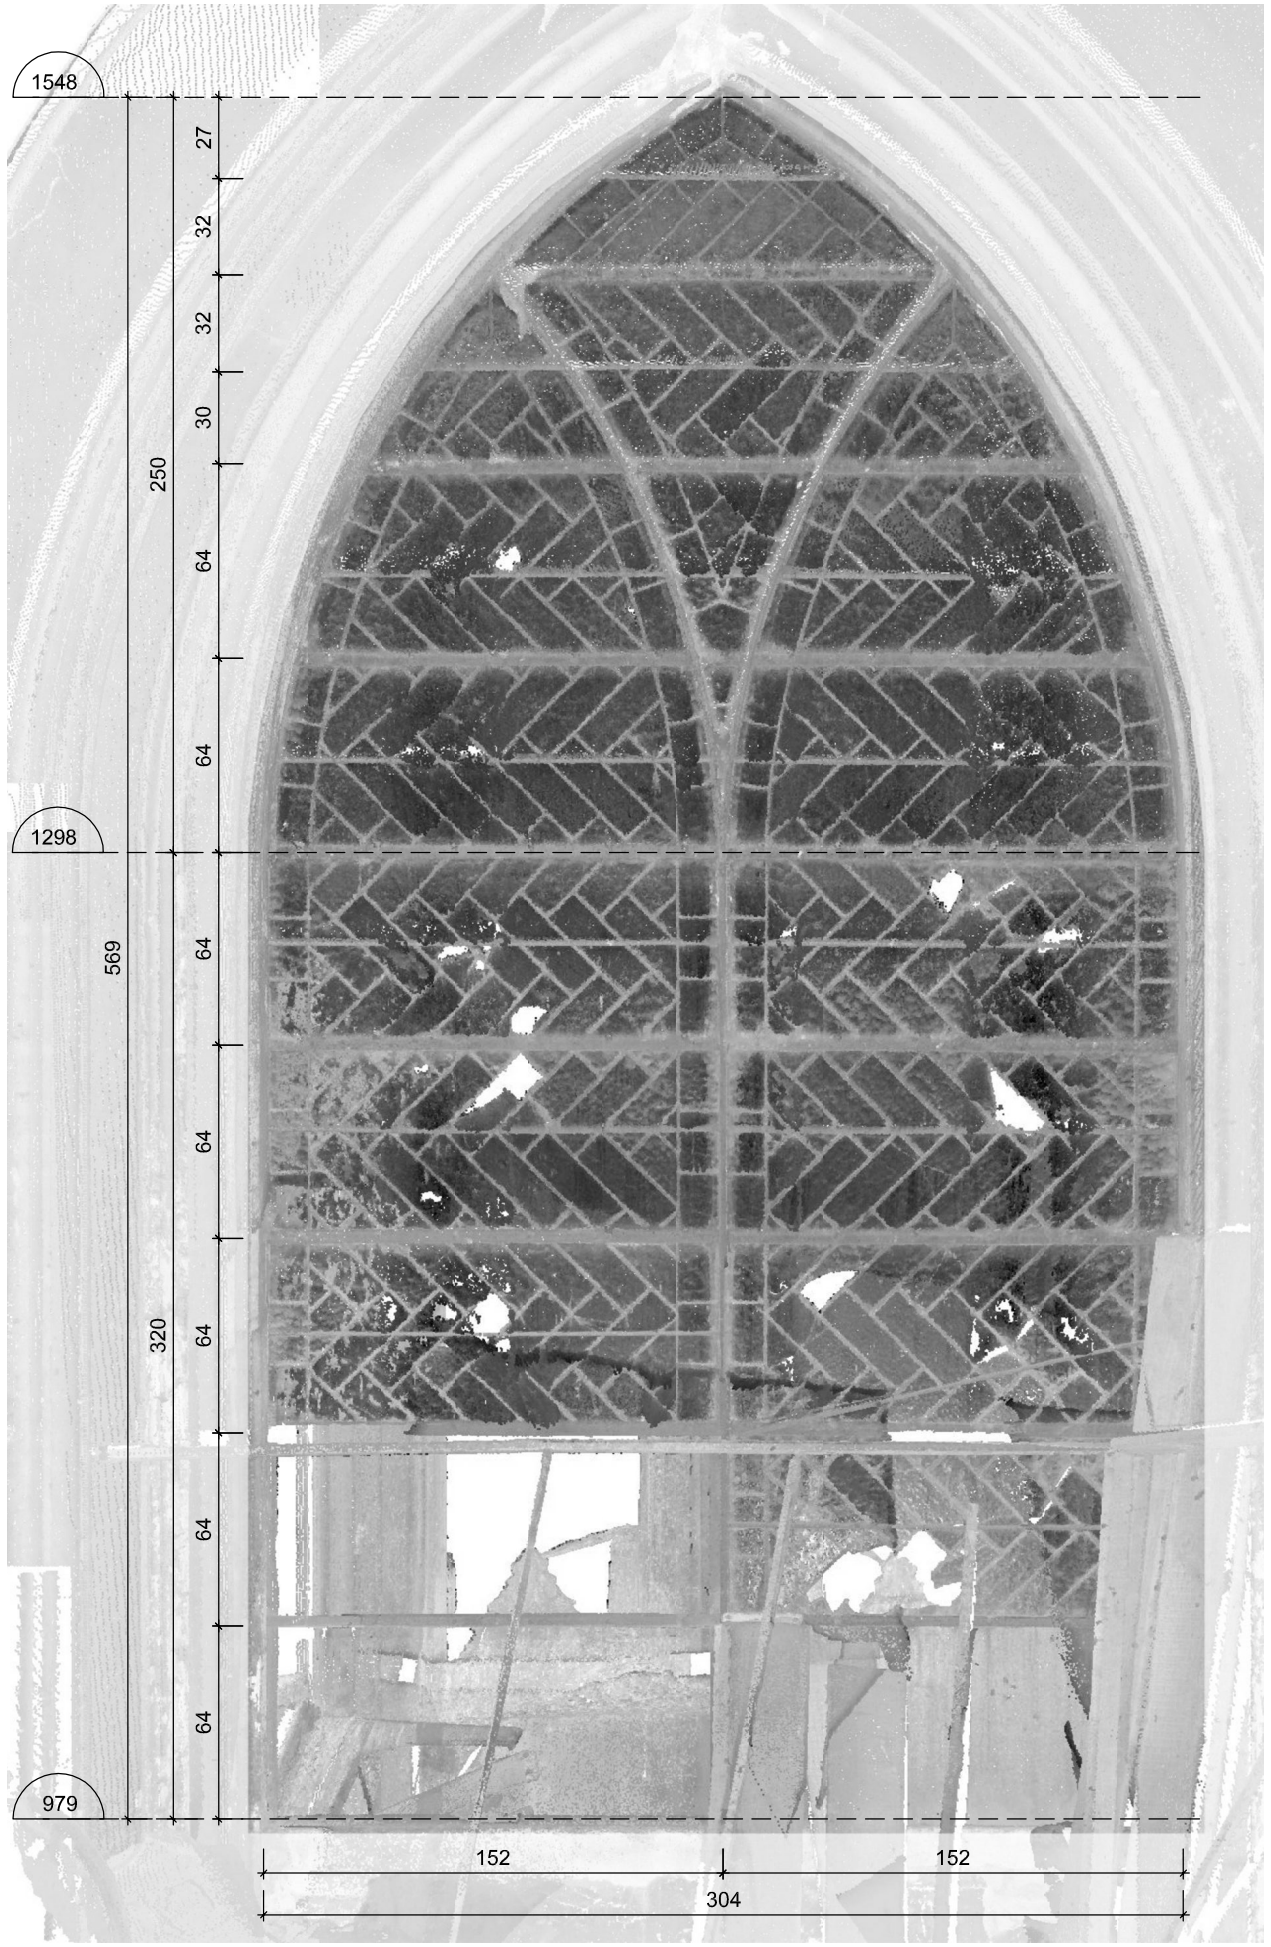

Levantamiento de Daños - Esc. 1/25

Ubicación

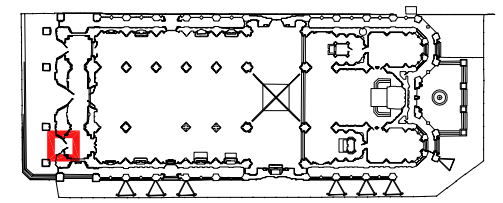

Dirección de Arquitectura
Ministerio de Obras Públicas
Gobierno de Chile

PROYECTO

Arqto. Dino Bozzi F.
TÁNDEM Limitada
contacto@tandemlimitada.cl

DIRECCIÓN DE ARQUITECTURA
DIRECCIÓN REGIONAL METROPOLITANA

PROYECTO: REPARACIÓN PARCIAL BASÍLICA DEL SALVADOR STGO

BASÍLICA DEL SALVADOR

Huérfanos 1796 - Santiago
Región Metropolitana

ES
Vi-03

LEVANTAMIENTO VITRAL 03 vitral geométrico en coro		1/25 Escala	Ago.13 Fecha

TD	TD 1305	LEV	DET	-	A
Emisor	Proyecto	Fase	Tipo	Zona	Índice

Dibujo: RM Control : VI

Archivo de ref. TD_1212_LEV_ES_VI-01-05.dwg