



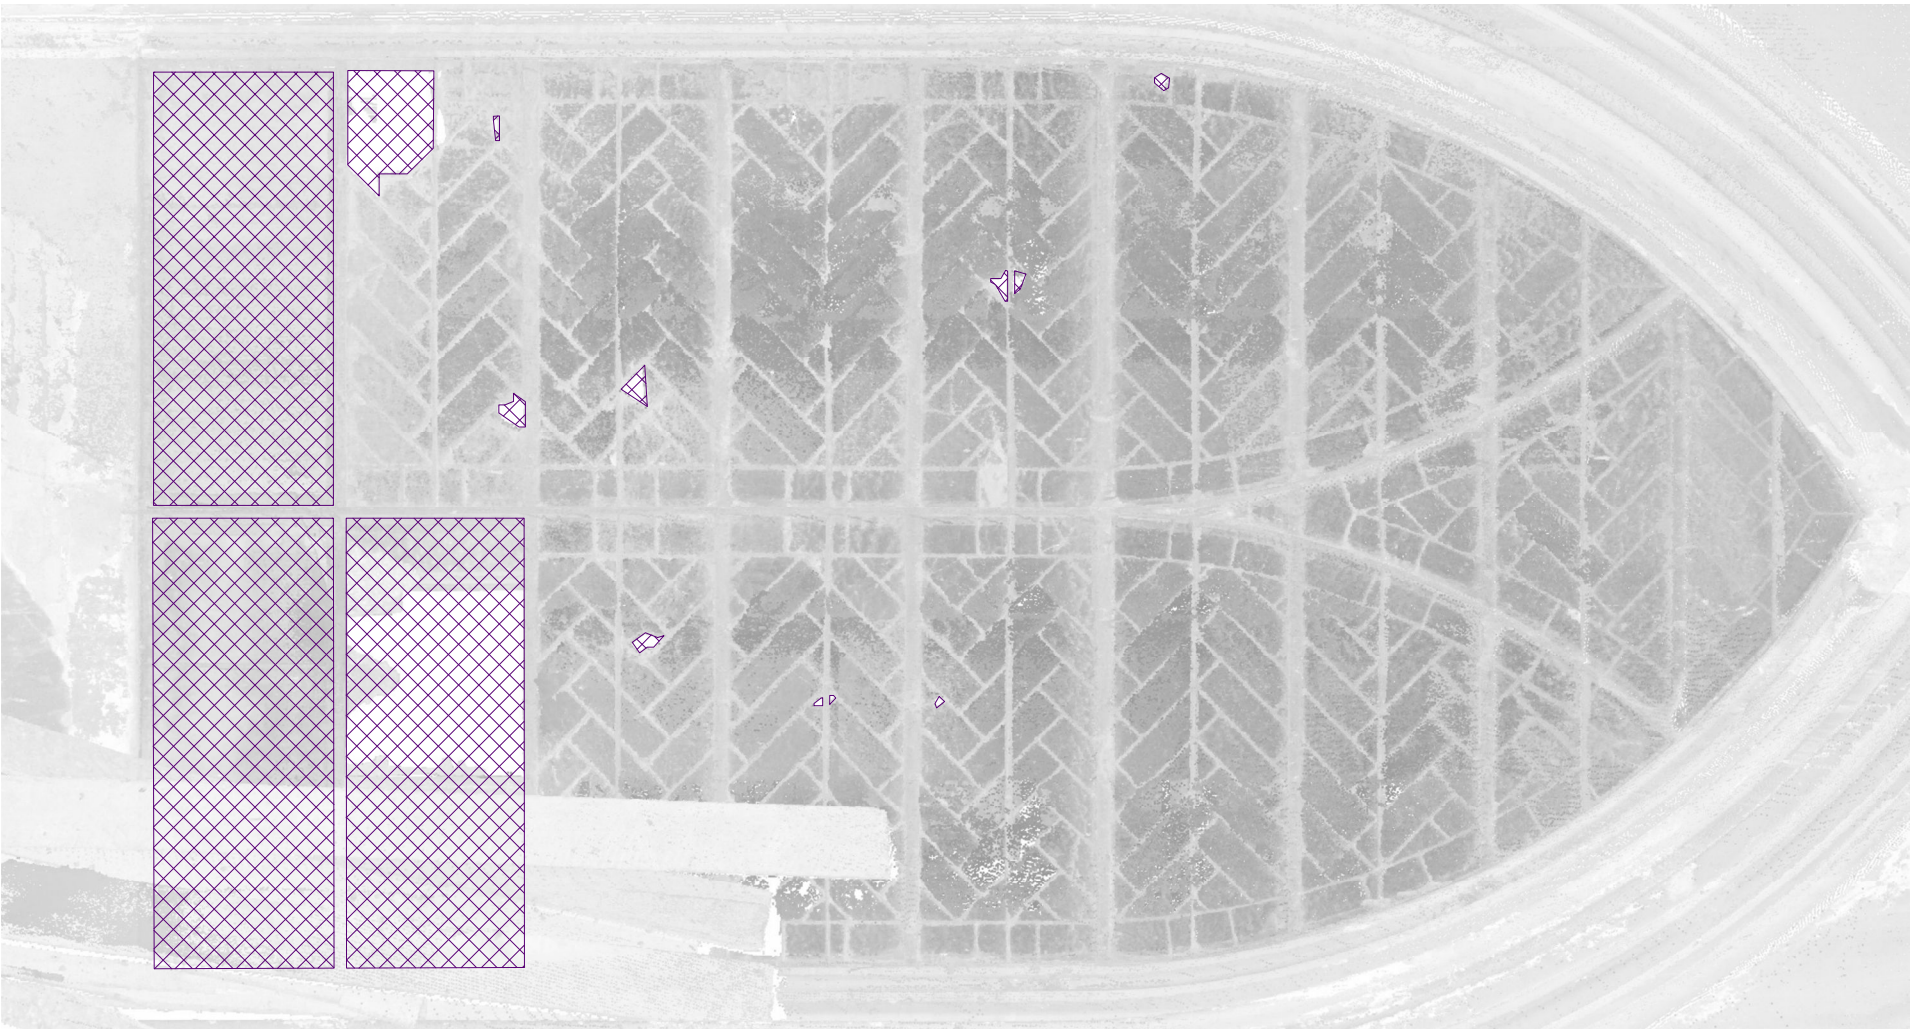

Elevación - Esc. 1/25

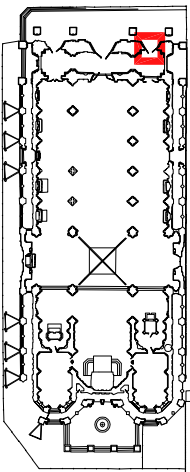

Levantamiento de Daños - Esc. 1/25

Ubicación							
				PROYECTO			
DIRECCIÓN DE ARQUITECTURA DIRECCIÓN REGIONAL METROPOLITANA				Arqto. Dino Bozzi F. TÁNDEM Limitada contacto@tandemlimitada.cl			
PROYECTO: REPARACIÓN PARCIAL BASÍLICA DEL SALVADOR STGO							
BASÍLICA DEL SALVADOR				ES			
Huérfanos 1796 - Santiago Región Metropolitana				Vi-05			
LEVANTAMIENTO VITRAL 03				1/25		Ago. 13	
vitral geométrico en coro				Escala		Fecha	
TD	TD	LEV	DET	-	A		
Emisor	Proyecto	Fase	Tipo	Zona	Índice		
Dibujó: RM				Controló: VI			
Archivo de ref.: TD_1212_LEV_ES_Vi01-05.dwg							