



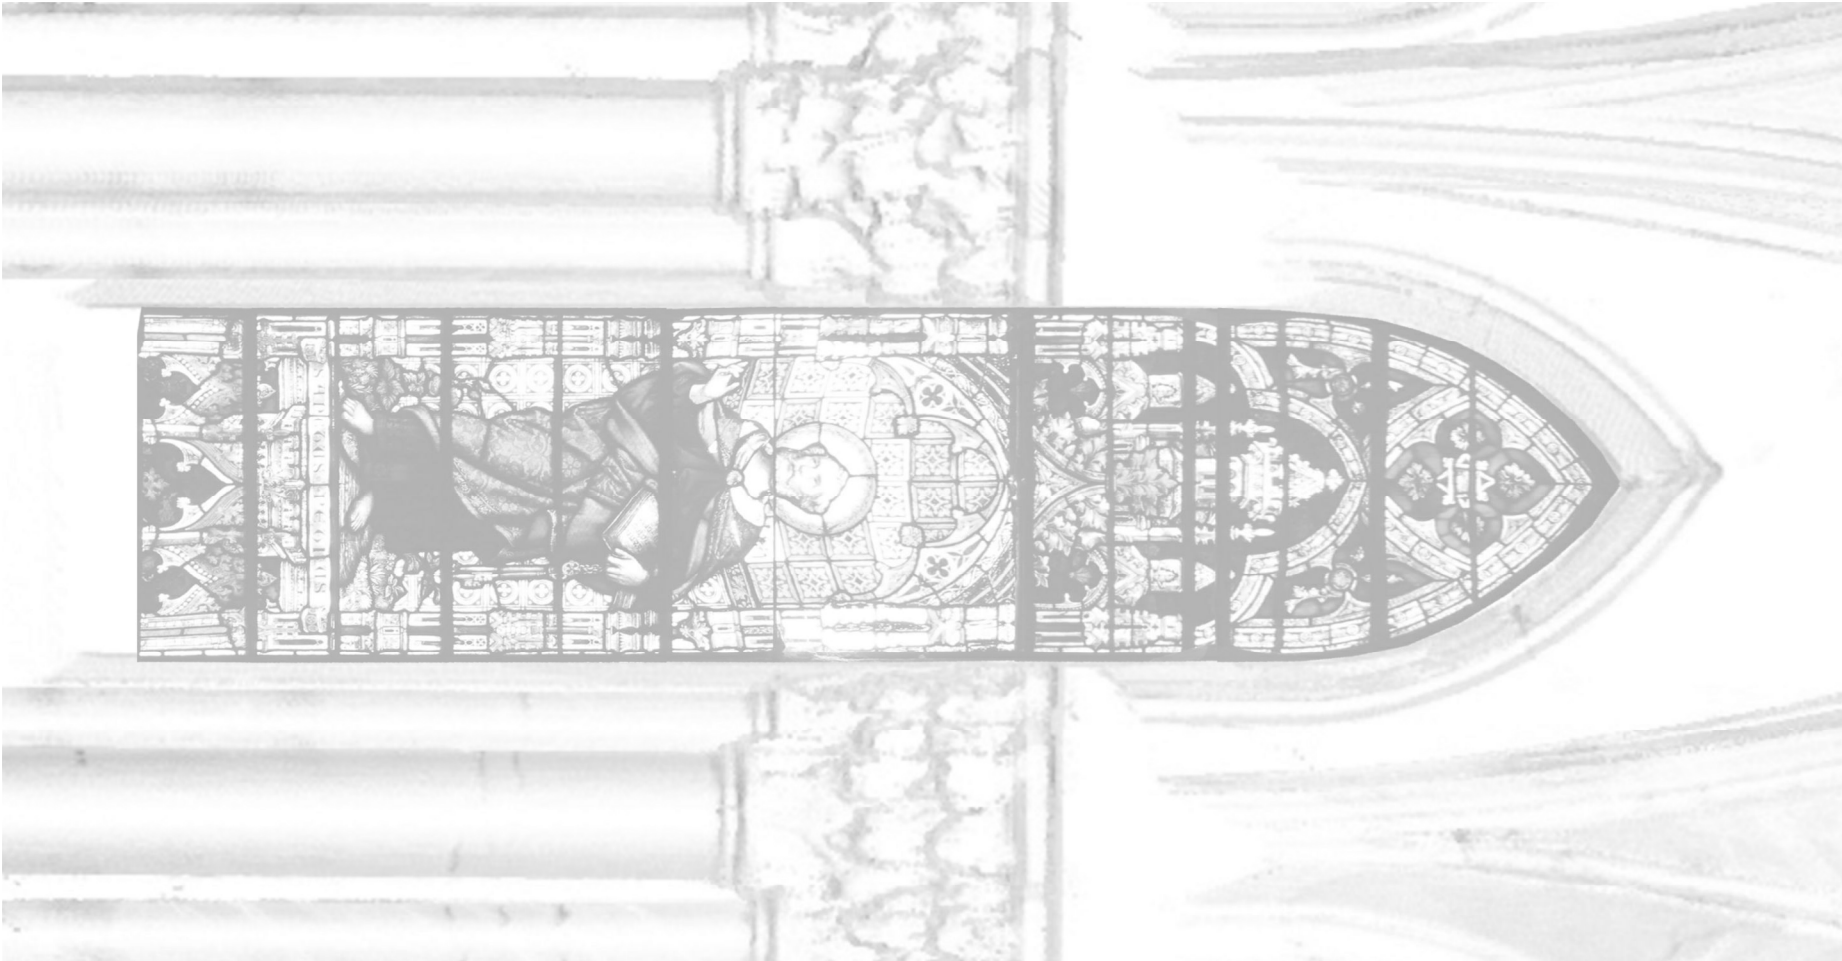

Elevación
Esc. 1/25

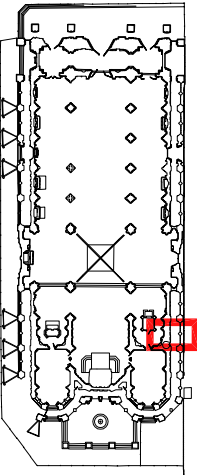

Levantamiento de Daños
Esc. 1/25

Ubicación				
				
DIRECCIÓN DE ARQUITECTURA DIRECCIÓN REGIONAL METROPOLITANA			PROYECTO	
PROYECTO: REPARACIÓN PARCIAL BASÍLICA DEL SALVADOR STGO			PROYECTO	
			Arqto. Dino Bozzi F. TÁNDEM Limitada contacto@tandemlimitada.cl	
BASÍLICA DEL SALVADOR				ES
Huérfanos 1796 - Santiago Región Metropolitana				Vi-14
LEVANTAMIENTO VITRAL 14				1/25
"San Pedro"				Escala
TD	TD	LEV	DET	-
Emisor	Proyecto	Fase	Tipo	Zona
Índice				A
Dibuj: RM Control: VI Archivo de ref.: TD_1212_LEV_ES_V406-14.dwg				