

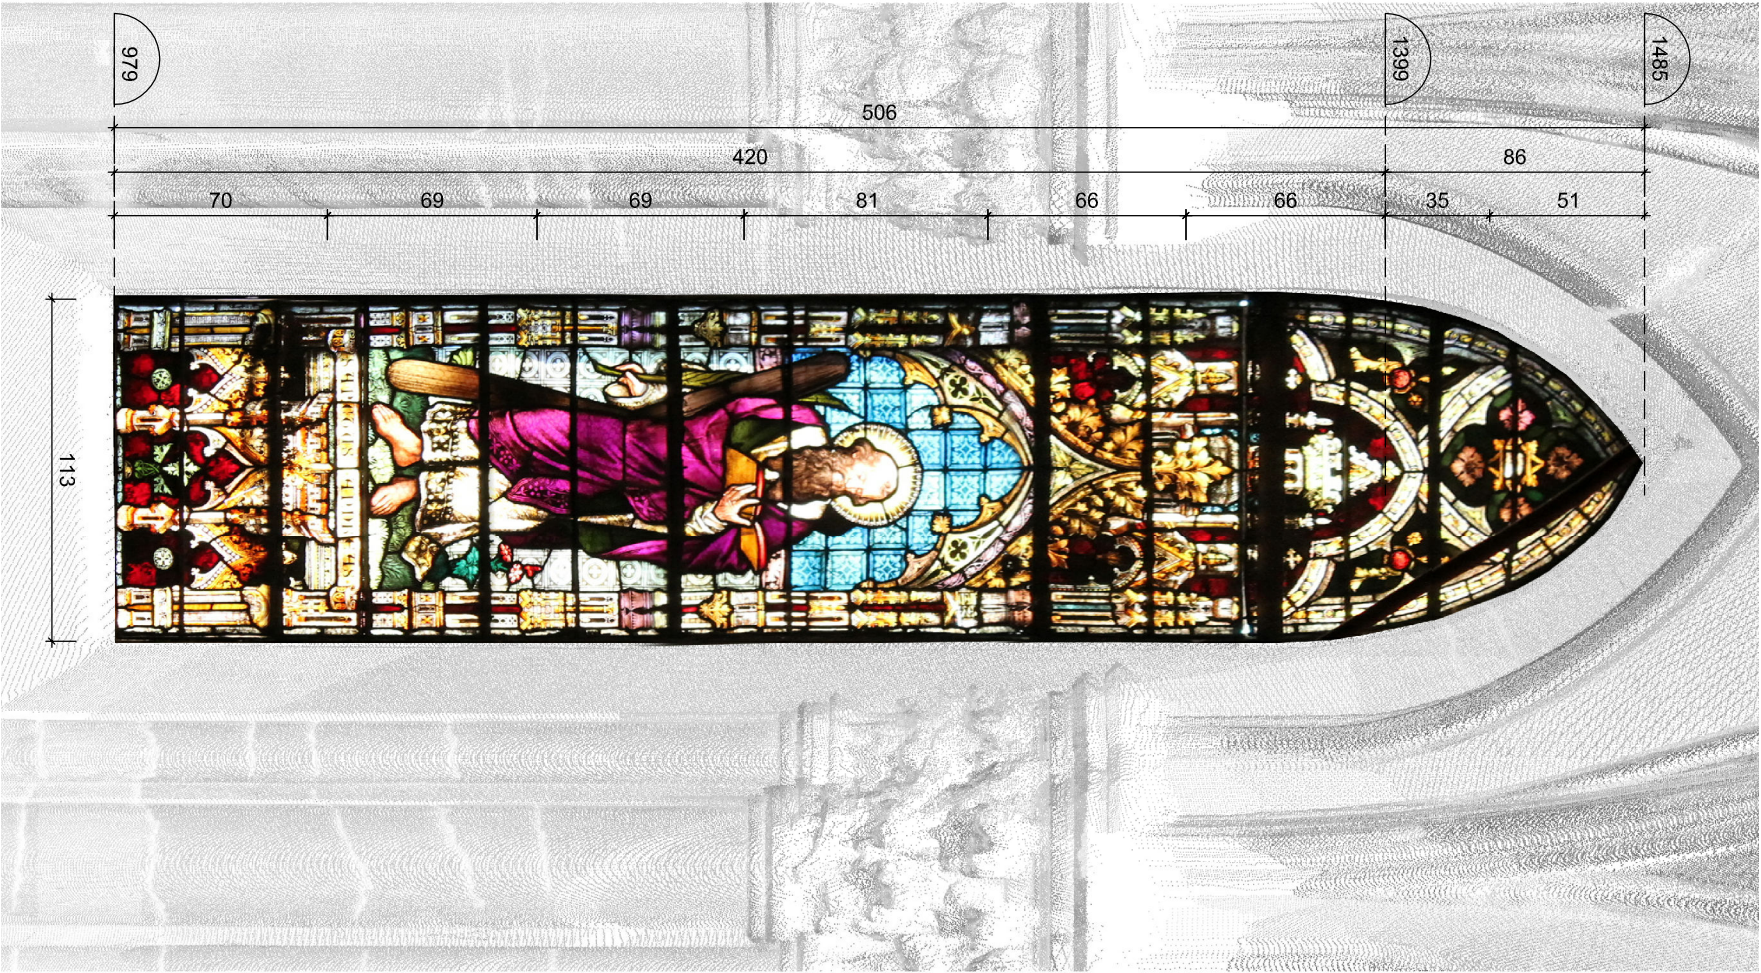


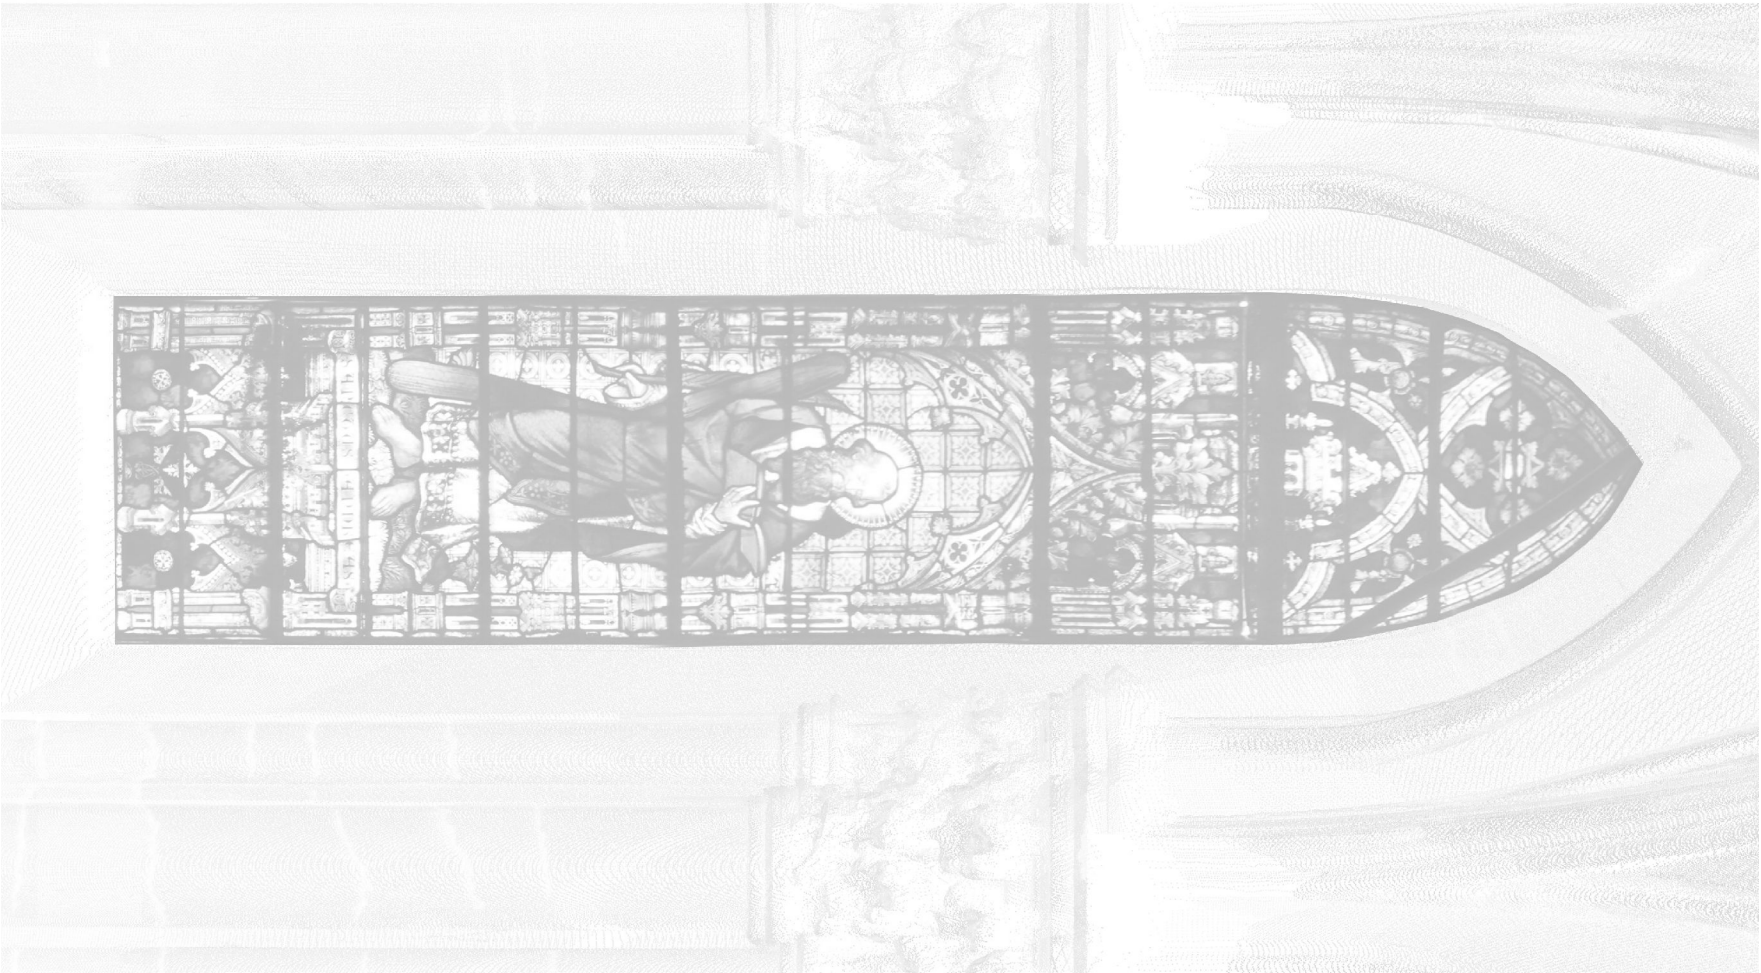

Elevación
Esc. 1/25

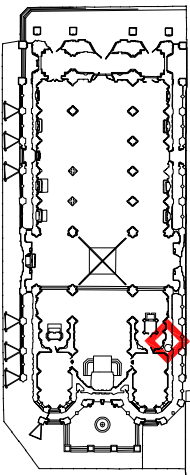

Levantamiento de Daños
Esc. 1/25

Ubicación				
				
			PROYECTO	
Arqto. Dino Bozzi F. TÁNDEM Limitada contacto@tandemlimitada.cl				
DIRECCIÓN DE ARQUITECTURA DIRECCIÓN REGIONAL METROPOLITANA				
PROYECTO: REPARACIÓN PARCIAL BASÍLICA DEL SALVADOR STGO				
BASÍLICA DEL SALVADOR				ES
Huérfanos 1796 - Santiago Región Metropolitana				Vi-15
LEVANTAMIENTO VITRAL 15			1/25	Ago. 13
"San Andrés"			Escala	Fecha
TD	TD	LEV	DET	-
1305				A
Emisor	Proyecto	Fase	Tipo	Zona
Dibuj: RM	Control: VI	Archivo de ref.: TD_1212_LEV_ES_VI-15-25.0m9		