

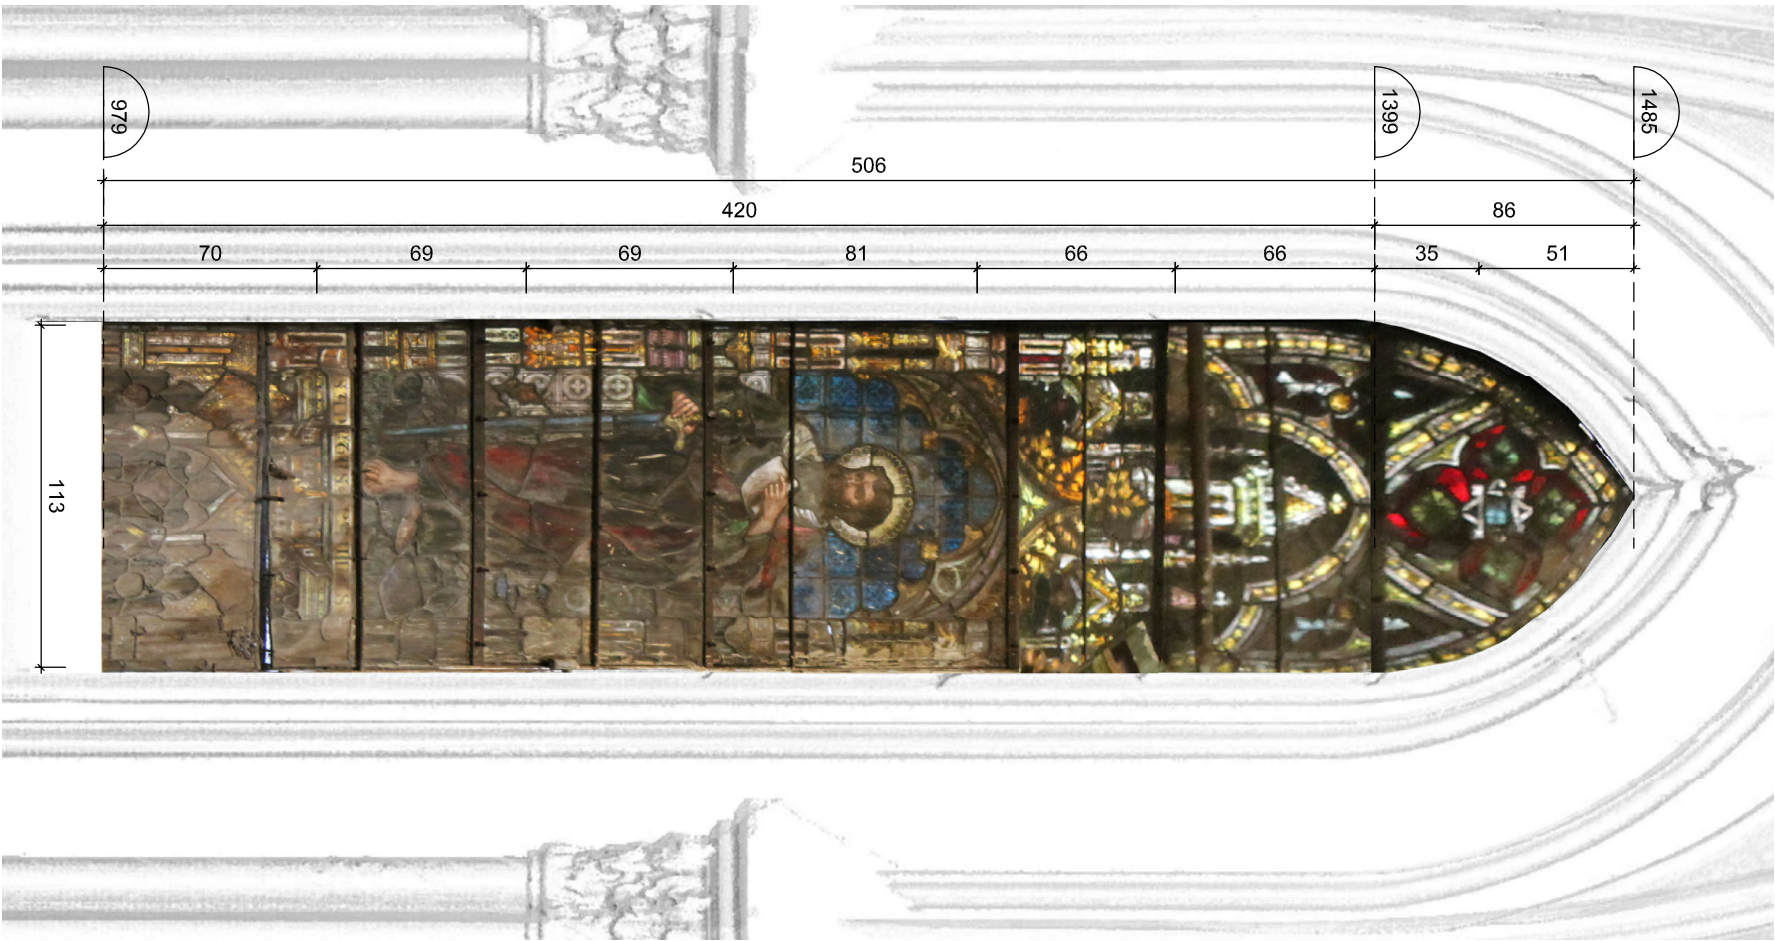


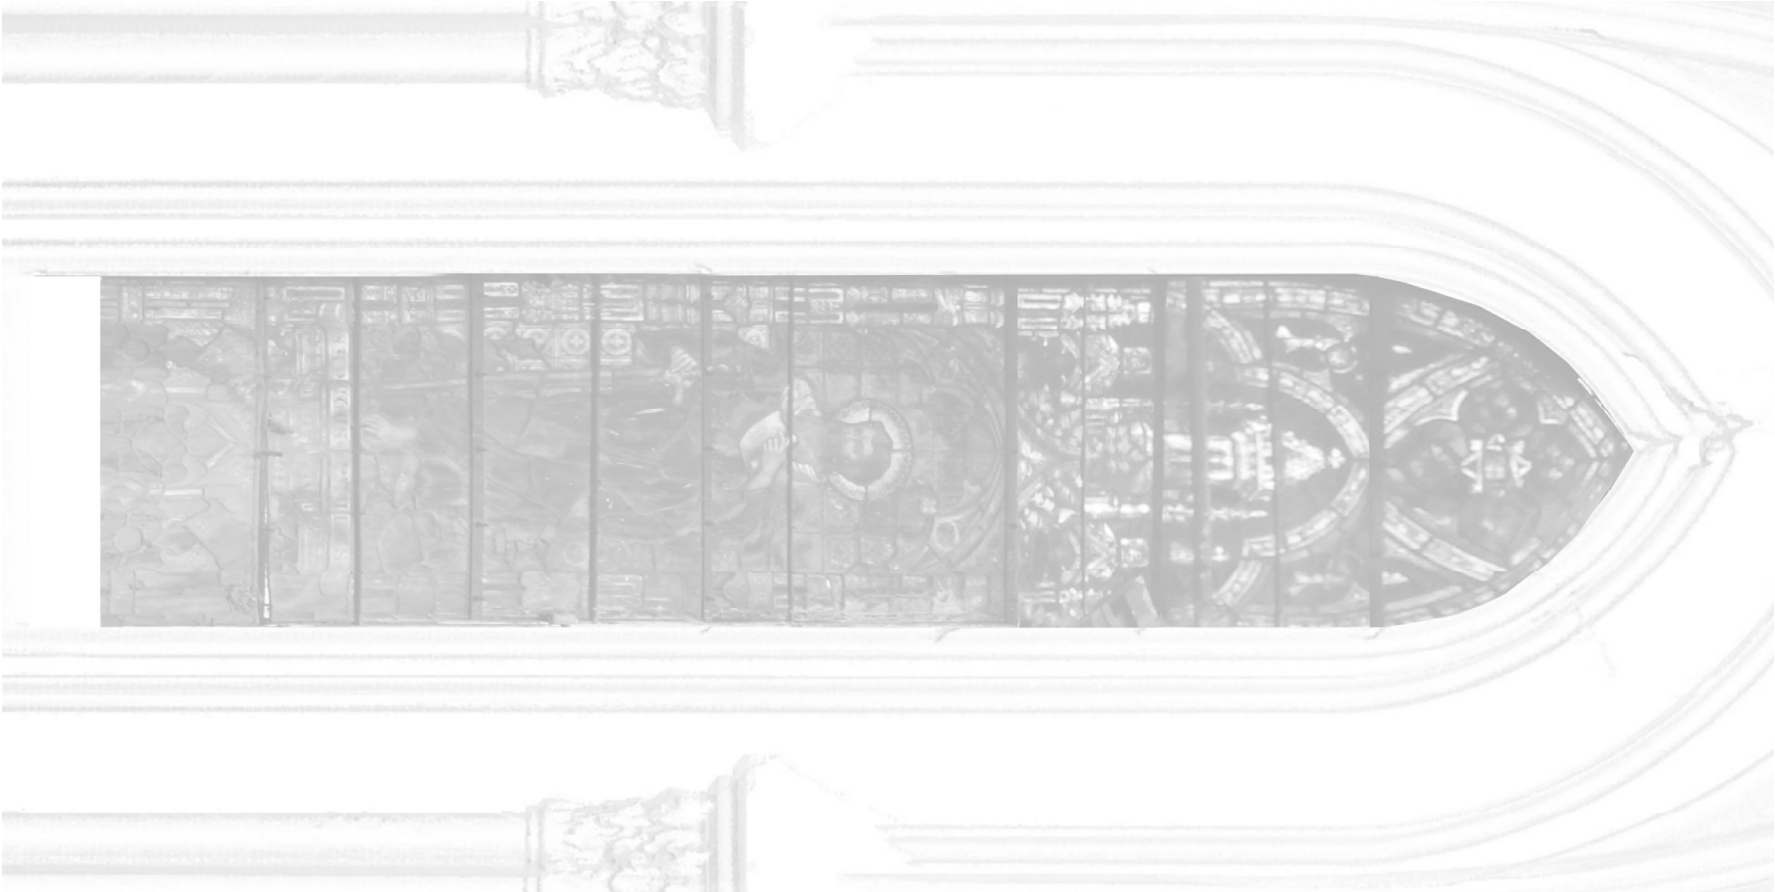

Elevación
Esc. 1/25

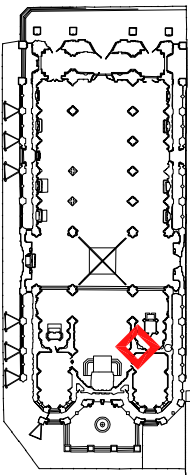

Levantamiento de Daños
Esc. 1/25

Ubicación					
			PROYECTO		
			Arqto. Dino Bozzi F. TÁNDEM Limitada contacto@tandemlimitada.cl		
DIRECCIÓN DE ARQUITECTURA DIRECCIÓN REGIONAL METROPOLITANA					
PROYECTO: REPARACIÓN PARCIAL BASÍLICA DEL SALVADOR STGO					
BASÍLICA DEL SALVADOR				ES	
Huérfanos 1796 - Santiago Región Metropolitana				Vi-17	
LEVANTAMIENTO VITRAL 17			1/25	Ago. 13	
"San Pablo"			Escala	Fecha	
TD	TD	LEV	DET	-	A
Emisor	Proyecto	Fase	Tipo	Zona	Índice
Dibuj: RM			Control: VI		
Archivo de ref.: TD_1212_LEV_ES_Vi-15-25.0m9					