



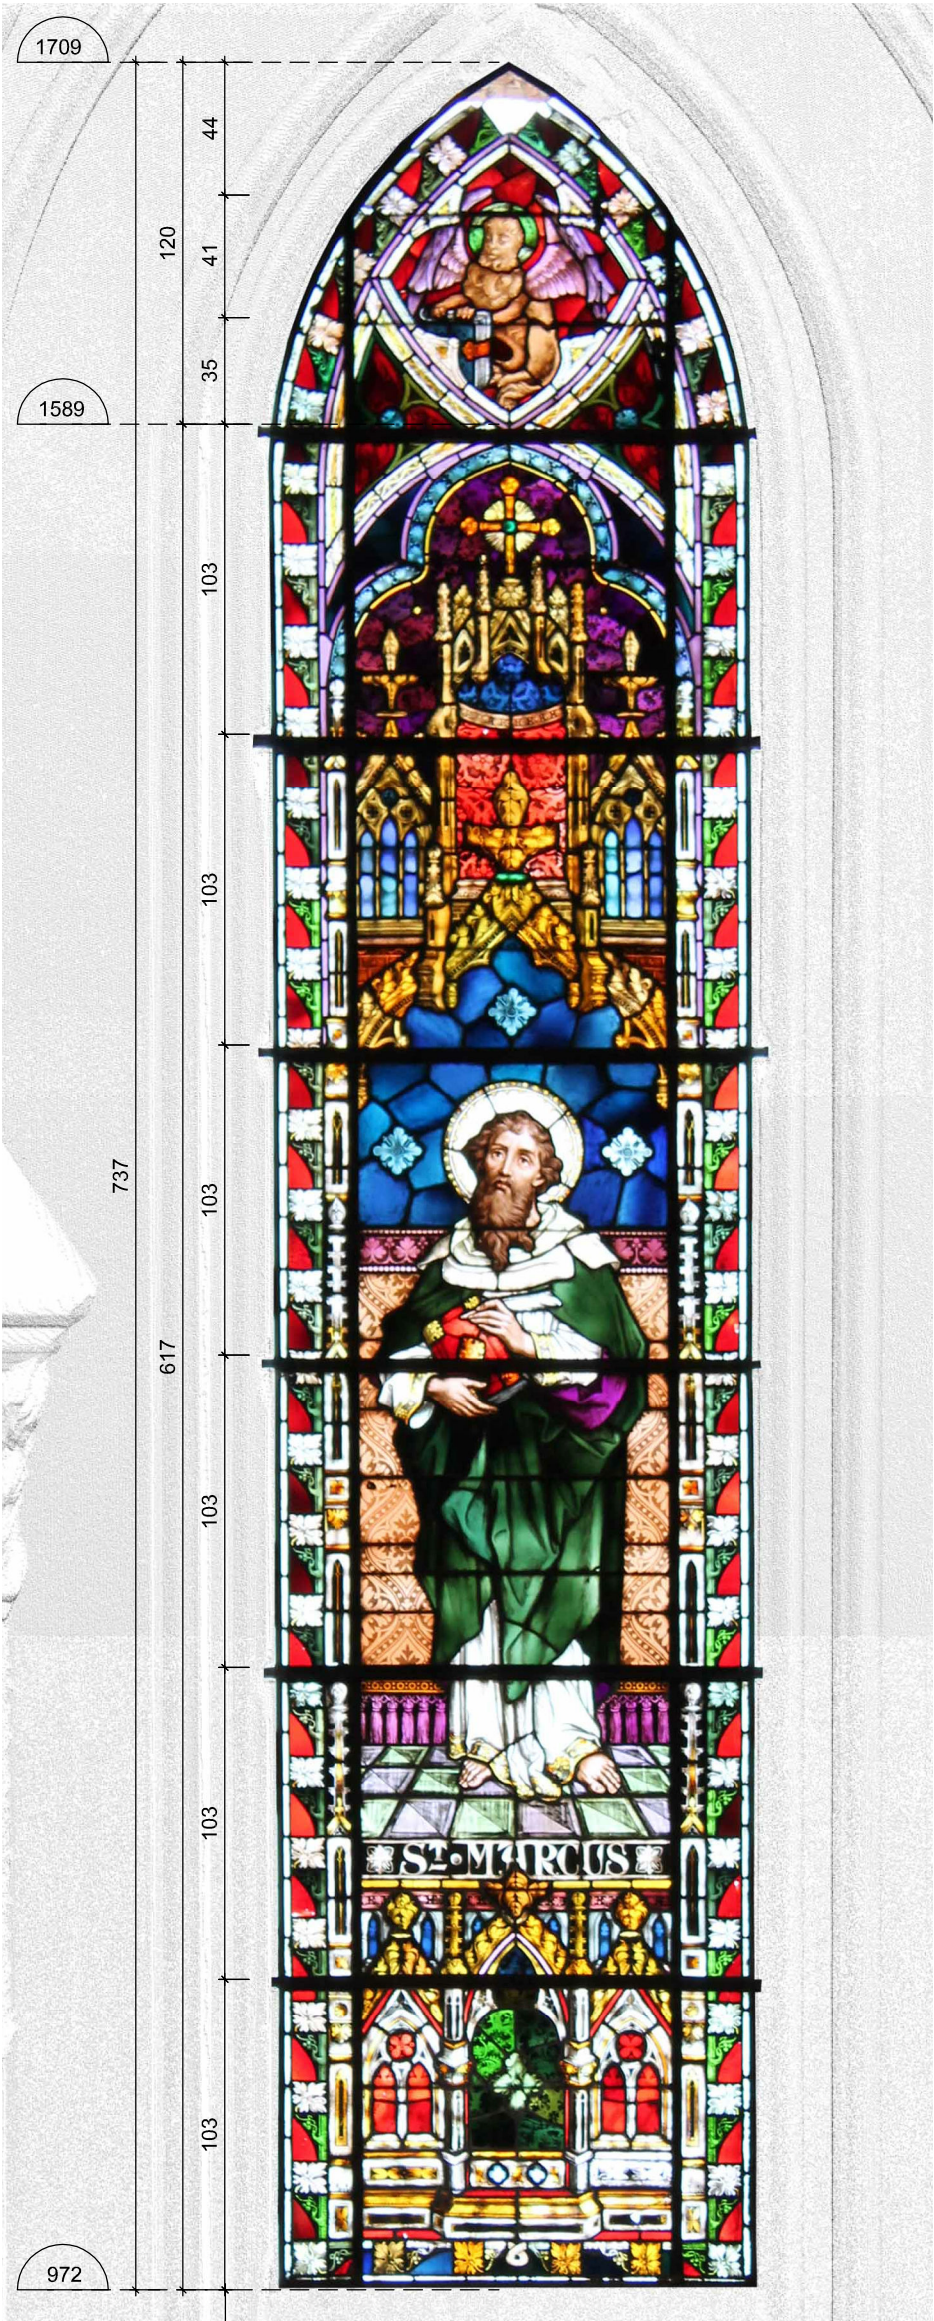

Elevación
Esc. 1/25

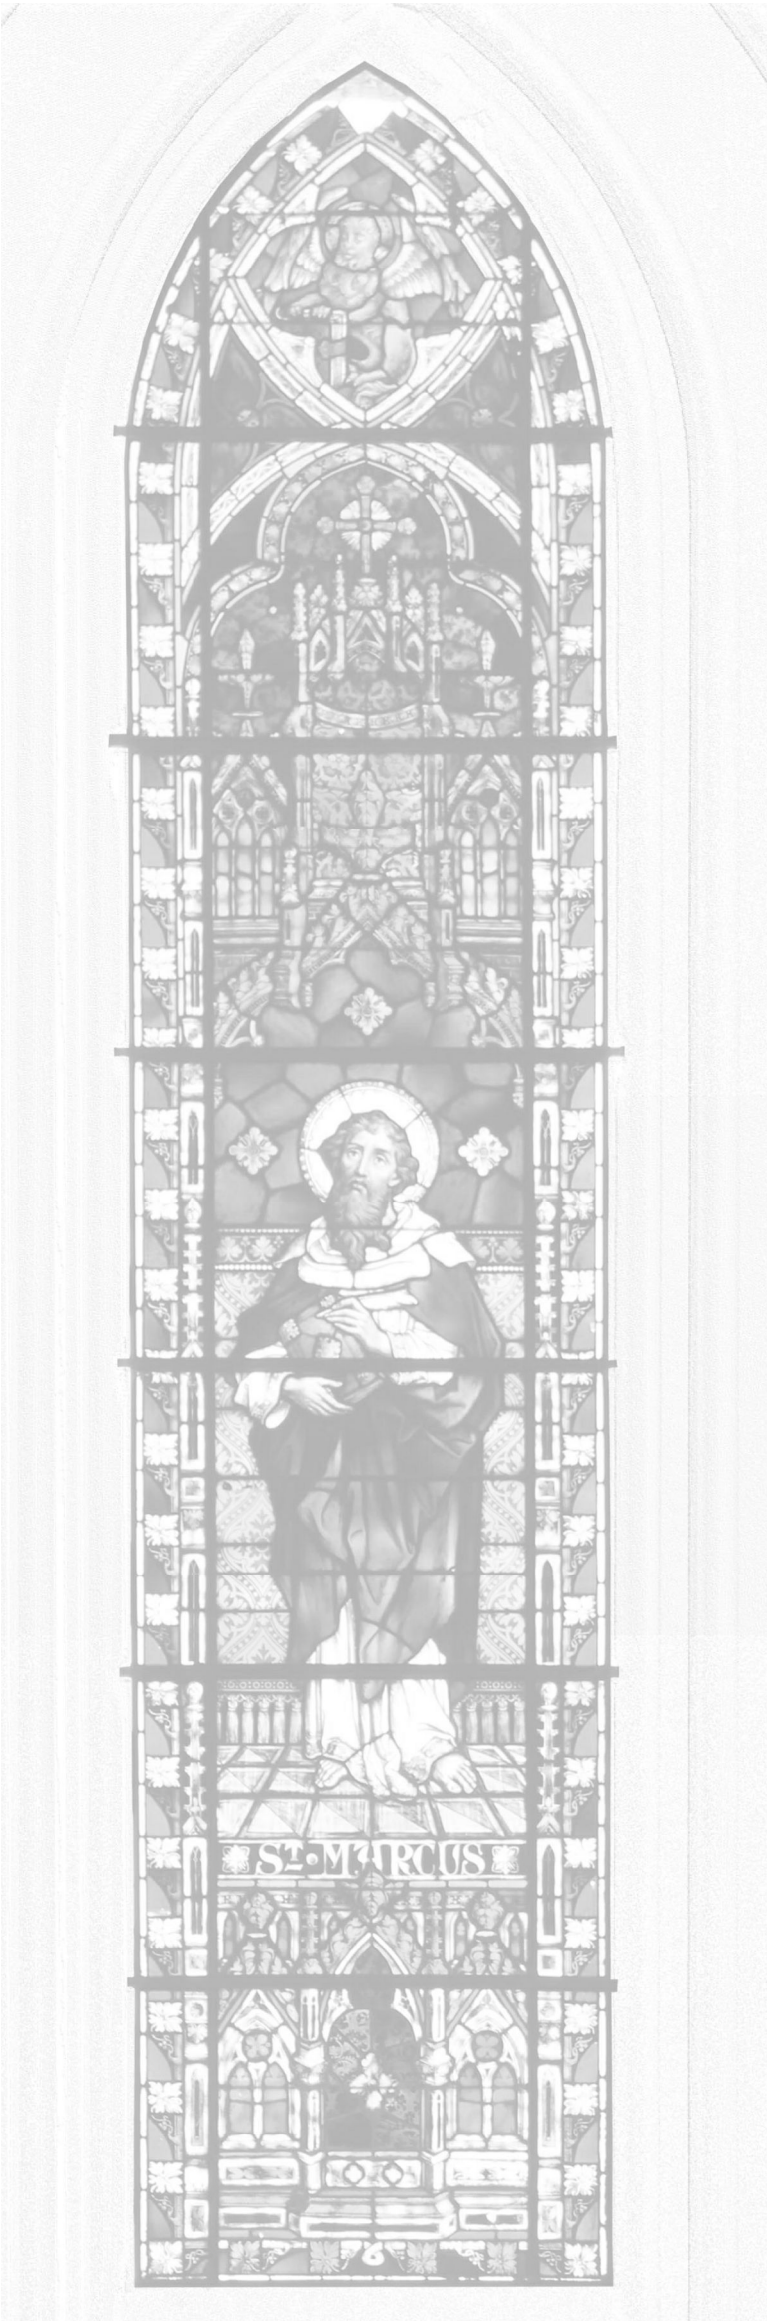

Levantamiento de Daños
Esc. 1/25

Ubicación					
			PROYECTO		
DIRECCIÓN DE ARQUITECTURA DIRECCIÓN REGIONAL METROPOLITANA			Arqto. Dino Bozzi F. TÁNDEM Limitada contacto@tandemlimitada.cl		
PROYECTO: REPARACIÓN PARCIAL BASÍLICA DEL SALVADOR STGO					
BASÍLICA DEL SALVADOR				ES	
Huérfanos 1796 - Santiago Región Metropolitana				Vi-19	
LEVANTAMIENTO VITRAL 19			1/25		
"San Marcos Evangelista"			Ago. 13		
TD			Escala		
TD	TD	LEV	DET	-	A
Emisor	Proyecto	Fase	Tipo	Zona	Índice
Dibuj: RM	Control: VI	Archivo de ref.: TD_1212_LEV_ES_Vi-15-25.dwg			