



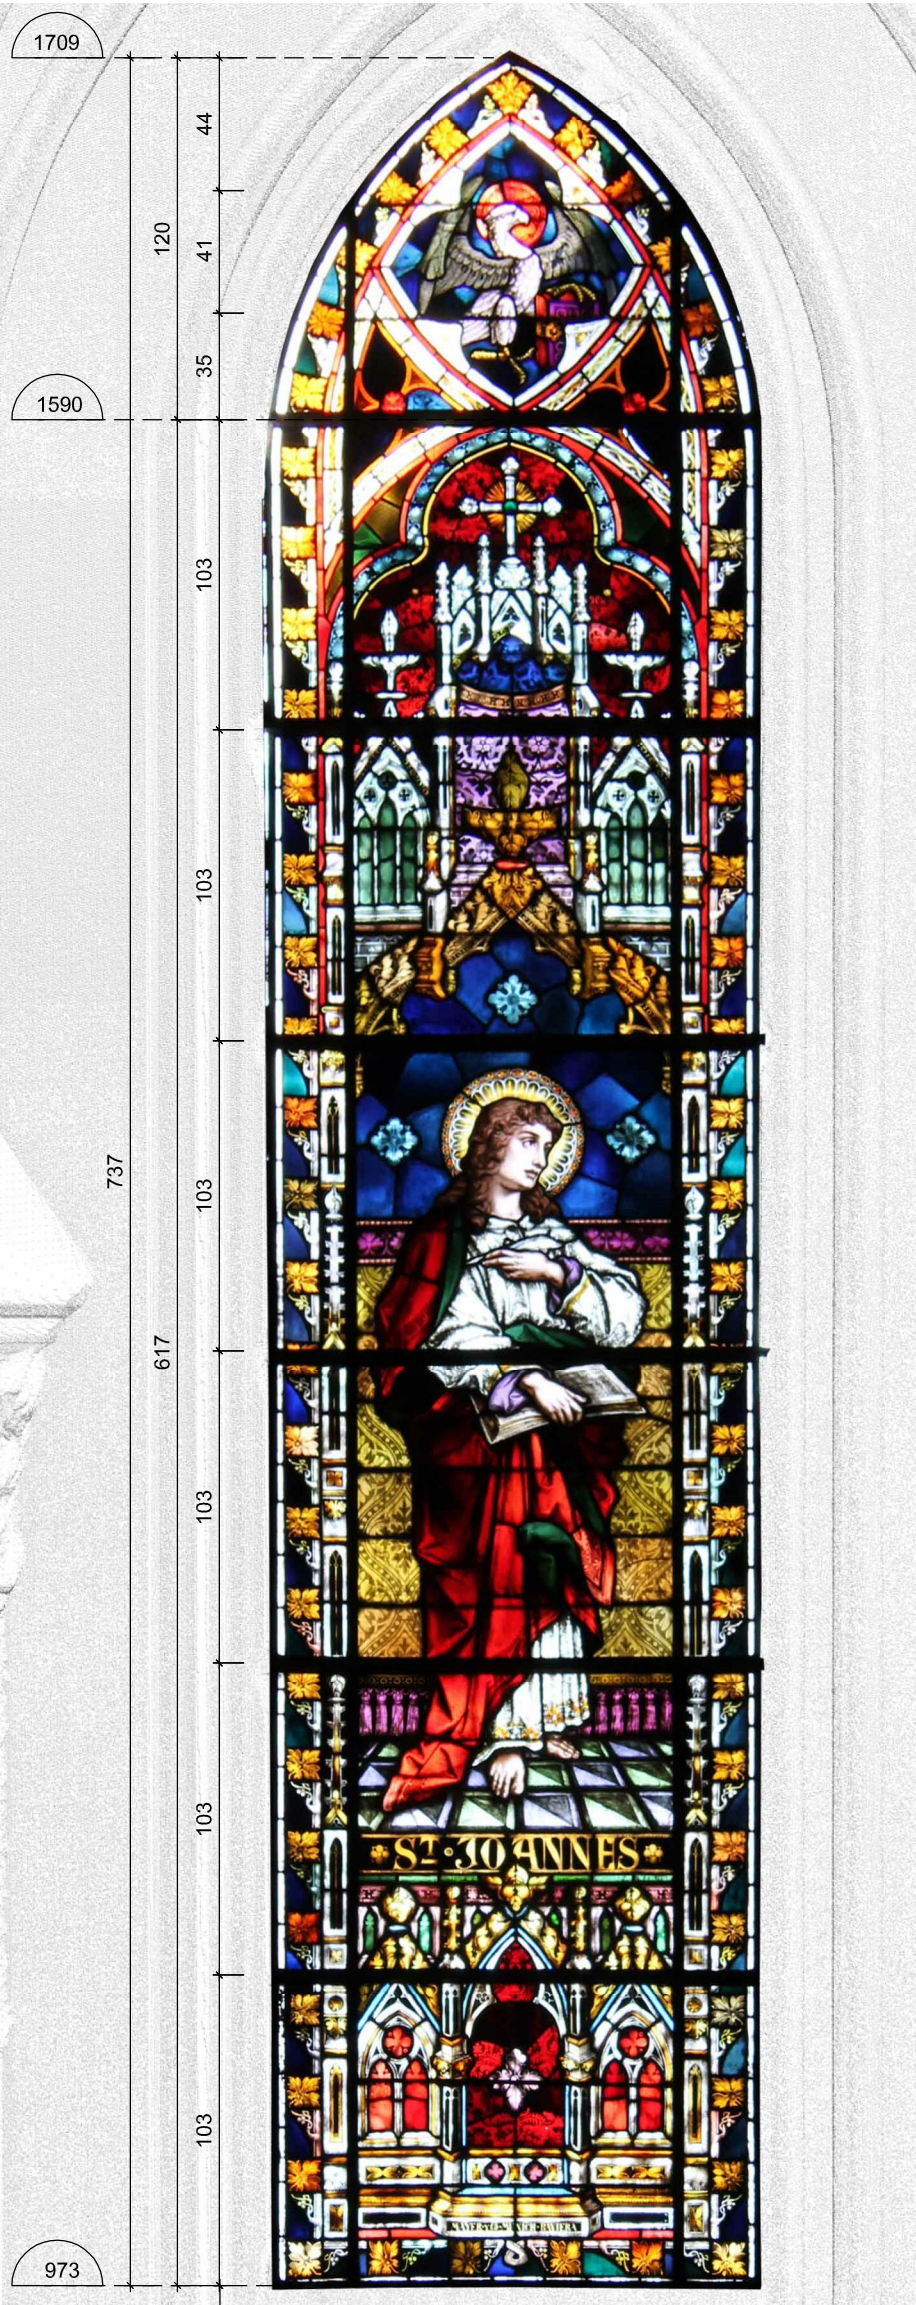

Elevación  
Esc. 1/25

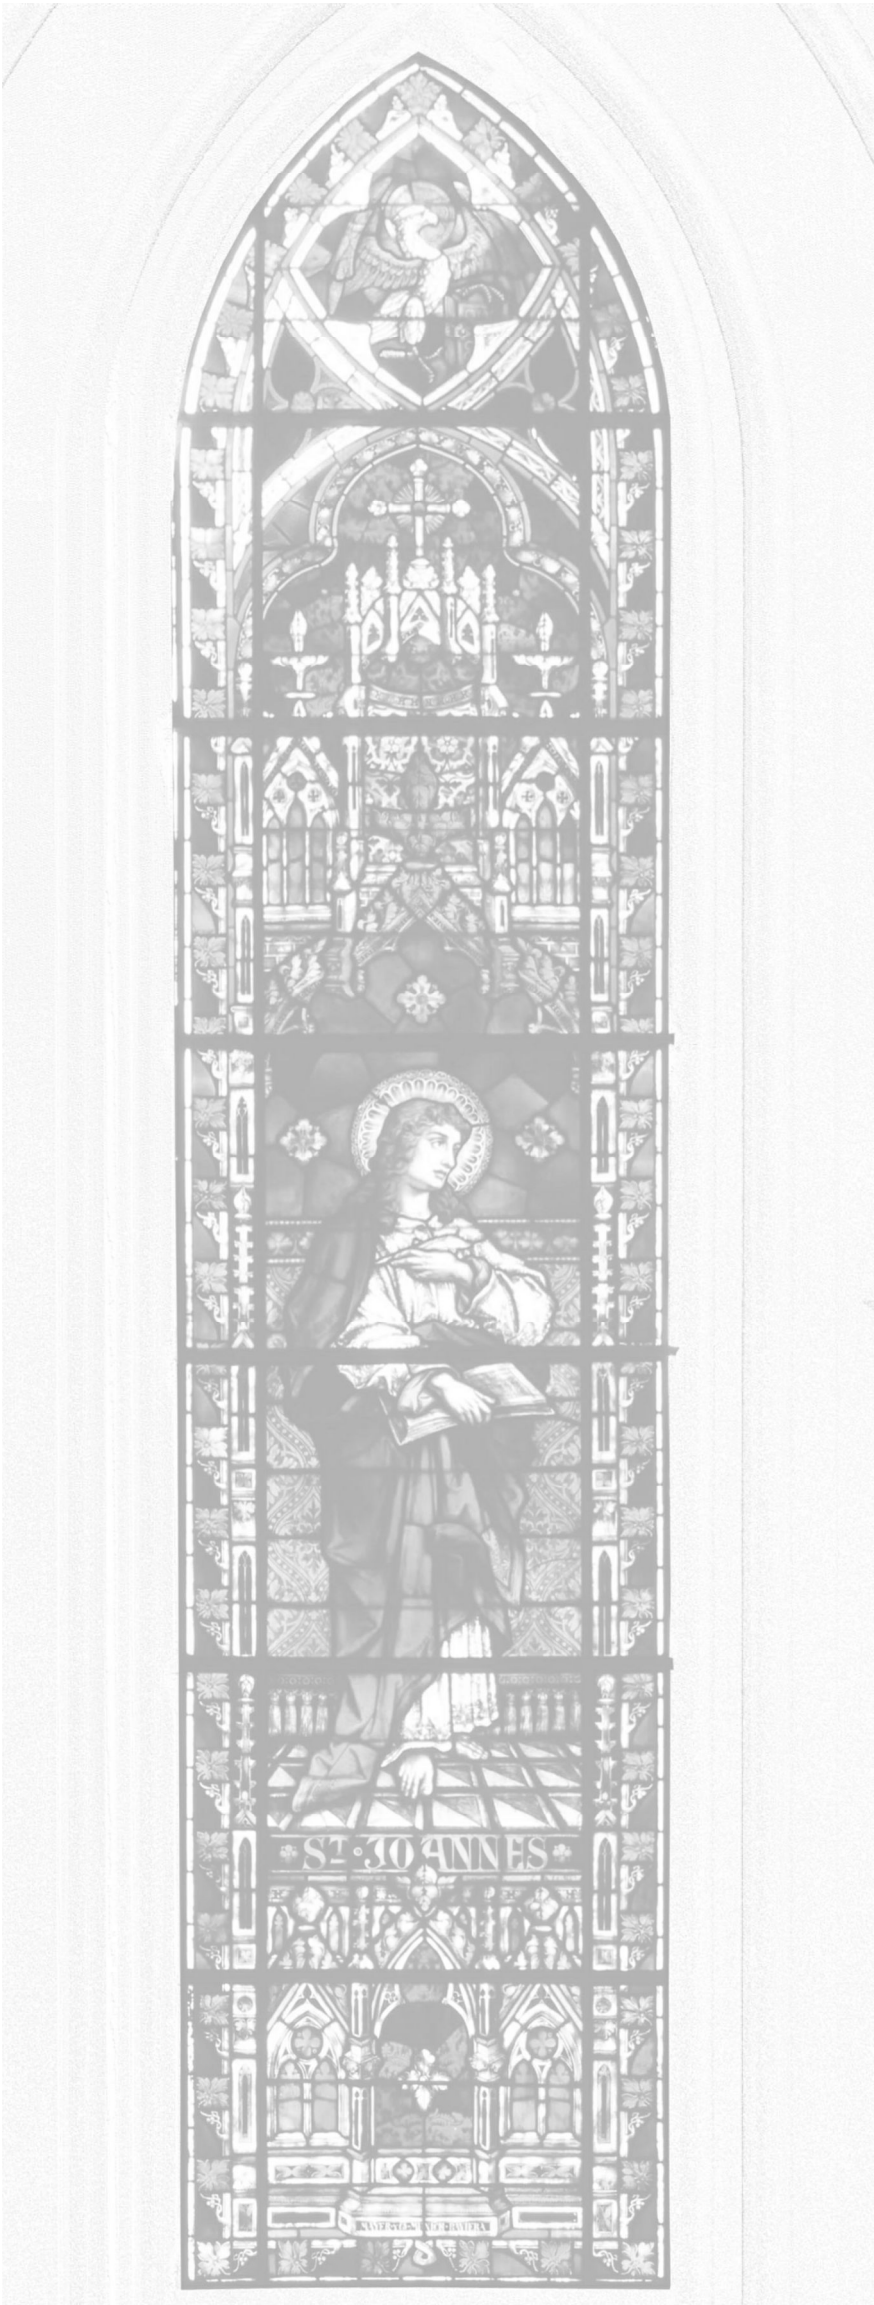

Levantamiento de Daños  
Esc. 1/25

|                                                               |             |                                               |                                                                       |        |        |         |
|---------------------------------------------------------------|-------------|-----------------------------------------------|-----------------------------------------------------------------------|--------|--------|---------|
| Ubicación                                                     |             |                                               |                                                                       |        |        |         |
|                                                               |             |                                               |                                                                       |        |        |         |
| DIRECCIÓN DE ARQUITECTURA<br>DIRECCIÓN REGIONAL METROPOLITANA |             |                                               | PROYECTO                                                              |        |        |         |
|                                                               |             |                                               | Arqto. Dino Bozzi F.<br>TÁNDEM Limitada<br>contacto@tandemlimitada.cl |        |        |         |
| PROYECTO: REPARACIÓN PARCIAL BASÍLICA DEL SALVADOR STGO       |             |                                               |                                                                       |        |        |         |
| BASÍLICA DEL SALVADOR                                         |             |                                               |                                                                       |        | ES     |         |
| Huérfanos 1796 - Santiago                                     |             |                                               |                                                                       |        |        |         |
| Región Metropolitana                                          |             |                                               |                                                                       |        |        |         |
| VI-22                                                         |             |                                               |                                                                       |        |        |         |
| LEVANTAMIENTO VITRAL 22                                       |             |                                               |                                                                       | 1/25   |        | Ago. 13 |
| "San Juan Evangelista"                                        |             |                                               |                                                                       | Escala | Fecha  |         |
| TD                                                            | TD          | LEV                                           | DET                                                                   | -      | A      |         |
| Emisor                                                        | Proyecto    | Fase                                          | Tipo                                                                  | Zona   | Índice |         |
| Dibuj: RM                                                     | Control: VI | Archivo de ref.: TD_1212_LEV_ES_VI-15-25-00w9 |                                                                       |        |        |         |