



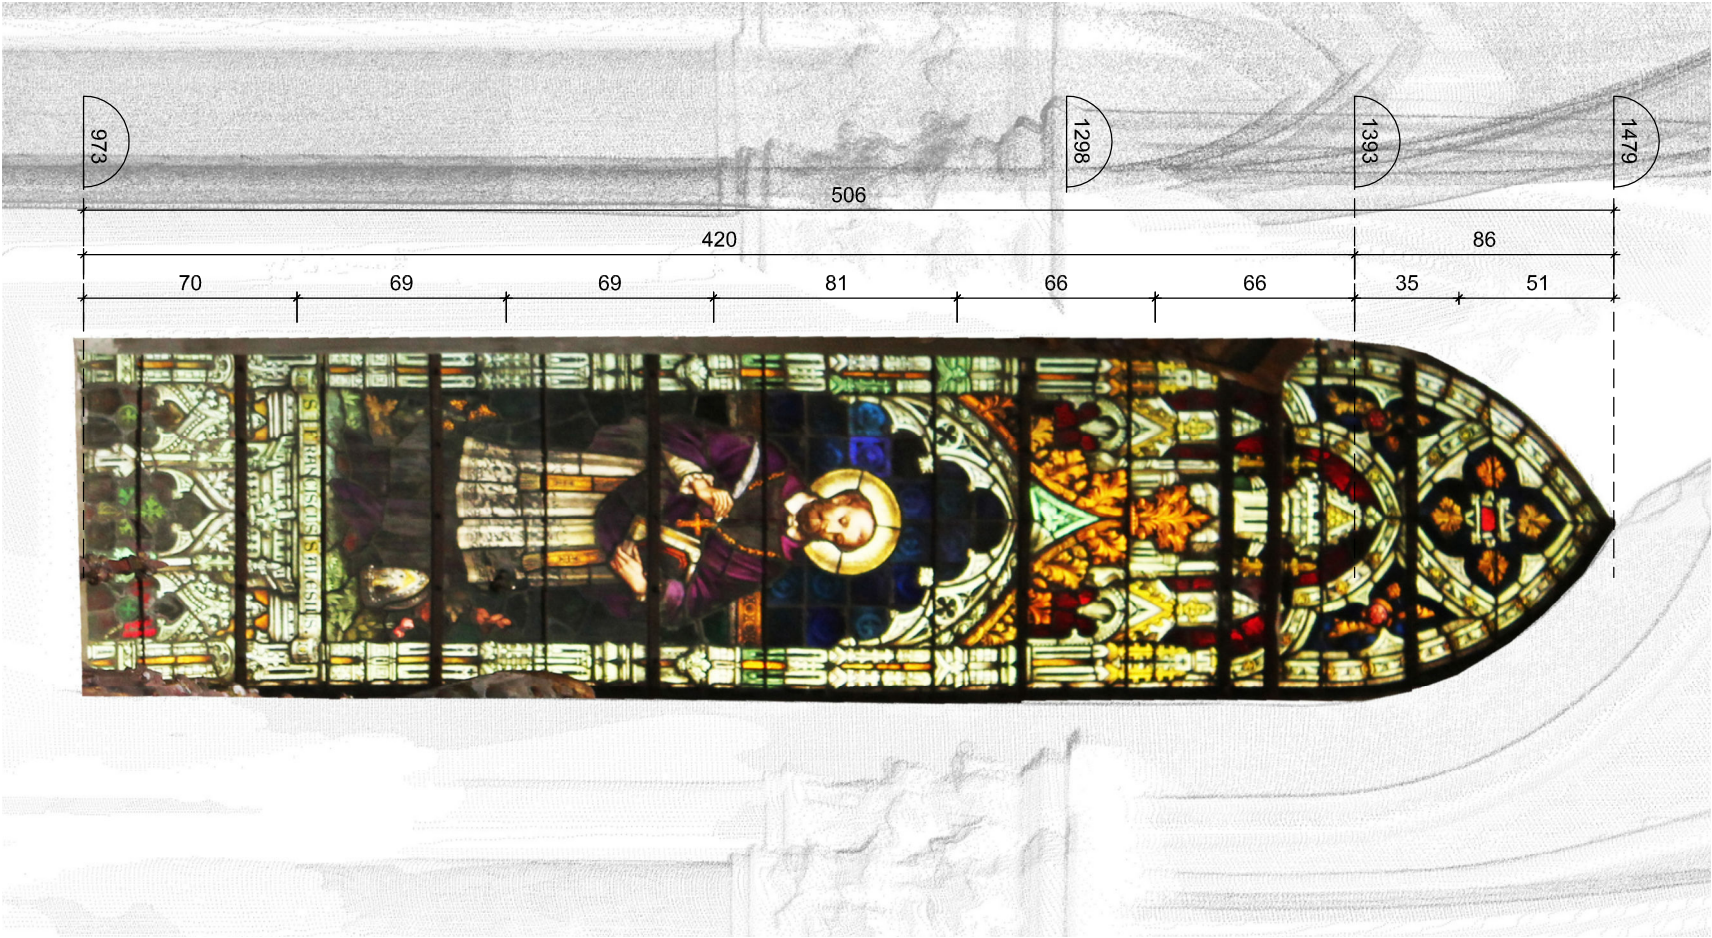

Elevación  
Esc. 1/25

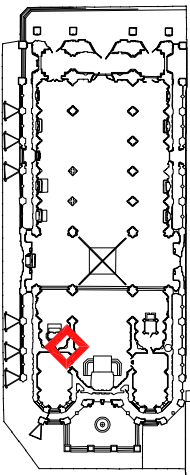

Levantamiento de Daños  
Esc. 1/25

|                                                                                     |          |      |                                                                       |         |        |
|-------------------------------------------------------------------------------------|----------|------|-----------------------------------------------------------------------|---------|--------|
| Ubicación                                                                           |          |      |                                                                       |         |        |
|  |          |      | PROYECTO                                                              |         |        |
|  |          |      | Arqto. Dino Bozzi F.<br>TÁNDEM Limitada<br>contacto@tandemlimitada.cl |         |        |
| DIRECCIÓN DE ARQUITECTURA<br>DIRECCIÓN REGIONAL METROPOLITANA                       |          |      |                                                                       |         |        |
| PROYECTO: REPARACIÓN PARCIAL BASÍLICA DEL<br>SALVADOR STGO                          |          |      |                                                                       |         |        |
| BASÍLICA DEL SALVADOR                                                               |          |      |                                                                       |         | ES     |
| Huérfanos 1796 - Santiago<br>Región Metropolitana                                   |          |      |                                                                       |         | Vi-23  |
| LEVANTAMIENTO VITRAL 23                                                             |          |      | 1/25                                                                  | Ago. 13 |        |
| "San Francisco de Sales"                                                            |          |      | Escala                                                                | Fecha   |        |
| TD                                                                                  | TD       | LEV  | DET                                                                   | -       | A      |
| Emisor                                                                              | Proyecto | Fase | Tipo                                                                  | Zona    | Índice |
| Dibuj: RM                                                                           |          |      | Control: VI                                                           |         |        |
| Archivo de ref.: TD_1212_LEV_ES_VI-15-25.dwg                                        |          |      |                                                                       |         |        |