
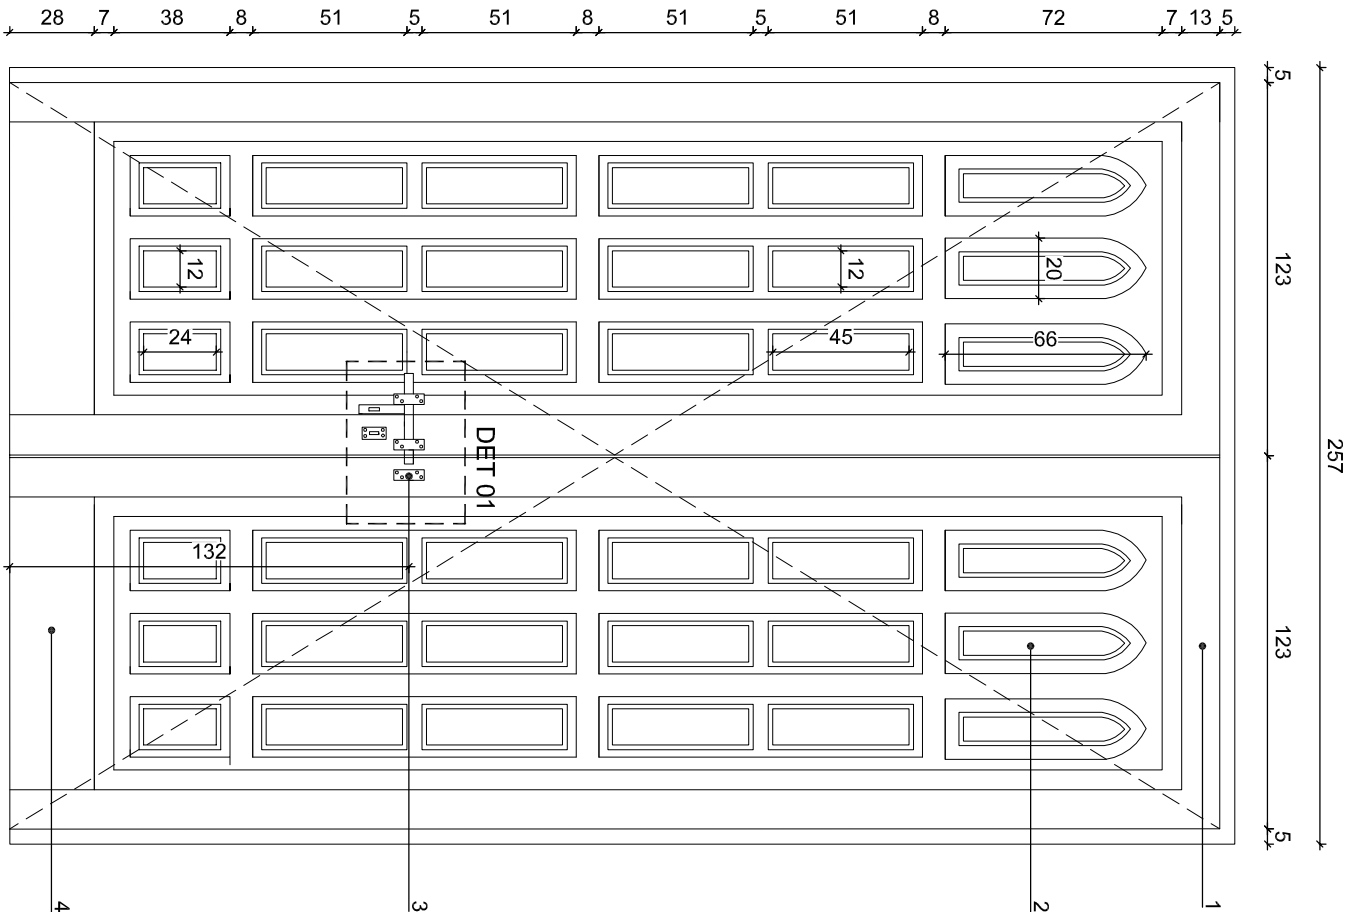
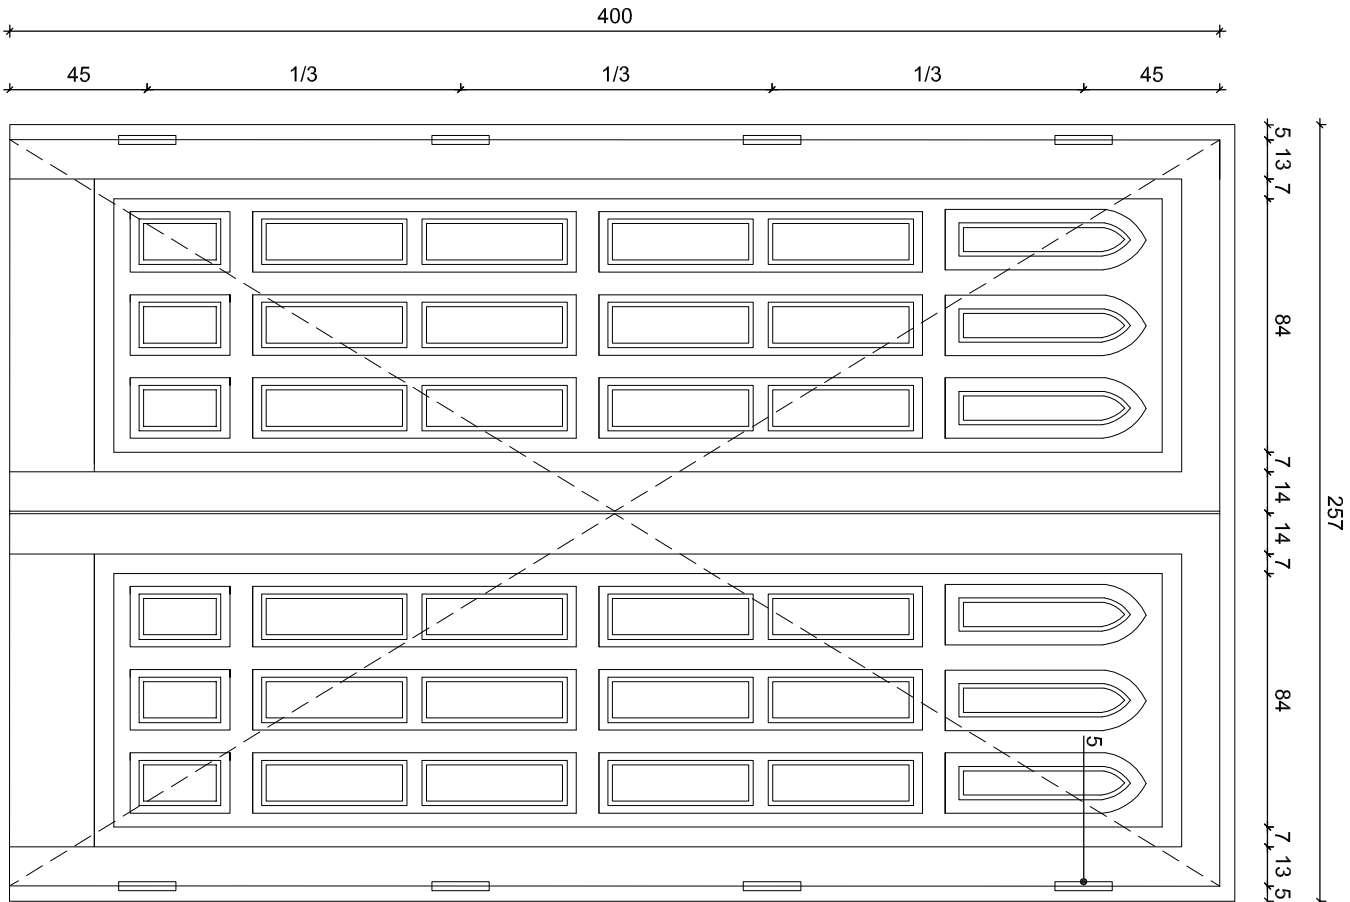


ELEVACIÓN EXTERIOR Esc. 1/25

ELEVACIÓN INTERIOR Esc. 1/25

CORTE Esc. 1/25

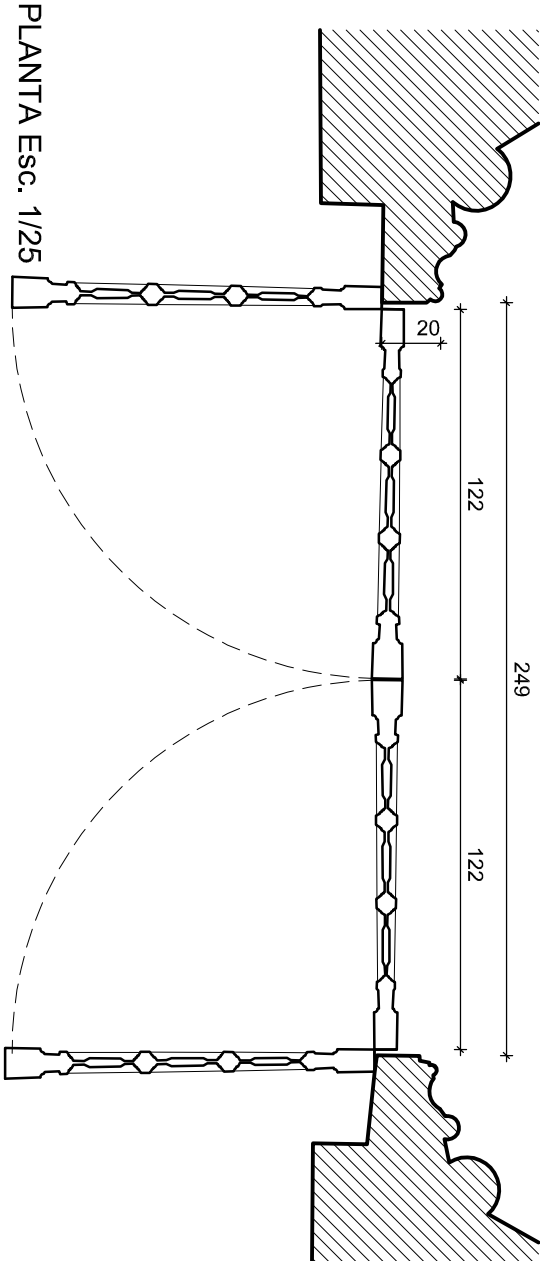


PLANTA Esc. 1/25

Nomenclatura

- 1.- Bastidor madera terminación pintura
- 2.- Tablero madera terminación pintura
- 3.- Cerrajería Fe Fundido
- 4.- Bisagras Fe Fundido
- 5.- Marco de madera. Ver detalle 05

Foto exterior

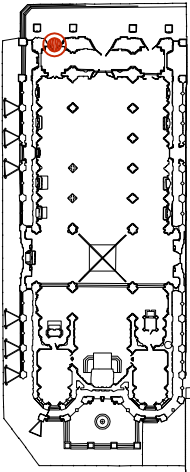

Ubicación



Arqto. Dino Bozzi F.
TÁNDEM Limitada
contacto@tandemlimitada.cl

PROYECTO

DIRECCIÓN DE ARQUITECTURA
DIRECCIÓN REGIONAL METROPOLITANA

PROYECTO: REPARACIÓN PARCIAL BASÍLICA DEL
SALVADOR STGO


BASÍLICA DEL SALVADOR
Huérfanos 1796 - Santiago
Región Metropolitana

ES
Pu-1a


LEVANTAMIENTO		1/25	Ago. 13
Puerta 01 - acceso poniente		Escala	Fecha
TD	TD	LEV	DET
Emisor	Proyecto	Fase	Tipo
Dibuj: FV		Control: VI	Archivo de ref.: TD_1212_LEV_ES_Pu-01-26_c.dwg

Nomenclatura


- 1.- Bastidor madera terminación pintura
- 2.- Tablero madera terminación pintura
- 3.- Cerrajería Fe Fundido
- 4.- Bisagras Fe Fundido
- 5.- Marco de madera. Ver detalle 05

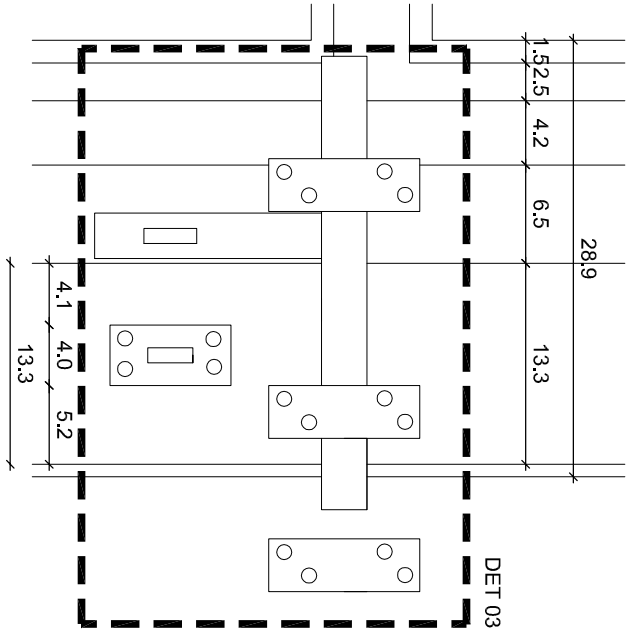


DETALLE 01
Esc. 1/5

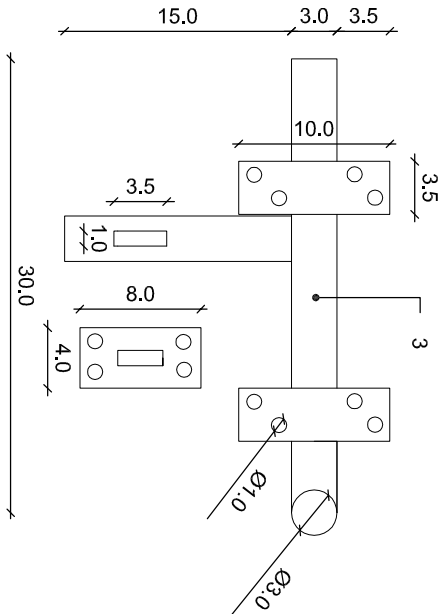


DETALLE 01b
Esc. 1/5

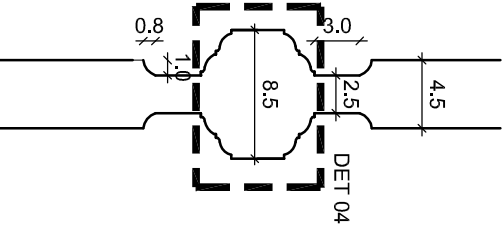


DETALLE 02
Esc. 1/5





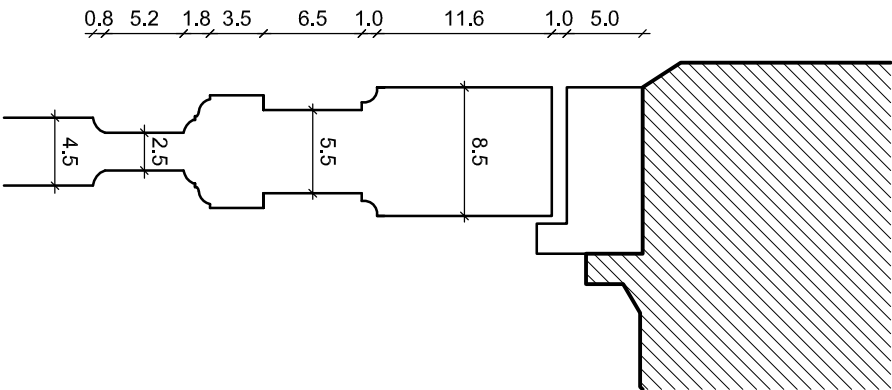


DETALLE 03
Esc. 1/5

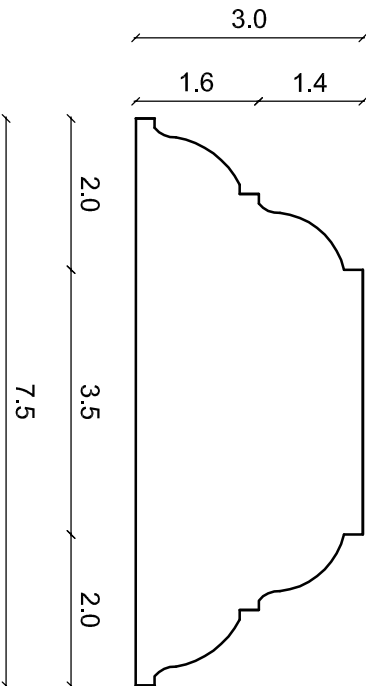

DETALLE 04
Esc. 1/1

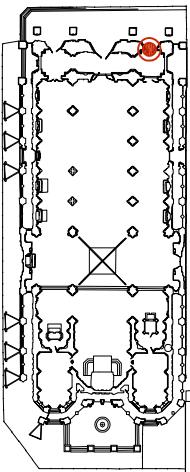Ubicación					
					
				PROYECTO	
DIRECCIÓN DE ARQUITECTURA DIRECCIÓN REGIONAL METROPOLITANA				Arqto. Dino Bozzi F. TÁNDEM Limitada contacto@tandemlimitada.cl	
PROYECTO: REPARACIÓN PARCIAL BASÍLICA DEL SALVADOR STGO					
BASÍLICA DEL SALVADOR				ES	
Huérfanos 1796 - Santiago Región Metropolitana				Pu-1a	
LEVANTAMIENTO				1/25	Ago. 13
Puerta 01				Escala	Fecha
TD	TD	LEV	DET	-	A
Emisor	Proyecto	Fase	Tipo	Zona	Índice
Dibujó: FV Control : VI Archivo de ref.: TD_1212_LEV_ES_Pu-01-26_c.dwg					

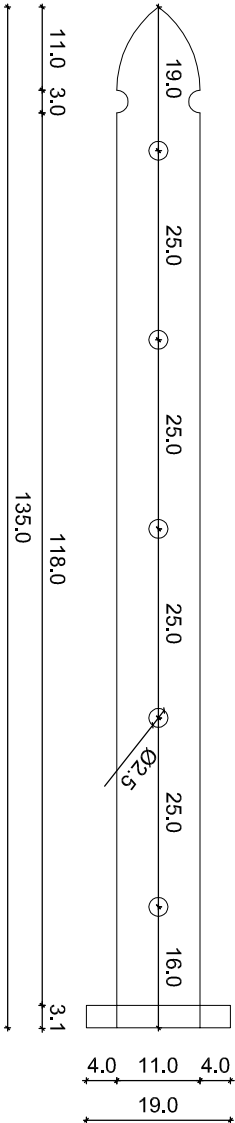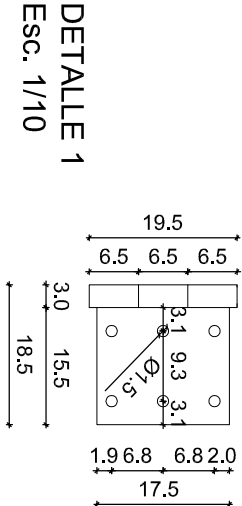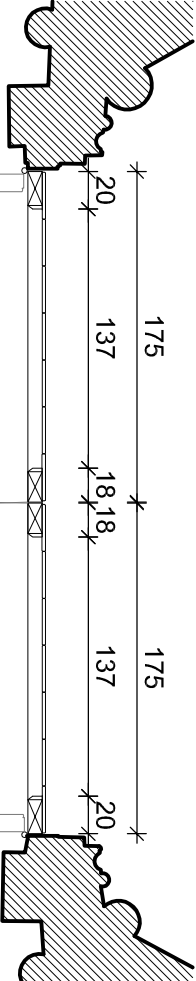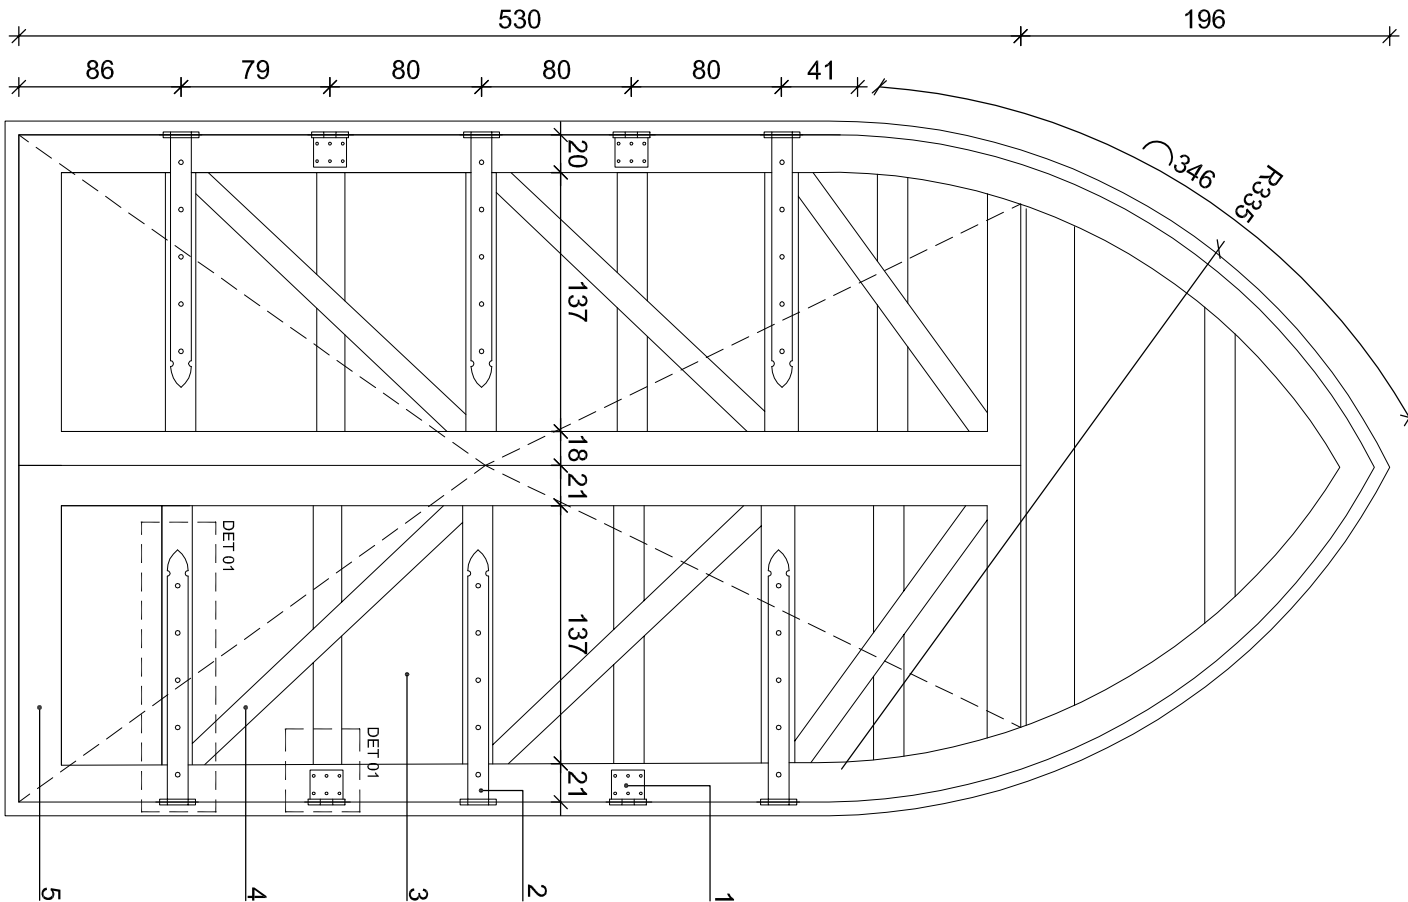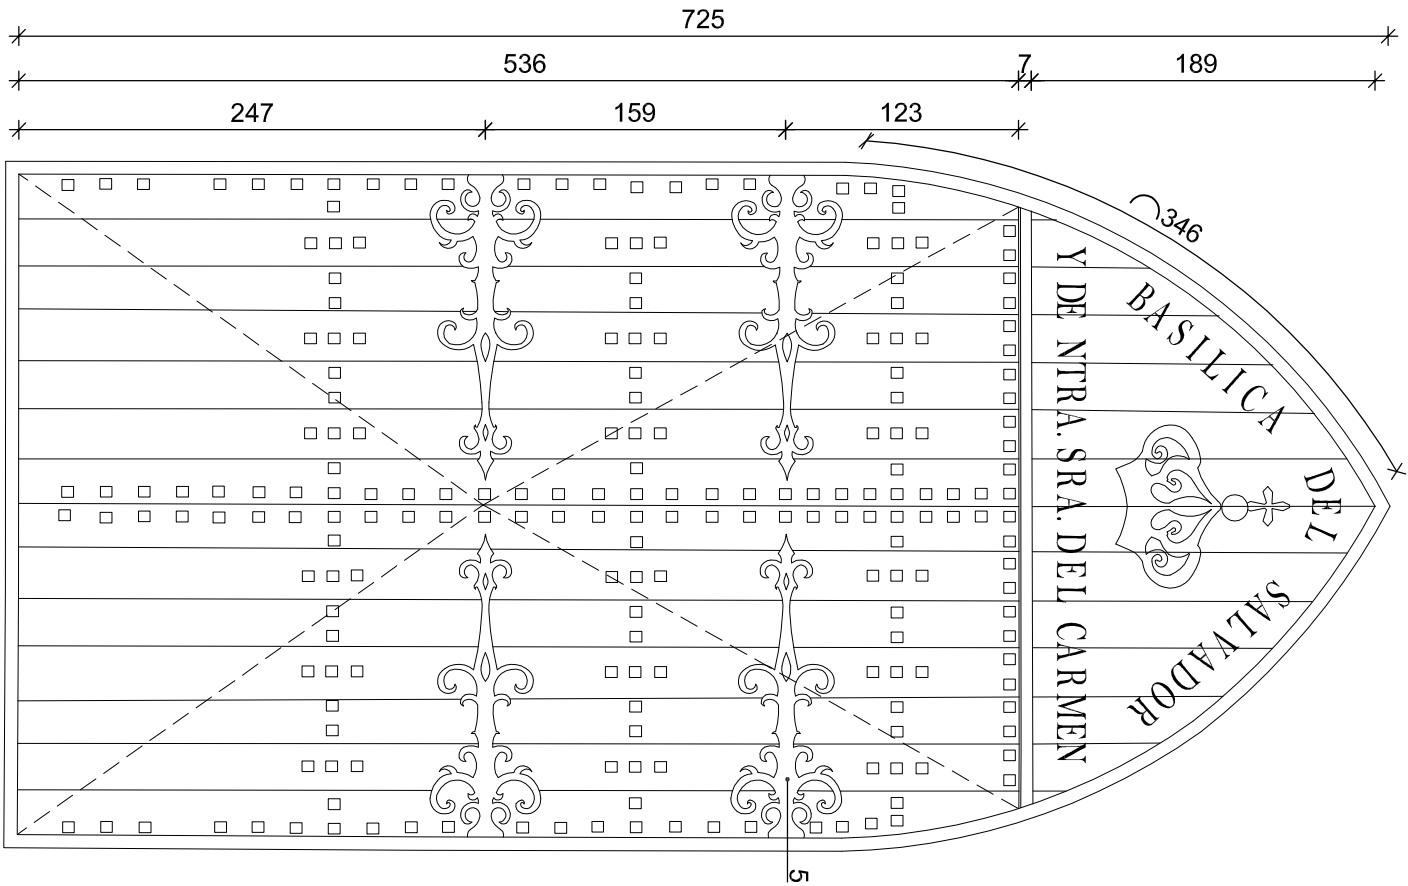

Nomenclatura

- 1.- Bisagra Fe fundido
- 2.- Herrajería Fe fundido
- 3.- Tablero de madera
- 4.- Arriostramiento de madera
- 5.- Bastidor de madera



Exterior



Interior


Ubicación					
PROYECTO					
DIRECCIÓN DE ARQUITECTURA		Arqto. Dino Bozzi F.			
DIRECCIÓN REGIONAL METROPOLITANA		TÁNDEM Limitada			
PROYECTO: REPARACIÓN PARCIAL BASÍLICA DEL SALVADOR STGO		contacto@tandemlimitada.cl			
LEVANTAMIENTO		1/25		Ago. 13	
Puerta 02		Escala		Fecha	
TD	TD	LEV	DET	-	A
Emisor	Proyecto	Fase	Tipo	Zona	Índice
Dibuj: FV		Control: VI		Archivo de ref.: TD_1212_LEV_ES_Pu-01-26_c04mg	

Leyenda

- 1.- tablero puerta
- 2.- bisagra
- 3.- marco
- 4.- cerrojo
- 5.- dintel




Fotografía

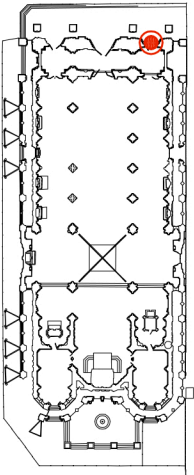

Ubicación


DIRECCIÓN DE ARQUITECTURA DIRECCIÓN REGIONAL METROPOLITANA		PROYECTO	
PROYECTO: REPARACIÓN PARCIAL BASÍLICA DEL SALVADOR STGO		Arqto. Dino Bozzi F. TÁNDEM Limitada contacto@tandemlimitada.cl	
BASÍLICA DEL SALVADOR		ES	
Huérfanos 1796 - Santiago Región Metropolitana		Pu-3a	
LEVANTAMIENTO		1/25	Ago. 13
Puerta 03		Escala	Fecha
TD	TD	LEV	DET
1305	1305	DET	-
Emisor	Proyecto	Fase	Tipo
DS	VI	Archivo de ref.	Índice
Dibujo: DS		Control : VI	
Archivo de ref.		TD_1212_LEV_ES_Pu-01-26_c.dwg	

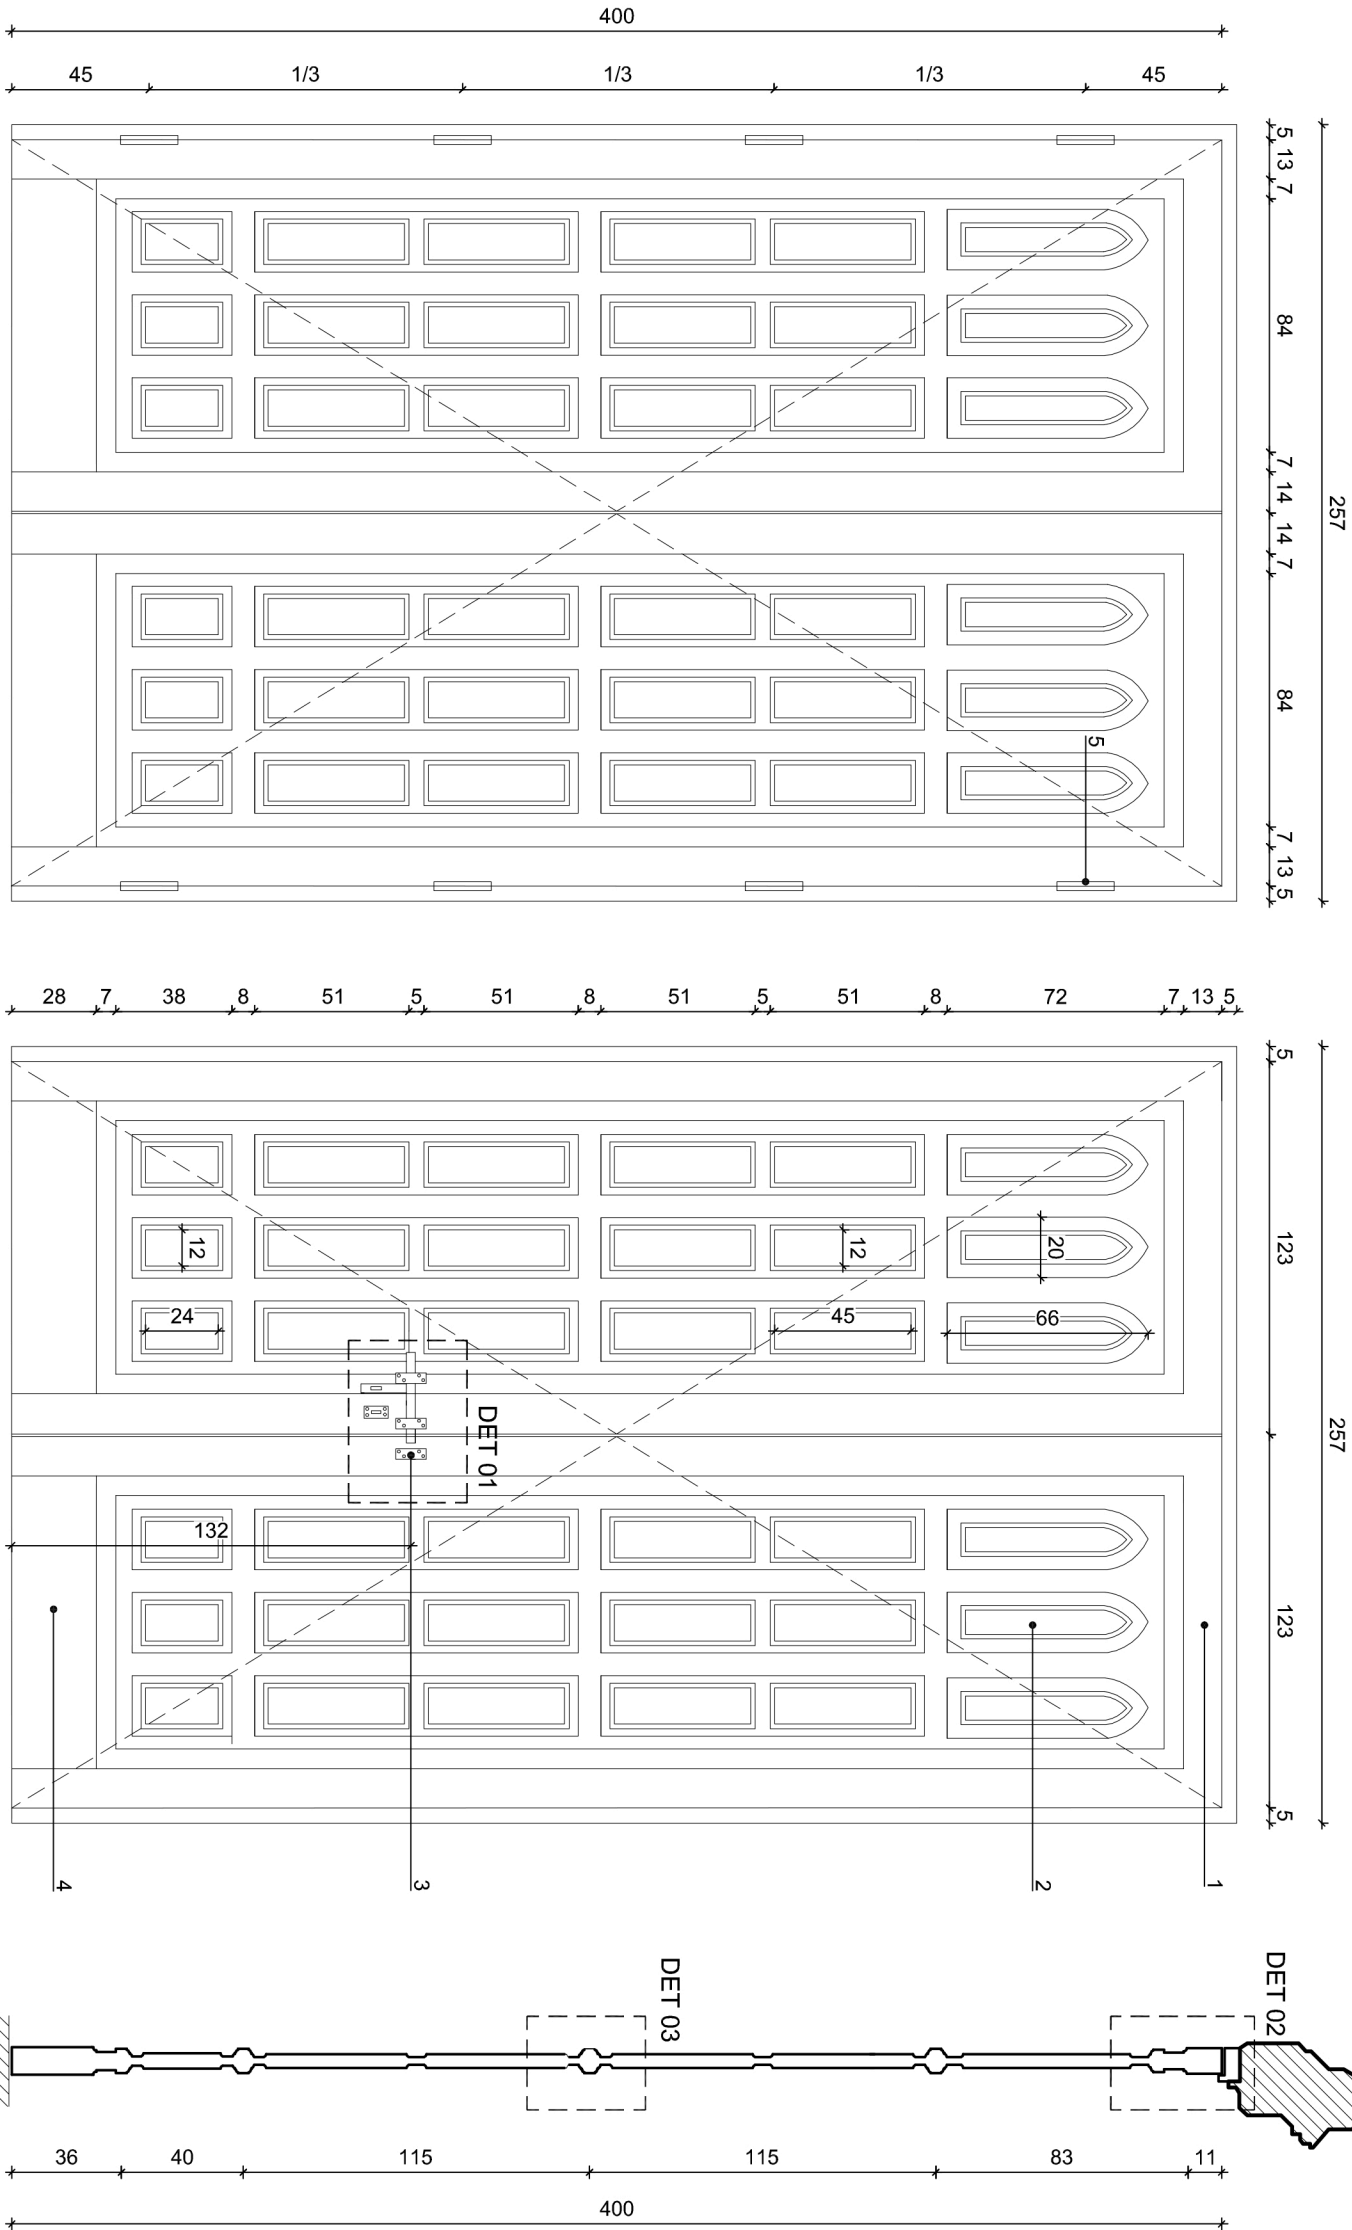

ELEVACIÓN EXTERIOR Esc. 1/25


ELEVACIÓN INTERIOR Esc. 1/25

CORTE Esc. 1/25

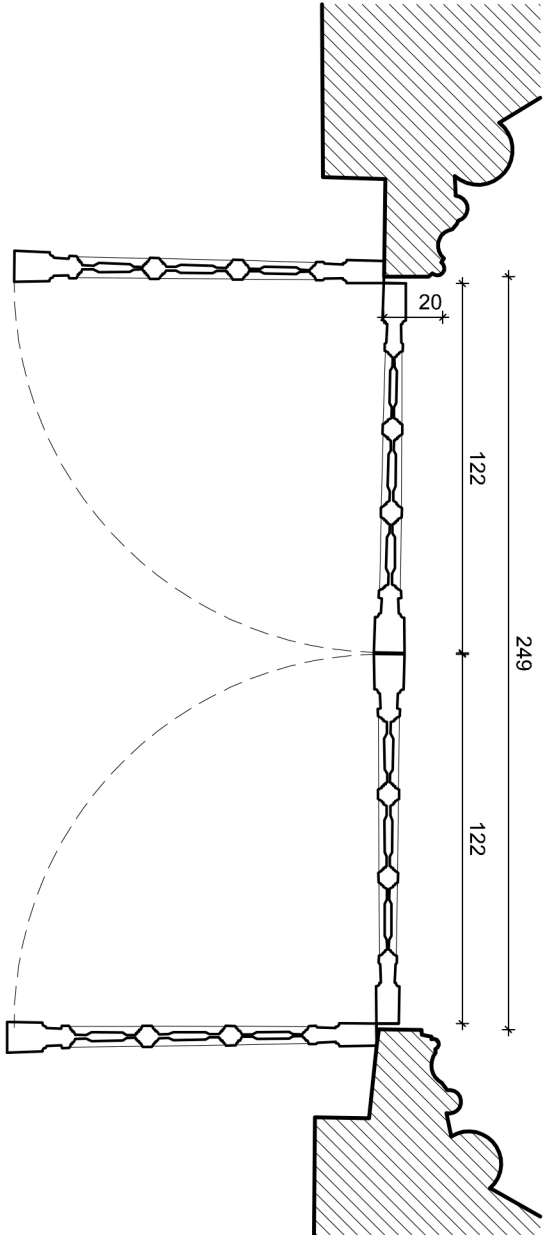


Nomenclatura


- 1.- Bastidor madera terminación pintura
- 2.- Tablero madera terminación pintura
- 3.- Cerrajería Fe Fundido
- 4.- Bisagras Fe Fundido
- 5.- Marco de madera. Ver detalle 05

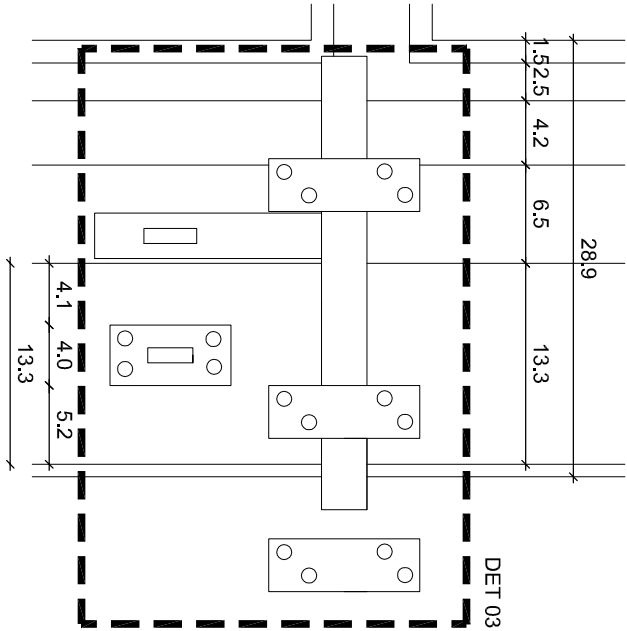


DETALLE 01
Esc. 1/5

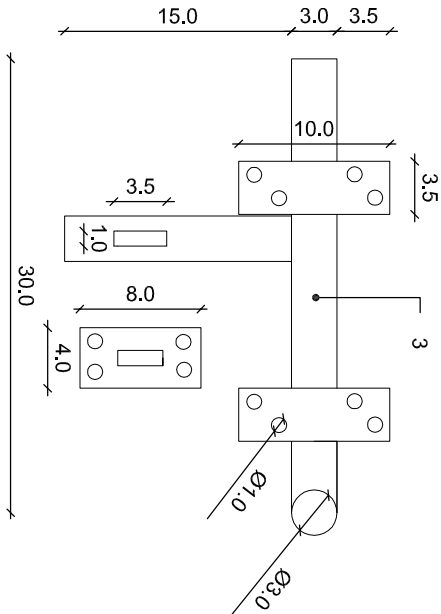


DETALLE 01b
Esc. 1/5

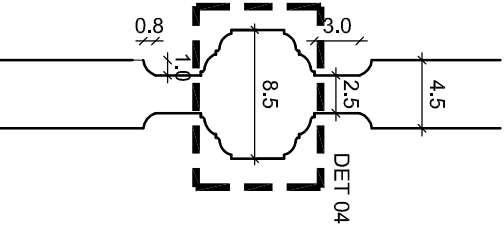


DETALLE 02
Esc. 1/5

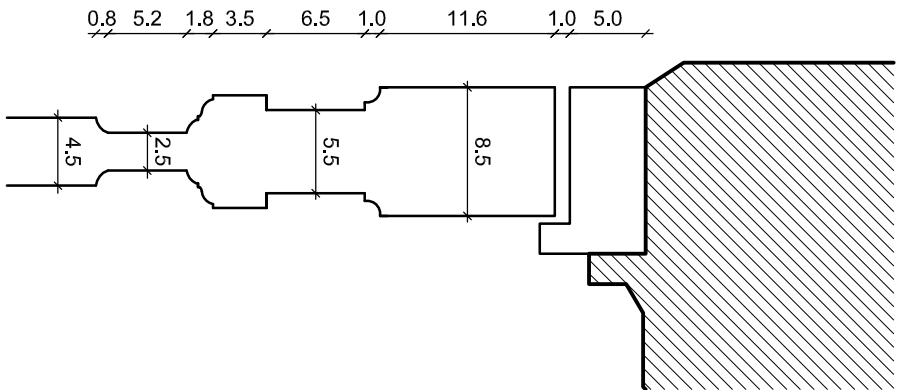

DETALLE 03
Esc. 1/5

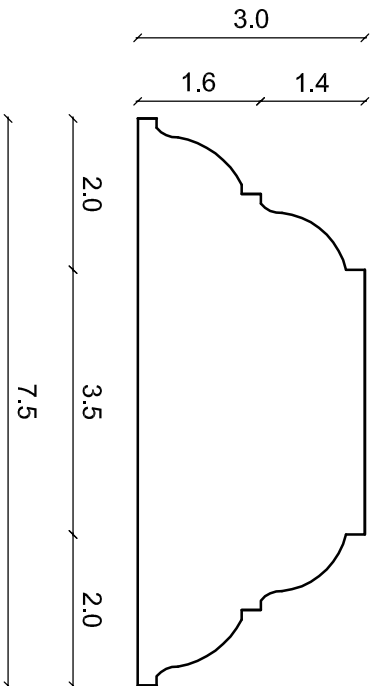

DETALLE 04
Esc. 1/1

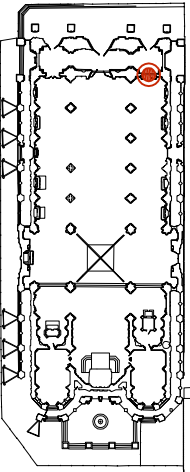Ubicación					
DIRECCIÓN DE ARQUITECTURA DIRECCIÓN REGIONAL METROPOLITANA		PROYECTO			
PROYECTO: REPARACIÓN PARCIAL BASÍLICA DEL SALVADOR STGO					
BASÍLICA DEL SALVADOR		ES			
Huérfanos 1796 - Santiago Región Metropolitana		Pu-3b			
LEVANTAMIENTO Puerta 03		1/25	Ago. 13		
TD		TD	LEV	DET	-
Emisor		Proyecto	Fase	Tipo	Zona
Dibuj: DS		Control: VI	Archivo de ref.: TD_1212_LEV_ES_Pu-01-26_c.dwg		

PUERTA 04:
Correspondiente a la puerta ubicada en la entrada, después del Nártex, en nave Este de la iglesia.

Puerta de madera de 352cm de ancho por 412 cm de altura con dos hojas abatibles hacia el exterior.



Fotografía

Ubicación

PROYECTO

Arqto. Dino Bozzi F.
TÁNDEM Limitada
contacto@tandemlimitada.cl

DIRECCIÓN DE ARQUITECTURA
DIRECCIÓN REGIONAL METROPOLITANA



PROYECTO: REPARACIÓN PARCIAL BASÍLICA DEL SALVADOR STGO

BASÍLICA DEL SALVADOR




Huérfanos 1796 - Santiago
Región Metropolitana

Pu-4a

LEVANTAMIENTO				1/40	Ago. 13
Puerta 04 - nártex poniente				Escala	Fecha
TD	TD	LEV	DET	-	A
Emisor	Proyecto	Fase	Tipo	Zona	Índice
Dibuj: DS	Control: VI		Archivo de ref.: TD_1212_LEV_ES_Pu-01-26_c.dwg		

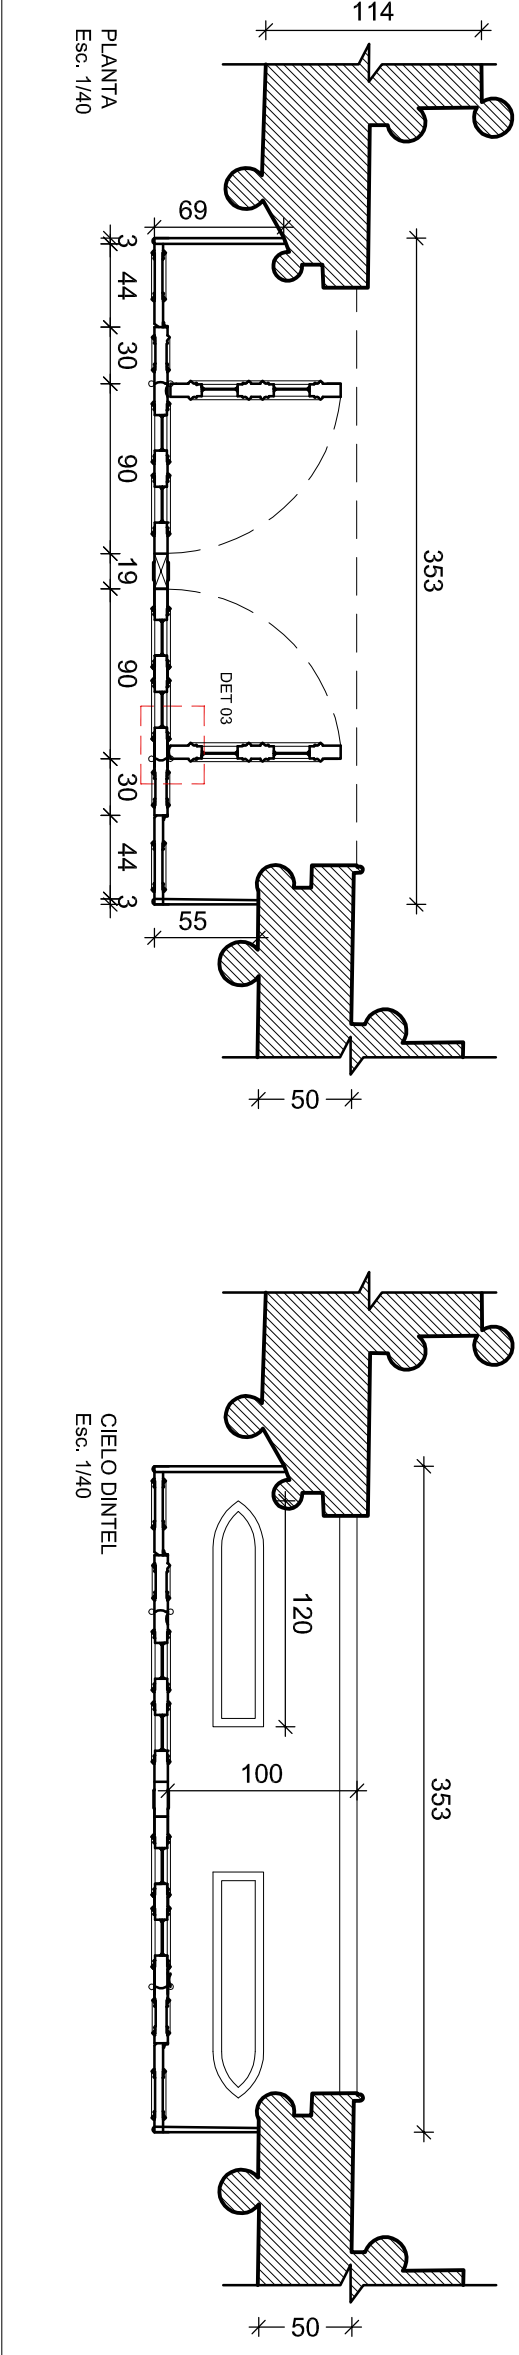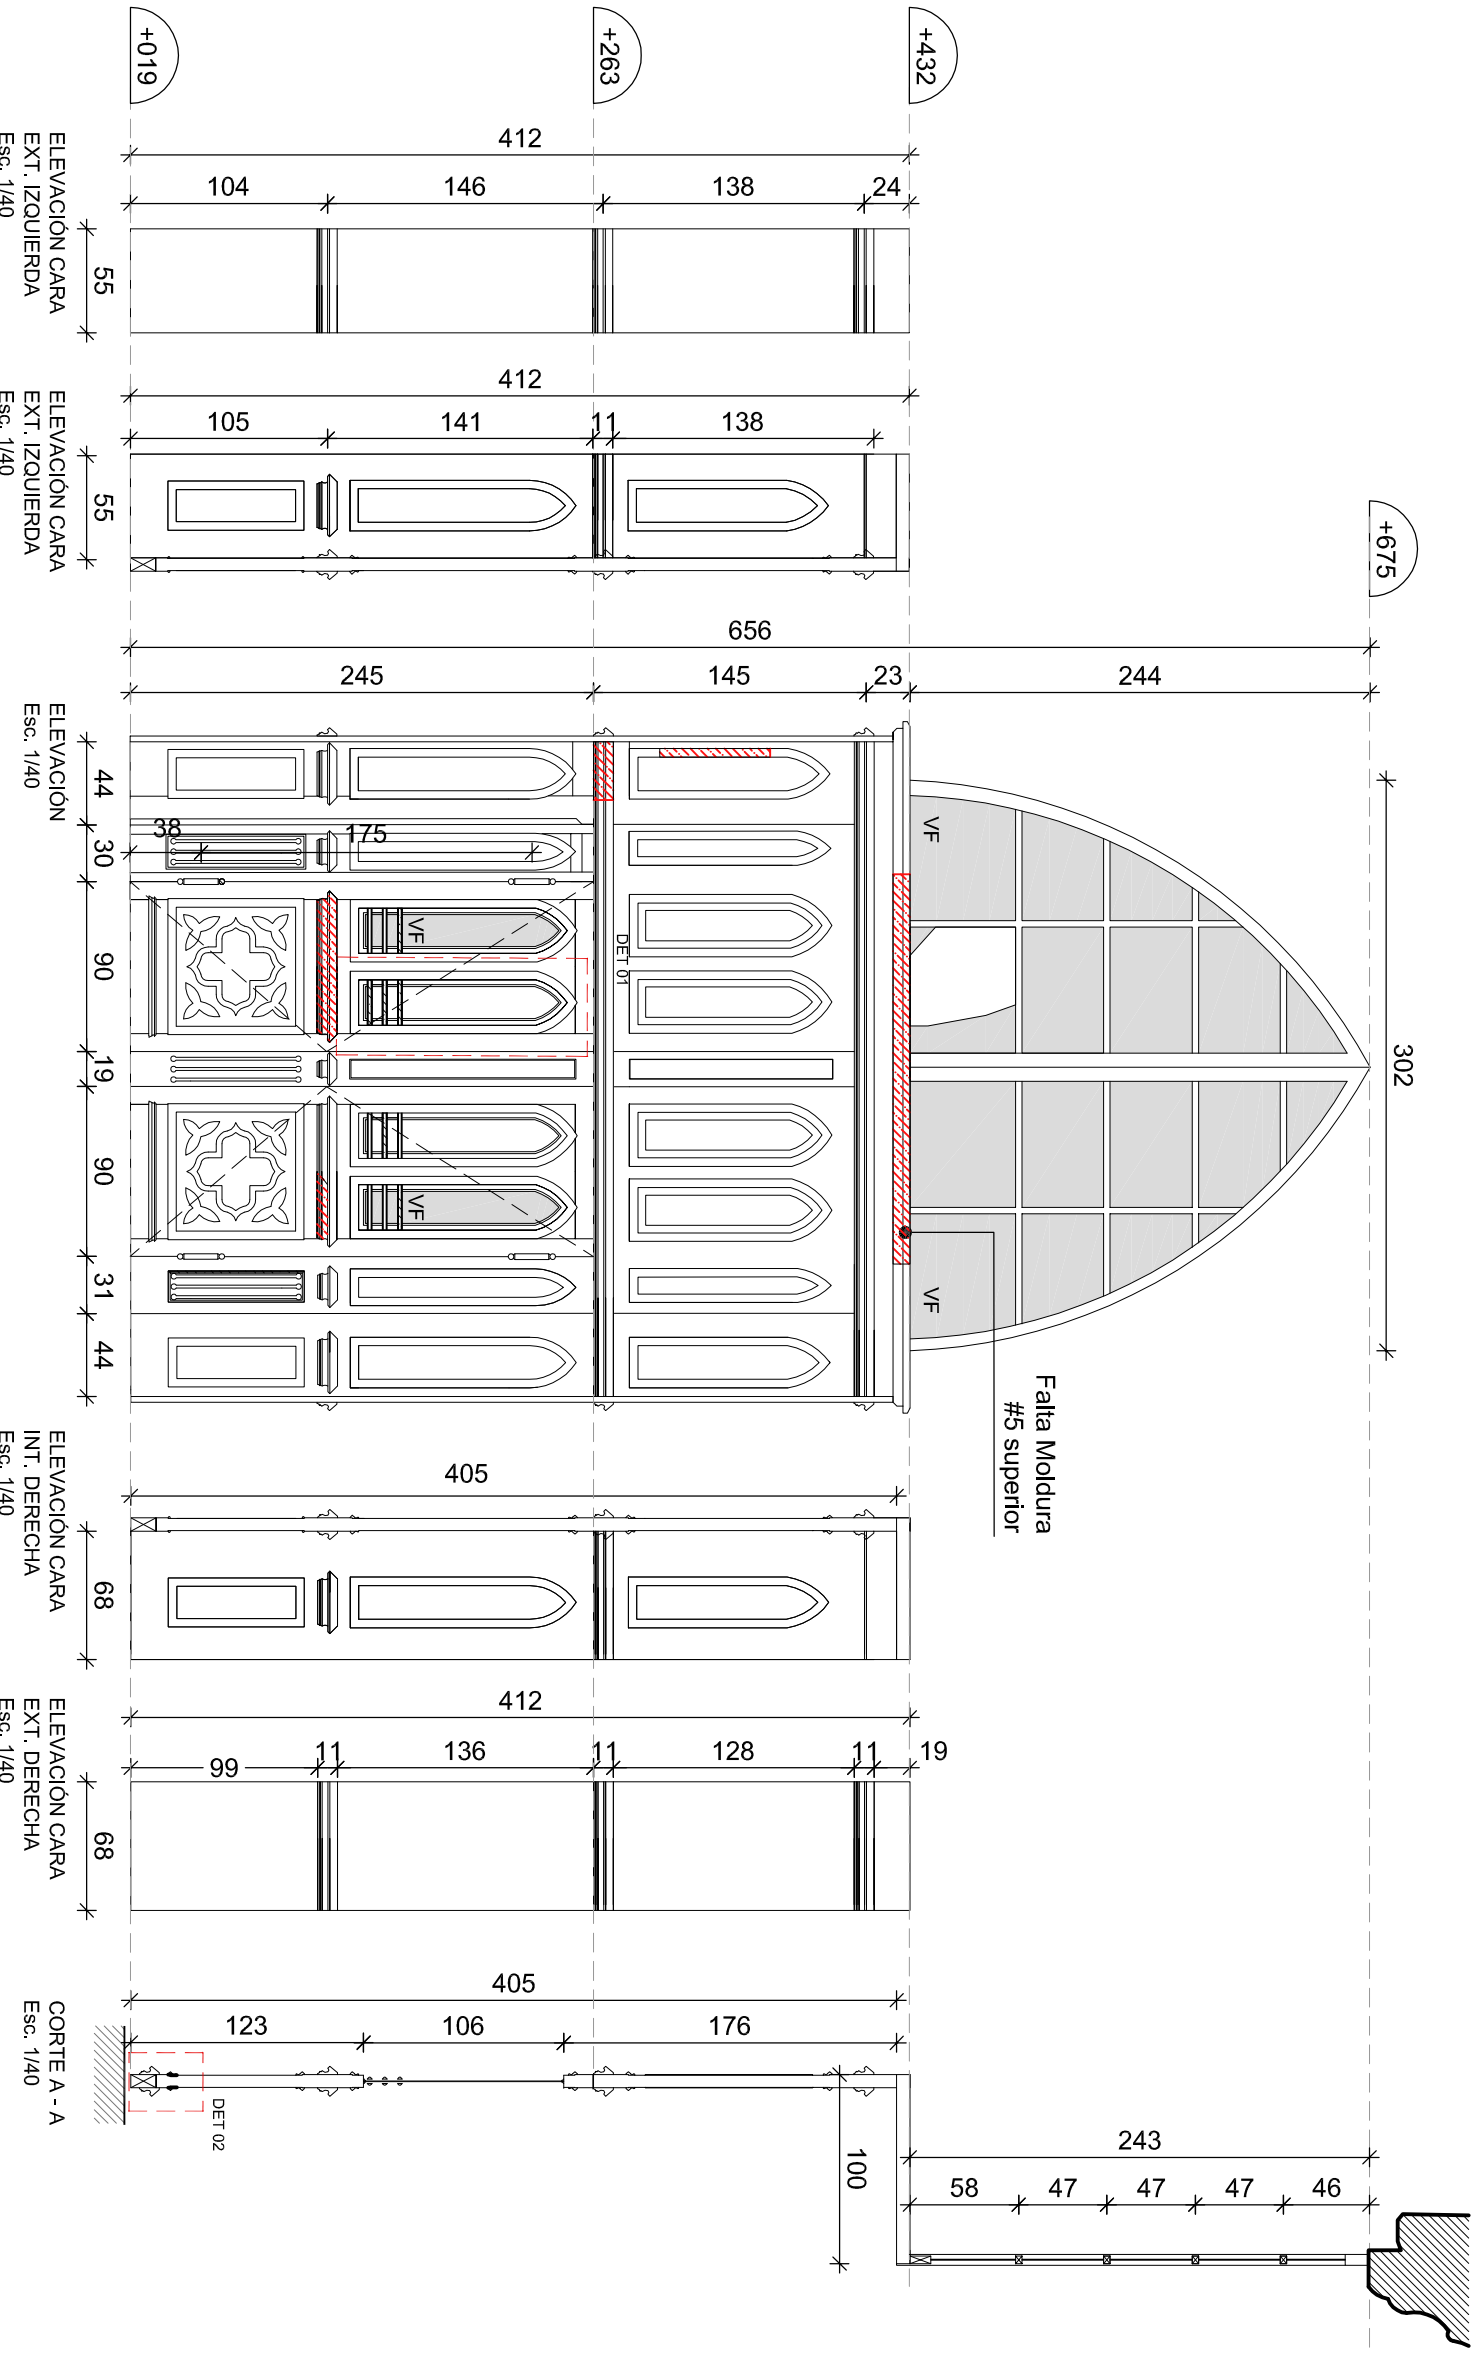



LEVANTAMIENTO				1/40	Ago. 13
Puerta 04 - nártex poniente				Escala	Fecha
TD	TD	LEV	DET	-	A
Emisor	Proyecto	Fase	Tipo	Zona	Índice
Dibuj: DS	Control: VI		Archivo de ref.: TD_1212_LEV_ES_Pu-01-26_c.dwg		

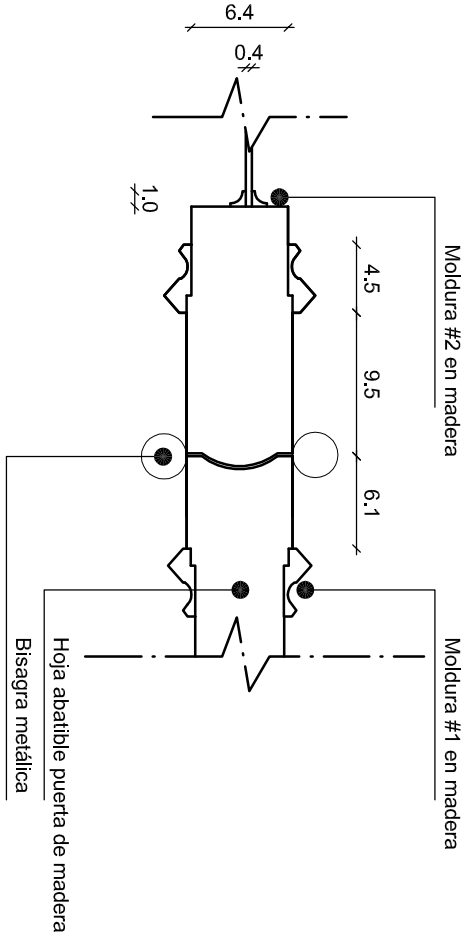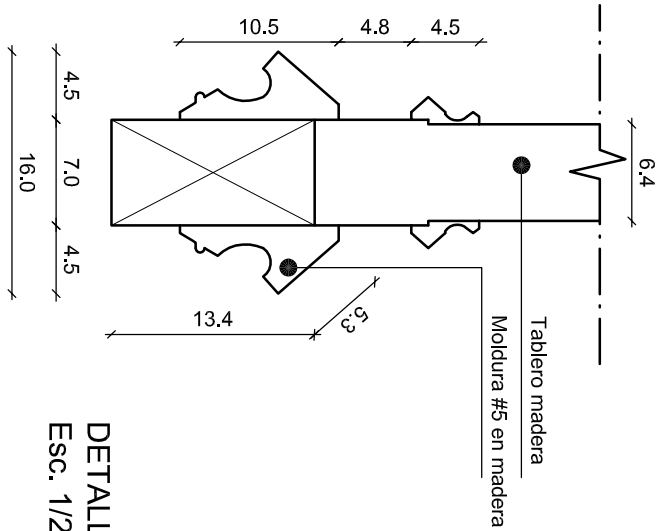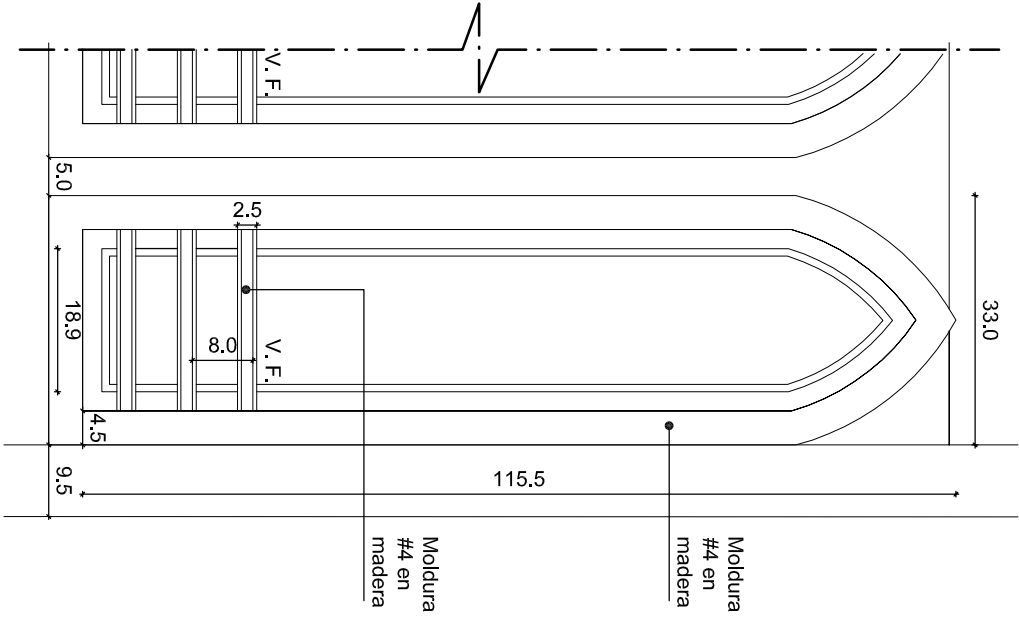

DETALLE 01
Esc. 1/2


DETALLE 02
Esc. 1/2

DETALLE 03
Esc. 1/2

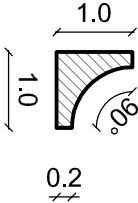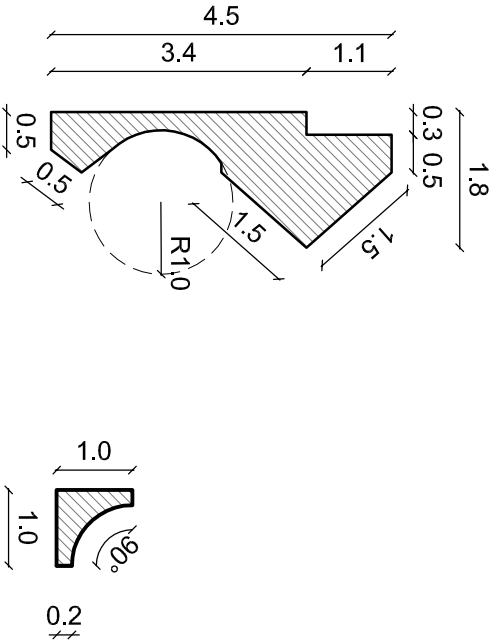


DETALLE MOLDURA #1
Esc. 1/1

DETALLE MOLDURA #2
Esc. 1/1

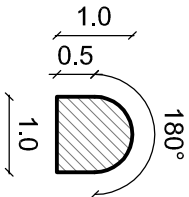




DETALLE MOLDURA #3
Esc. 1/1

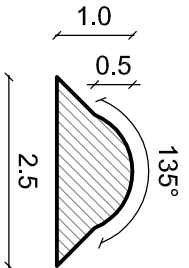

DETALLE MOLDURA #4
Esc. 1/1

DETALLE MOLDURA #xx
Esc. 1/1

DETALLE MOLDURA #xx
Esc. 1/1

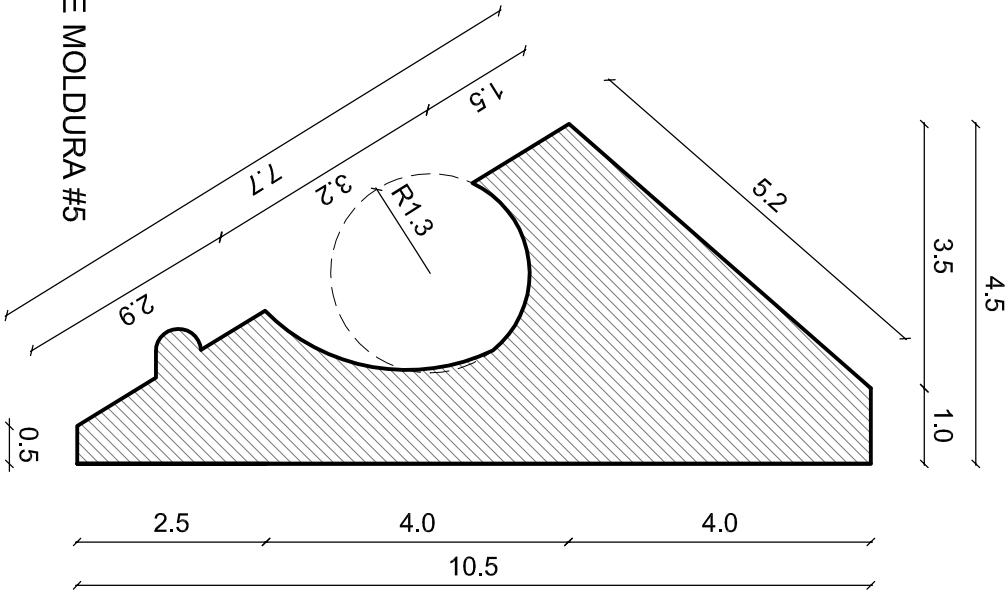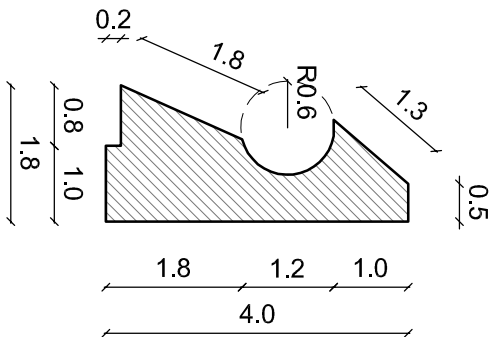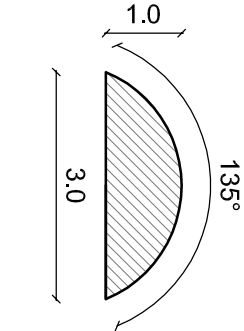

DETALLE MOLDURA #5
Esc. 1/1


DETALLE 01: Correspondiente a ventanilla de vidrio fijo en hoja de puerta 04. Muestra dimensiones y presencia de 3 molduras en la parte inferior de esta.

DETALLE 02: Muestra detalle del corte B - B, correspondiente a la interior de la hoja de la puerta 04. Se detalla dimensiones de las piezas y ubicacion de respectivas molduras.

DETALLE 03: Muestra detalle de vista en planta. Corresponde al encuentro de hoja fija con hoja abatibles. Se detalla ubicación de bisgras y dimensión de respectivas molduras.



Ubicación			
PROYECTO		DIRECCIÓN DE ARQUITECTURA DIRECCIÓN REGIONAL METROPOLITANA	
PROYECTO: REPARACIÓN PARCIAL BASÍLICA DEL SALVADOR STIGO		PROYECTO	
BASÍLICA DEL SALVADOR		ES	
Huérfanos 1796 - Santiago Región Metropolitana		Pu-4b	
LEVANTAMIENTO		1/25	Ago. 13
Puerta 04 - nártex poniente		Escala	Fecha
TD	TD	LEV	DET
1305	1305	LEV	DET
Emisor	Proyecto	Fase	Tipo
Dibuj: DS	Control: VI	Archivo de ref. TD_1212_LEV_ES_Pu-01-26_c.dwg	Zona
		Índice	

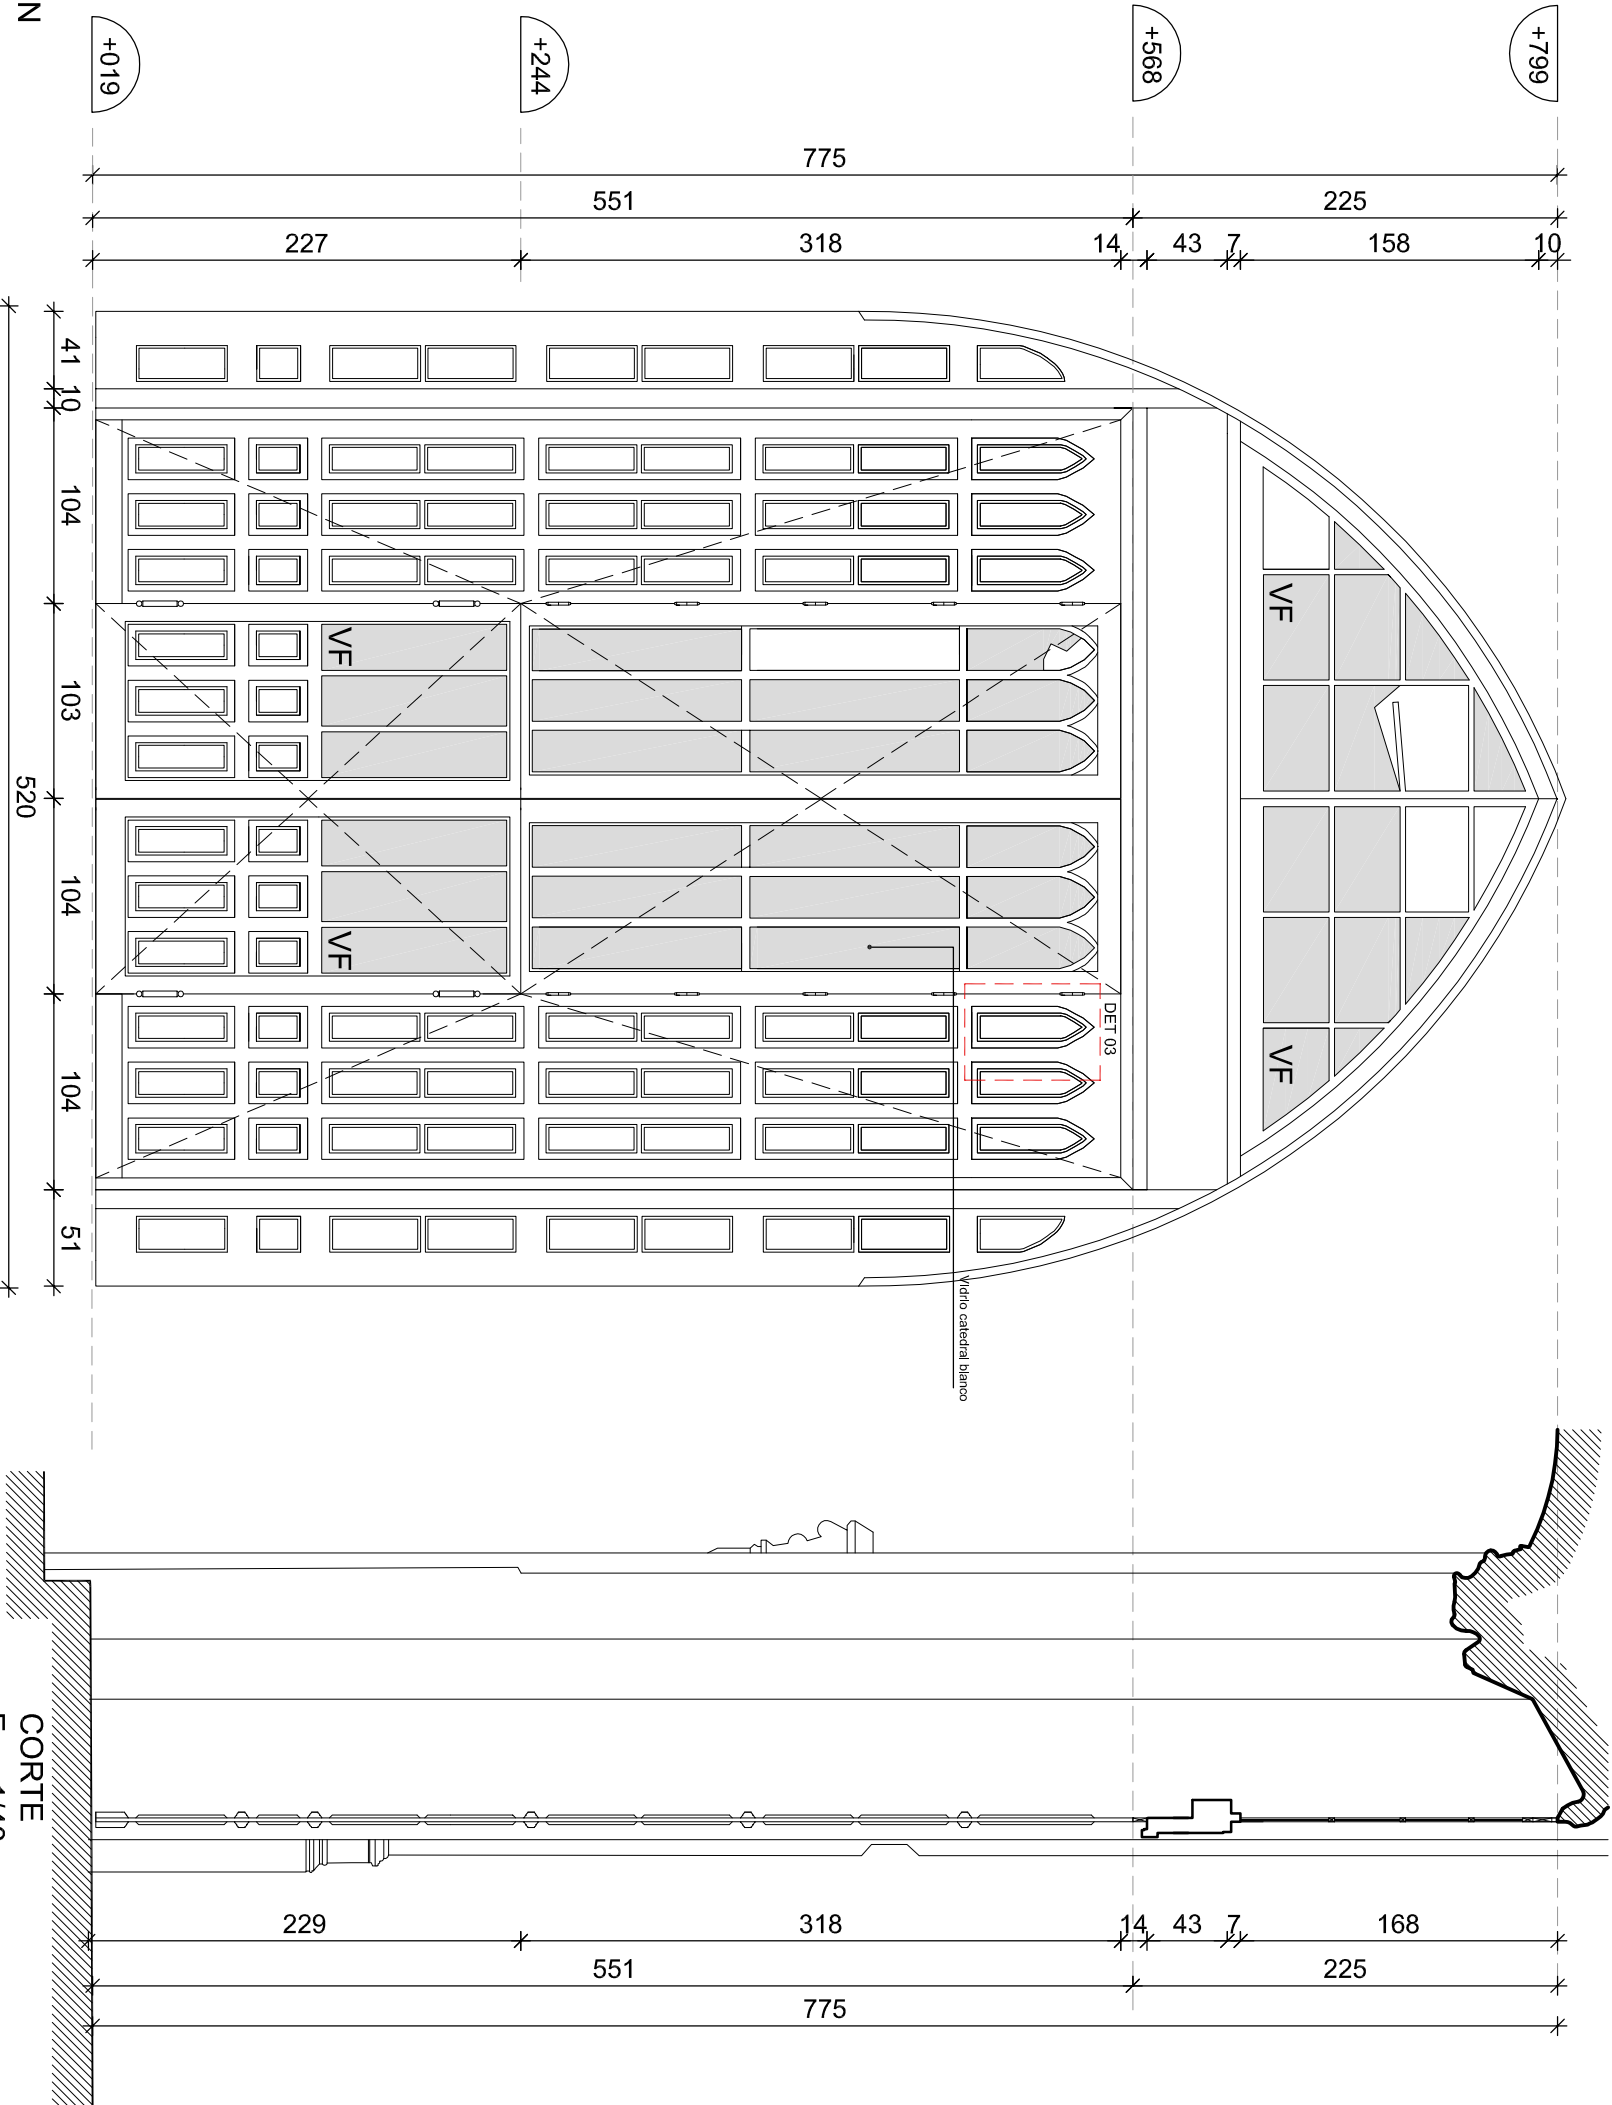


Fotografía

Ubicación					
			PROYECTO		
DIRECCIÓN DE ARQUITECTURA DIRECCIÓN REGIONAL METROPOLITANA			Arqto. Dino Bozzi F. TÁNDEM Limitada contacto@tandemlimitada.cl		
PROYECTO: REPARACIÓN PARCIAL BASÍLICA DEL SALVADOR STGO					
BASÍLICA DEL SALVADOR				ES	
Huérfanos 1796 - Santiago Región Metropolitana				Pu-5a	
LEVANTAMIENTO Puerta 05 - central nártex			1/25	Ago. 13	
TD	TD	LEV	DET	-	A
Emisor	Proyecto	Fase	Tipo	Zona	Índice
Dibuj: DS Control: VI					
Archivo de ref.: TD_1212_LEV_ES_Pu-01-26_c.dwg					


DETALLE 01: Correspondiente a encuentro entre ambas hojas abatibles inferiores de puerta 05. Se muestran dimensiones detalladas.

DETALLE 02: Muestra detalle del vista en planta puerta 05, correspondiente a encuentro de hoja de madera con estructura de albañilería. No hay presencia de marco y ningún tipo de fijación. Unión a estructura por radier y cielo.



DETALLE 03: Correspondiente a hoja abatible de madera, vista en elevación. Se muestran dimensiones detalladas del elemento arqueado

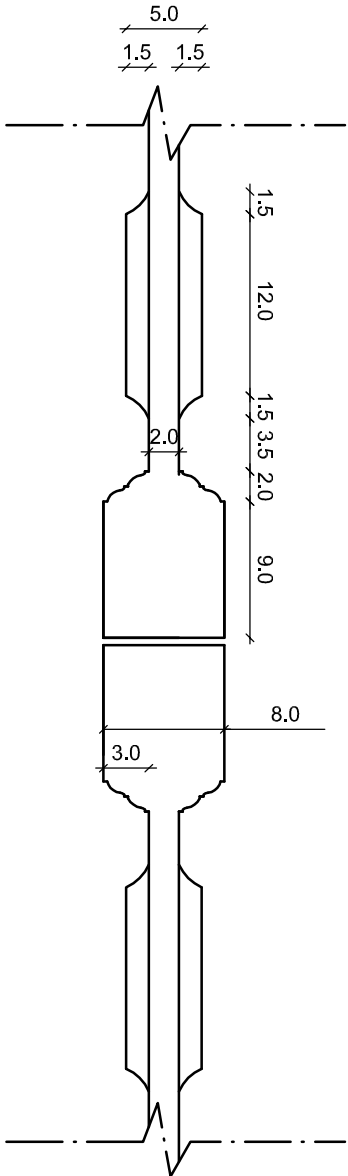



DETALLE 01
Esc. 1/5

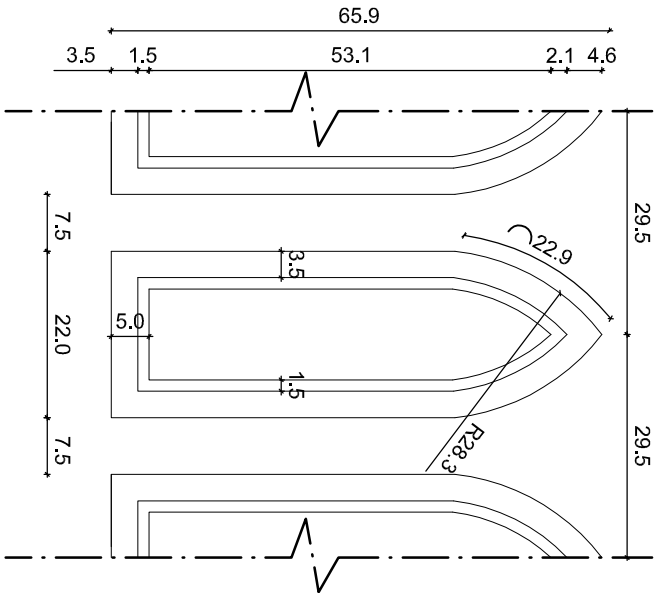

DETALLE MÓDULO TIPO
Esc. 1/10

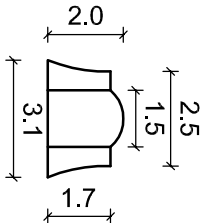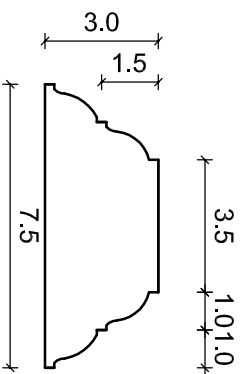

DETALLE 02
Esc. 1/5

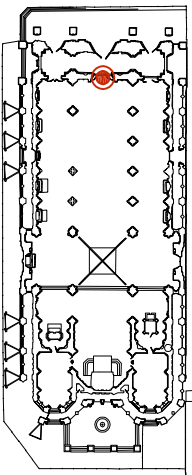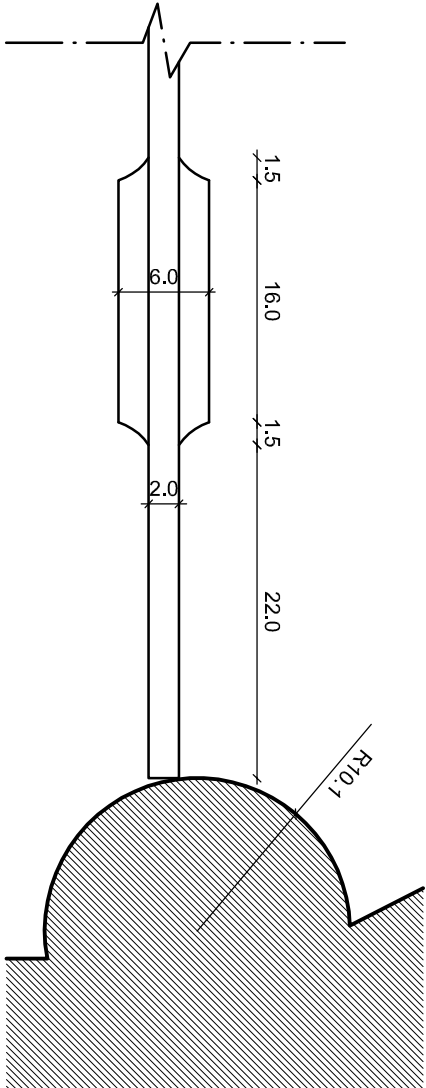

Ubicación



PROYECTO

Arqto. Dino Bozzi F.
TÁNDEM Limitada
contacto@tandemlimitada.cl

DIRECCIÓN DE ARQUITECTURA
DIRECCIÓN REGIONAL METROPOLITANA



PROYECTO: REPARACIÓN PARCIAL BASÍLICA DEL
SALVADOR STGO

BASÍLICA DEL SALVADOR
Huérfanos 1796 - Santiago
Región Metropolitana


ES
Pu-5b

DETALLE 03
Esc. 1/2

LEVANTAMIENTO				1/25	Ago. 13
Puerta 05 - central nártex				Escala	Fecha
TD	TD 1305	LEV	DET	-	A
Emisor	Proyecto	Fase	Tipo	Zona	Índice
Dibujó: DS Controló: VI Archivo de ref.: TD_1212_LEV_ES_Pu-01-26_c.dwg					

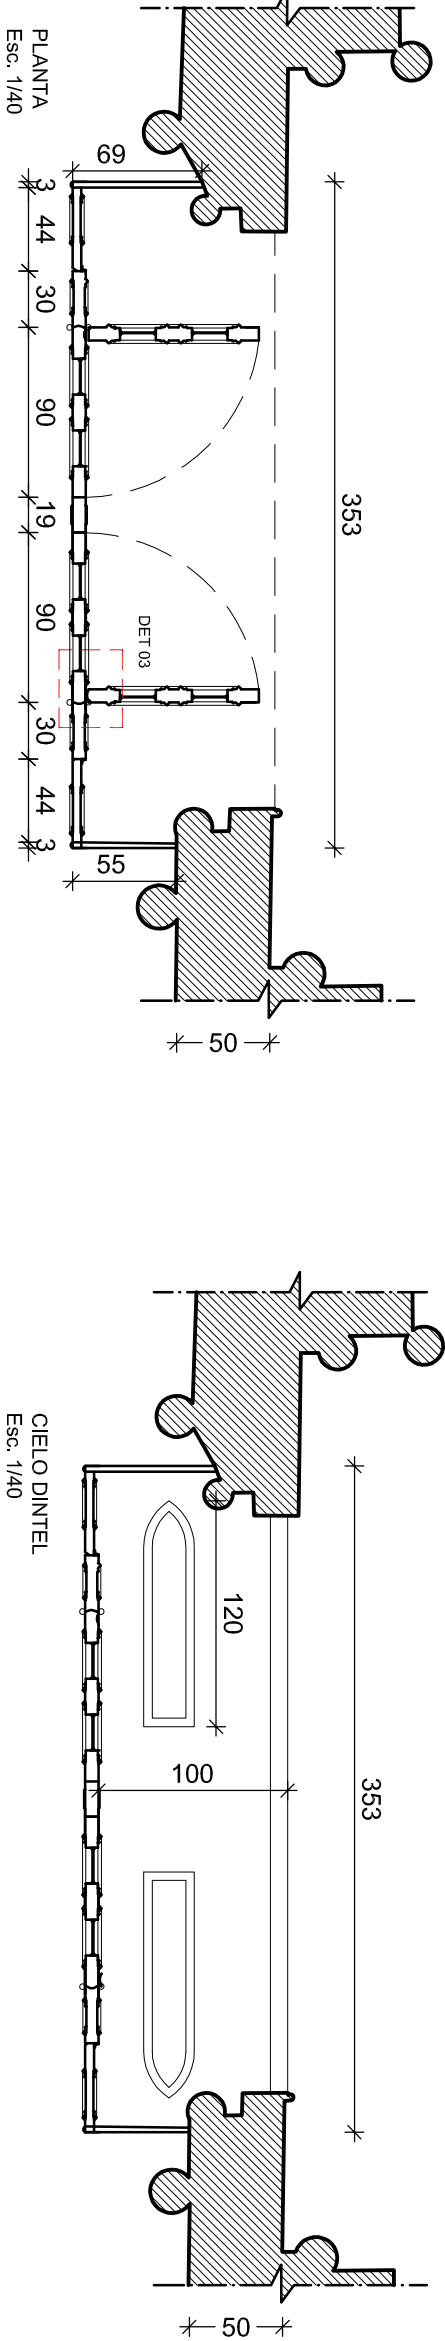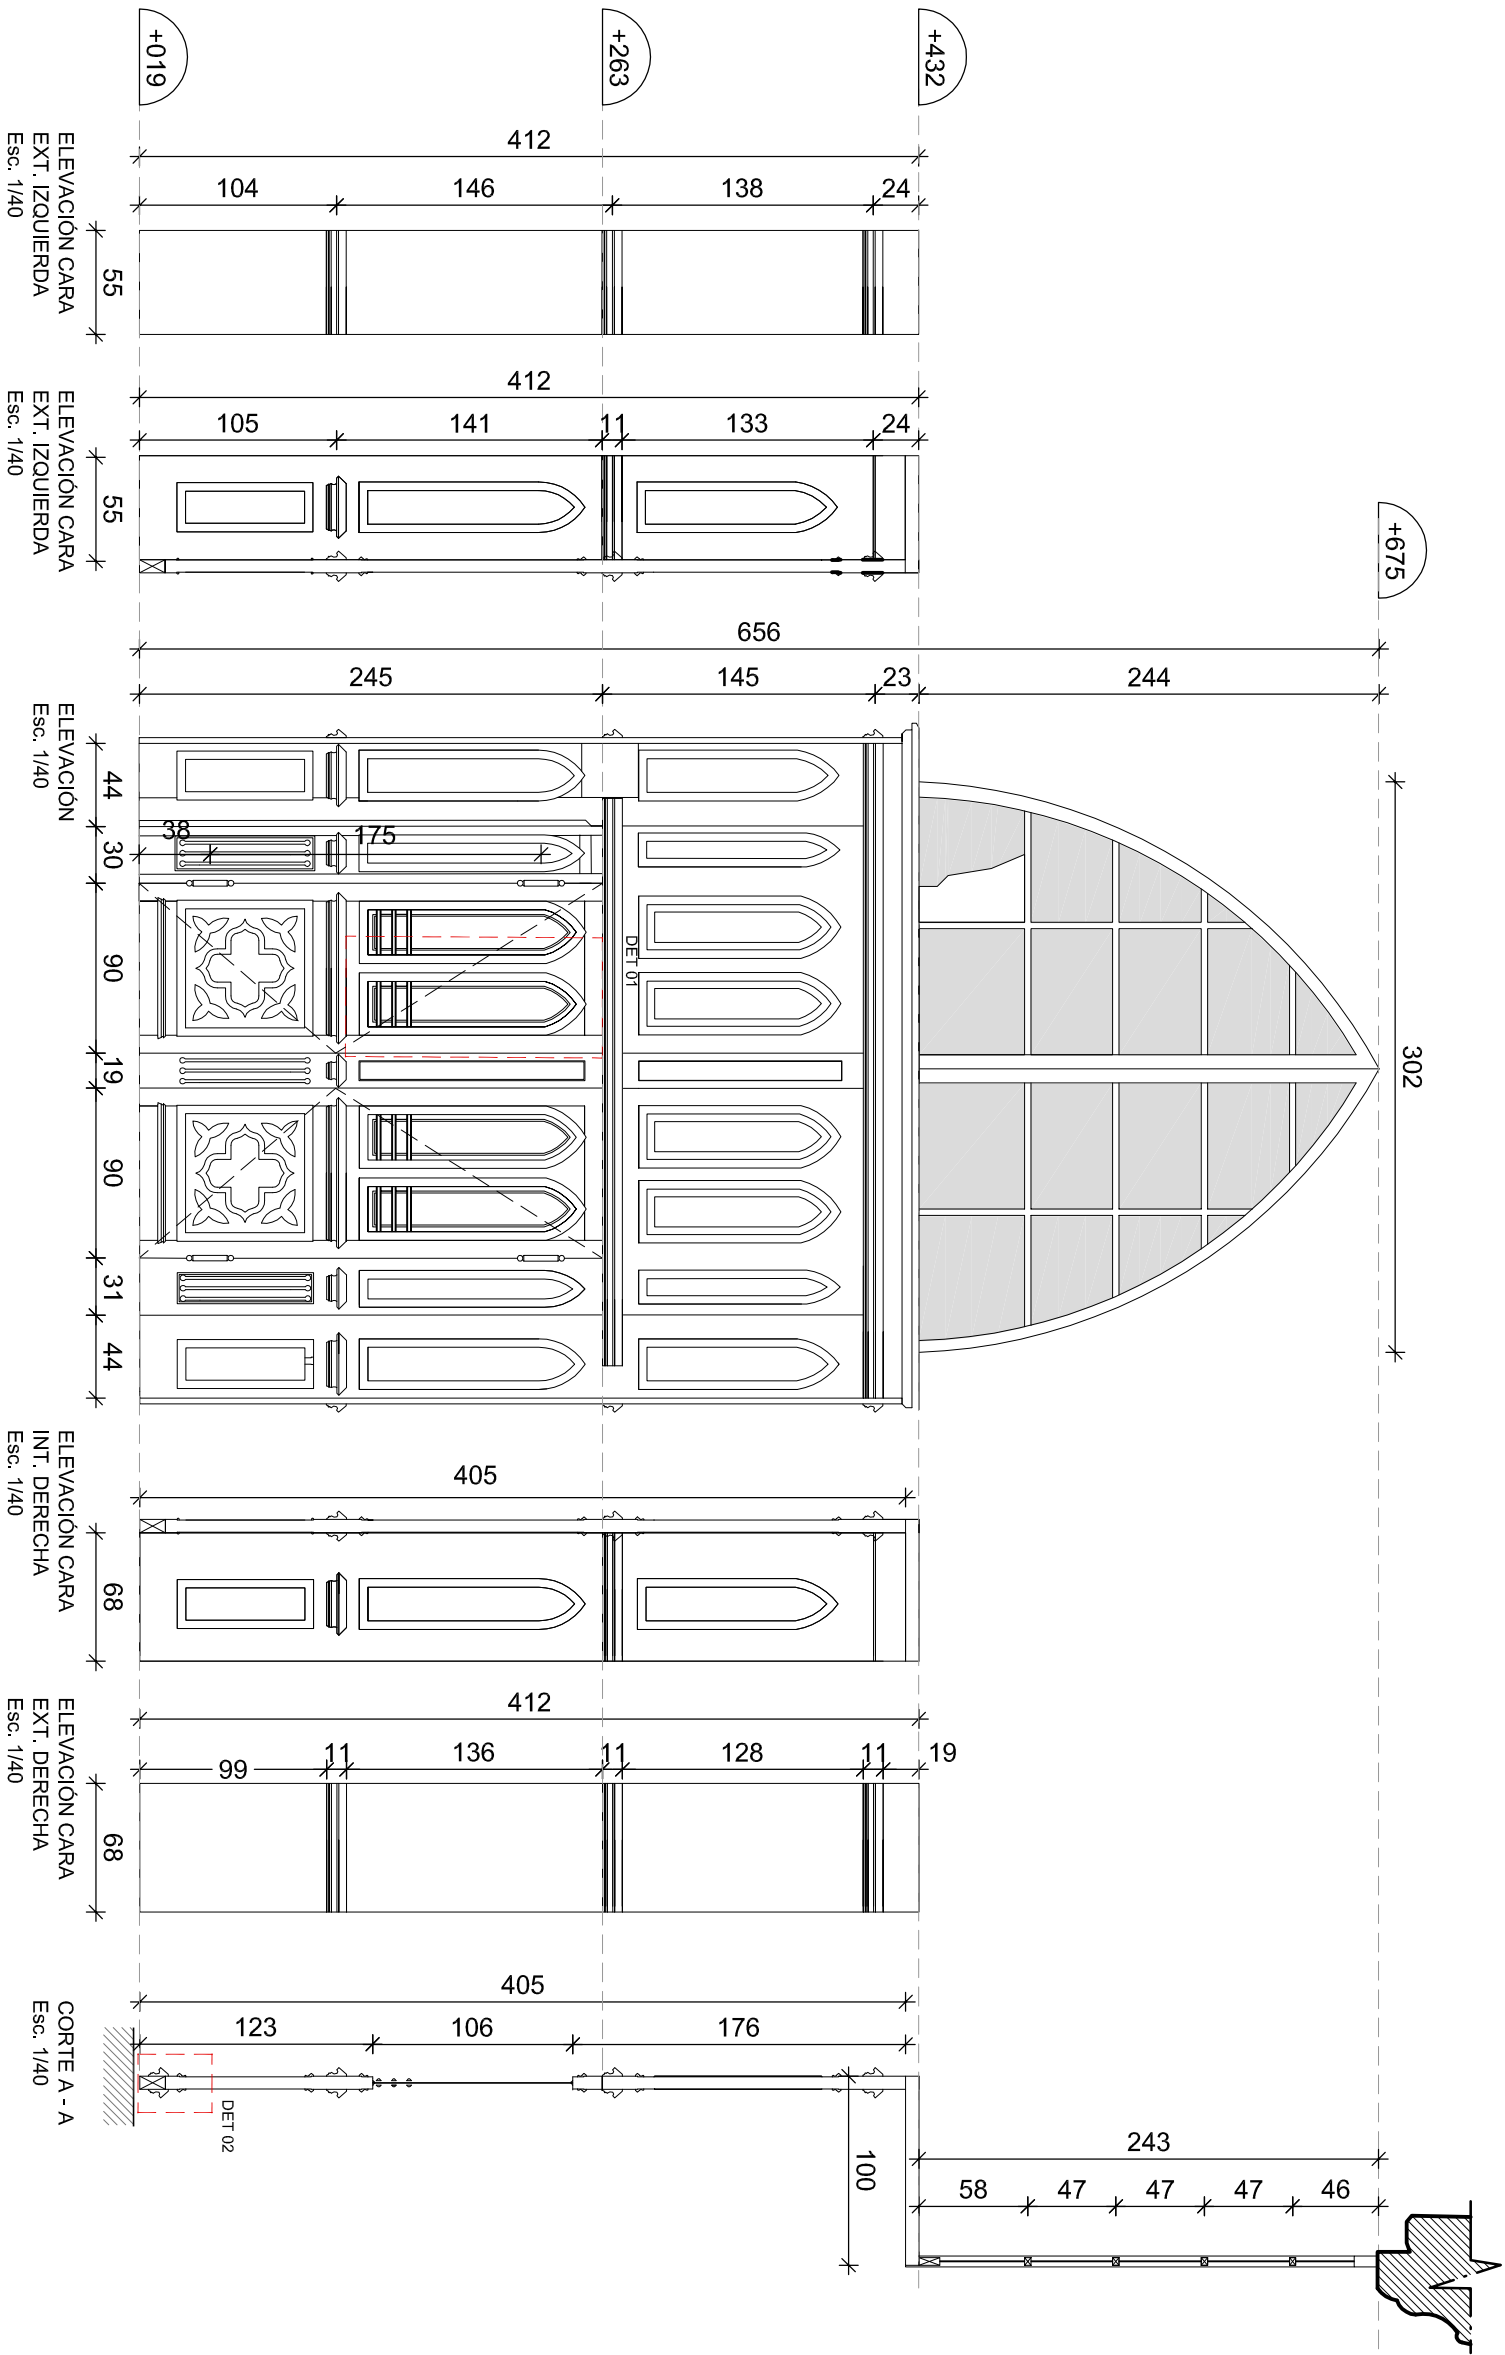




Fotografía

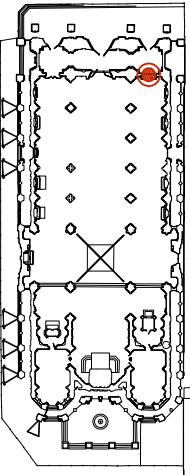Ubicación			
DIRECCIÓN DE ARQUITECTURA DIRECCIÓN REGIONAL METROPOLITANA		PROYECTO	
PROYECTO: REPARACIÓN PARCIAL BASÍLICA DEL SALVADOR STGO		Argto. Dino Bozzi F. TÁNDEM Limitada contacto@tandemlimitada.cl	
BASÍLICA DEL SALVADOR		Pu-06	
LEVANTAMIENTO		1/40	
Puerta 06 - nártex oriente		Escala	
TD		Ago. 13	
TD		Escala	
TD		Fecha	
Emisor		Índice	
Proyecto		-	
Fase		Zona	
Tipo		-	
Detalle		-	
Archivo de ref. TD_1212_LEV_ES_Pu-01-26_c.dwg		-	


DETALLE 01: Correspondiente a ventanilla de vidrio fijo en hoja de puerta 04. Muestra dimensiones y presencia de 3 molduras en la parte inferior de esta.

DETALLE 02: Muestra detalle del corte B - B, correspondiente a la interior de la hoja de la puerta 04. Se detalla dimensiones de las piezas y ubicacion de respectivas molduras.


DETALLE 03: Muestra detalle de vista en planta. Corresponde al encuentro de hoja fija con hoja abatibles. Se detalla ubicación de bisagras y dimensión de respectivas molduras.

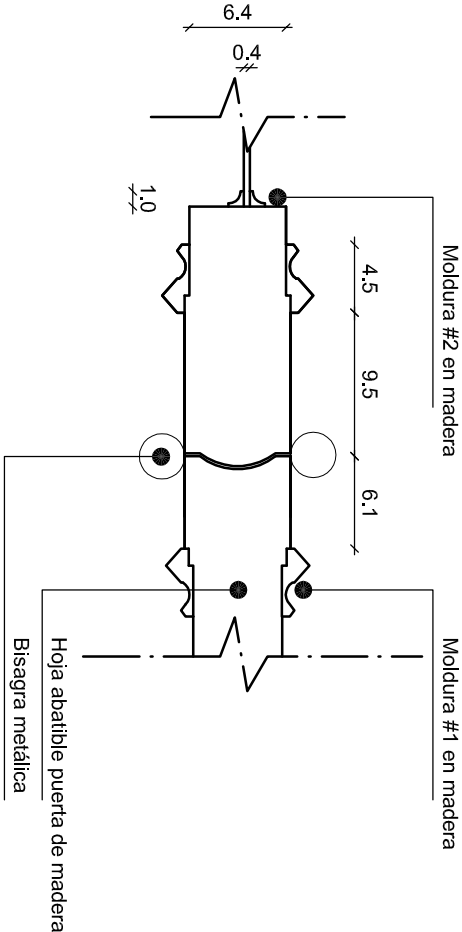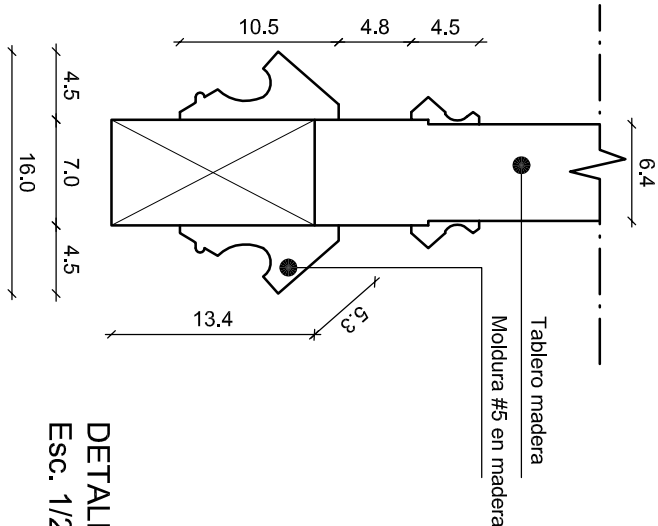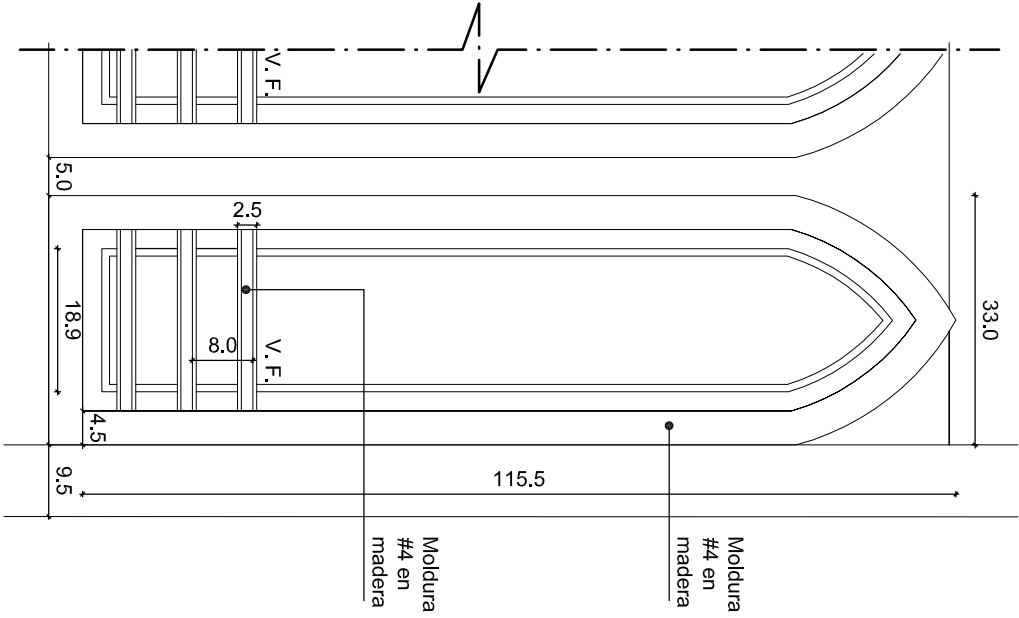

DETALLE 01
Esc. 1/2

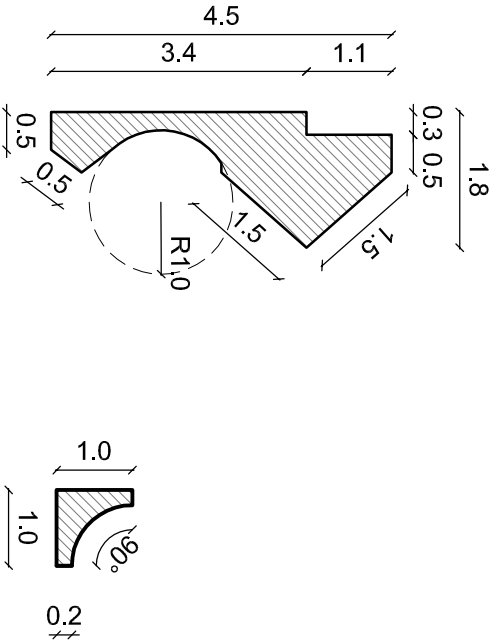


DETALLE MOLDURA #1
Esc. 1/1

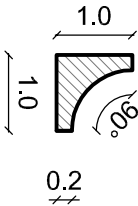


DETALLE MOLDURA #2
Esc. 1/1


DETALLE MOLDURA
Esc. 1/1

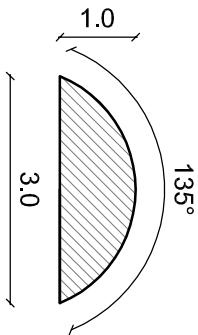


DETALLE MOLDURA
Esc. 1/1

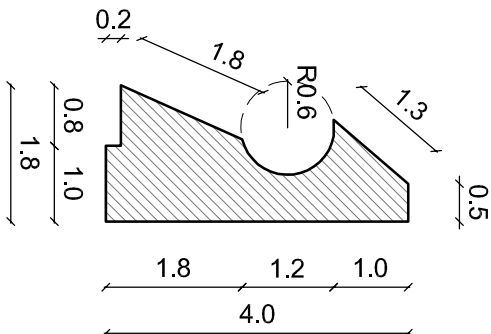


DETALLE MOLDURA #3
Esc. 1/1

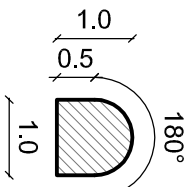


DETALLE MOLDURA #4
Esc. 1/1

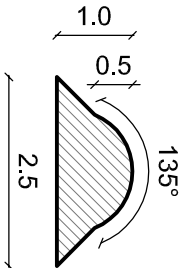



DETALLE MOLDURA #5
Esc. 1/1

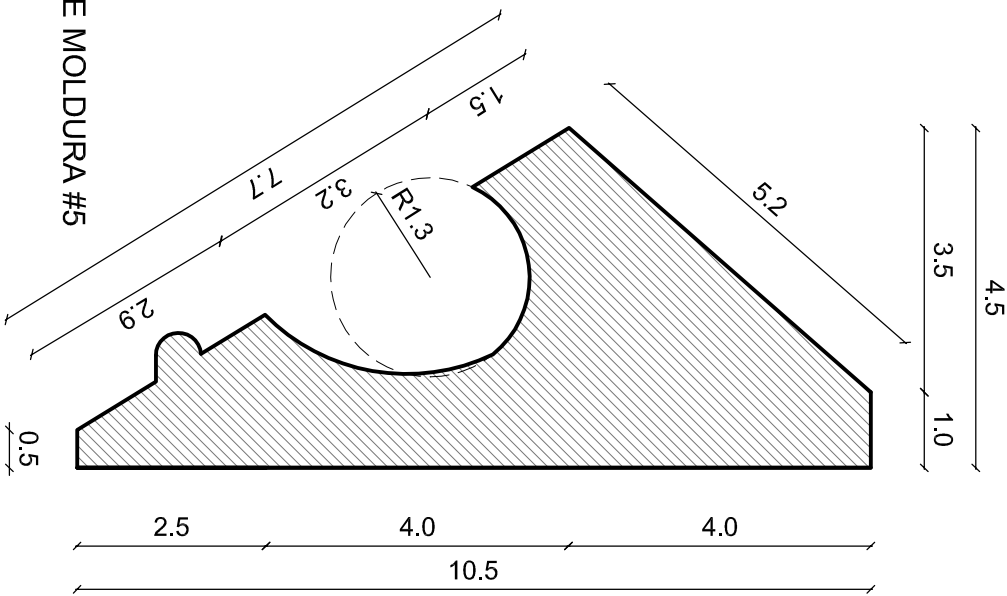


Ubicación

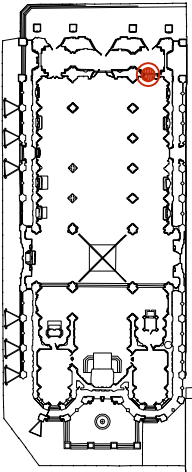

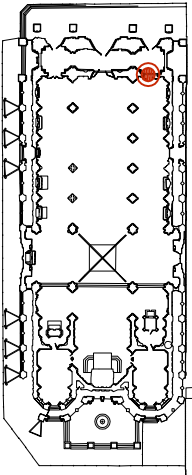
Ubicación					
					
PROYECTO					
			Arqto. Dino Bozzi F. TÁNDEM Limitada contacto@tandemlimitada.cl		
DIRECCIÓN DE ARQUITECTURA DIRECCIÓN REGIONAL METROPOLITANA					
PROYECTO: REPARACIÓN PARCIAL BASÍLICA DEL SALVADOR STGO					
BASÍLICA DEL SALVADOR					
Huérfanos 1796 - Santiago Región Metropolitana					
LEVANTAMIENTO					
Puerta 06 - nártex oriente					
TD	TD	LEV	DET	-	A
Emisor	Proyecto	Fase	Tipo	Zona	Índice
Dibuj: DS	Control: VI	Archivo de ref.: TD_1212_LEV_ES_Pu-01-26_c.dwg			

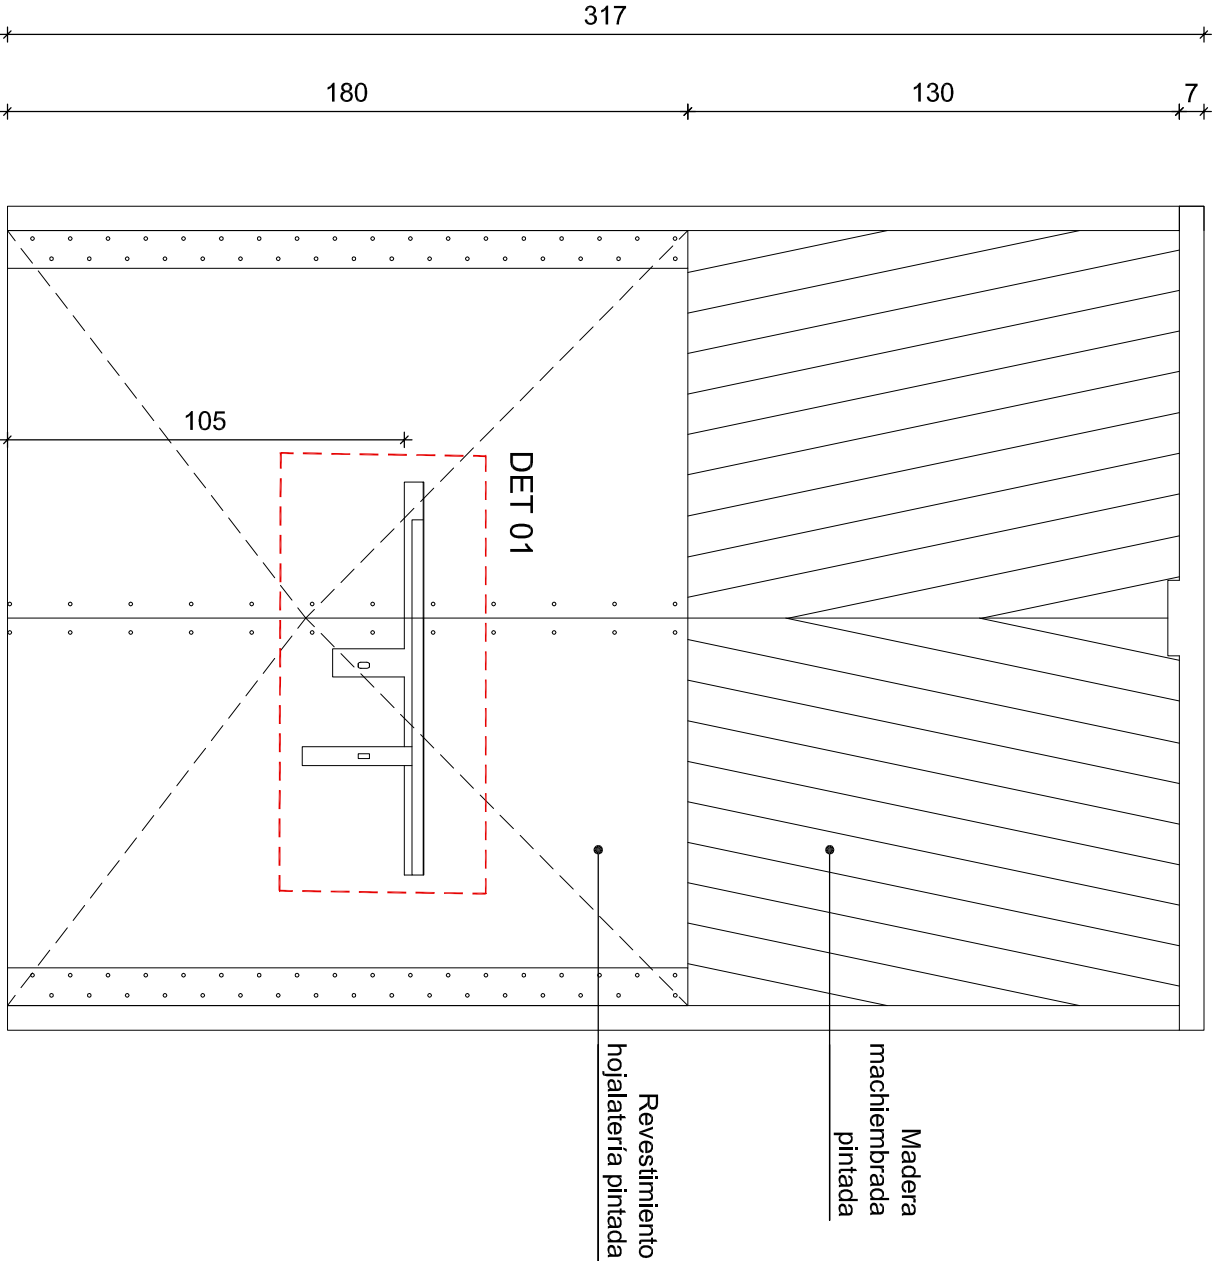


ELEVACIÓN EXTERIOR
Esc. 1/20

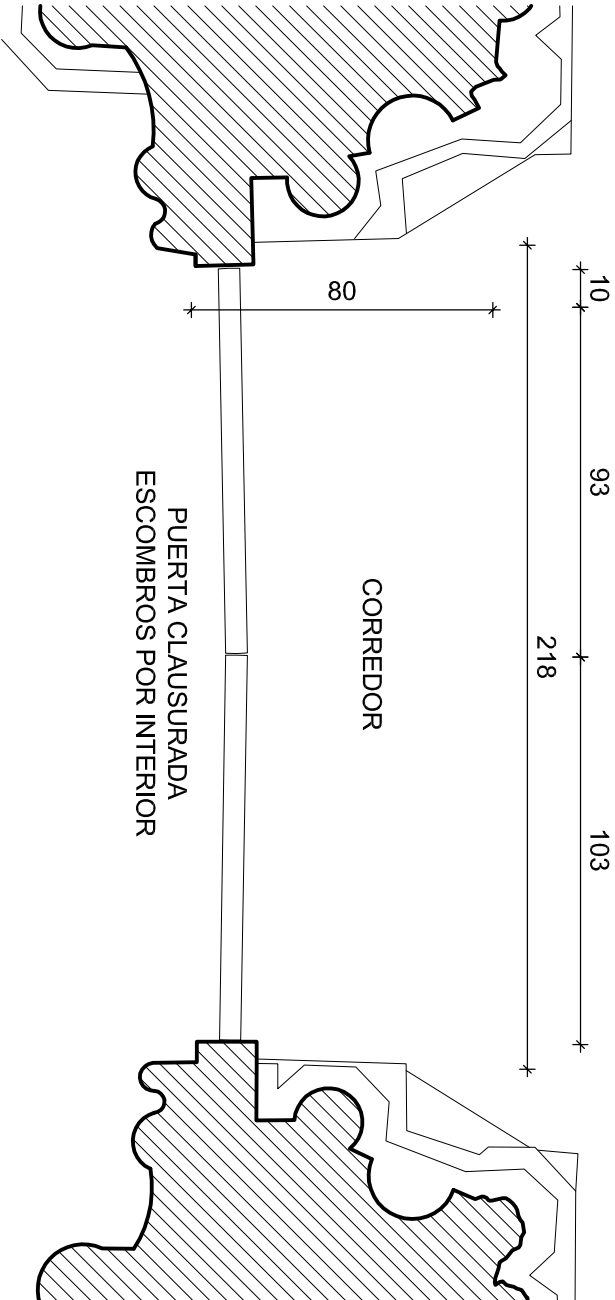

PLANTA
Esc. 1/20

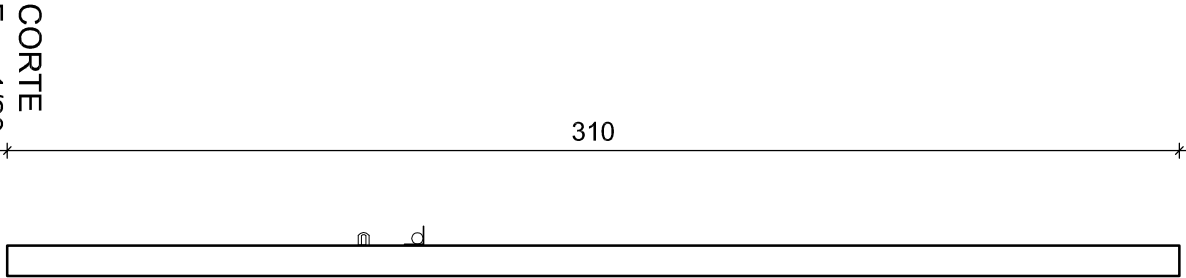


CORTE
Esc. 1/20

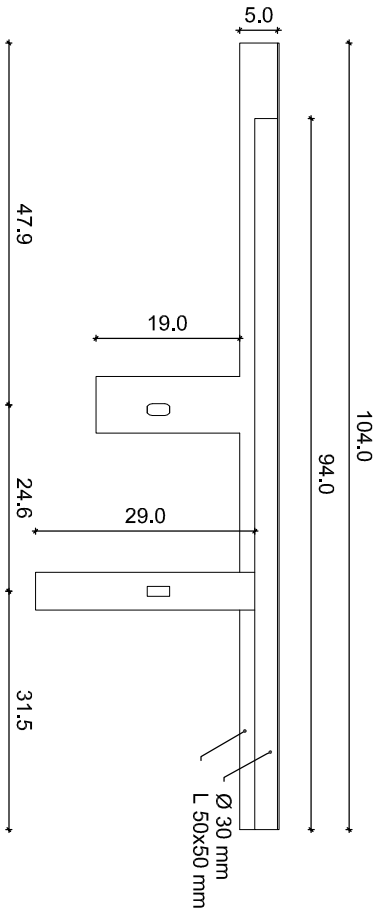


DETALLE 1
Esc. 1/10




Fotografía

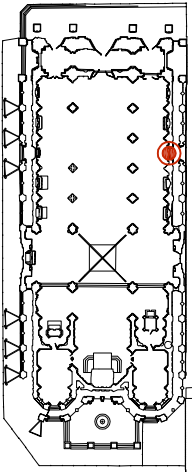


Ubicación

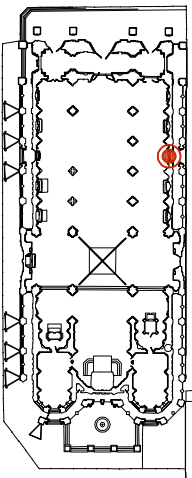Ubicación					
					
			PROYECTO		
DIRECCIÓN DE ARQUITECTURA Ministerio de Obras Públicas			Argto. Dino Bozzi F. TÁNDEM Limitada contacto@tandemlimitada.cl		
DIRECCIÓN DE ARQUITECTURA DIRECCIÓN REGIONAL METROPOLITANA					
PROYECTO: REPARACIÓN PARCIAL BASÍLICA DEL SALVADOR STGO					
BASÍLICA DEL SALVADOR				ES	
Huérfanos 1796 - Santiago Región Metropolitana				Pu-07	
LEVANTAMIENTO			1/20		
Puerta 07 - nave oriente			Ago. 13		
			Escala		
TD	TD	LEV	DET	-	A
Emisor	Proyecto	Fase	Tipo	Zona	Índice
Dibujó: DS					
Controló: VI					
Archivo de ref.: TD_1212_LEV_ES_Pu-07-286_c.dwg					

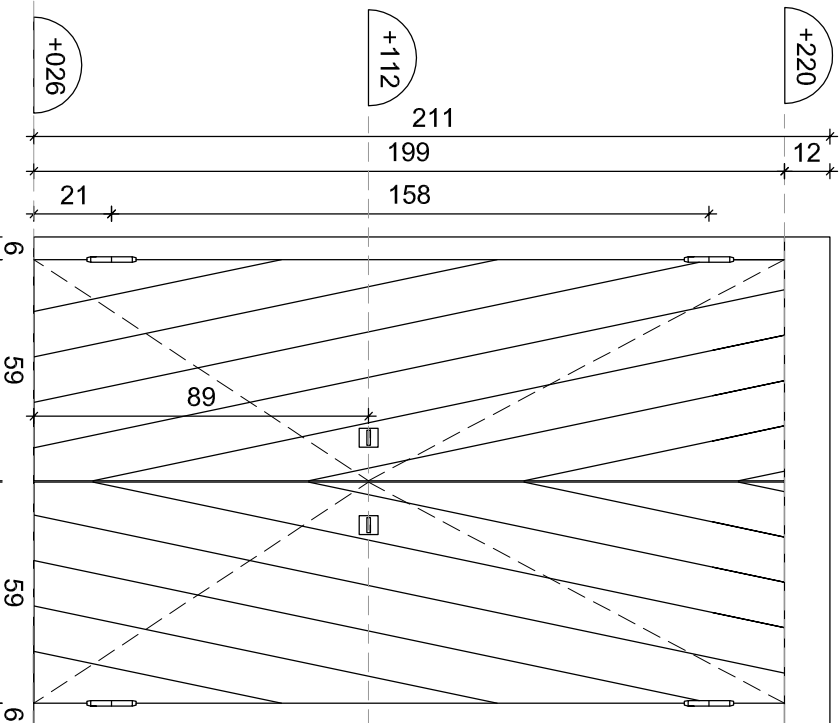


Pu 08 - EXT.
Esc. 1/20

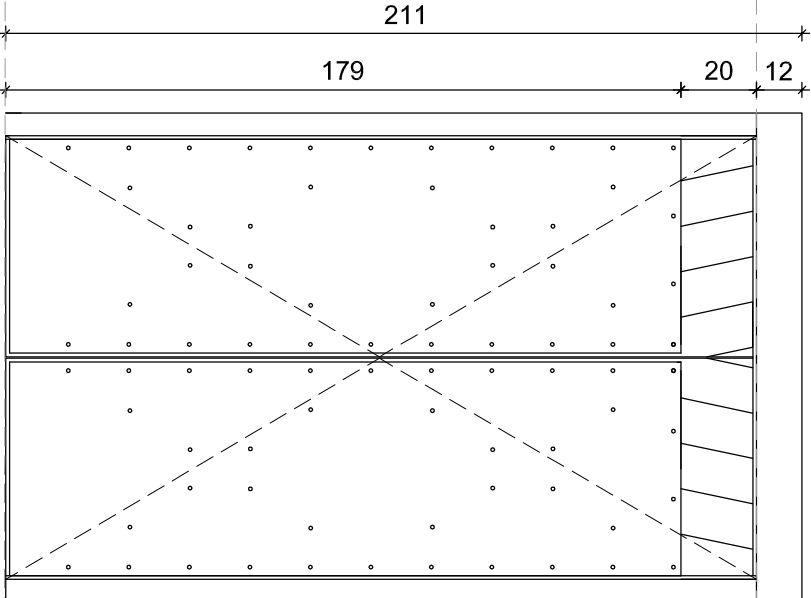


Pu 08 - INTERIOR
Esc. 1/20




Pu 08 - CORTE
Esc. 1/20

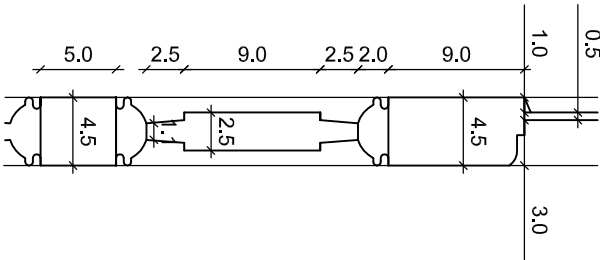


DETALLE 1
Esc. 1/10

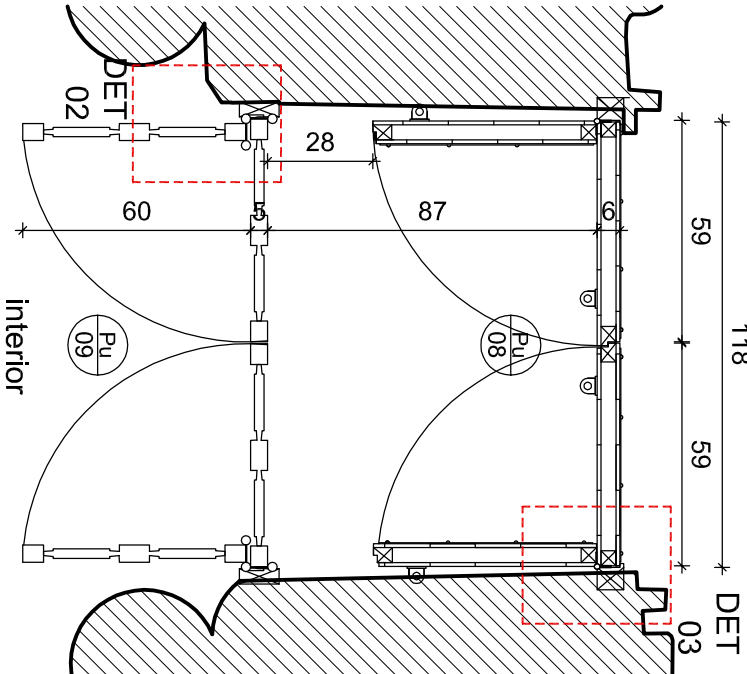


PLANTA PUERTAS 8 Y 9
Esc. 1/20

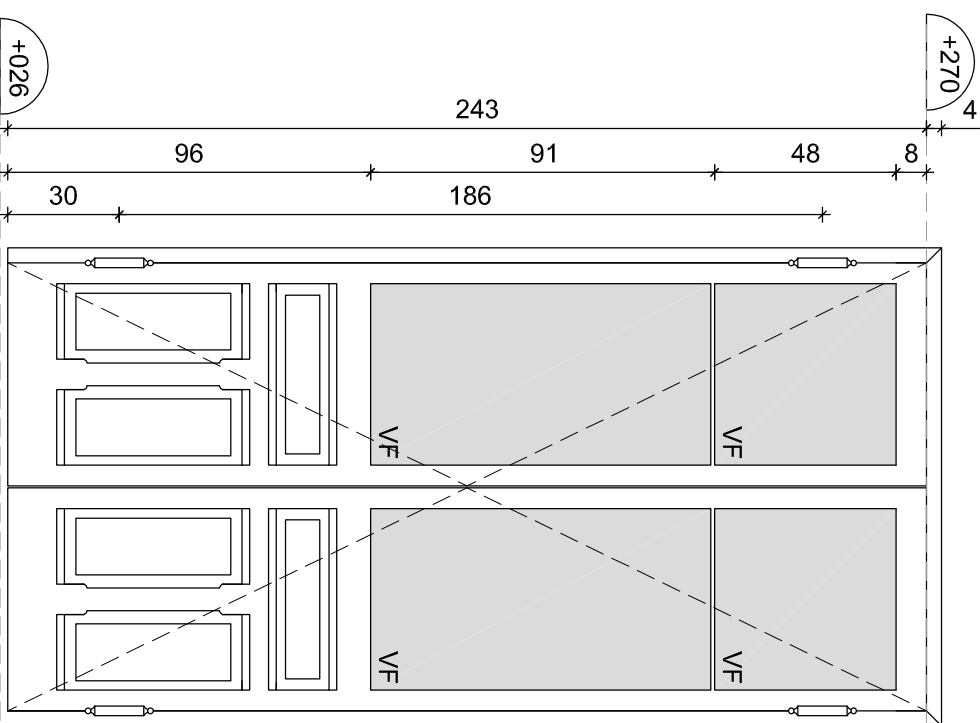


Pu 09 - EXT.
Esc. 1/20

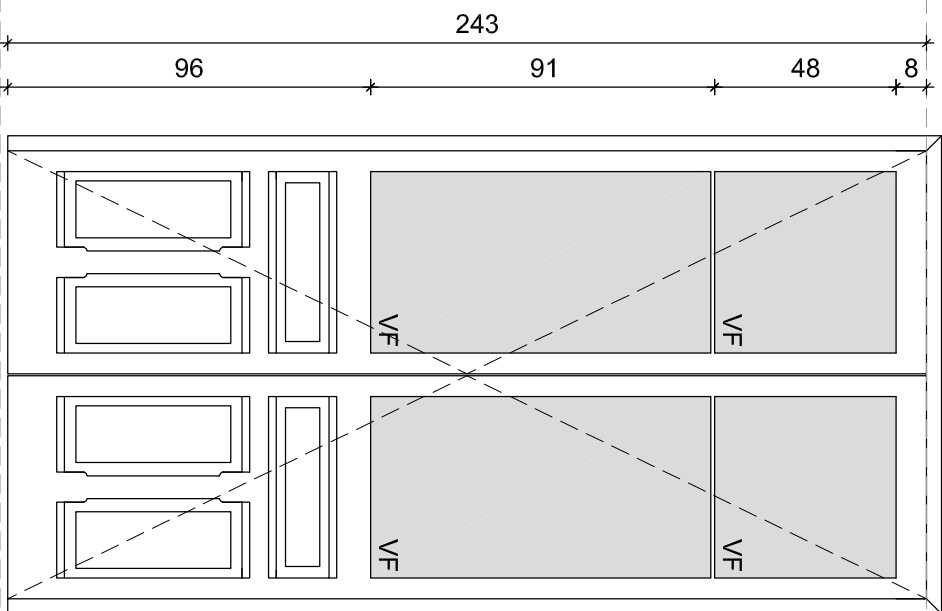


Pu 09 - INTERIOR
Esc. 1/20

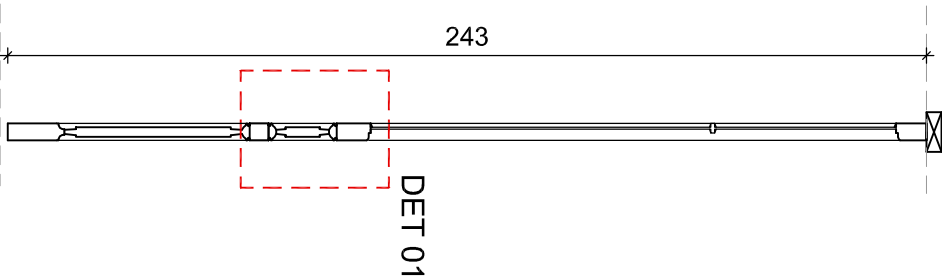

Pu 09 - CORTE
Esc. 1/20

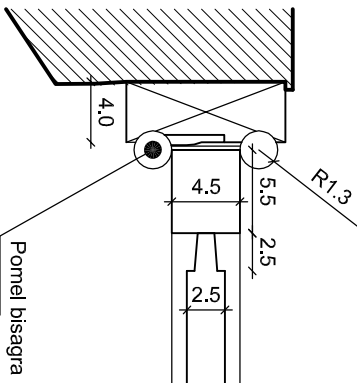


DETALLE 2
Esc. 1/10

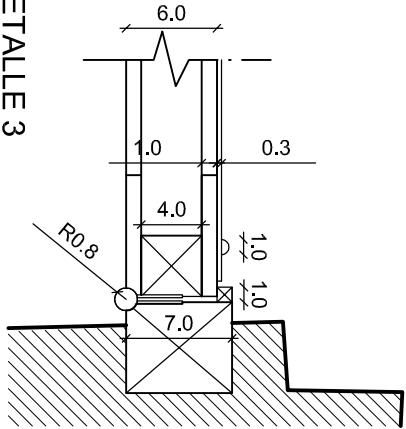


DETALLE 3
Esc. 1/10

Ubicación		PROYECTO	
DIRECCIÓN DE ARQUITECTURA DIRECCIÓN REGIONAL METROPOLITANA		Arqto. Dino Bozzi F. TÁNDEM Limitada contacto@tandemlimitada.cl	
PROYECTO: REPARACIÓN PARCIAL BASÍLICA DEL SALVADOR STGO			
BASÍLICA DEL SALVADOR		ES Pu 08-09	
Huérfanos 1796 - Santiago Región Metropolitana			
LEVANTAMIENTO		1/20	Ago. 13
Puertas 08 y 09 en transepto		Escala	Fecha
TD	TD 1305	LEV	DET
Emisor	Proyecto	Fase	Tipo
Dibujó: DS		Controló: VI	Archivo de ref.: TD_1212_LEV_ES_Pu-01-206_c00mg

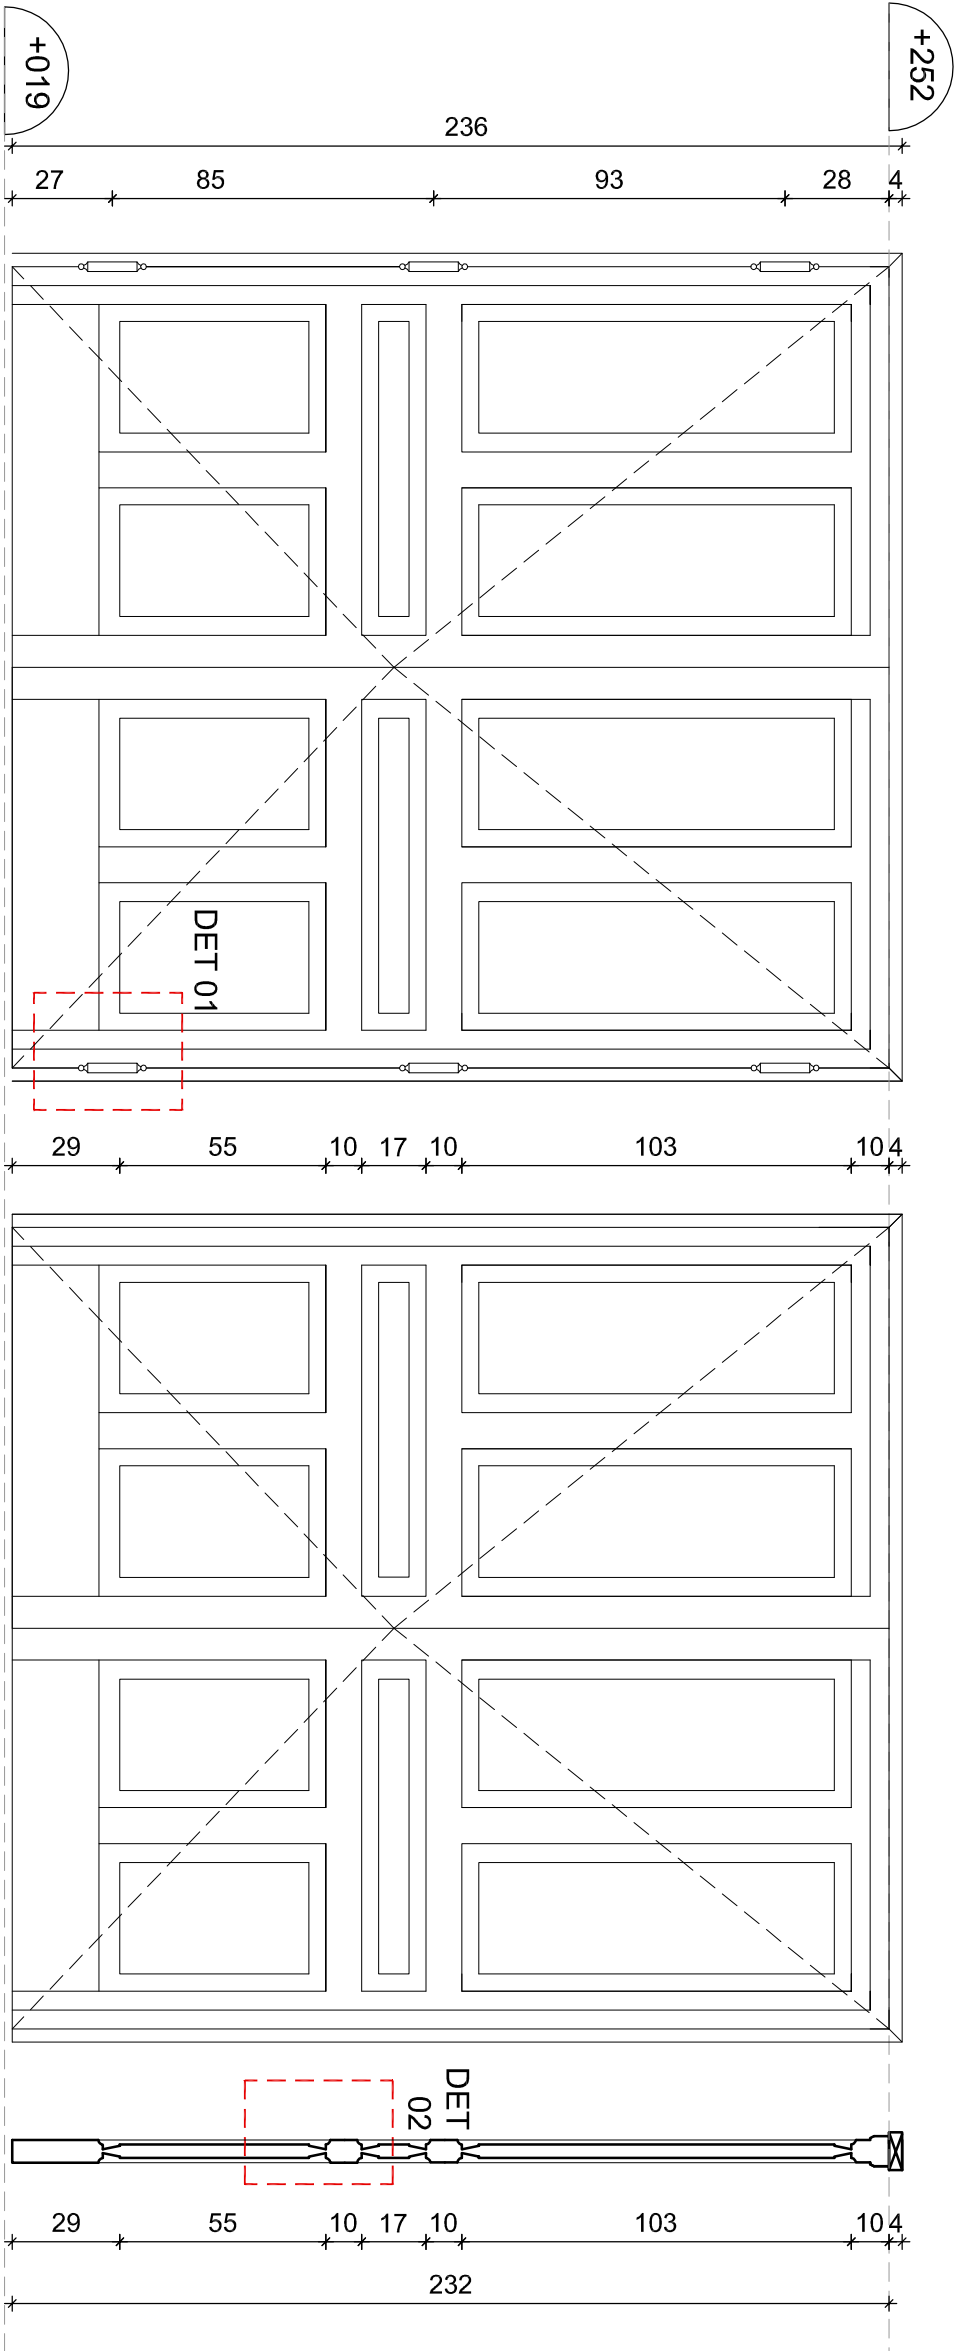



Fotografía

Ubicación

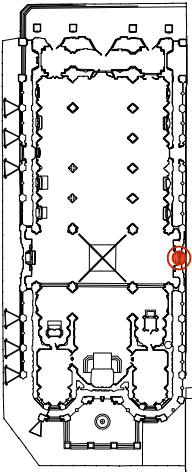


ELEVACIÓN INTERIOR
Esc. 1/20

ELEVACIÓN EXTERIOR
Esc. 1/20

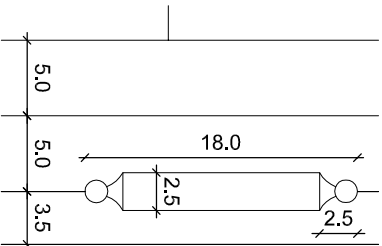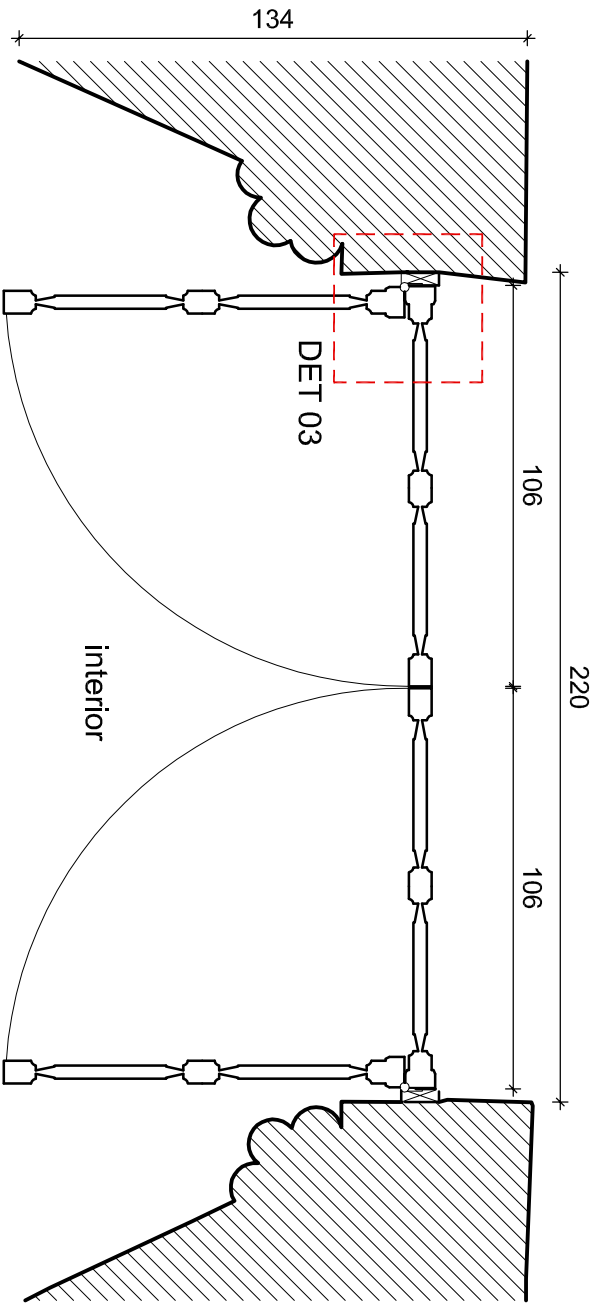









DETALLE 1
Esc. 1/5


DETALLE 2
Esc. 1/5


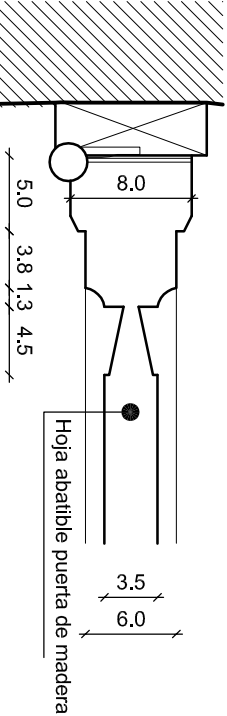


PLANTA
Esc. 1/20

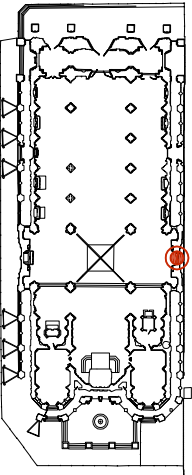Ubicación				
				
			PROYECTO	
Arqto. Dino Bozzi F. TÁNDEM Limitada contacto@tandemlimitada.cl				
DIRECCIÓN DE ARQUITECTURA DIRECCIÓN REGIONAL METROPOLITANA				
PROYECTO: REPARACIÓN PARCIAL BASÍLICA DEL SALVADOR STGO				
BASÍLICA DEL SALVADOR			ES	
Huérfanos 1796 - Santiago Región Metropolitana			Pu-10	
LEVANTAMIENTO Puerta 10 - transepto			1/20	Ago. 13
			Escala	Fecha
TD	TD 1305	LEV	DET	-
Emisor	Proyecto	Fase	Tipo	Zona
			Índice	A
Dibujó: DS Control: VI				
Archivo de ref.: TD_1212_LEV_ES_Pu-01-286_c.dwg				

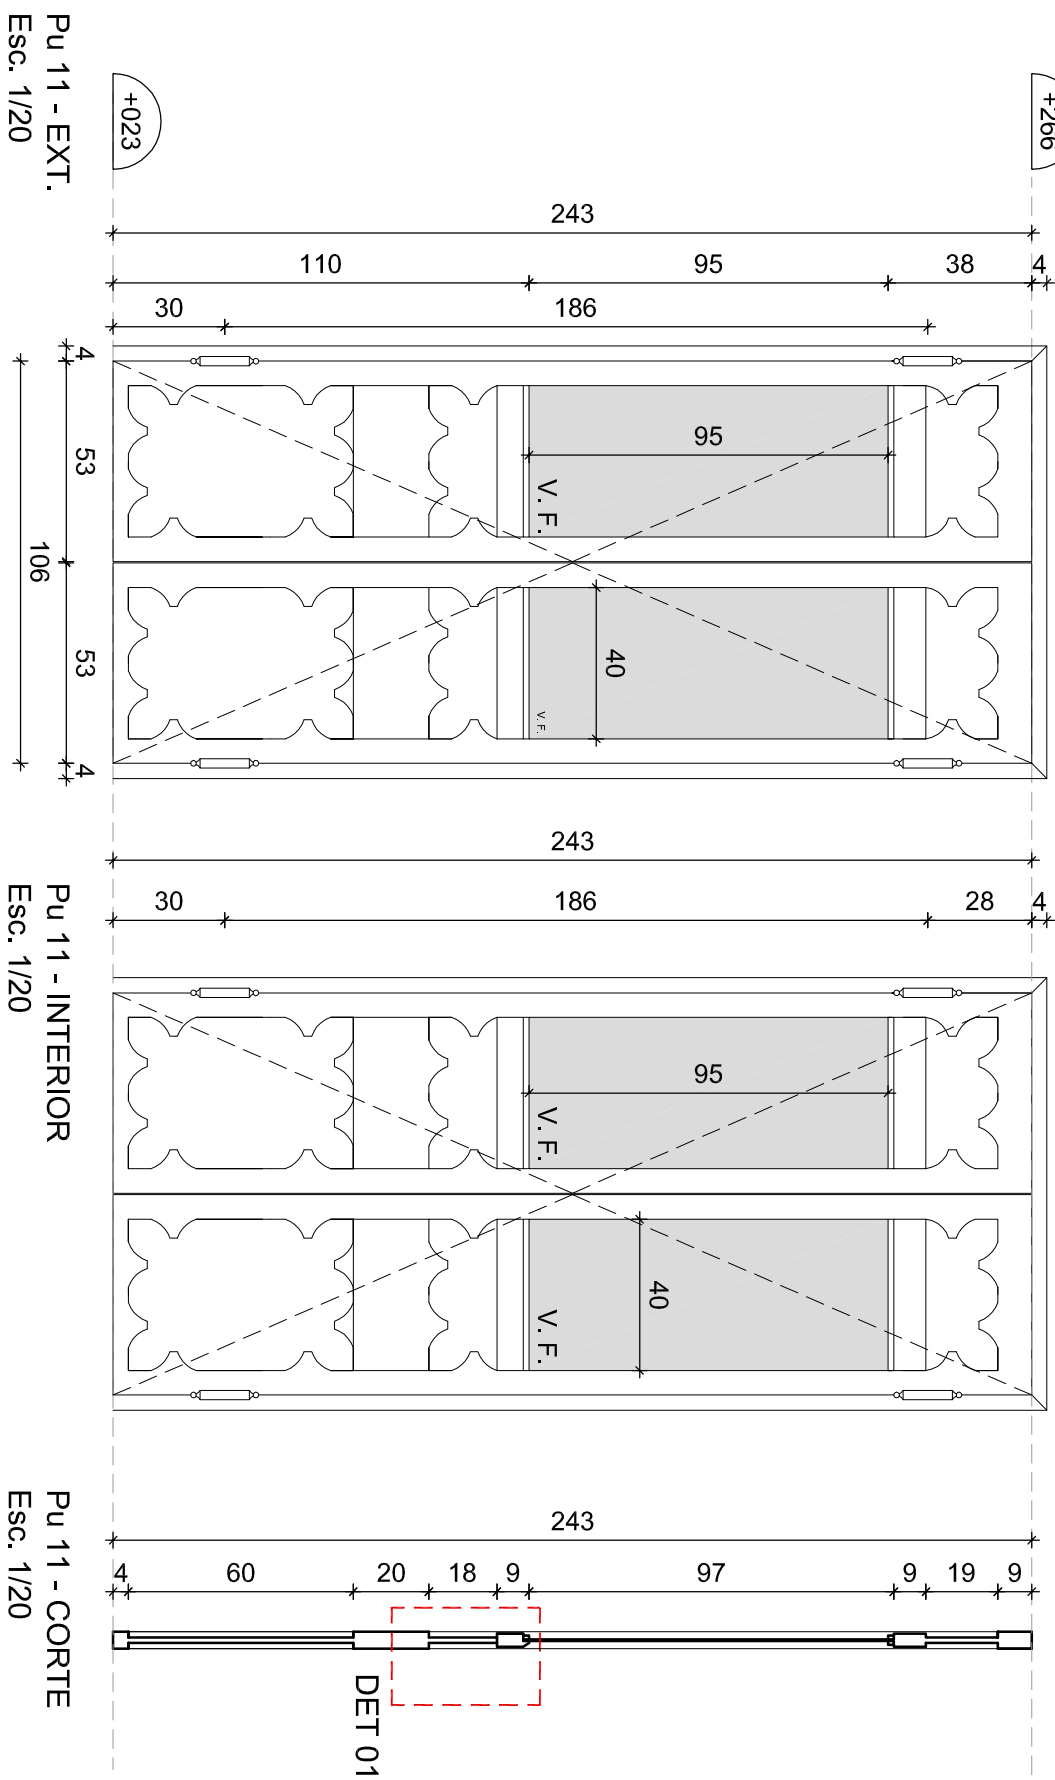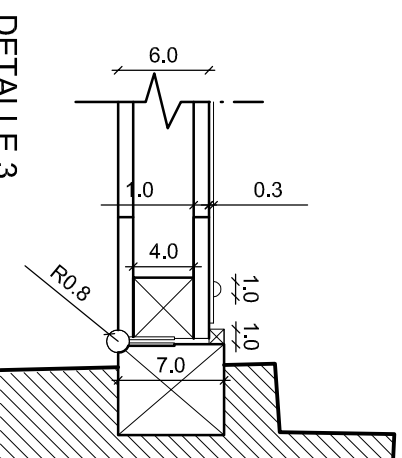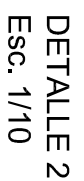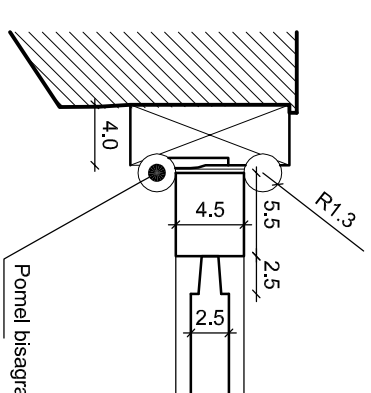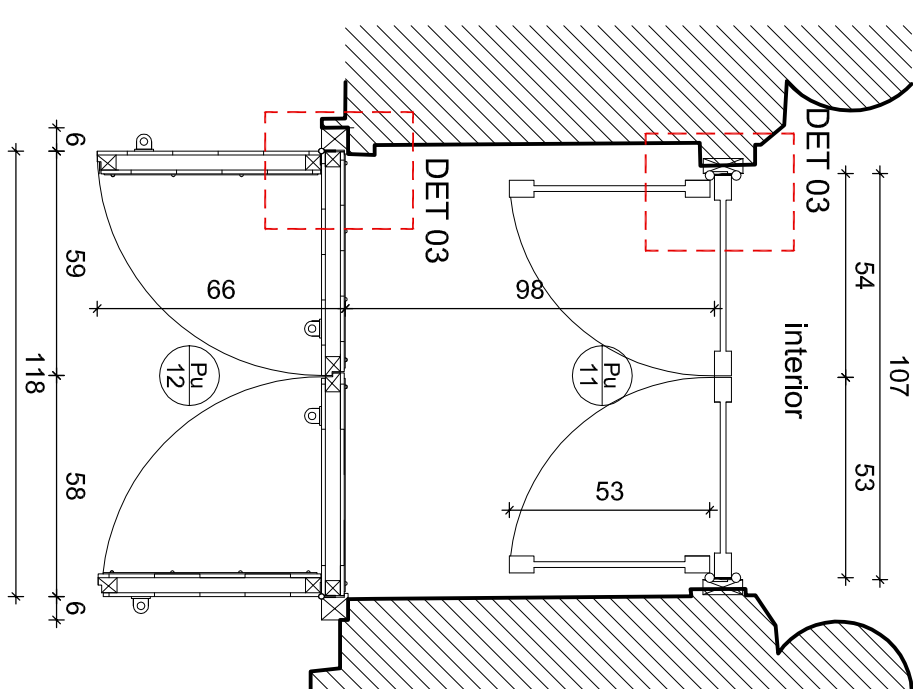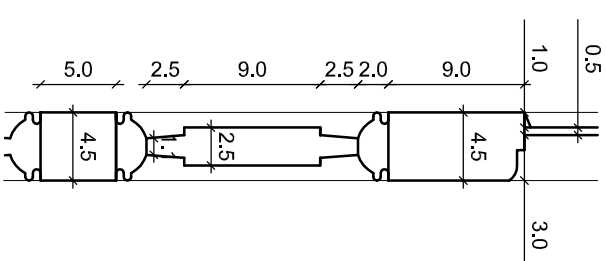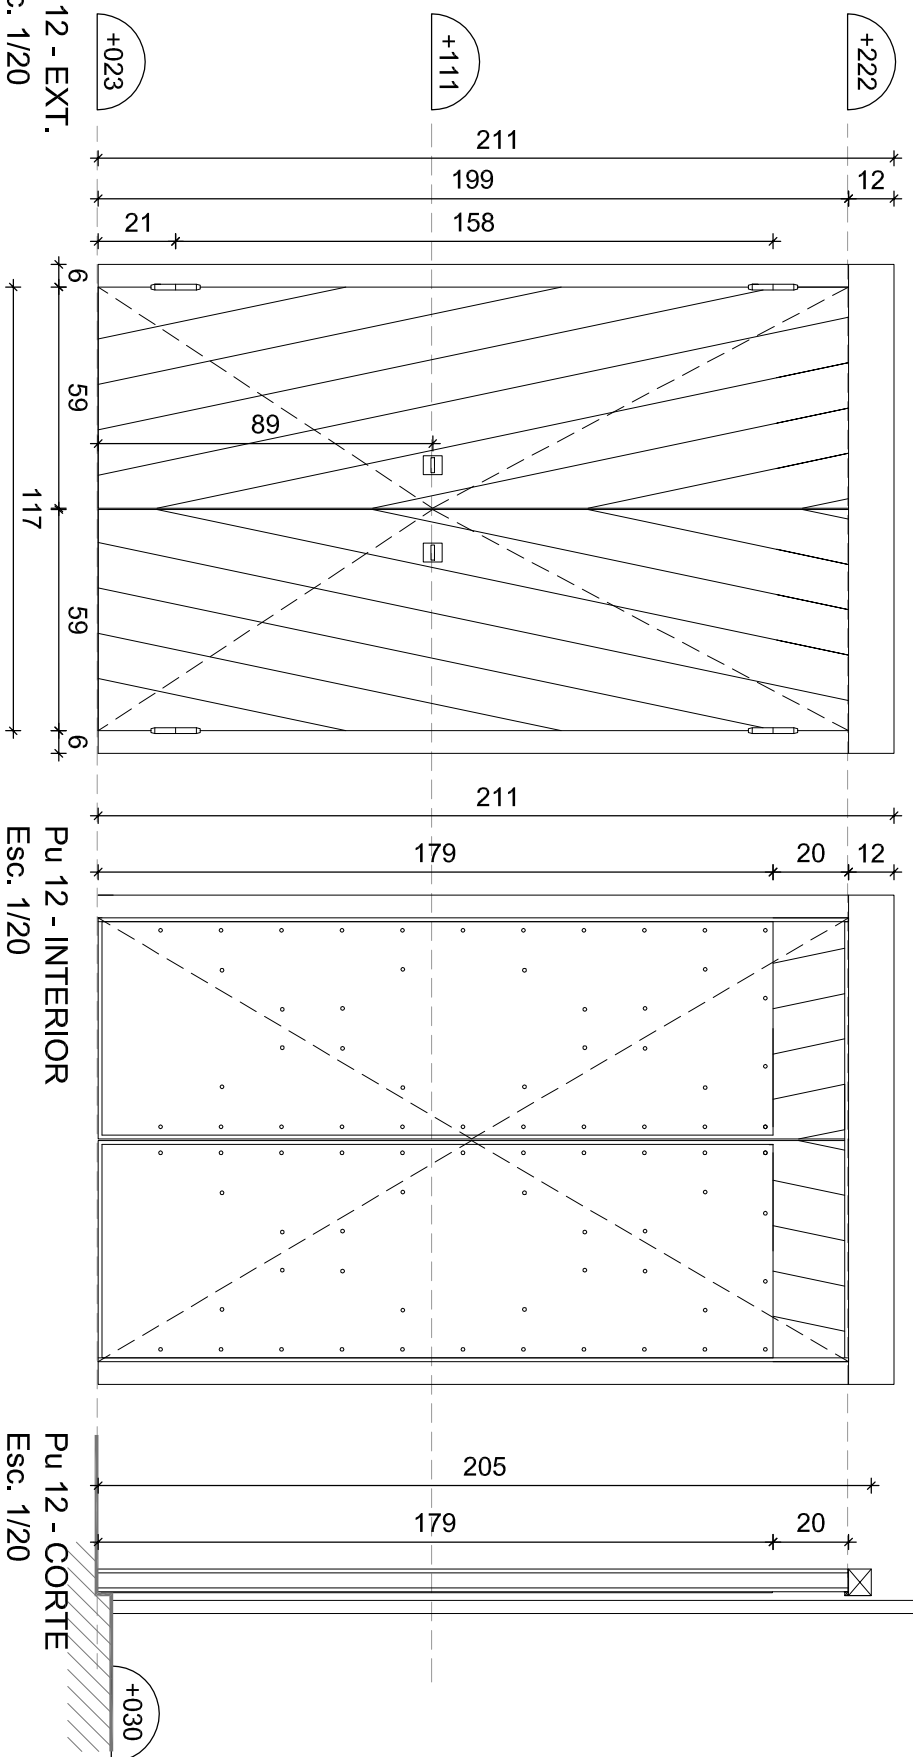


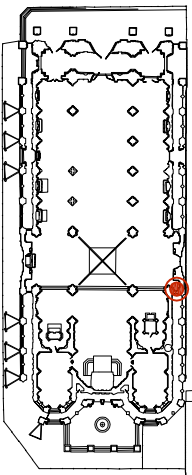Ubicación				
				
		PROYECTO		
DIRECCIÓN DE ARQUITECTURA DIRECCIÓN REGIONAL METROPOLITANA			Arqto. Dino Bozzi F. TÁNDEM Limitada contacto@tandemlimitada.cl	
PROYECTO: REPARACIÓN PARCIAL BASÍLICA DEL SALVADOR STGO				
BASÍLICA DEL SALVADOR Huérfanos 1796 - Santiago Región Metropolitana		ES Pu 11-12		
LEVANTAMIENTO Puertas 11 y 12 - transepto		1/25	Ago. 13	
		Escala	Fecha	
TD 1305	LEV	DET -	A	
Emisor Proyecto	Fase	Tipo	Zona	Índice
Dibujó: DS Controló: VI Archivo de ref.: TD_1212_LEV_ES_Pu-01-26_c.dwg				

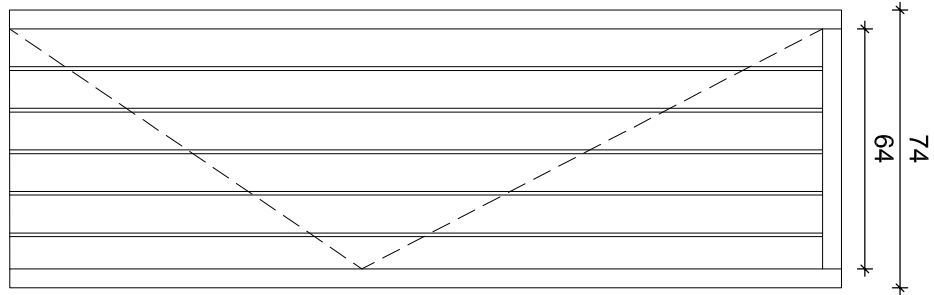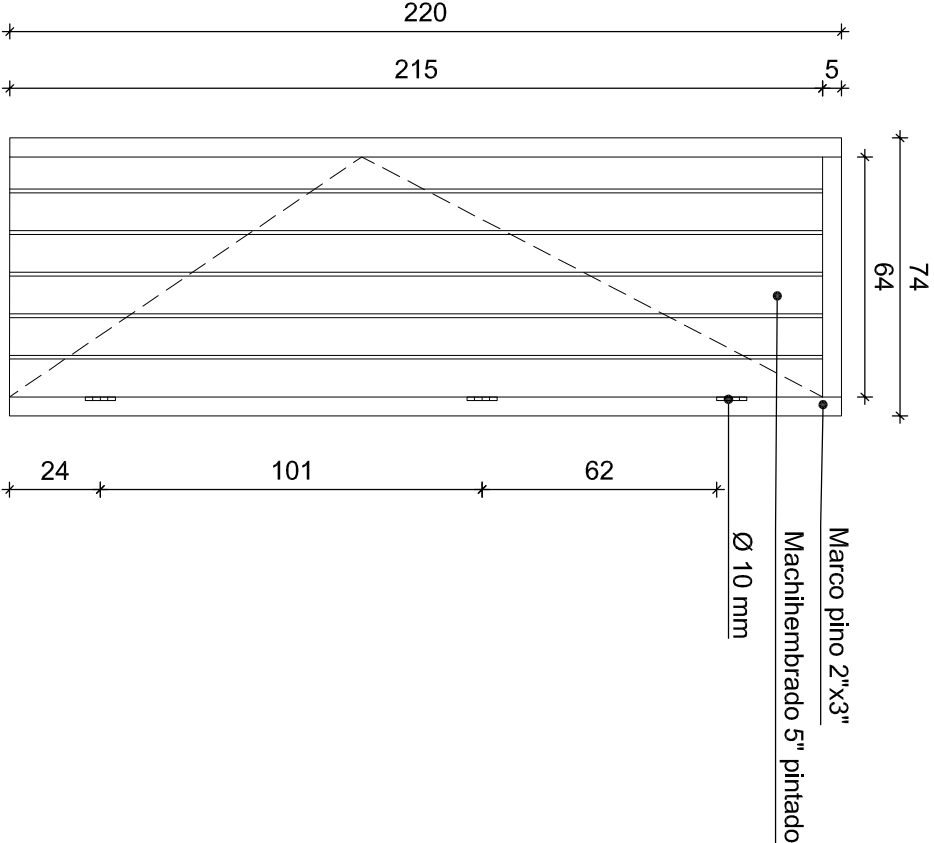


ELEVACIÓN EXTERIOR
Esc. 1/20

ELEVACIÓN INTERIOR
Esc. 1/20

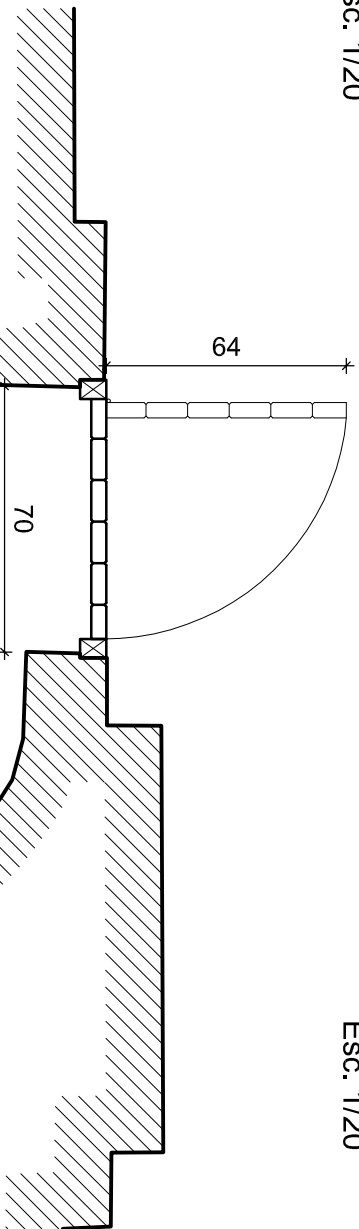


PLANTA
Esc. 1/20

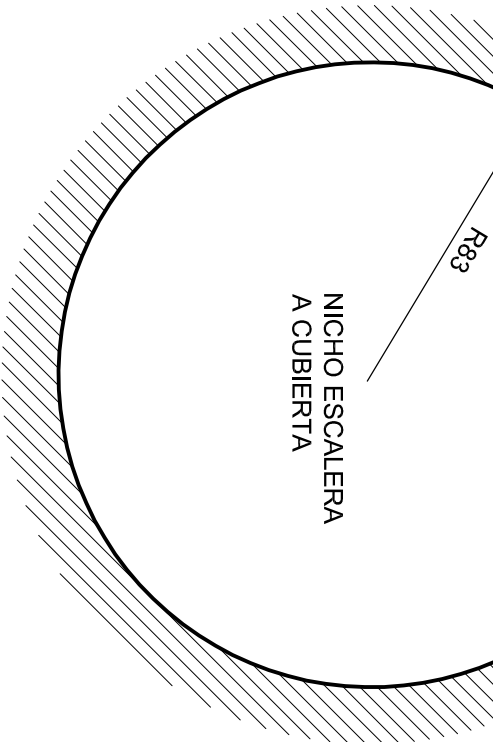


Fotografía

Ubicación					
			PROYECTO		
DIRECCIÓN DE ARQUITECTURA DIRECCIÓN REGIONAL METROPOLITANA			Arqto. Dino Bozzi F. TÁNDEM Limitada contacto@tandemlimitada.cl		
PROYECTO: REPARACIÓN PARCIAL BASÍLICA DEL SALVADOR STGO					
BASÍLICA DEL SALVADOR				ES	
Huérfanos 1796 - Santiago Región Metropolitana				Pu-13	
LEVANTAMIENTO			1/20		Ago. 13
Puerta 13 - nicho escalera			Escala		Fecha
TD	TD	LEV	DET	-	A
Emisor	Proyecto	Fase	Tipo	Zona	Índice
Dibujó: DS Controló: VI Archivo de ref.: TD_1212_LEV_ES_Pu-01-26_c.dwg					

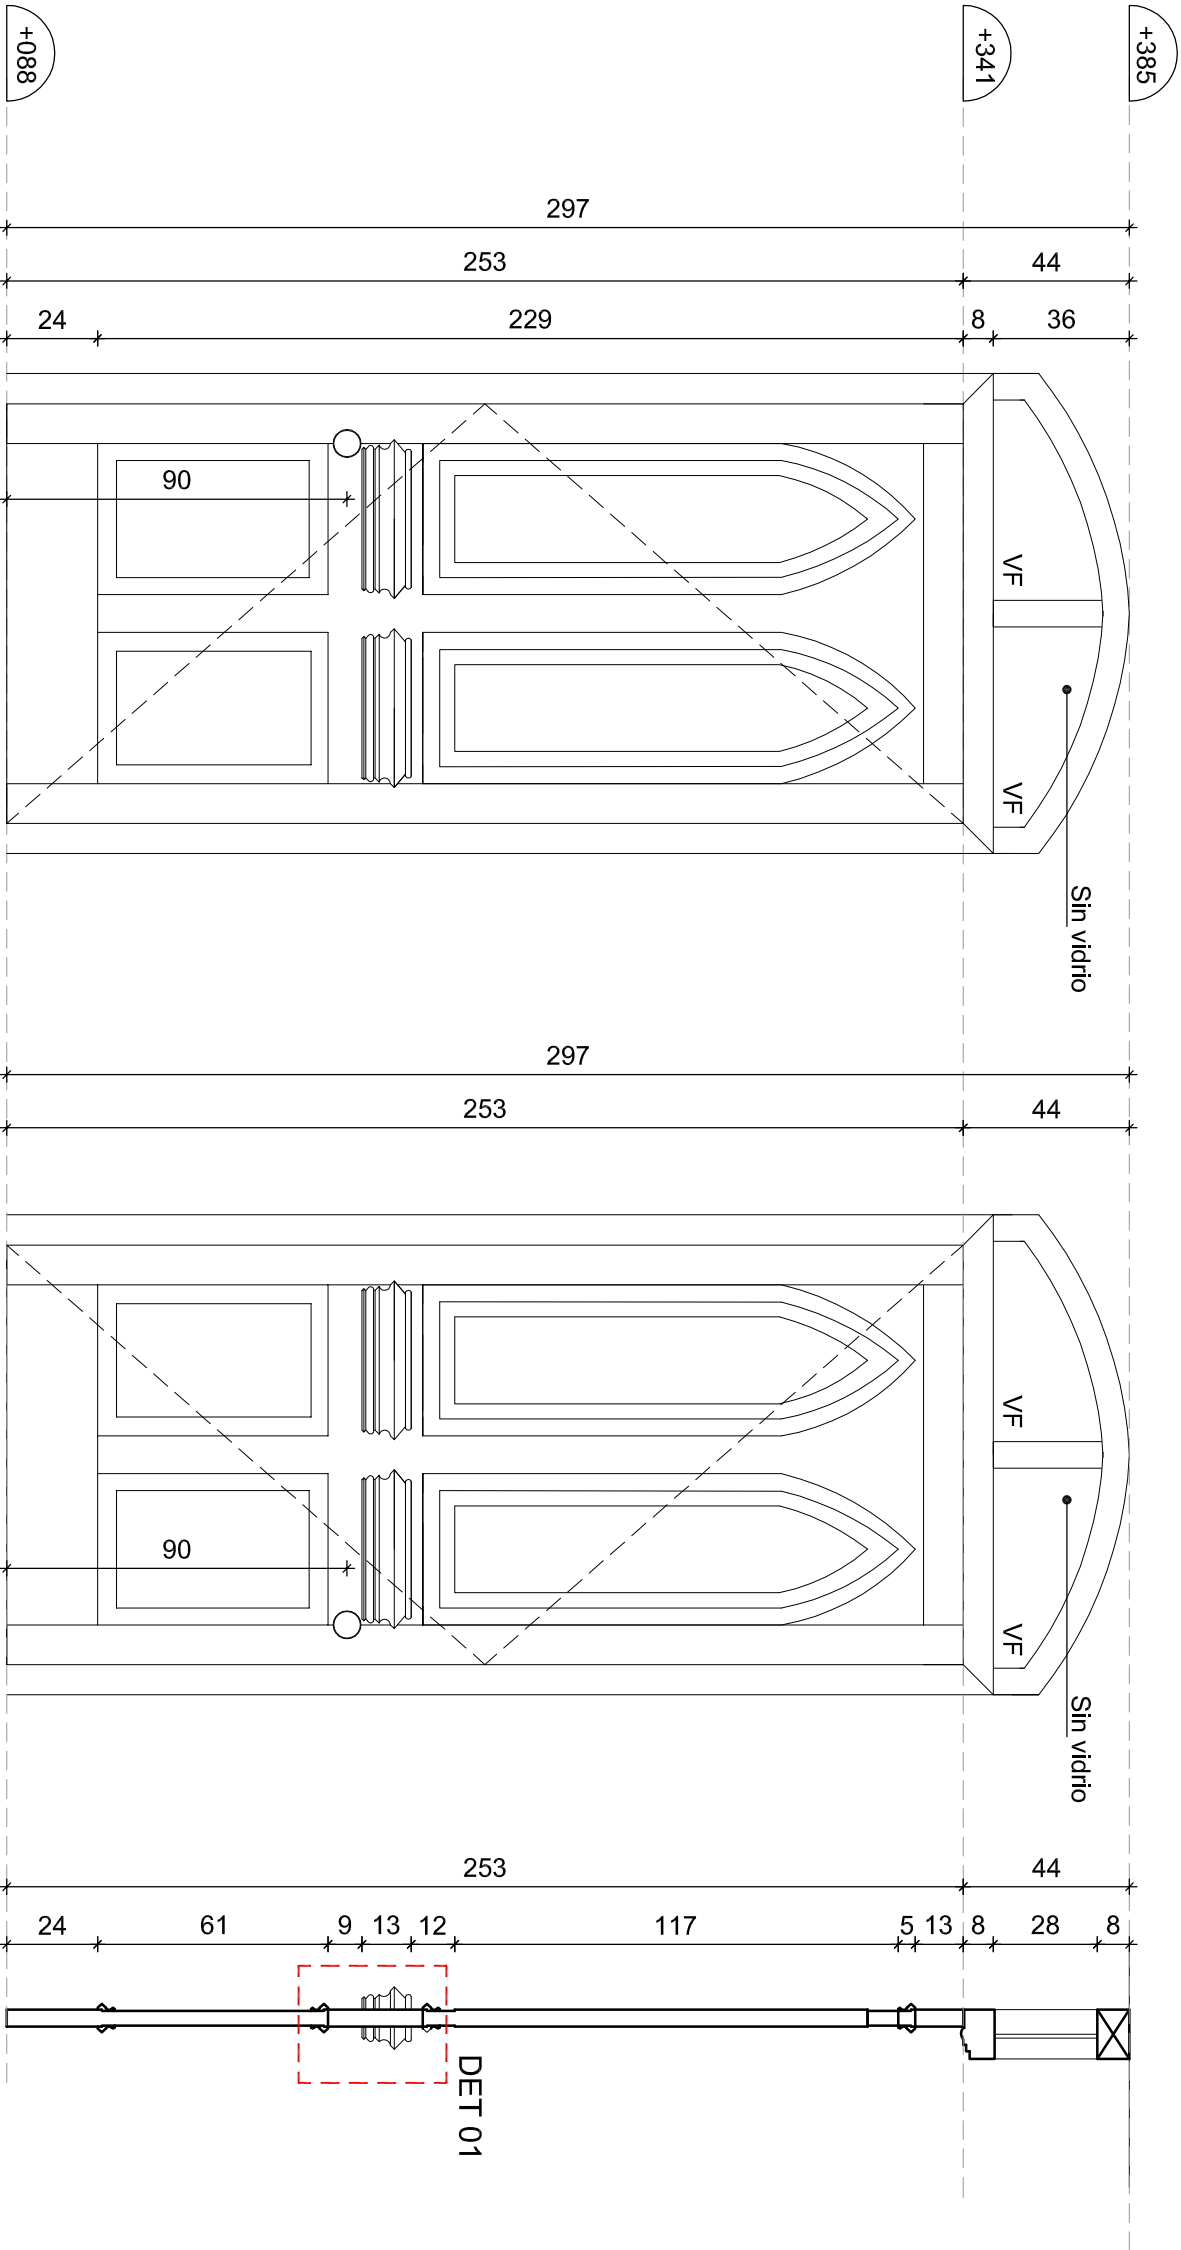

Fotografía

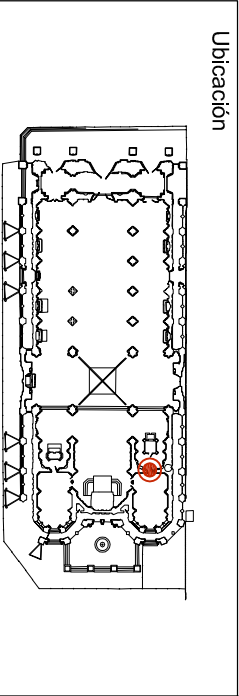

**Dirección de
Arquitectura**
Ministerio de Obras
Públicas
Gobierno de Chile

PROYECTO

Arqto. Dino Bozzi F.
TÁNDEM Limitada
contacto@tandemlimitada.cl

DIRECCIÓN DE ARQUITECTURA
DIRECCIÓN REGIONAL METROPOLITANA

PROYECTO: REPARACIÓN PARCIAL BASÍLICA DEL
SALVADOR STGO

BASÍLICA DEL SALVADOR



Huérfanos 1796 - Santiago
Región Metropolitana


ES

LEVANTAMIENTO				1/20	Ago. 13
Puerta 14 - Altar Virgen				Escala	Fecha
TD	TD	LEV	DET	-	A
Emisor	Proyecto	Fase	Tipo	Zona	Índice
Dibuj: DS	Contini: VI	Archivo de ref.: TD_1212_LEV_ES_Pu-01-286_c.dwg			





Fotografía

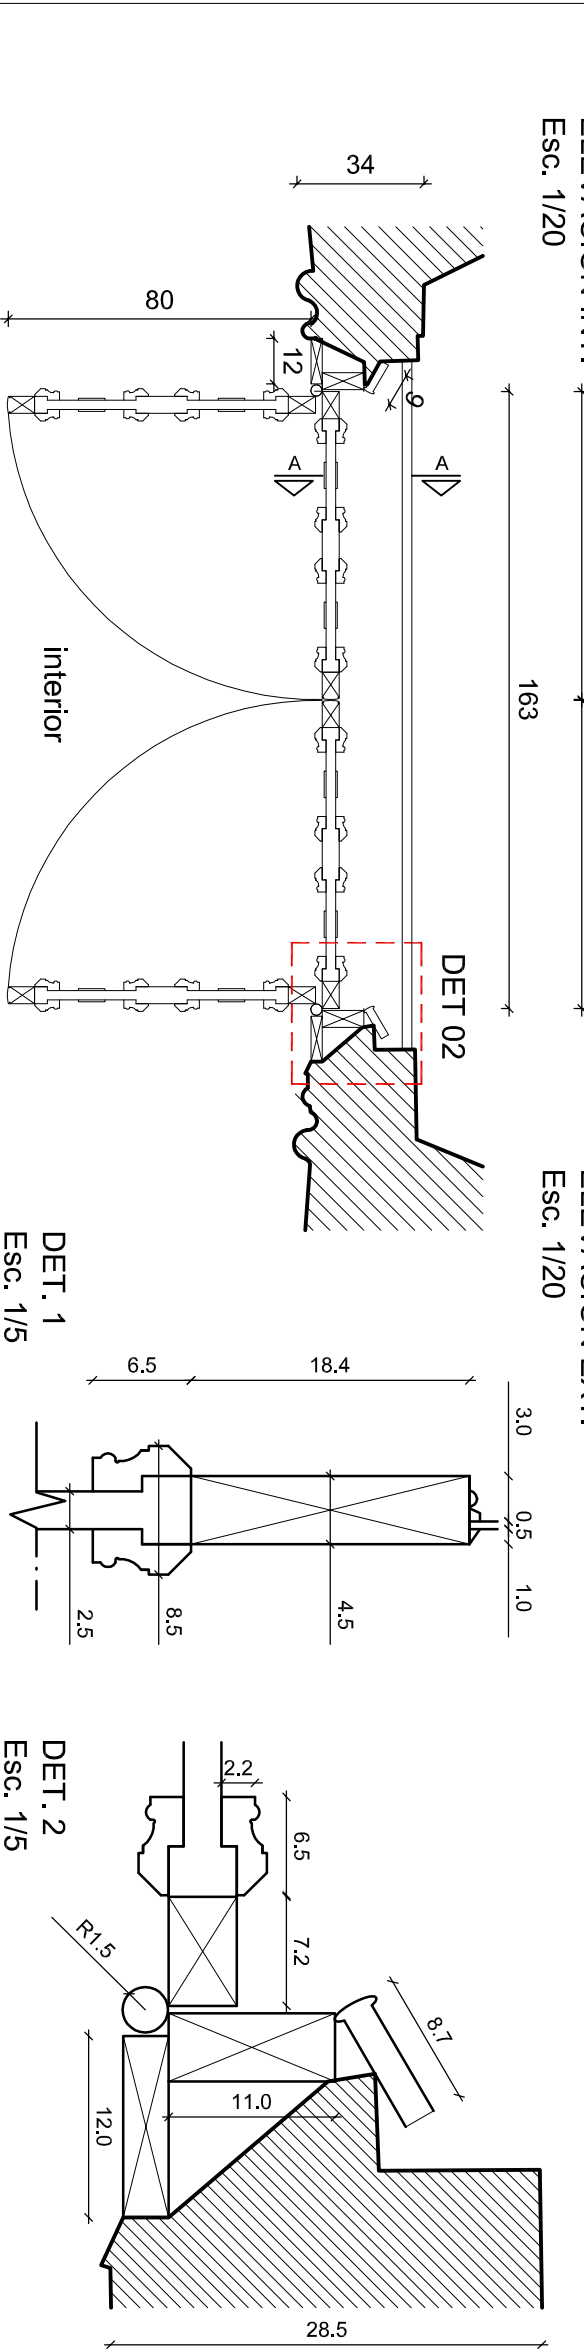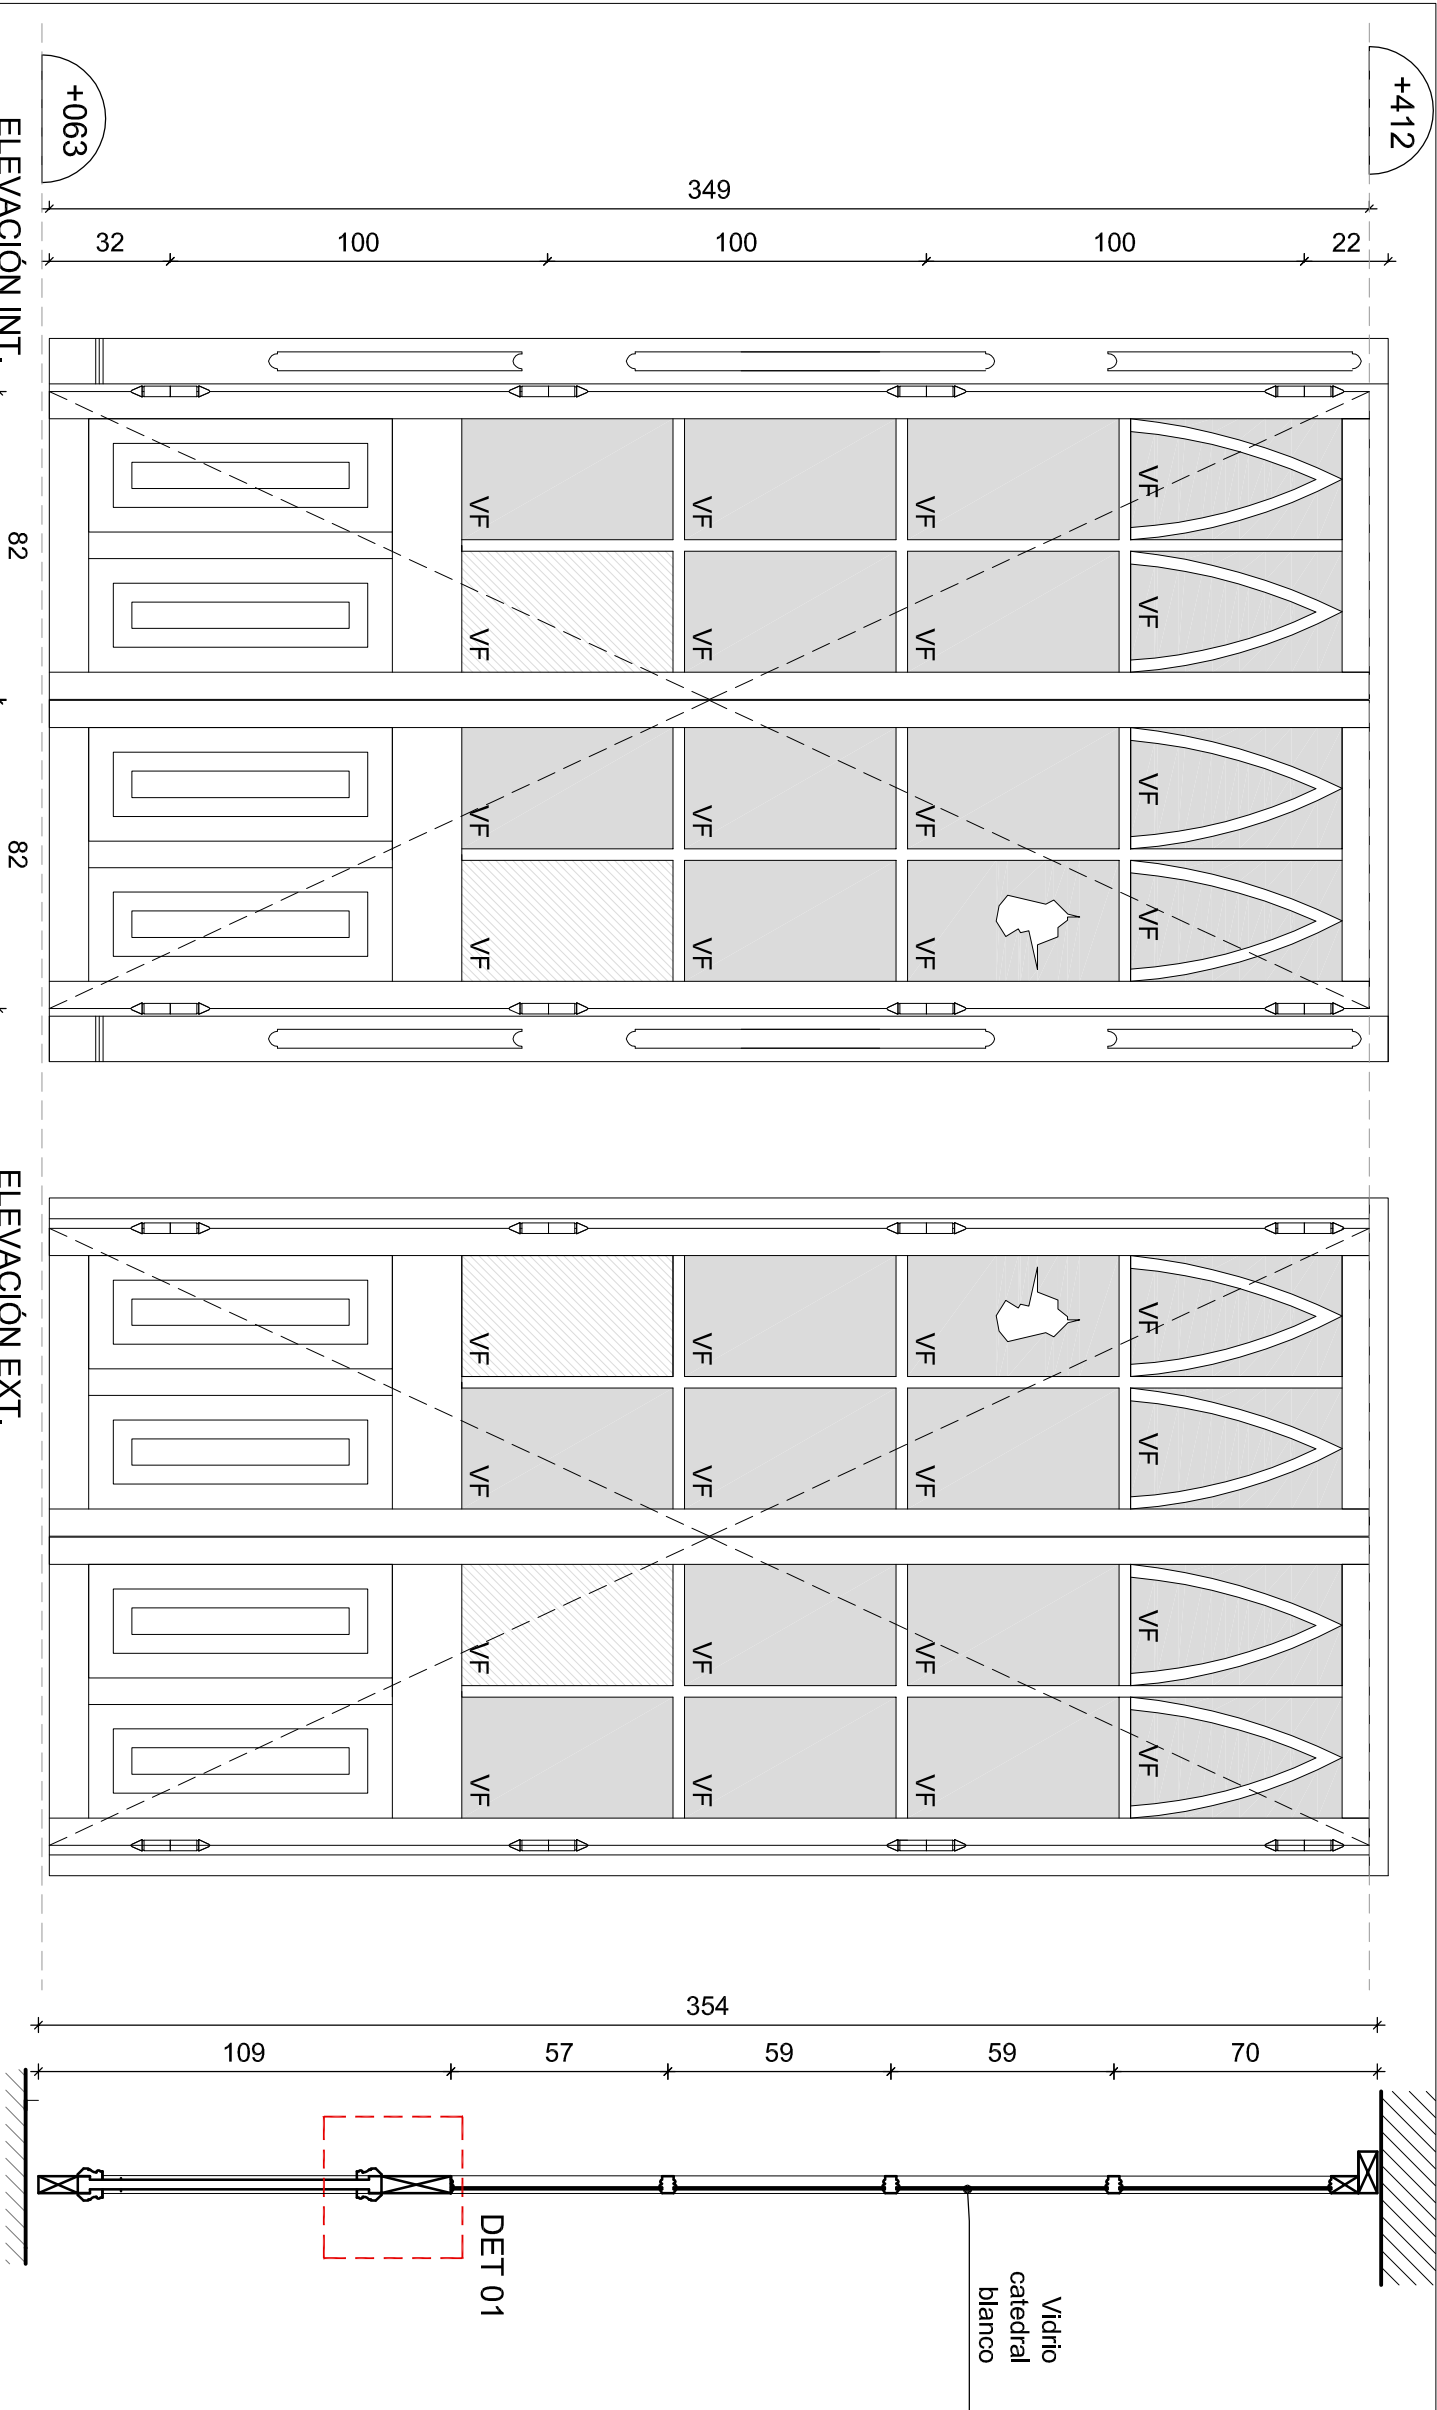


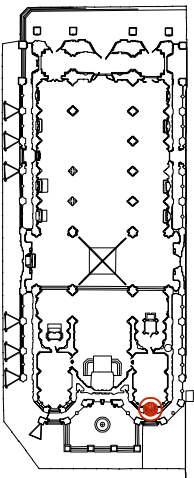
Ubicación								
								
PROYECTO			PROYECTO					
			Arqto. Dino Bozzi F. TÁNDEM Limitada contacto@tandemlimitada.cl					
DIRECCIÓN DE ARQUITECTURA DIRECCIÓN REGIONAL METROPOLITANA								
PROYECTO: REPARACIÓN PARCIAL BASÍLICA DEL SALVADOR STGO								
BASÍLICA DEL SALVADOR								
Huérfanos 1796 - Santiago Región Metropolitana				Pu-15				
LEVANTAMIENTO			1/20					
Puerta 15 - Capilla oriente			Escala					
TD	TD	LEV	DET	-	A			
Emisor	Proyecto	Fase	Tipo	Zona	Índice			
Dibuj: DS Control: VI Archivo de ref.: TD_1212_LEV_ES_Pu-01-286_c04mg								



Fotografía puerta tipo

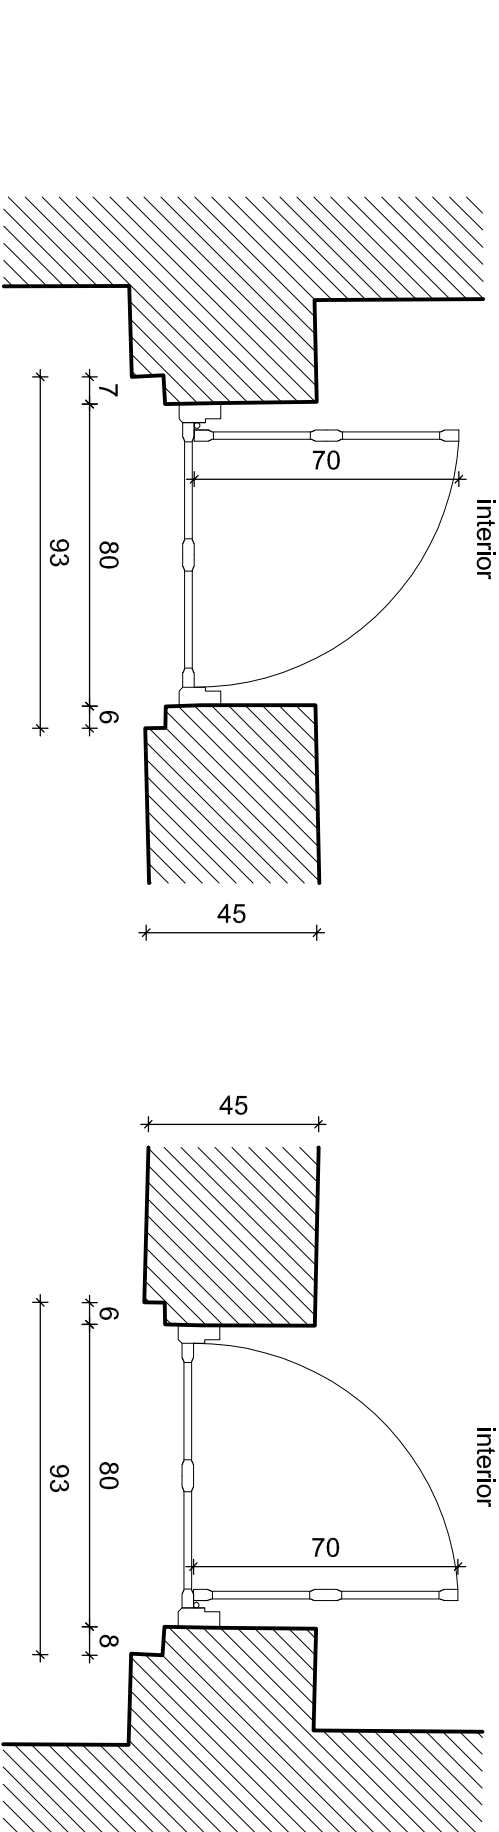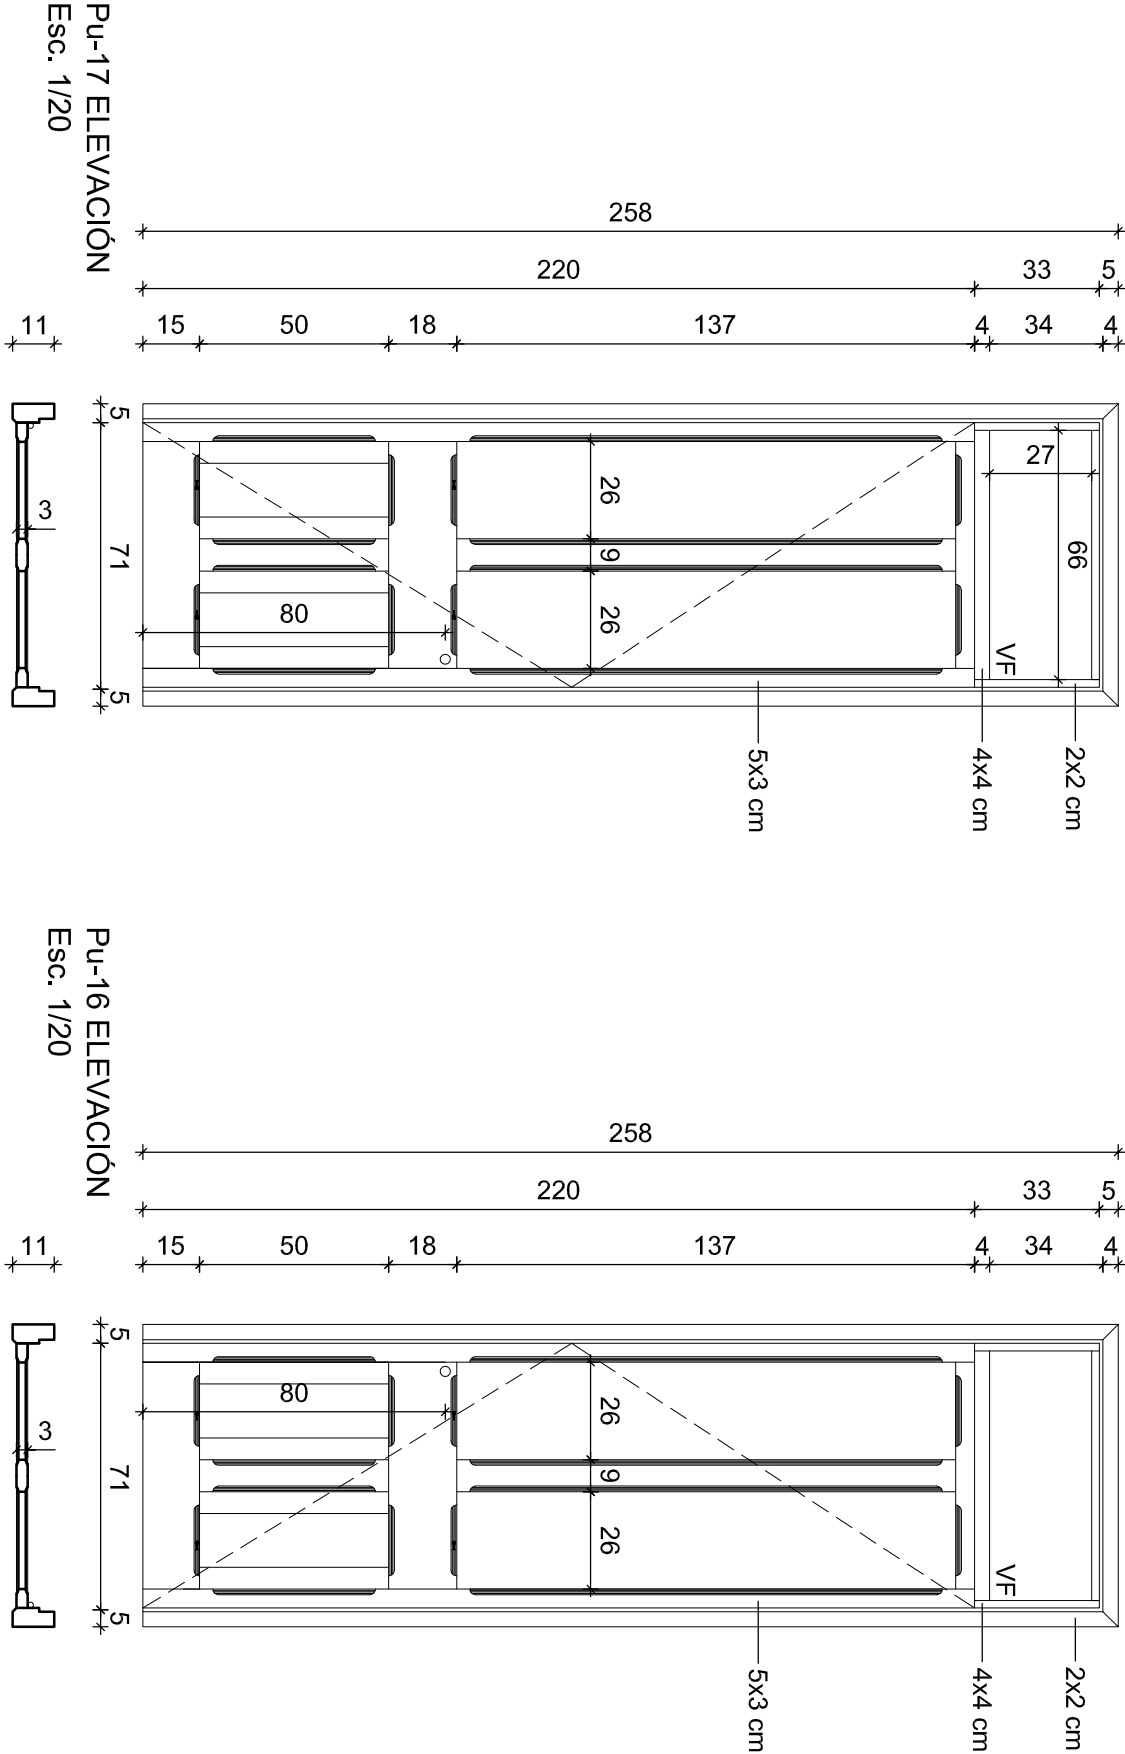


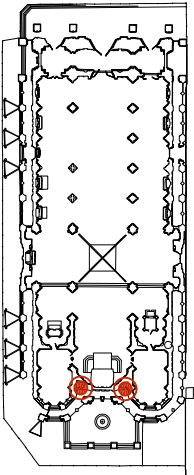Ubicación				
				
PROYECTO			PROYECTO	
 Dirección de Arquitectura Ministerio de Obras Públicas Gobierno de Chile			Arqto. Dino Bozzi F. TÁNDEM Limitada contacto@tandemlimitada.cl	
DIRECCIÓN DE ARQUITECTURA DIRECCIÓN REGIONAL METROPOLITANA				
PROYECTO: REPARACIÓN PARCIAL BASÍLICA DEL SALVADOR STGO				
BASÍLICA DEL SALVADOR			ES Pu 16-17	
Huérfanos 1796 - Santiago Región Metropolitana				
LEVANTAMIENTO			1/25	Ago. 13
Puertas 16 - 17 - baños ext.			Escala	Fecha
TD	TD 1305	LEV	DET	-
Emisor	Proyecto	Fase	Tipo	Zona
Índice			Índice	
Dibujó: DS Controló: VI Archivo de ref.: TD_1212_LEV_ES_Pu-01-26_c.dwg				

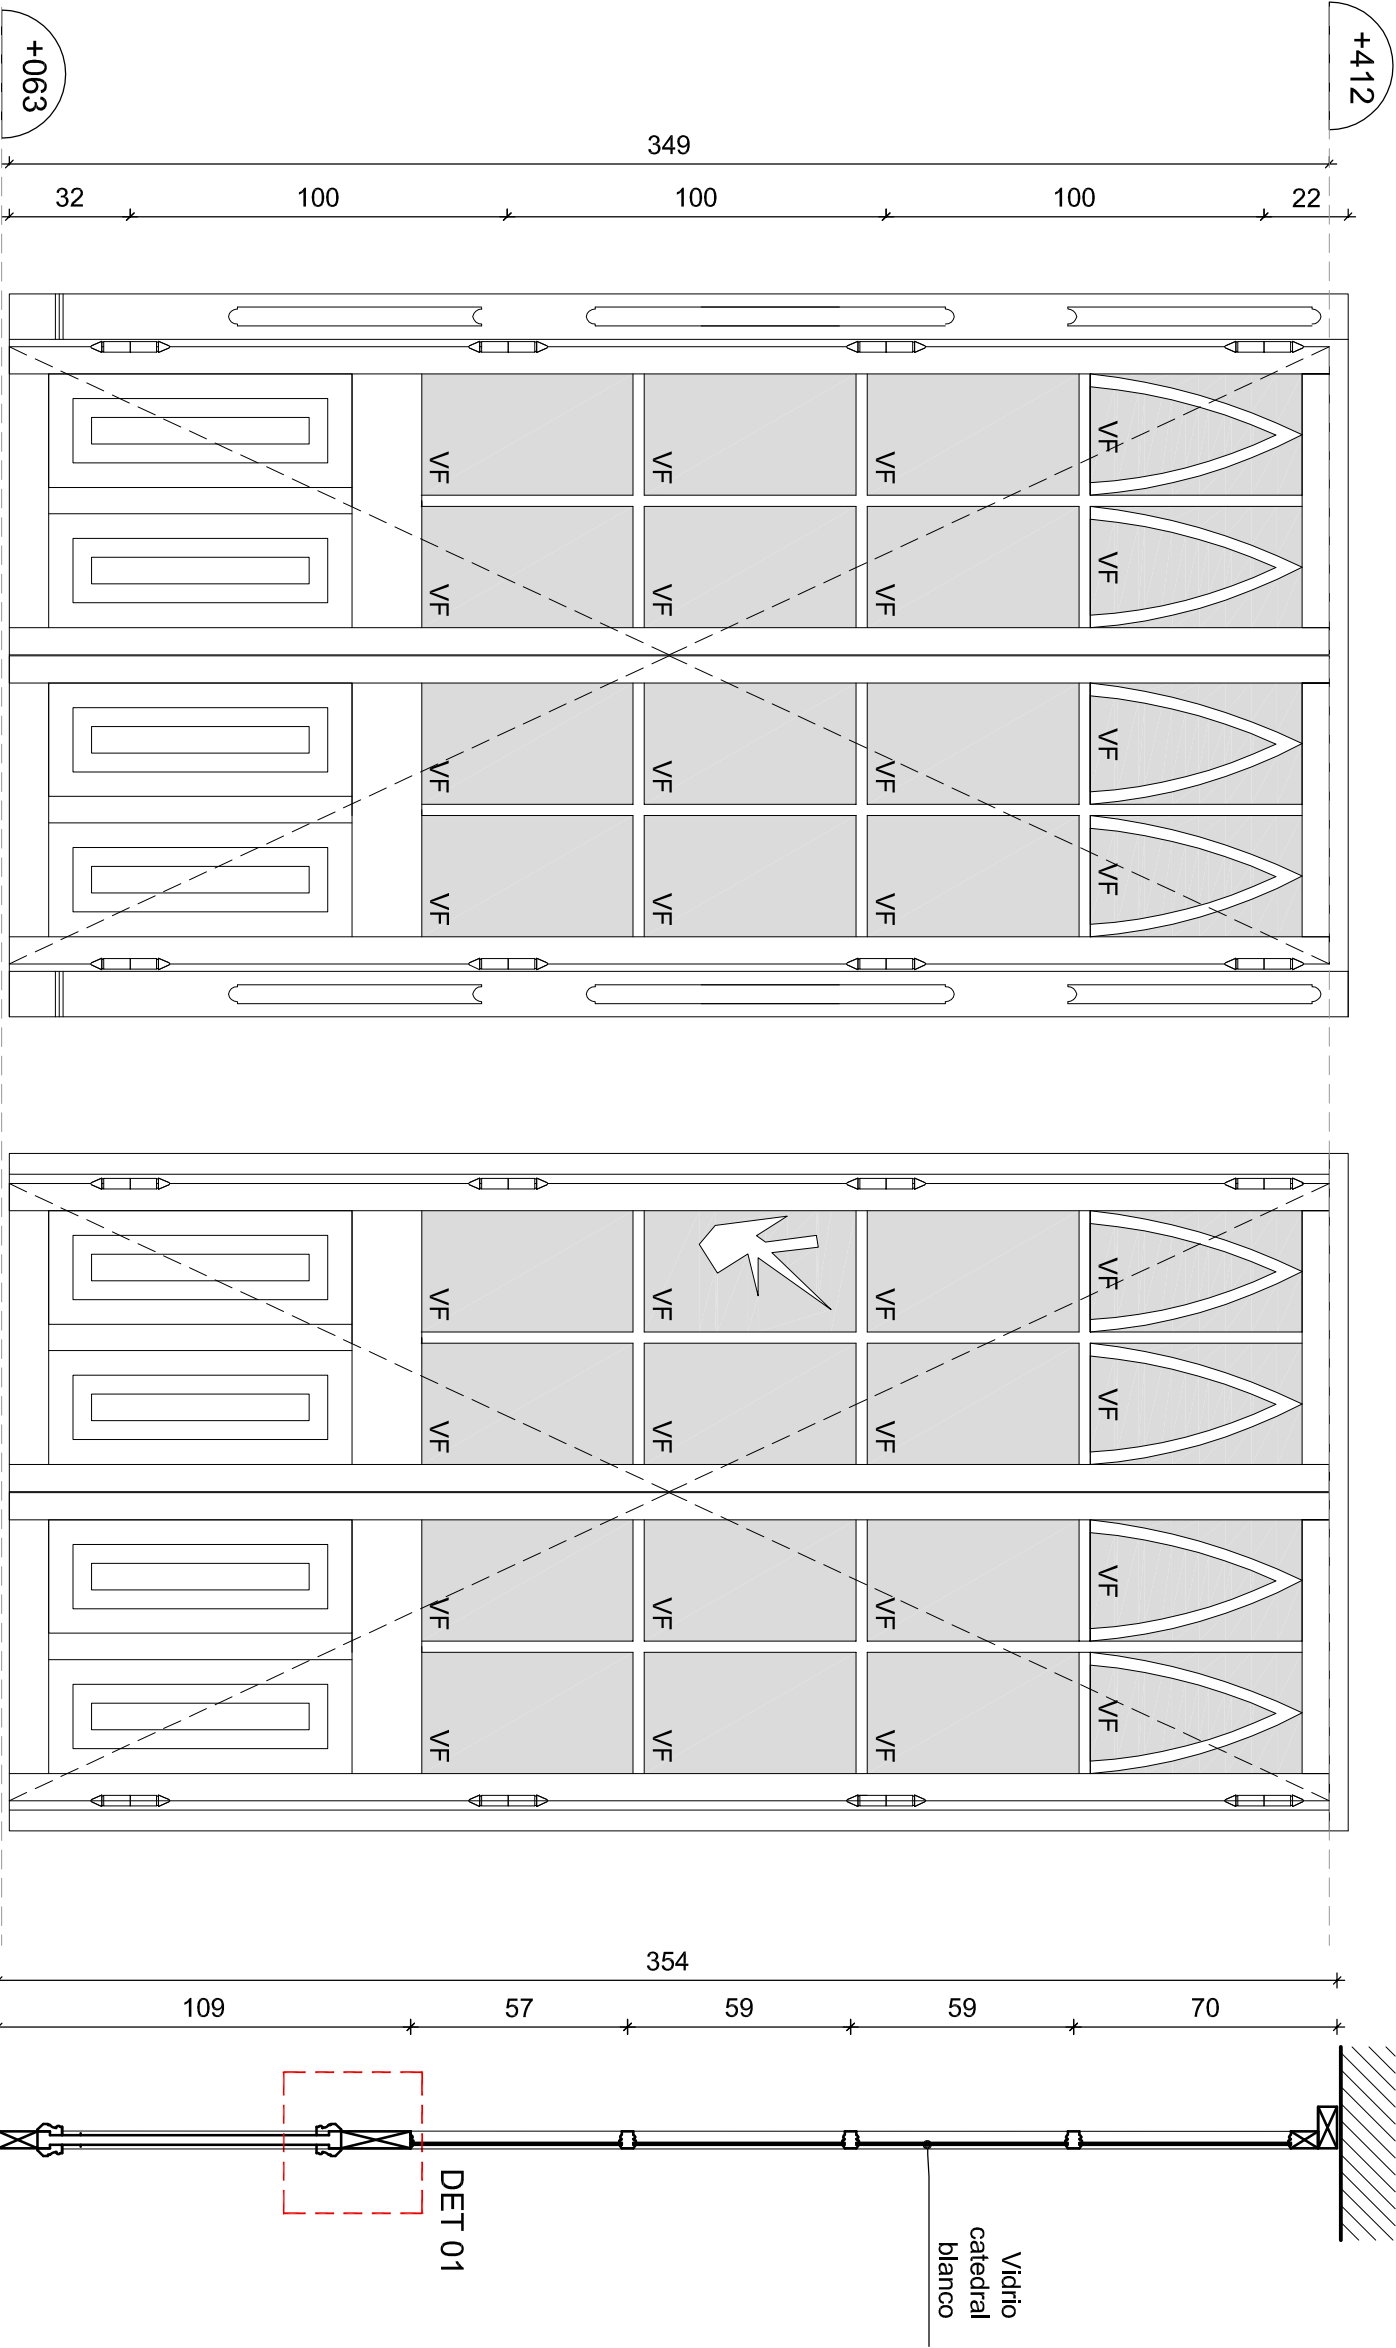


ELEVACIÓN INT.
Esc. 1/20

ELEVACIÓN EXT.
Esc. 1/20

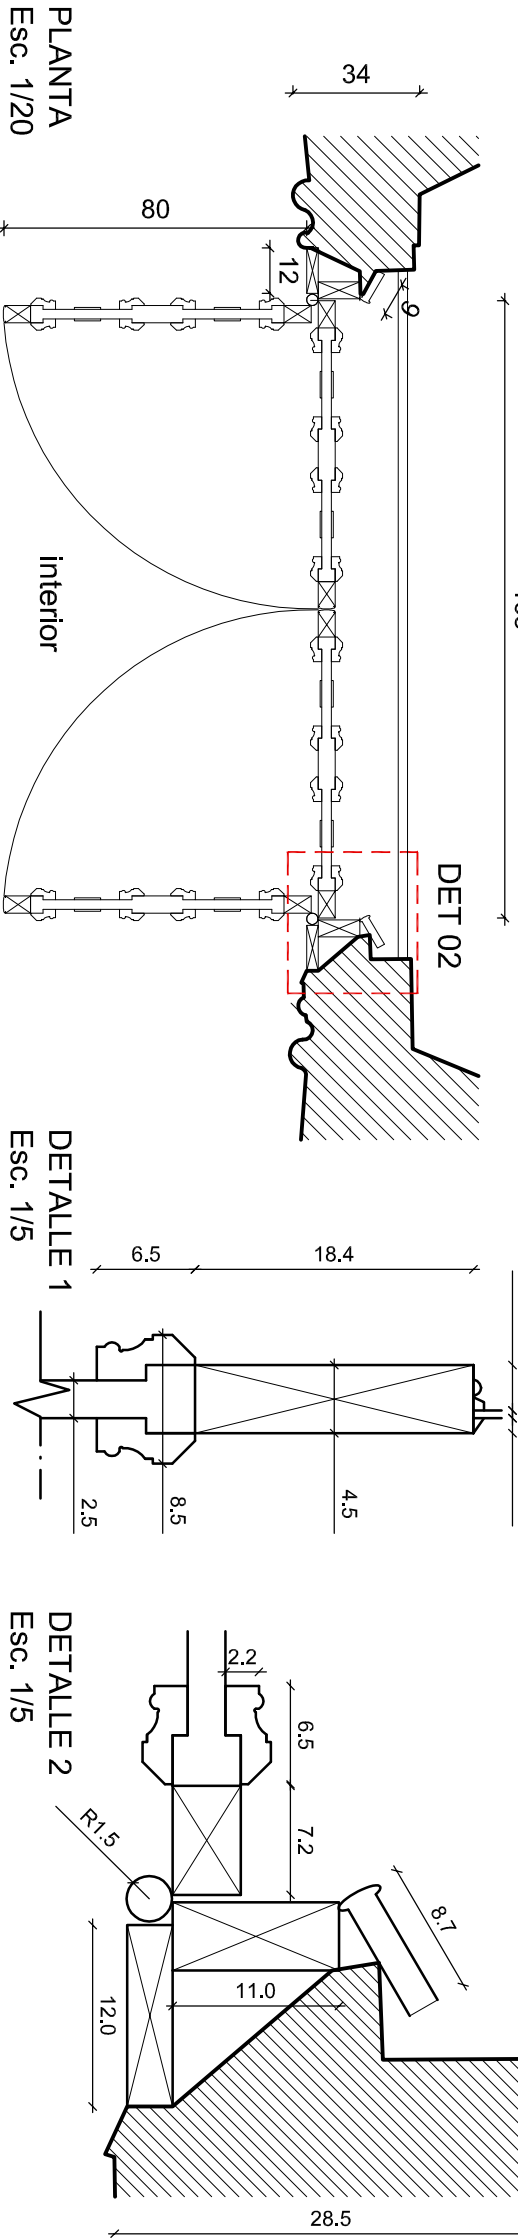

PLANTA
Esc. 1/20


DETALLE 1
Esc. 1/5

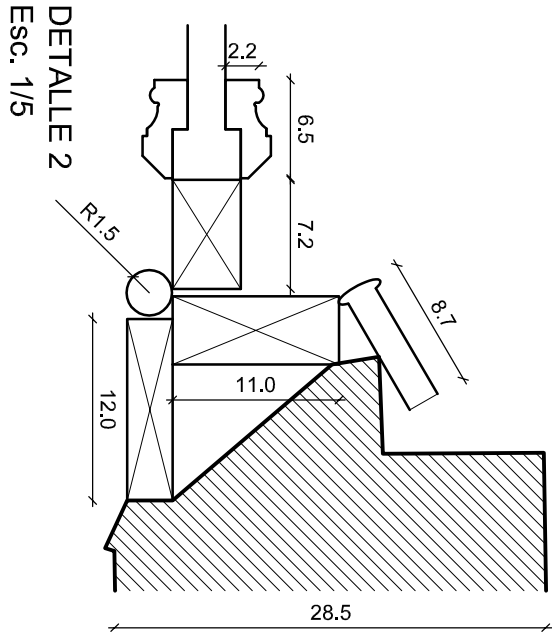


DETALLE 2
Esc. 1/5



Fotografía
Obs.: Puerta junto a derrumbe, clausurada.

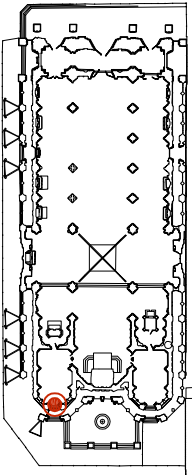
Ubicación									
									
					PROYECTO				
DIRECCIÓN DE ARQUITECTURA DIRECCIÓN REGIONAL METROPOLITANA					Argto. Dino Bozzi F. TÁNDEM Limitada contacto@tandemlimitada.cl				
PROYECTO: REPARACIÓN PARCIAL BASÍLICA DEL SALVADOR STGO									
BASÍLICA DEL SALVADOR					ES				
Huérfanos 1796 - Santiago Región Metropolitana					Pu-18				
LEVANTAMIENTO Puerta 18 - sacristía					1/25		Ago. 13		
Escala					Fecha				
TD	TD	LEV	DET	-	A		Índice		
Emisor	Proyecto	Fase	Tipo	Zona	Índice				
Obra: 05 Control: V1 Archivo de ref. TD_1212_LEV_ES_Pu-01-26_c.dwg									

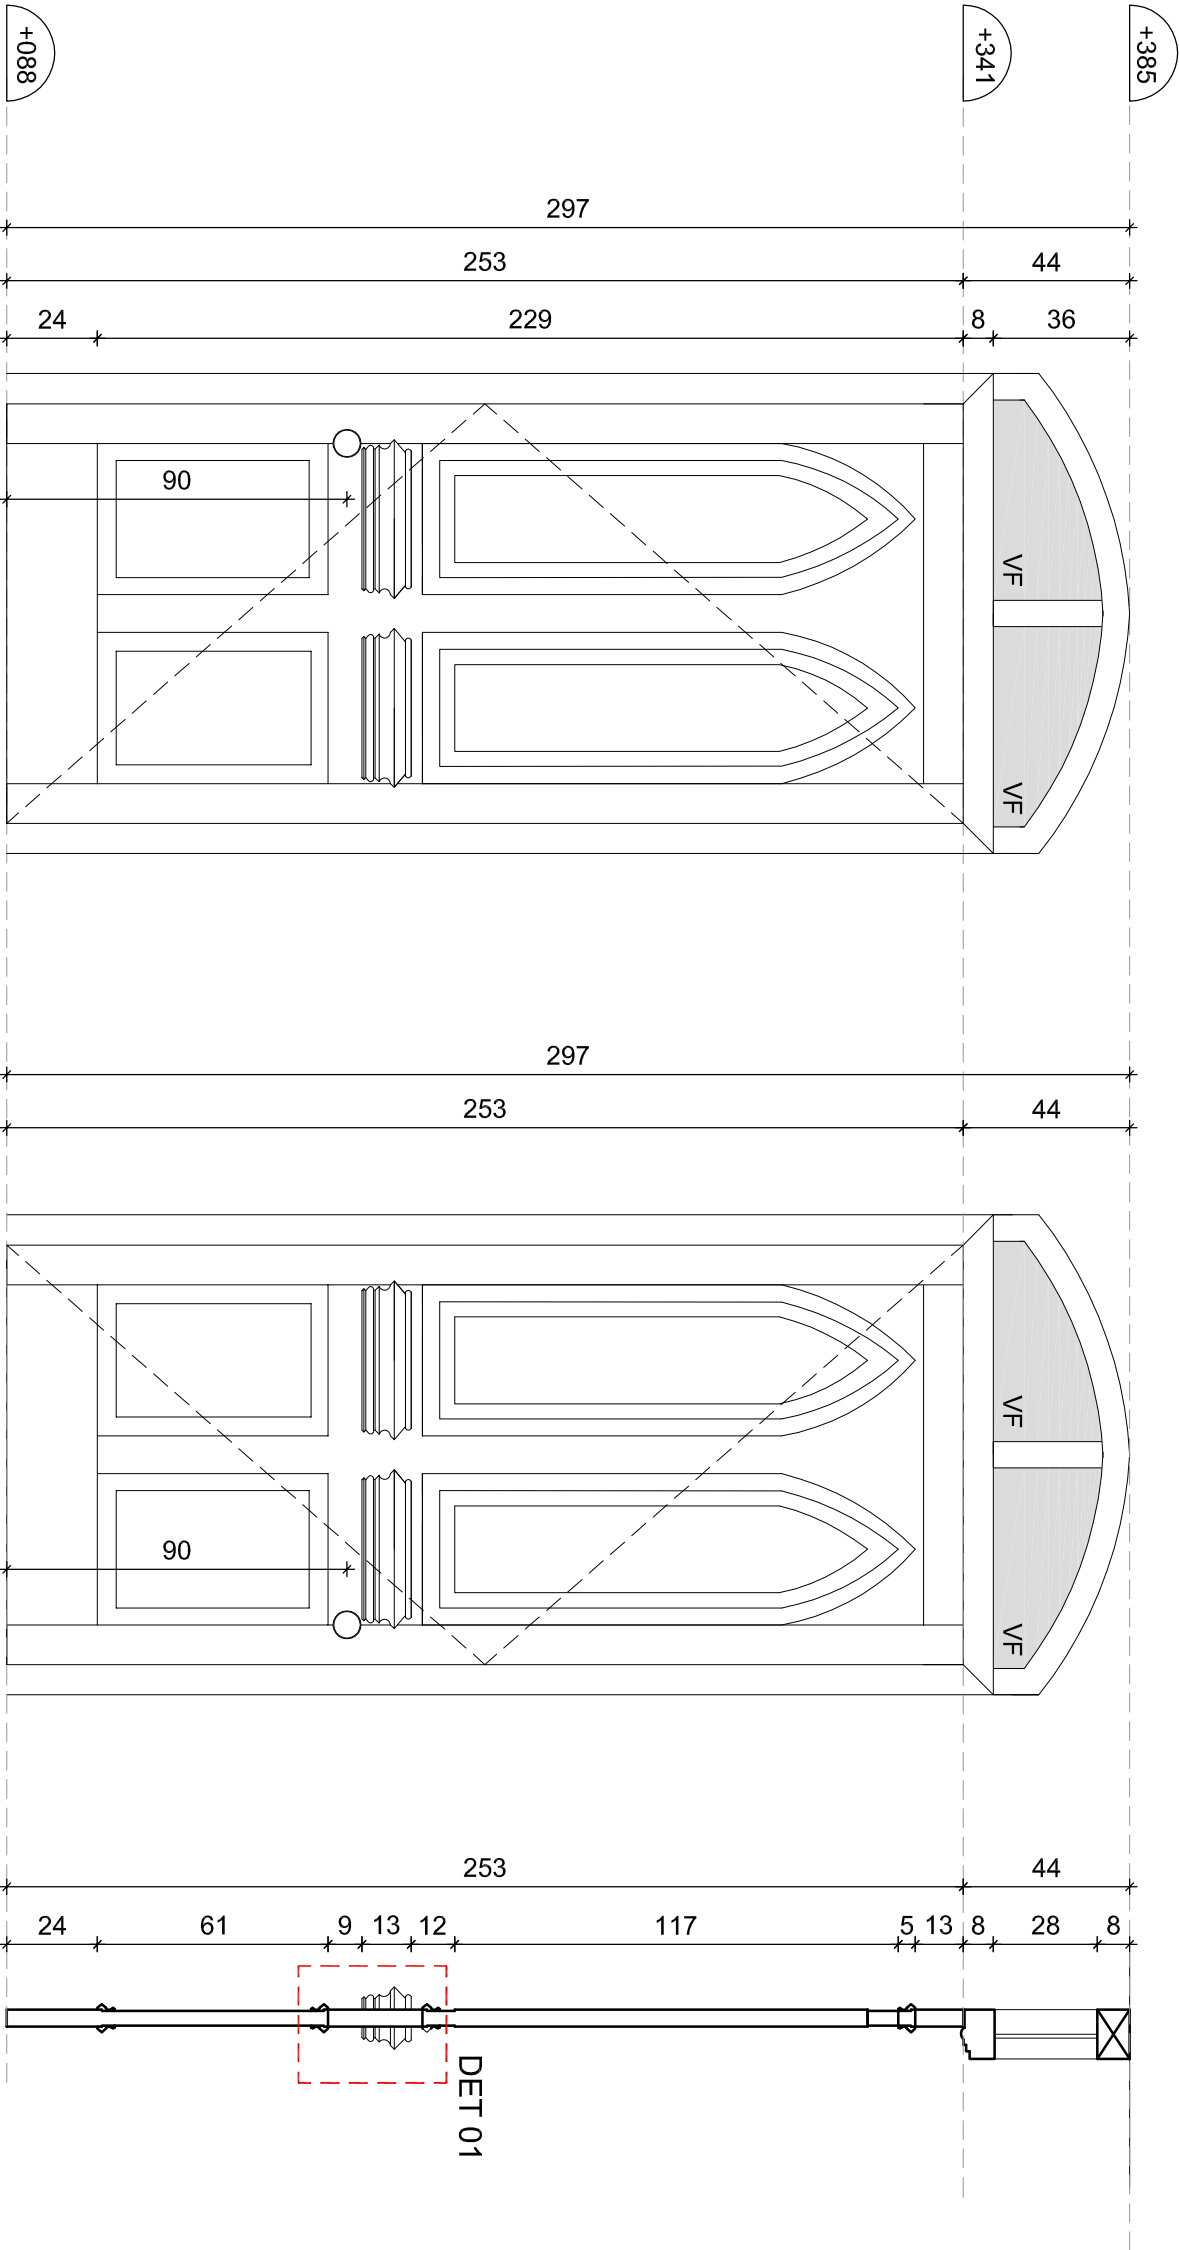


ELEVACIÓN INT.
Esc. 1/20

ELEVACIÓN EXT.
Esc. 1/20


CORTE
Esc. 1/20

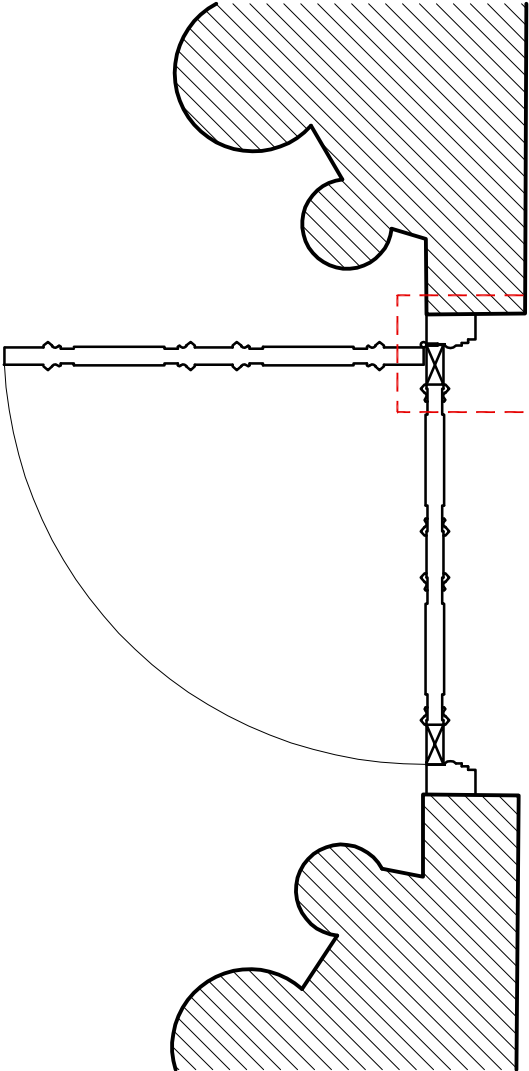


DET 02

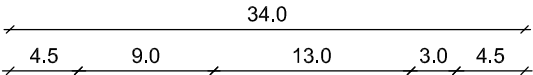

DETALLE 1

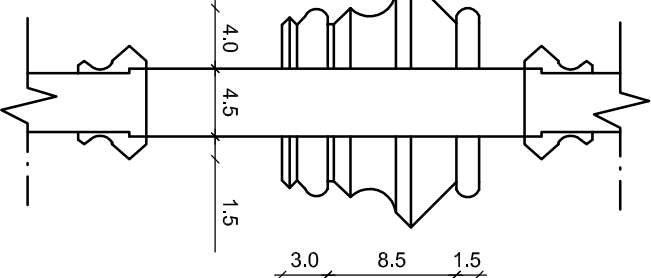


DETALLE 2

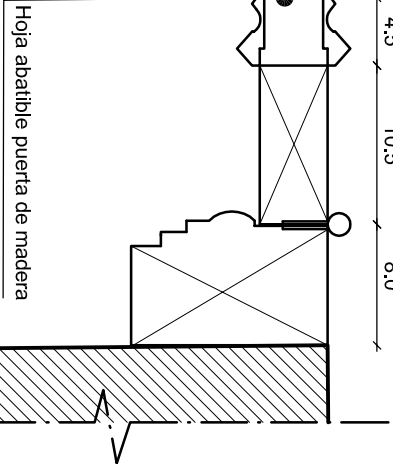

PLANTA
Esc. 1/20

DETALLE 1
Esc. 1/5

DETALLE 2
Esc. 1/5

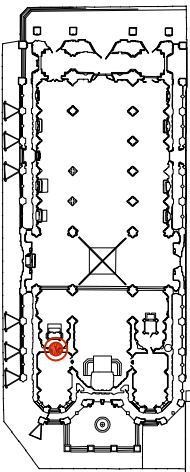Ubicación					
					
				PROYECTO	
DIRECCIÓN DE ARQUITECTURA DIRECCIÓN REGIONAL METROPOLITANA				Arqto. Dino Bozzi F. TÁNDEM Limitada contacto@tandemlimitada.cl	
PROYECTO: REPARACIÓN PARCIAL BASÍLICA DEL SALVADOR STGO					
BASÍLICA DEL SALVADOR				ES	
Huérfanos 1796 - Santiago Región Metropolitana				Pu-19	
LEVANTAMIENTO				1/20	Ago. 13
Puerta 19 - Altar San José				Escala	Fecha
TD	TD	LEV	DET	-	A
Emisor	Proyecto	Fase	Tipo	Zona	Índice
Dibujó: DS Controló: VI Archivo de ref.: TD_1212_LEV_ES_Pu-01-26_c.dwg					