


PLANTA BASILICA PRIMER PISO

ESC: 1 / 100 DISPOSICIÓN DE EQUIPOS Y CANALIZACIONES

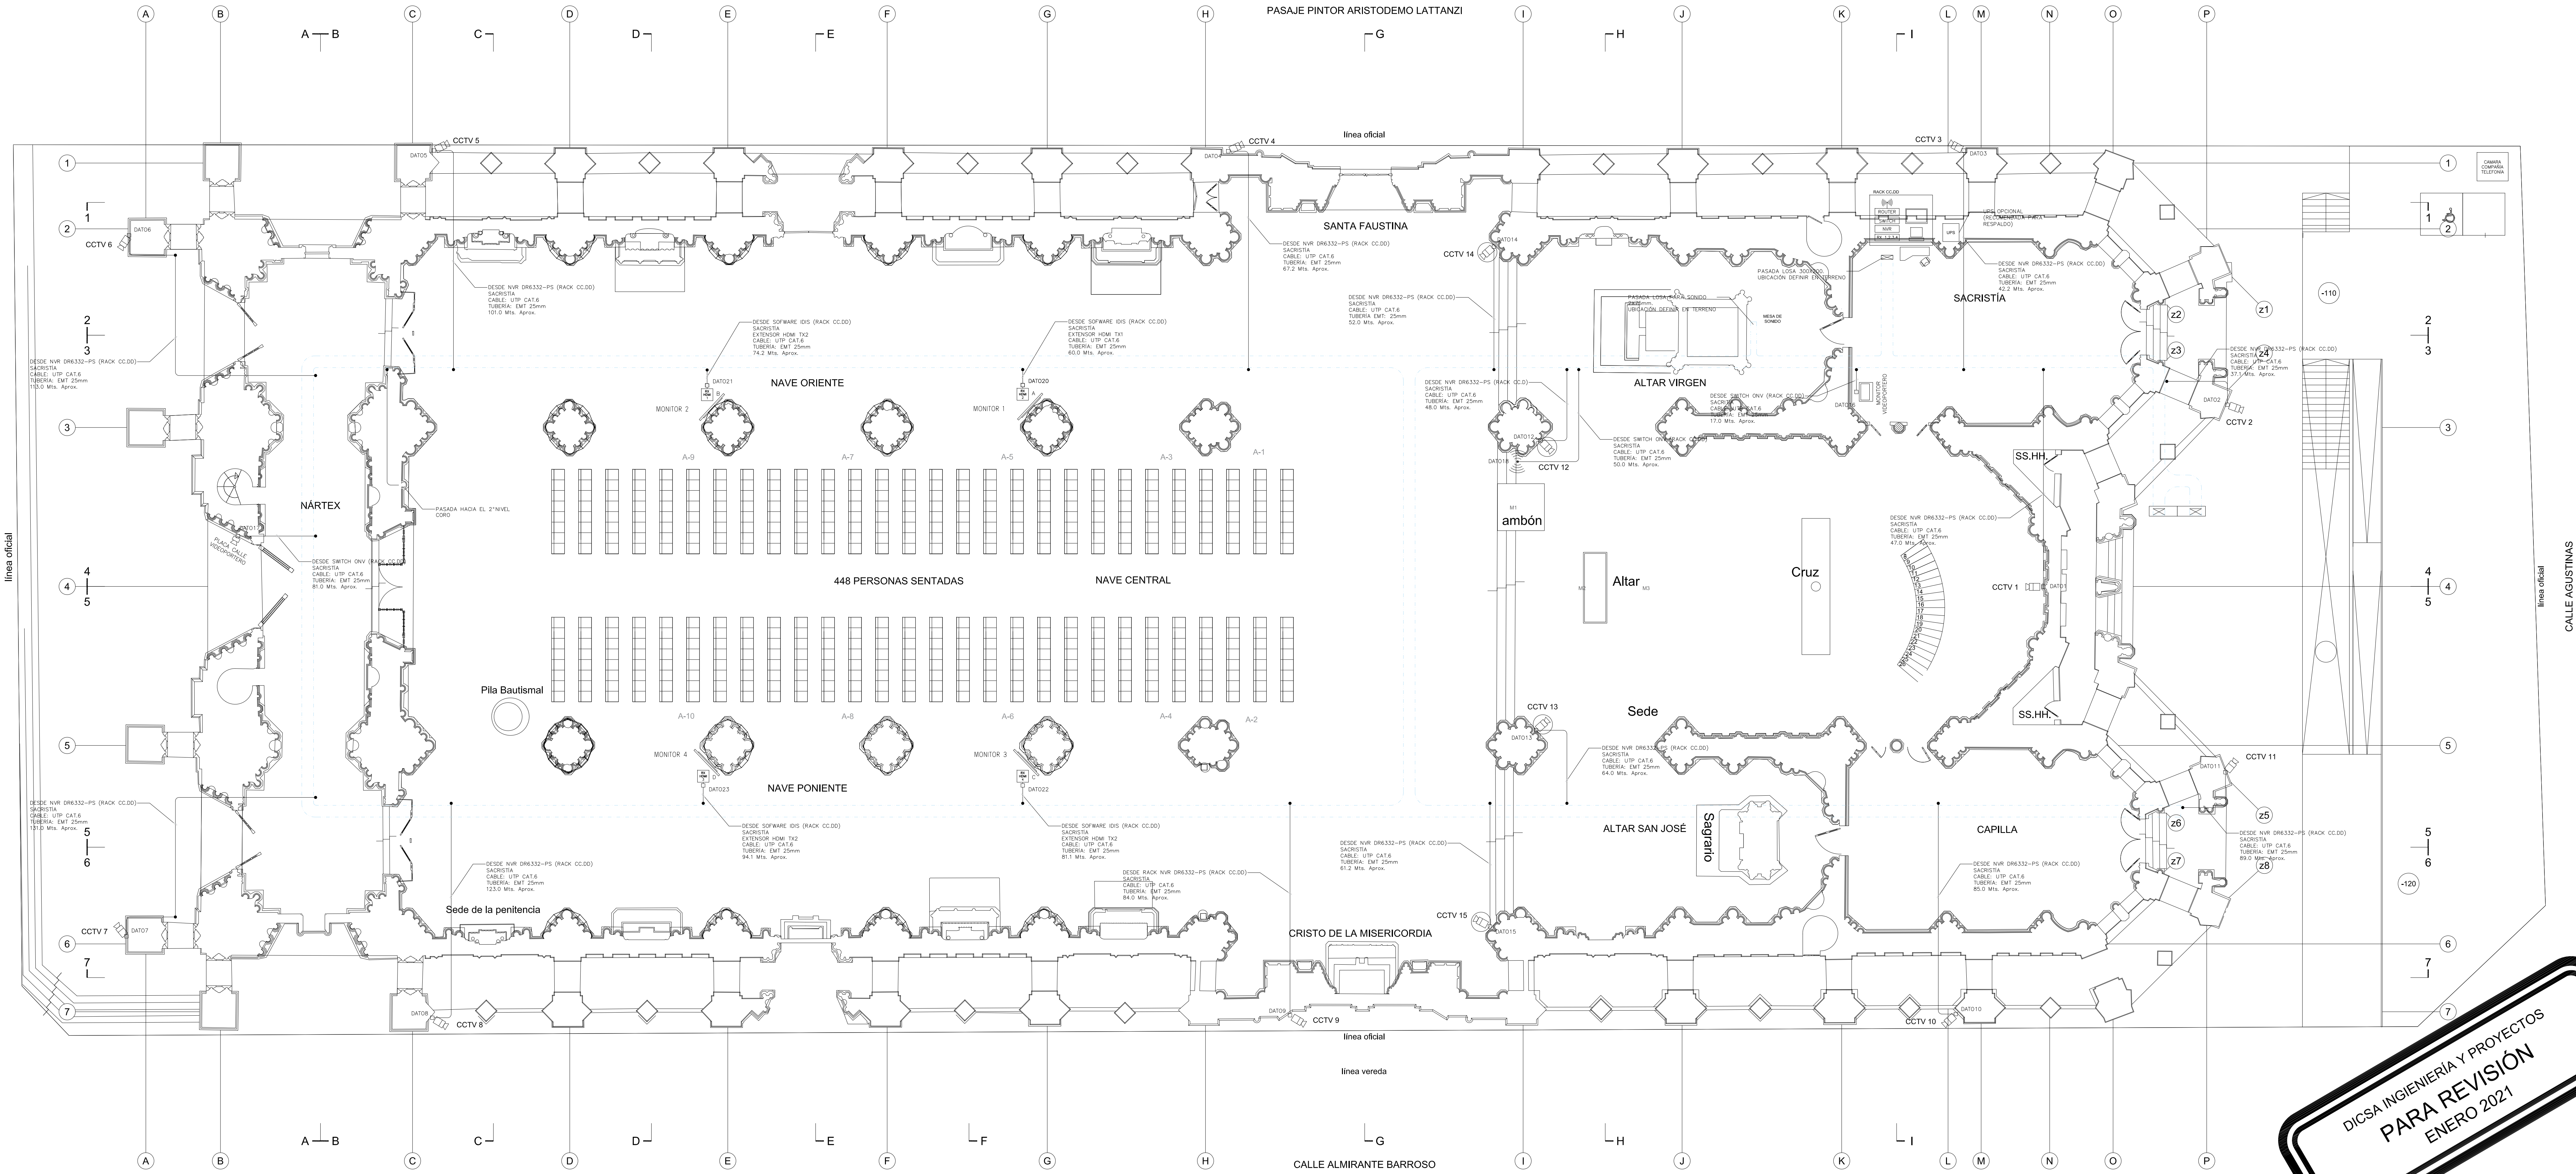

DICSA INGENIERÍA Y PROYECTOS
PARA REVISIÓN
ENERO 2021

CARACTERÍSTICAS DEL SISTEMA

SOFTWARE DE GESTIÓN (MOVIL O DESKTOP).

Visualización de video en vivo.
Visualización de grabaciones permite estudiar las imagenes registradas, para posteriormente analizarla, ya sea por personal de seguridad o apedido de las autoridades pertinentes.
Gestión de equipo de grabación (NVR), creación de usuarios para la gestión del monitoreo.

NVR (DR-4316PS).

Rendimiento total entrante 320 Mbps.
Grabación en tiempo real de hasta 480ips UHD.
Admite Códec H.265 / H.264.
Admite pantalla UHD.
Pantalla en vivo de hasta 480ips.
Fácil de instalar, configurar y reproducir con cámaras DirecIP.
Conmutador PoE de 32 canales incorporado.
Admite la configuración de red con un clic a través del servicio FEN.
Admite cámaras de terceros (Axis, panasonic, ONVIF)

CÁMARA MINI DOMO (DC-D4212R).

Fácil instalación con DirecIP NVR.
Resolución Fullm HD (1080p).
Lente Focal fija (f = 4 mm).
Día y noche (ICR).
PoE (IEEE 802.3 af Clase 2).
LED IR (distancia: 20m)
Diseño mecánico de 3 ejes para instalación.
Soporta Onvif.

CAMARA BULLET (DC-E4212WR).

Fácil instalación con DirecIP NVR.
Resolución Full HD (1080p).
Lente de foco fijo (f = 4.0m).
IK10 / IP66 soporta.
PoE (IEEE 802.3 af Clase 2).
Día y noche (ICR).
LED IR (distancia: 20m).
Diseño mecánico de 3 ejes para instalación.
Soporta Onvif.

PANTALLA PROFESIONAL (UD55E-B).

Uniformidad de brillo y precisión de color con la tecnología Samsung Color Expert y calibración de fábrica.
Diseño ultra estrecho de bisel a bisel de 3,5mm para una apariencia casi perfecta de la pared de video.
Mensaje claro através de un papel antideslumbrante (haze 44%), con funcionamiento fiable las 24 horas del tiempo por 7 días de la semana.
Tamaño 55".
Tiempo de respuesta 8ms.
Tipo D-LED DID.
Brillo 500nit.
Colores de Pantalla 8 Bits. 16.7M.
Resolución de contraste 4000:1.
Gama de colores 72%.
C/R inamico MEGA DCR.
Entradas DVI-D, HDMI X 2, HDCP 2.2, Mini Jack Stereo, USB (sólo actualización de Firmware).
Salidas DP1.2, Mini Jack estéreo.


SIMBOLOGÍA

ITEM	SIMBOLO	DESCRIPCIÓN	MODELO
1	ROUTER	ROUTER HI-FI	PACOM 8101
2	NVR	NVR 32 CANALES	LK-95
3	SWITCH	SWITCH	ONV
4	EXTENSOR HDM X	EXTENSOR HDM RX 1	CAT.5E/6 100M
5	MOD.IDIS	MODULO IDIS	AL-1112
6	PANEL ALARMAS	PANEL ALARMAS	PACOM 8002
7	MONITOR	MONITOR 55"	UD55E-B SAMSUNG
8	RAYO LINEAL	RAYO LINEAL	AX-2RL100
9	SENSOR TÉRMICO	SENSOR TÉRMICO	F220-135
10	MONITOR VIDEOPORTERO	MONITOR VIDEOPORTERO	DAHUA IP
11	ANTENA WI-FI	ANTENA WI-FI	360° TIPO PLATO

ITEM	SIMBOLO	DESCRIPCIÓN	MODELO
12	MONITOR CCTV	MONITOR CCTV	25"
13	PLACA CALLE VIDEOPORTERO	PLACA CALLE VIDEOPORTERO	DAHUA IP
14	SOFTWARE	SOFTWARE	IDIS CENTER GMS (ALARMAS)
15	TECLADO	TECLADO	PACOM 8101
16	SIRENA ESTROBOSCOPICA	SIRENA ESTROBOSCOPICA	LK-95
17	SENSOR QUIEBRE VIDRIOS	SENSOR QUIEBRE VIDRIOS	LK-4105C
18	SENSOR DE HUMO	SENSOR DE HUMO	541NB
19	SENSOR MAGNÉTICO	SENSOR MAGNÉTICO	SM-216Q
20	PALANCA DE INCEDIO	PALANCA DE INCEDIO	MS-400
21	CAMARA BULLET	CAMARA BULLET	BULLET DC-E4212WR
22	CAMARA DOMO	CAMARA DOMO	DOMO DC-4212R

PLANTA CORO

ESC: 1 / 100 DISPOSICIÓN DE EQUIPOS Y CANALIZACIÓN

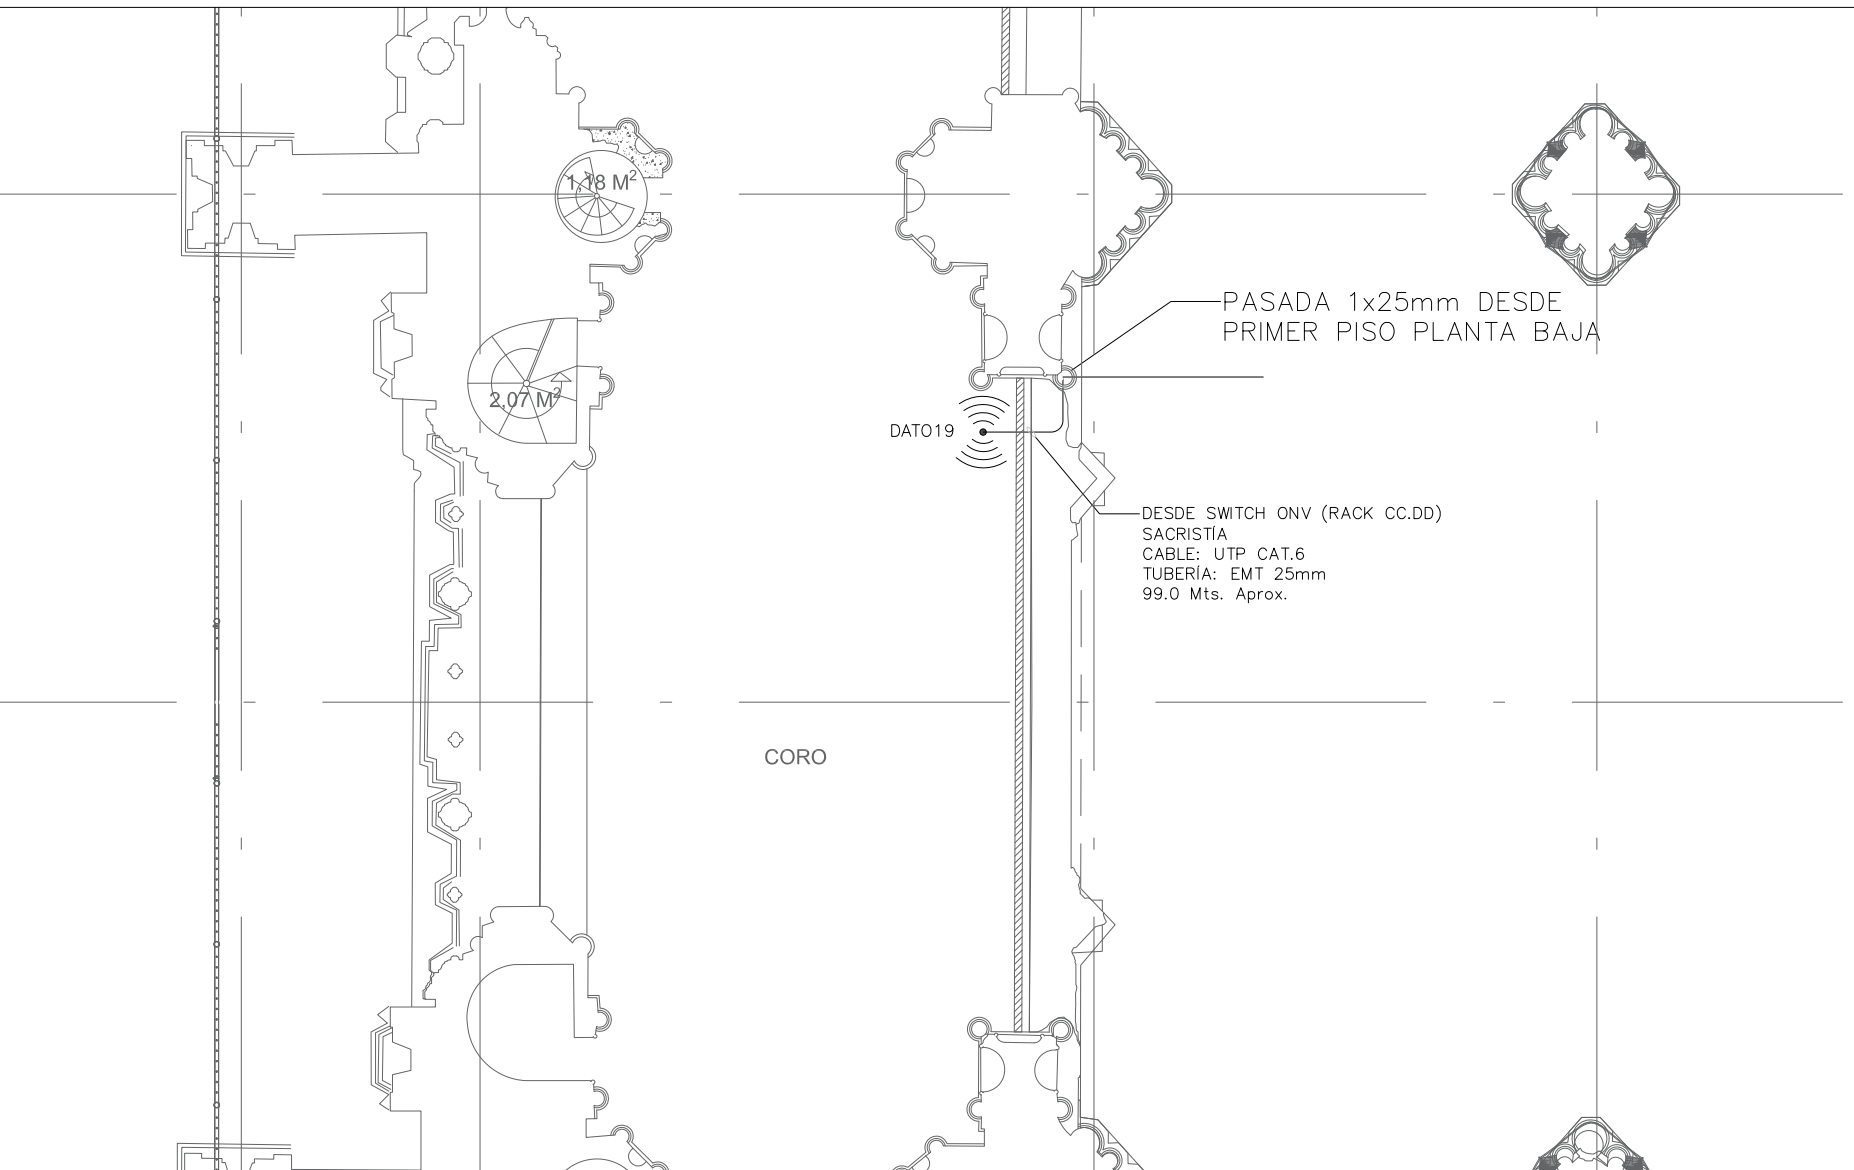

PROYECTO DE SEGURIDAD Y PANTALLAS TV

PROYECTO:	BASILICA EL SALVADOR
PROYECTISTAS:	R.A.C - J.G (BTCO)
DIBUJANTE:	C.A.A
FECHA:	31/01/2021
VERSIÓN:	2

REVISIÓN: 5

ESPECIALIDAD:	CORRIENTES DÉBILES
CONTENIDO:	DISTRIBUCIÓN DE EQUIPOS CCTV Y MONITORES TV



REVISÓ:	R.R.G
CONTACTO:	contacto@dicsa.cl
FORMATO	ESCALA
A1	1/100
LÁMINA N°	1/4