


PLANTA BASILICA

ESC: 1 / 100


DISPOSICIÓN DE EQUIPOS Y CANALIZACIONES

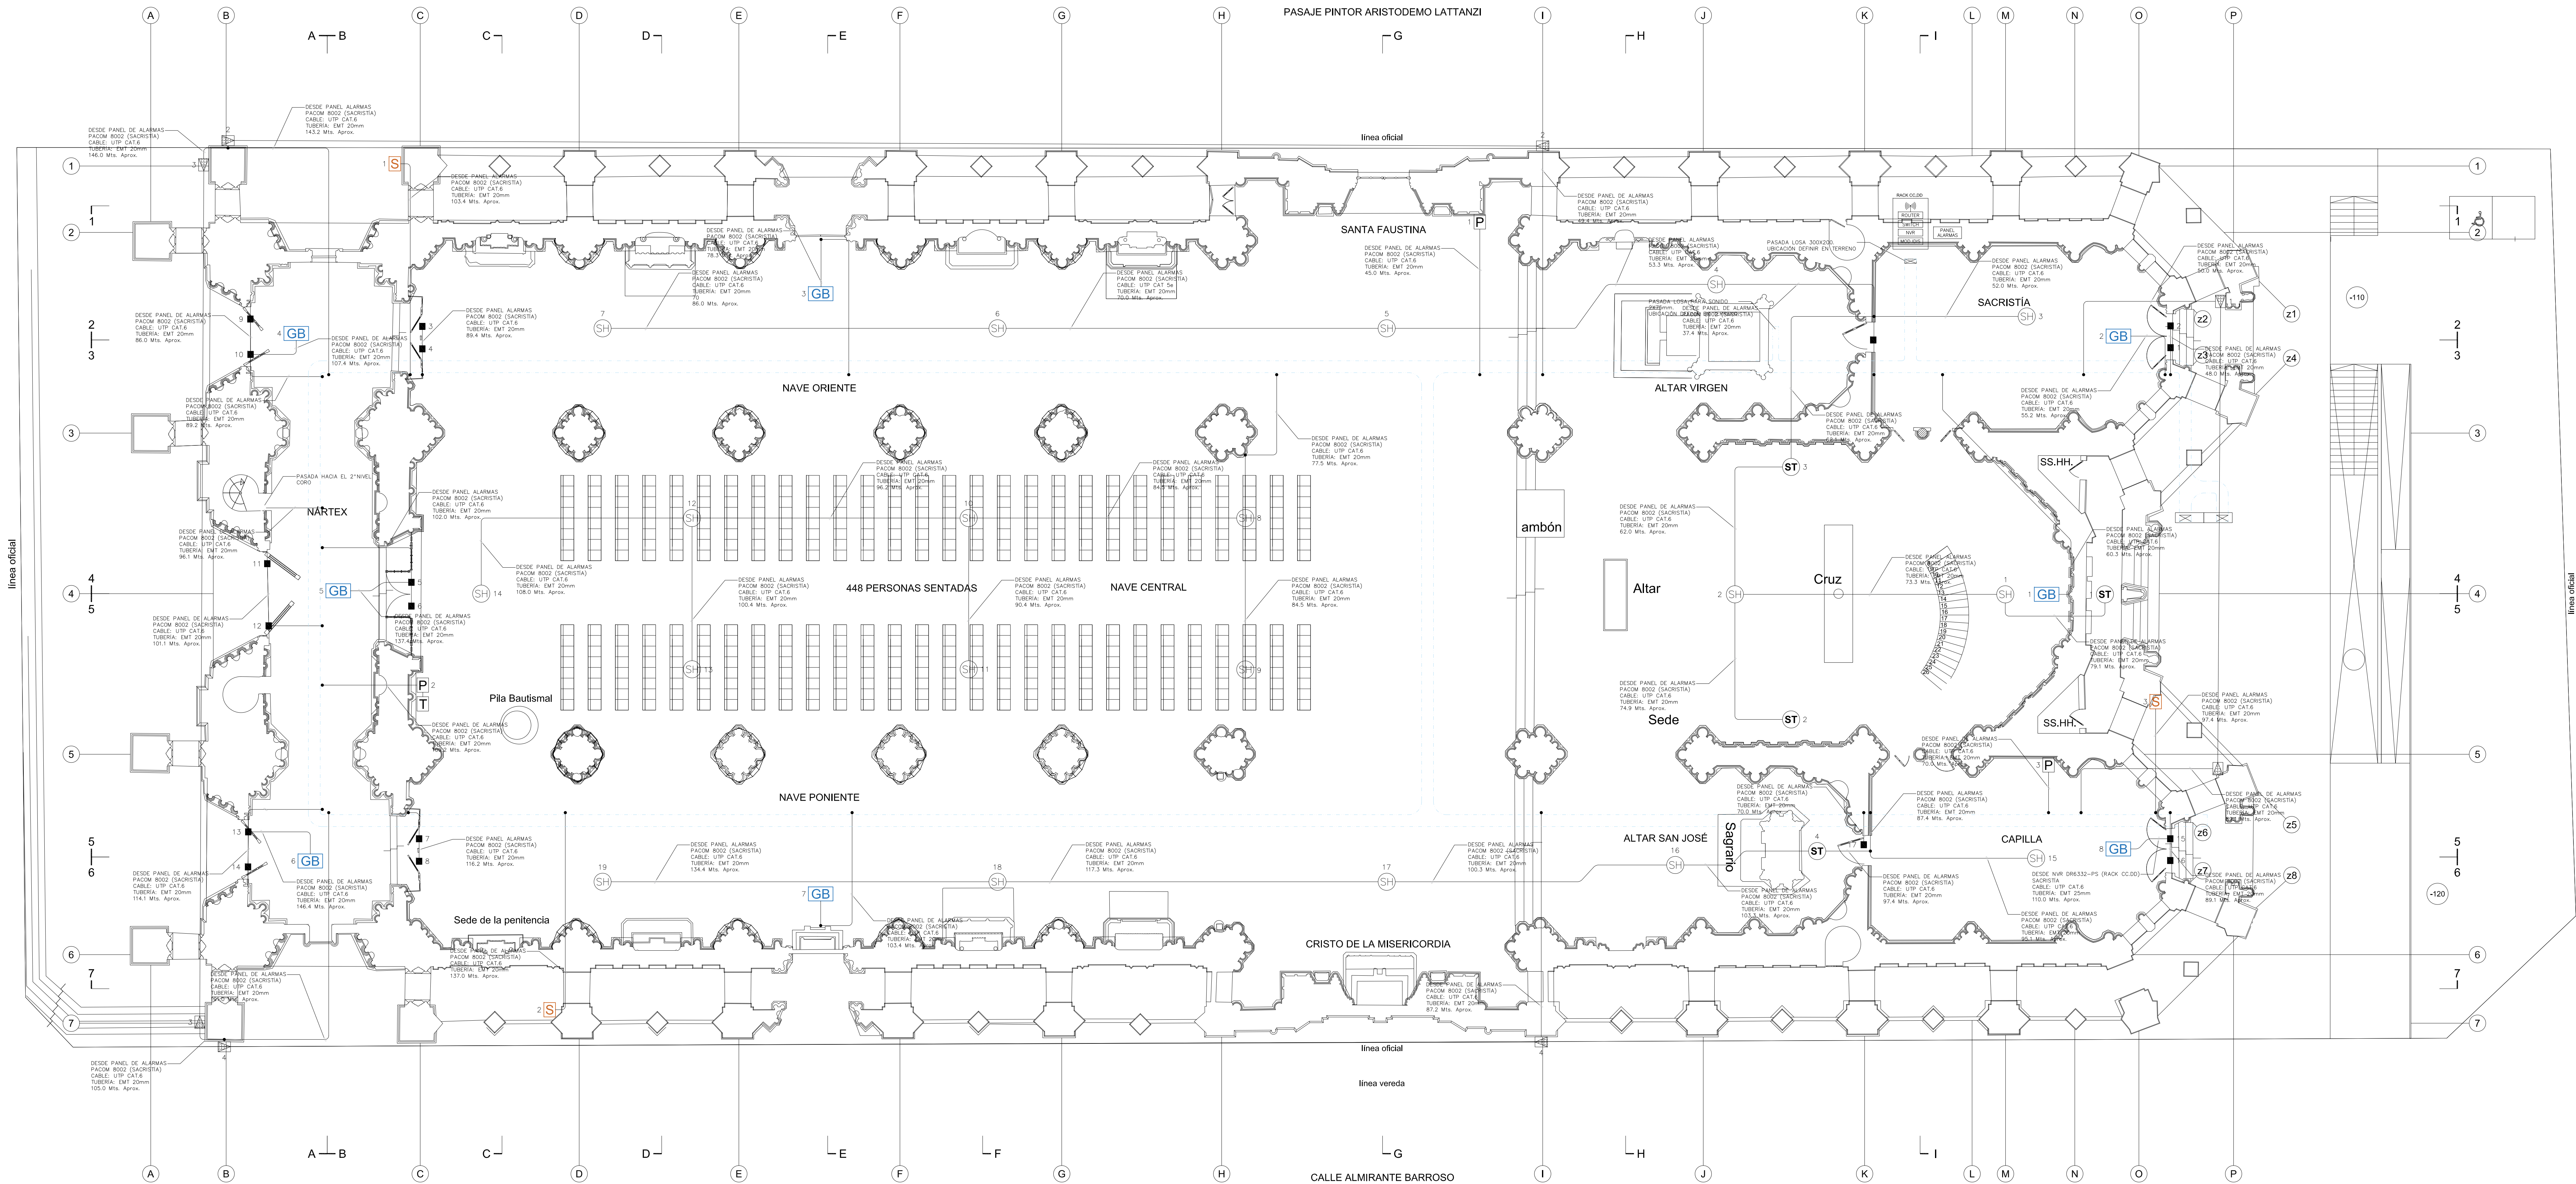

PLANTA CORO

ESC: 1 / 100

DISPOSICIÓN DE EQUIPOS Y CANALIZACIÓN

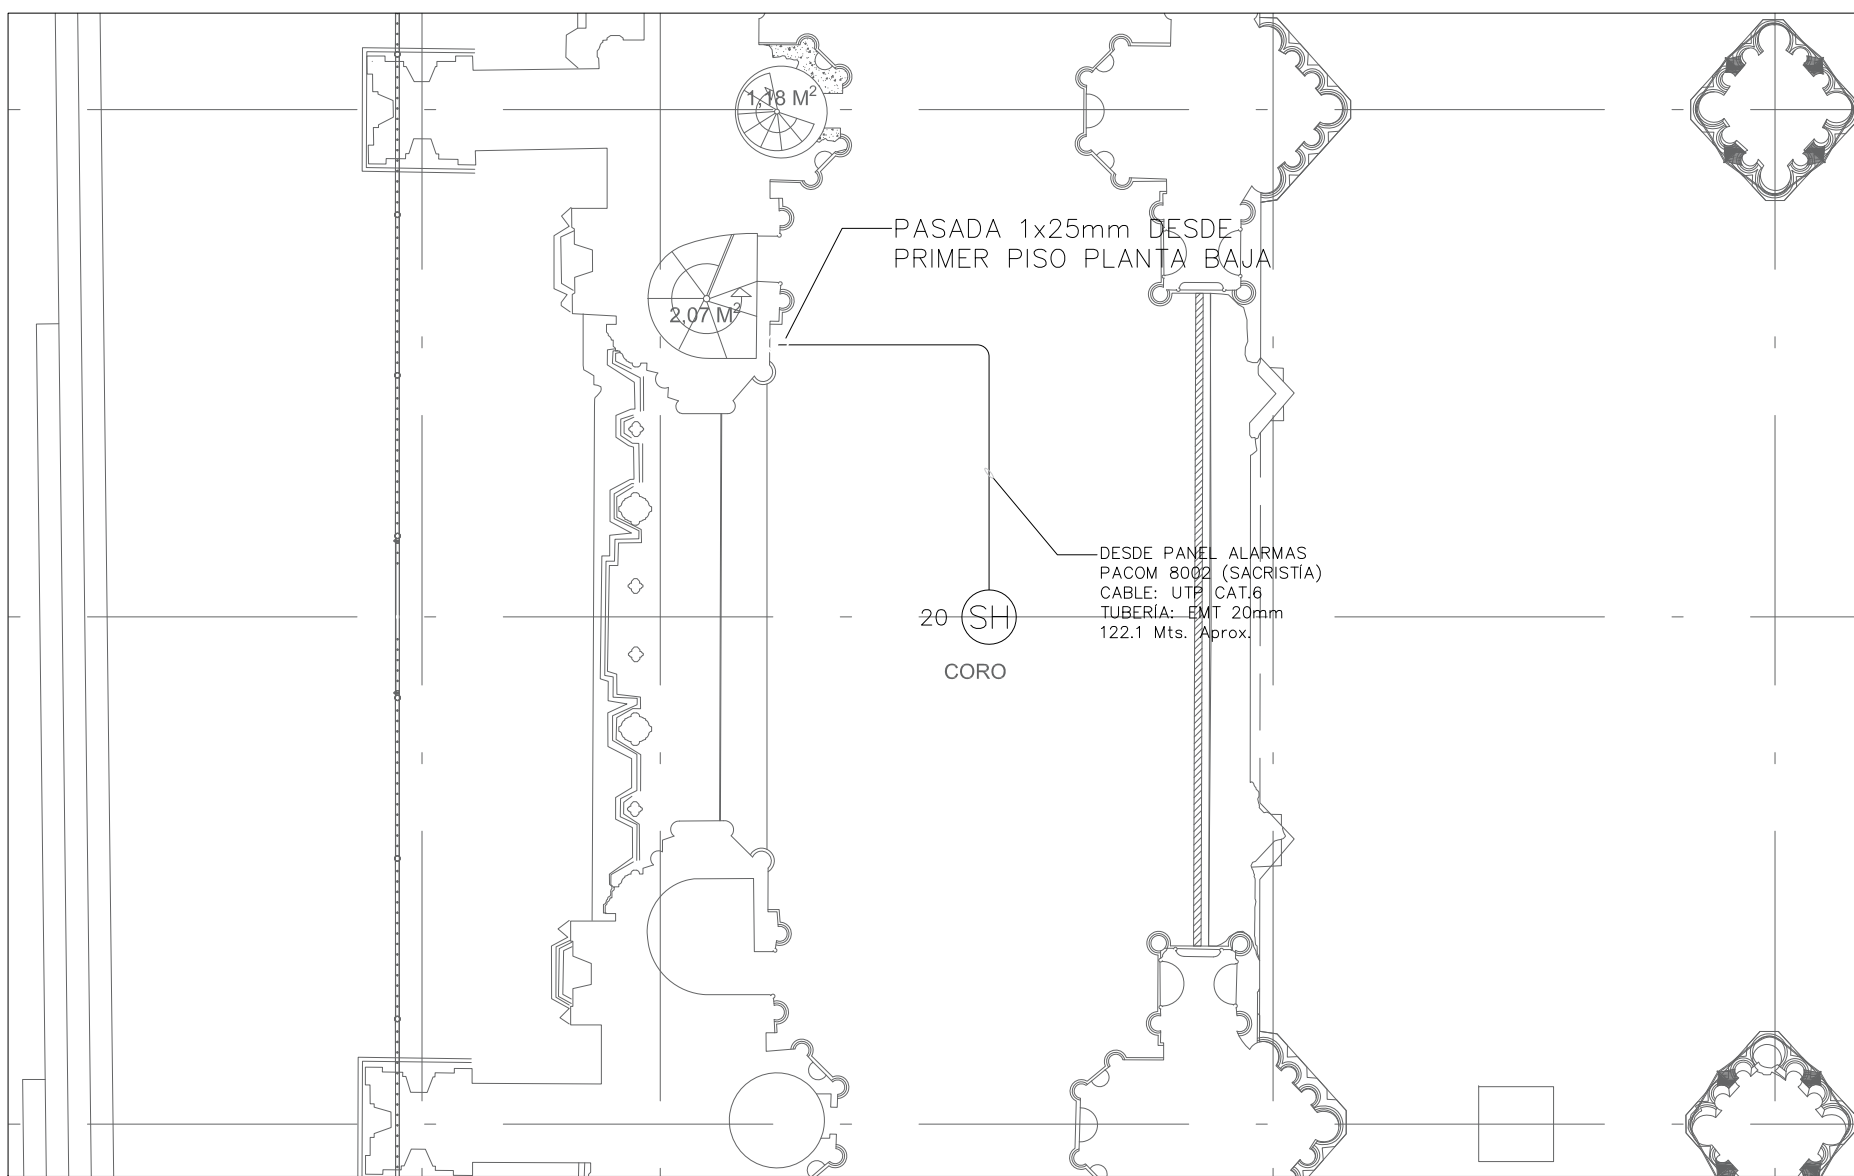

SIMBOLOGÍA

ITEM	SÍMBOLO	DESCRIPCIÓN	MODELO
1	ROUTER	ROUTER HI-FI	PACOM 8101
2	NVR	NVR 32 CANALES	LK-95
3	SWITCH	SWITCH	ONV
4	EXTENSOR HDM RX 1	EXTENSOR HDM RX 1	CAT.5E/6 100M
5	MOD.IDIS	MÓDULO IDIS	AL-1112
6	PANEL ALARMAS	PANEL ALARMAS	PACOM 8002
7	MONITOR 55"	MONITOR 55"	UD55E-B SAMSUNG
8	RAYO LINEAL	RAYO LINEAL	AX-2RL100
9	SENSOR TÉRMICO	SENSOR TÉRMICO	F220-135
10	MONITOR VIDEOPORTERO	MONITOR VIDEOPORTERO	DAHUA IP
11	ANTENA WI-FI	ANTENA WI-FI	360° TIPO PLATO

ITEM	SÍMBOLO	DESCRIPCIÓN	MODELO
12	MONITOR CCTV	MONITOR CCTV	25"
13	PLACA CALLE VIDEOPORTERO	PLACA CALLE VIDEOPORTERO	DAHUA IP
14	SOFTWARE	SOFTWARE	IDIS CENTER GMS (ALARMAS)
15	TECLADO	TECLADO	PACOM 8101
16	SIRENA ESTROBOSCOPICA	SIRENA ESTROBOSCOPICA	LK-95
17	SENSOR QUIEBRE VIDRIOS	SENSOR QUIEBRE VIDRIOS	LK-410SC
18	SENSOR DE HUMO	SENSOR DE HUMO	541NB
19	SENSOR MAGNÉTICO	SENSOR MAGNÉTICO	SM-216Q
20	PALANCA DE INCENDIO	PALANCA DE INCENDIO	MS-400
21	CAMARA BULLET	CAMARA BULLET	BULLET DC-E4212WR
22	CAMARA DOMO	CAMARA DOMO	DOMO DC-4212R

PROYECTO DE SEGURIDAD Y PANTALLAS TV

PROYECTO:	BASILICA EL SALVADOR
PROYECTISTAS:	R.A.C - J.G (BTCO)
DIBUJANTE:	C.A.A
FECHA:	31/01/2021
VERSIÓN:	2
REVISIÓN:	5

ESPECIALIDAD:	CORRIENTES DÉBILES
CONTENIDO:	DISTRIBUCIÓN DE EQUIPOS DE INCENDIO E INTRUSIÓN
REVISÓ:	R.R.G
CONTACTO:	contacto@dicisa.cl
FORMATO:	ESCALA
A1	1/100
LÁMINA N°	3/4

