


DIAGRAMA Y SIMBOLOGÍA


DETALLE DE CONEXIÓN DE EQUIPOS

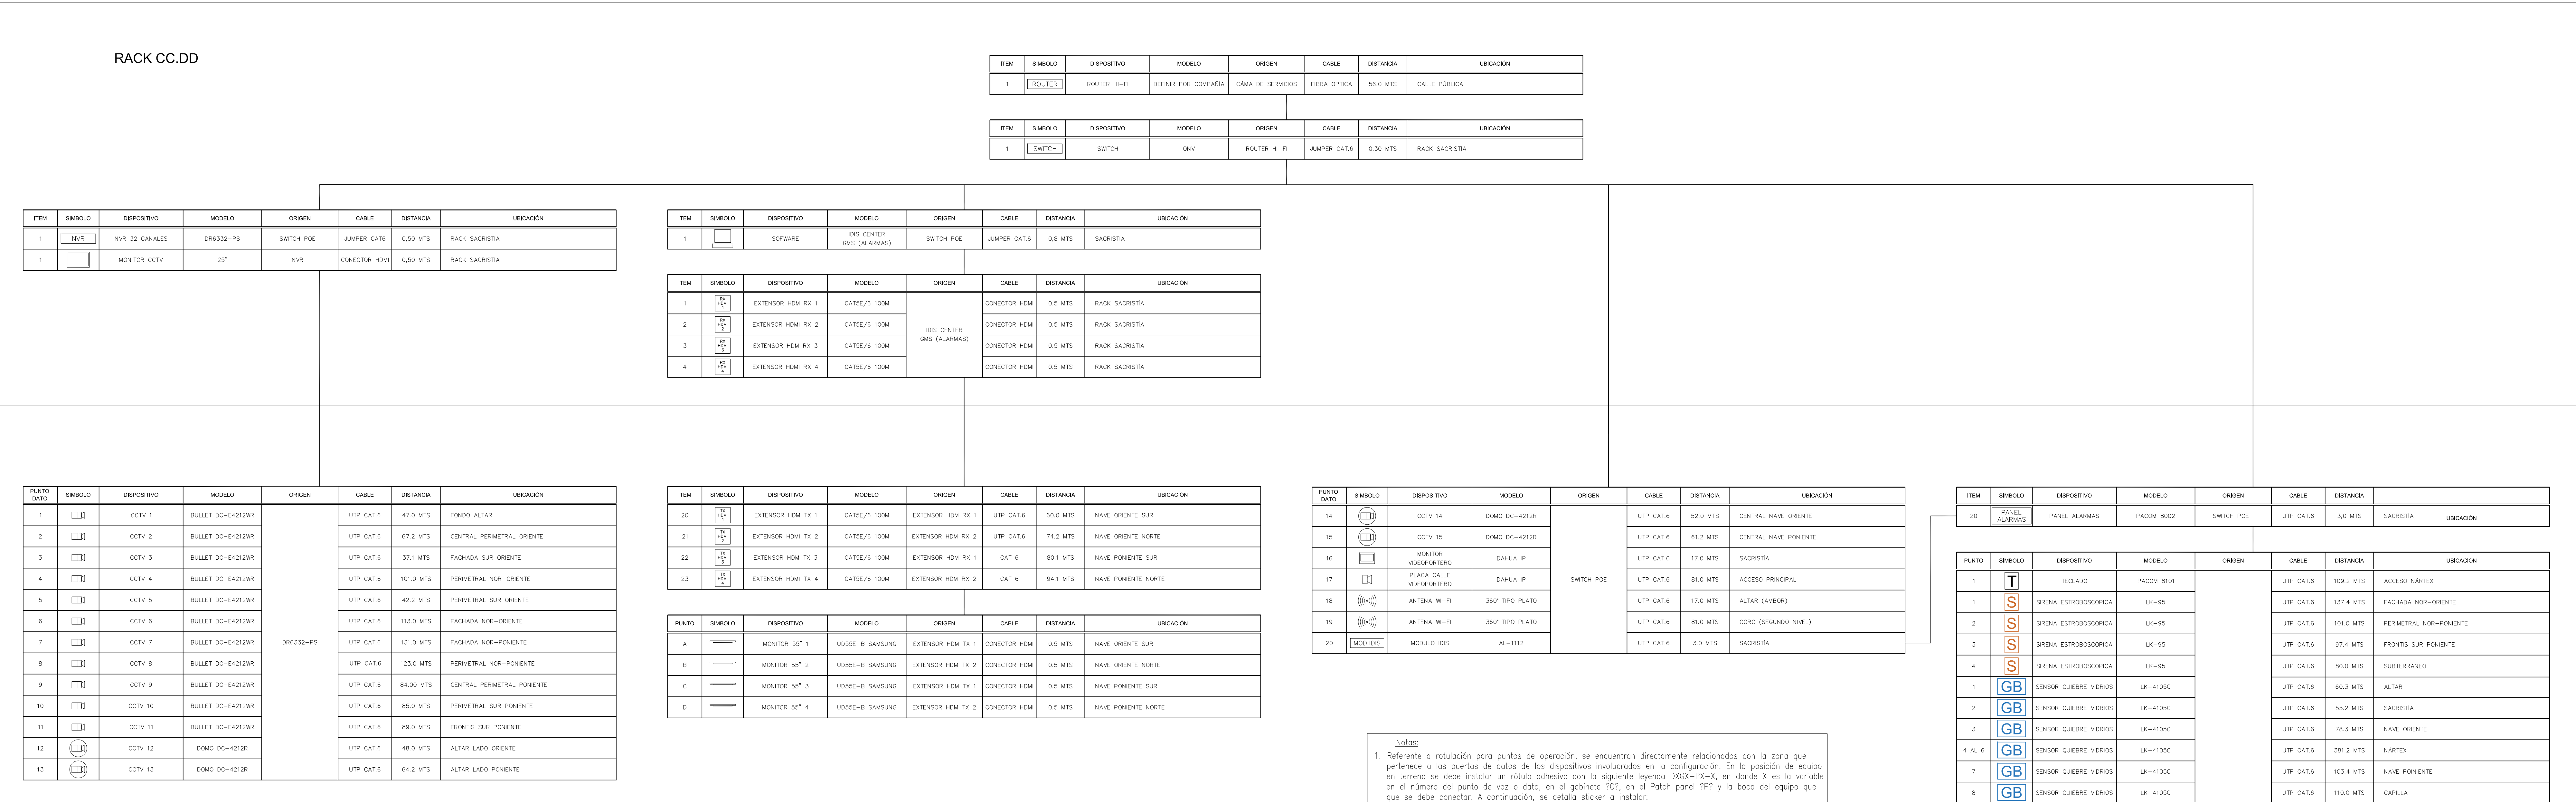

CORTE PILARES

ESC: S / E

DETALLES DE POSICIONAMIENTO DE EQUIPOS

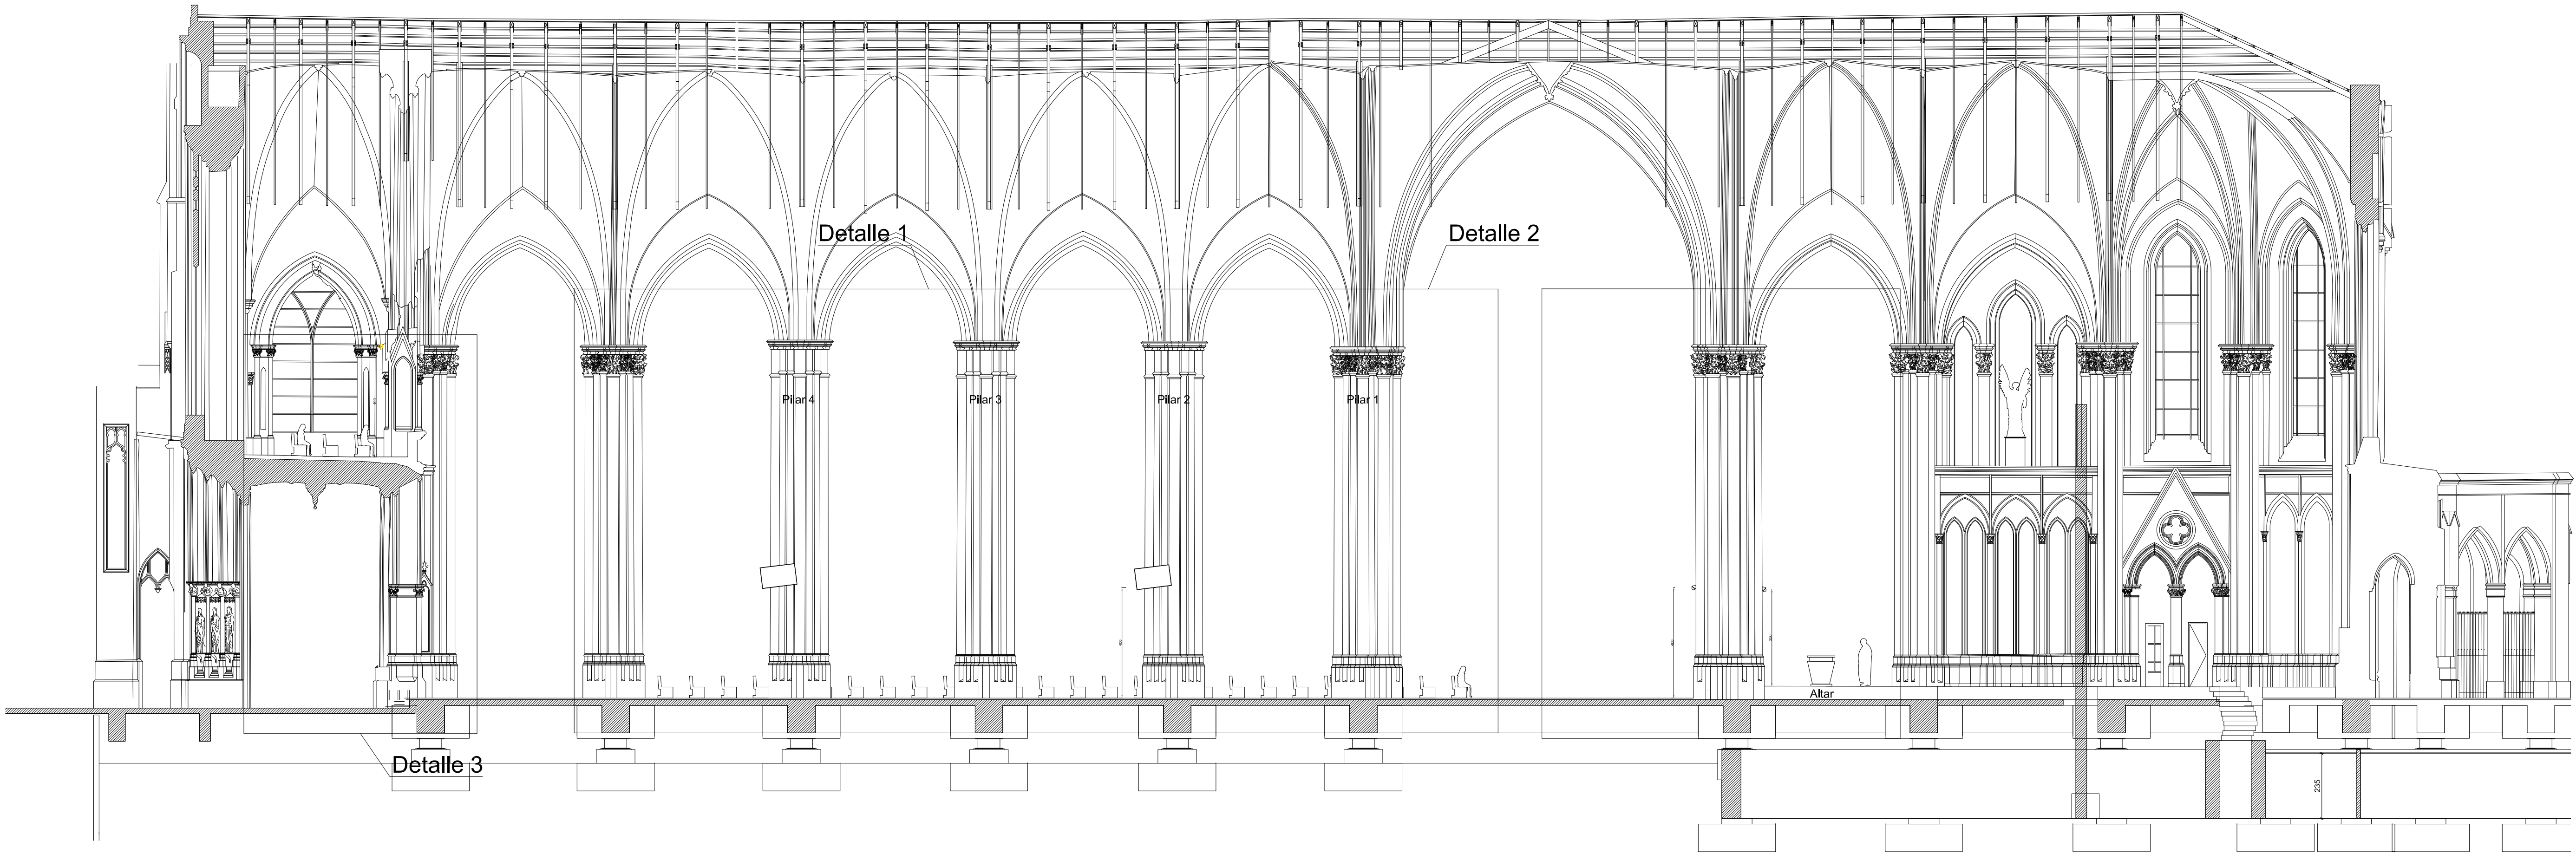

ITEM	SÍMBOLO	DISPOSITIVO	MODELO	ORIGEN	CABLE	DISTANCIA	UBICACIÓN
20		PANEL ALARMAS	PACOM 8002	SWITCH POE	UTP CAT.6	3,0 MTS	SACRISTIA UBICACIÓN

PUNTO	SÍMBOLO	DISPOSITIVO	MODELO	ORIGEN	CABLE	DISTANCIA	UBICACIÓN
1		TECLADO	PACOM 8101		UTP CAT.6	109,2 MTS	ACCESO NARTEX
1		SIRENA ESTROBOSCOPICA	LK-95		UTP CAT.6	137,4 MTS	FACHADA NOR-ORIENTE
3		SIRENA ESTROBOSCOPICA	LK-95		UTP CAT.6	101,0 MTS	PERIMETRAL NOR-PONIENTE
2		SIRENA ESTROBOSCOPICA	LK-95		UTP CAT.6	97,4 MTS	FRONTIS SUR PONIENTE
4		SIRENA ESTROBOSCOPICA	LK-95		UTP CAT.6	80,0 MTS	SUBTERRANEO
1		SENSOR QUIEBRE VIDRIOS	LK-4105C		UTP CAT.6	60,3 MTS	ALTAR
2		SENSOR QUIEBRE VIDRIOS	LK-4105C		UTP CAT.6	55,2 MTS	SACRISTIA
3		SENSOR QUIEBRE VIDRIOS	LK-4105C		UTP CAT.6	78,3 MTS	NAVE ORIENTE
4 AL 6		SENSOR QUIEBRE VIDRIOS	LK-4105C		UTP CAT.6	381,2 MTS	NARTEX
7		SENSOR QUIEBRE VIDRIOS	LK-4105C		UTP CAT.6	103,4 MTS	NAVE PONIENTE
8		SENSOR QUIEBRE VIDRIOS	LK-4105C		UTP CAT.6	110,0 MTS	CAPILLA
1 AL 2		SENSOR DE HUMO	541NB		UTP CAT.6	73,5 MTS	ALTAR
3		SENSOR DE HUMO	541NB		UTP CAT.6	52,0 MTS	SACRISTIA
4		SENSOR DE HUMO	541NB		UTP CAT.6	37,4 MTS	ALTAR VIRGEN
5 AL 7		SENSOR DE HUMO	541NB		UTP CAT.6	86,0 MTS	NAVE ORIENTE
8 AL 14		SENSOR DE HUMO	541NB		UTP CAT.6	108,0 MTS	NAVE CENTRAL
15		SENSOR DE HUMO	541NB		UTP CAT.6	110,0 MTS	CAPILLA
16		SENSOR DE HUMO	541NB		UTP CAT.6	103,3 MTS	ALTAR SAN JOSE
17 AL 19		SENSOR DE HUMO	541NB		UTP CAT.6	134,4 MTS	NAVE PONIENTE
20		SENSOR DE HUMO	541NB		UTP CAT.6	122,1 MTS	CORO (SEGUNDO NIVEL)
21 AL 26		SENSOR DE HUMO	541NB		UTP CAT.6	128,1 MTS	SUBTERRANEO ORIENTE
27		SENSOR DE HUMO	541NB		UTP CAT.6	33,0 MTS	SALA ELECTRICA
28		SENSOR DE HUMO	541NB		UTP CAT.6	40,0 MTS	BODEGA
29		SENSOR DE HUMO	541NB		UTP CAT.6	50,0 MTS	CAPILLA SUBTERRANEA
30 AL 33		SENSOR DE HUMO	541NB		UTP CAT.6	178,5 MTS	SUBTERRANEO CENTRAL
34 AL 39		SENSOR DE HUMO	541NB		UTP CAT.6	182,0 MTS	SUBTERRANEO PONIENTE
1 AL 2		SENSOR MAGNETICO	SM-216Q		UTP CAT.6	48,0 MTS	SACRISTIA
3 AL 6		SENSOR MAGNETICO	SM-216Q		UTP CAT.6	307,6 MTS	ACCESO NARTEX
9 AL 14		SENSOR MAGNETICO	SM-216Q		UTP CAT.6	301,2 MTS	FACHADA NORTE
15 AL 16		SENSOR MAGNETICO	SM-216Q		UTP CAT.6	89,1 MTS	CAPILLA
1		PALANCA DE INCENDIO	MS-400		UTP CAT.6	45,0 MTS	ALTAR SANTA FAUSTINA
2		PALANCA DE INCENDIO	MS-400		UTP CAT.6	109,2 MTS	ACCESO NARTEX
3		PALANCA DE INCENDIO	MS-400		UTP CAT.6	70,0 MTS	CAPILLA Y SUBTERRANEO
4		PALANCA DE INCENDIO	MS-400		UTP CAT.6	82,0 MTS	SUBTERRANEO
1		RAYO LINEAL	AX-2RL100		UTP CAT.6	139,0 MTS	FACHADA SUR
2		RAYO LINEAL	AX-2RL100		UTP CAT.6	192,6 MTS	PERIMETRAL ORIENTE
3		RAYO LINEAL	AX-2RL100		UTP CAT.6	231,0 MTS	FACHADA NORTE
4		RAYO LINEAL	AX-2RL100		UTP CAT.6	188,2 MTS	PERIMETRAL PONIENTE
1 AL 3		SENSOR TERMICO	F220-135		UTP CAT.6	154,0 MTS	ALTAR
4		SENSOR TERMICO	F220-135		UTP CAT.6	97,4 MTS	ALTAR SAN JOSE

PROYECTO DE SEGURIDAD Y PANTALLAS TV

PROYECTO:	BASILICA EL SALVADOR
PROYECTISTAS:	R.A.C - J.G (BTCO)
DIBUJANTE:	C.A.A
FECHA:	31/01/2021
VERSIÓN:	2
REVISIÓN:	5

ESPECIALIDAD:	CORRIENTES DÉBILES
CONTENIDO:	DIAGRAMAS Y DETALLES DE INSTALACIÓN

REVISÓ:		R.R.G	
CONTACTO:		contacto@dicsa.cl	
FORMATO	ESCALA	LÁMINA N°	4/4
A1	1/100		