
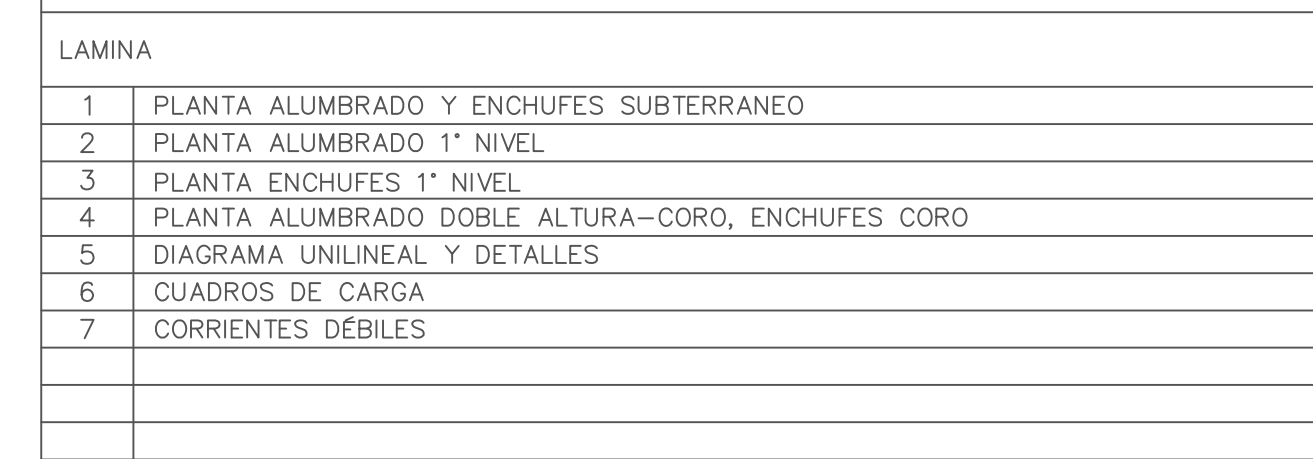
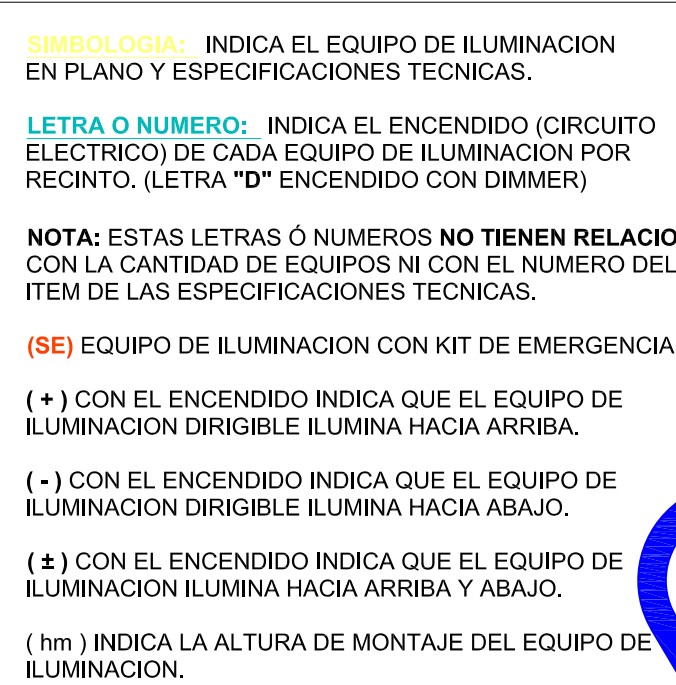
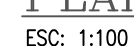
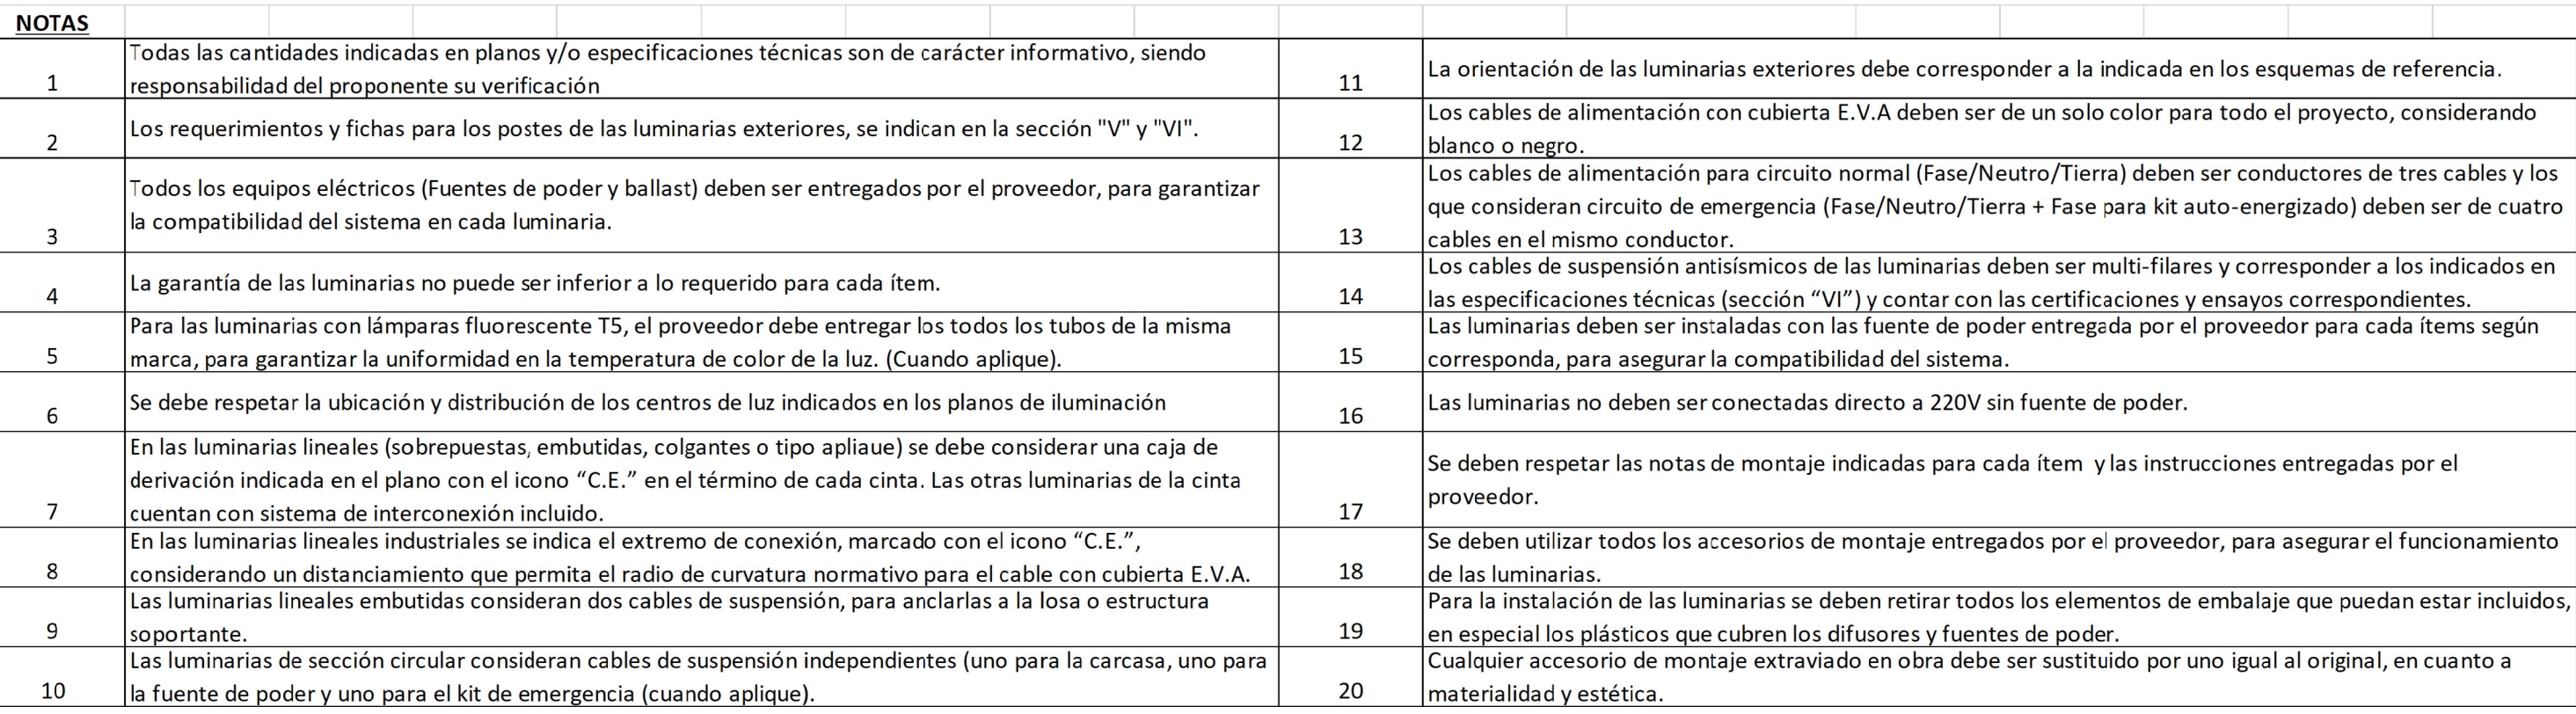


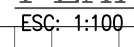

Notas:

- Todos los artefactos (Enchufe) serán mínimos a 0.35m, salvo indicación contraria en planos.
- Todos los artefactos (Enchufe) que serán montados sobre muros de muestres (en ± 0.1) serán efecto a ventilación y coordinación según altura muestre.
- Todas las conexiones que se realicen pre-embudadas serán de ducto $\varnothing 25$, las vainas subterráneas serán de PVC rígido de 1.6mm de espesor y serán de ducto $\varnothing 25$ (salvo lo que se indica en exterior o expuestas a daños mecánicos según c.a.g.)
- Los artefactos serán de tipo "brazo" y serán de 1.6mm de espesor. P 55
- (1) dimensión de los datos de corte, se efectuara en conducto $\Phi 3.31$ mm, salvo indicación expresa.
- (2) conducto neutro será de igual sección que el conducto de fase ($\Phi 3.31$ mm), en los circuitos de la empresa y computados.
- Los planos, registro y coordinación en general se deberá ejecutar, consultar en terreno con los circuitos constructivos y con los especialistas correspondientes, con el respectivo visto bueno de la I.T.O. Empresa.
- Las dimensiones de los planos eléctricos solo son referencias, el contratista deberá que se ajuste lo que se indique en los planos, en caso de discrepancia, prevalecerá lo que se indique en los planos.
- Las dimensiones de los planos eléctricos (h-u-c) eléctricos deberán ser derivadas con un cable de 2.5mm de $11.37mm \pm 2.5mm$ y deberá contar con un cable en todo su recorrido.
- En caso de que el cable no sea suficiente para la instalación en la placa de montaje de cada enchufe indicando el número de circuito o cable correspondiente.
- Los materiales que requieren certificación por su uso, cumplirán con este requisito.
- Los materiales que no requieren certificación, pero que se deseará que sean de mejor calidad, el contratista consultará previamente no obstante, estas últimas prevalecerán sobre los planos.
- Todos los materiales serán de marca reconocida y serán de tipo "brazo" y serán de 1.6mm de espesor. PMS.
- En etapa de construcción deberá conformar medidas para montaje de luminarias.

3	AQIN	01/10/20	REVISIÓN PARA DOCUMENTO DEL 07/2020		
REV.	POR	FECHA	MOTIVO		
MODIFICACIONES					
CONTENIDO:				LÁMINA	
PLANTA ALUMBRADO Y ENCHUFES SUBTERRANEO				1	
ARCHIVO-CAD :			DIMENSIONES FORMATO:		

PROYECTO ELECTRICO DE ALUMBRADO
RESTAURACIÓN BASILICA
DEL SALVADOR

AGUSTINAS N°1781	LAMINA 01 DE 07	ESCALA: INDICADA
: SANTIAGO	FECHA: DICIEMBRE 2019	
	PROYECTO: A.Q.H.	DIBUJO : C.A.A.
	REVISO : A.Q.H. -	R.R.G.
ARIO	PROYECTO:	

PARROQUIA EL SALVADOR
RUT: 453.326-7
R.L.:
RUT:

ALEJANDRO QUEZADA HELMS
8.957.164-2
INGENIERO ELECTRICO
LIC. SEC. CLASE A