
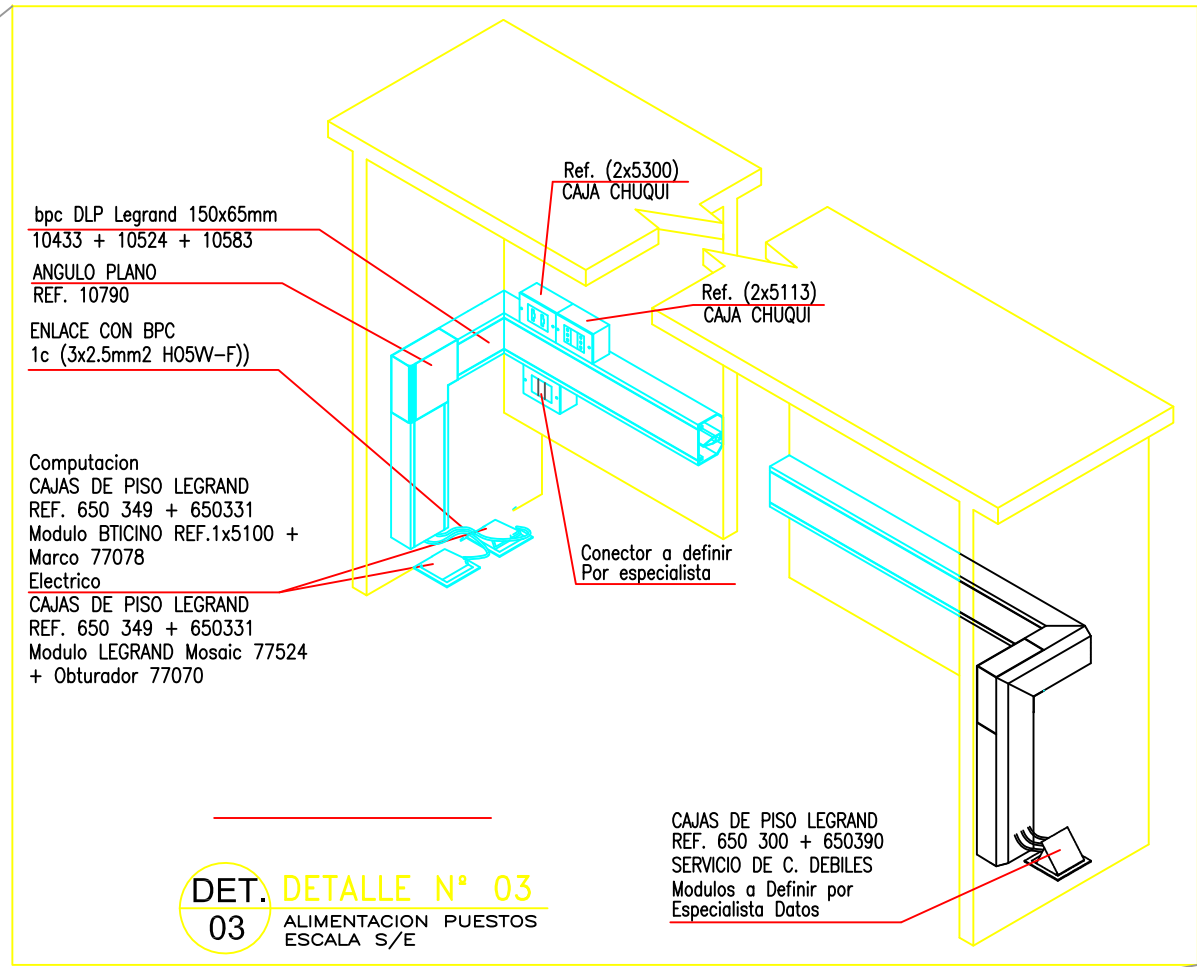


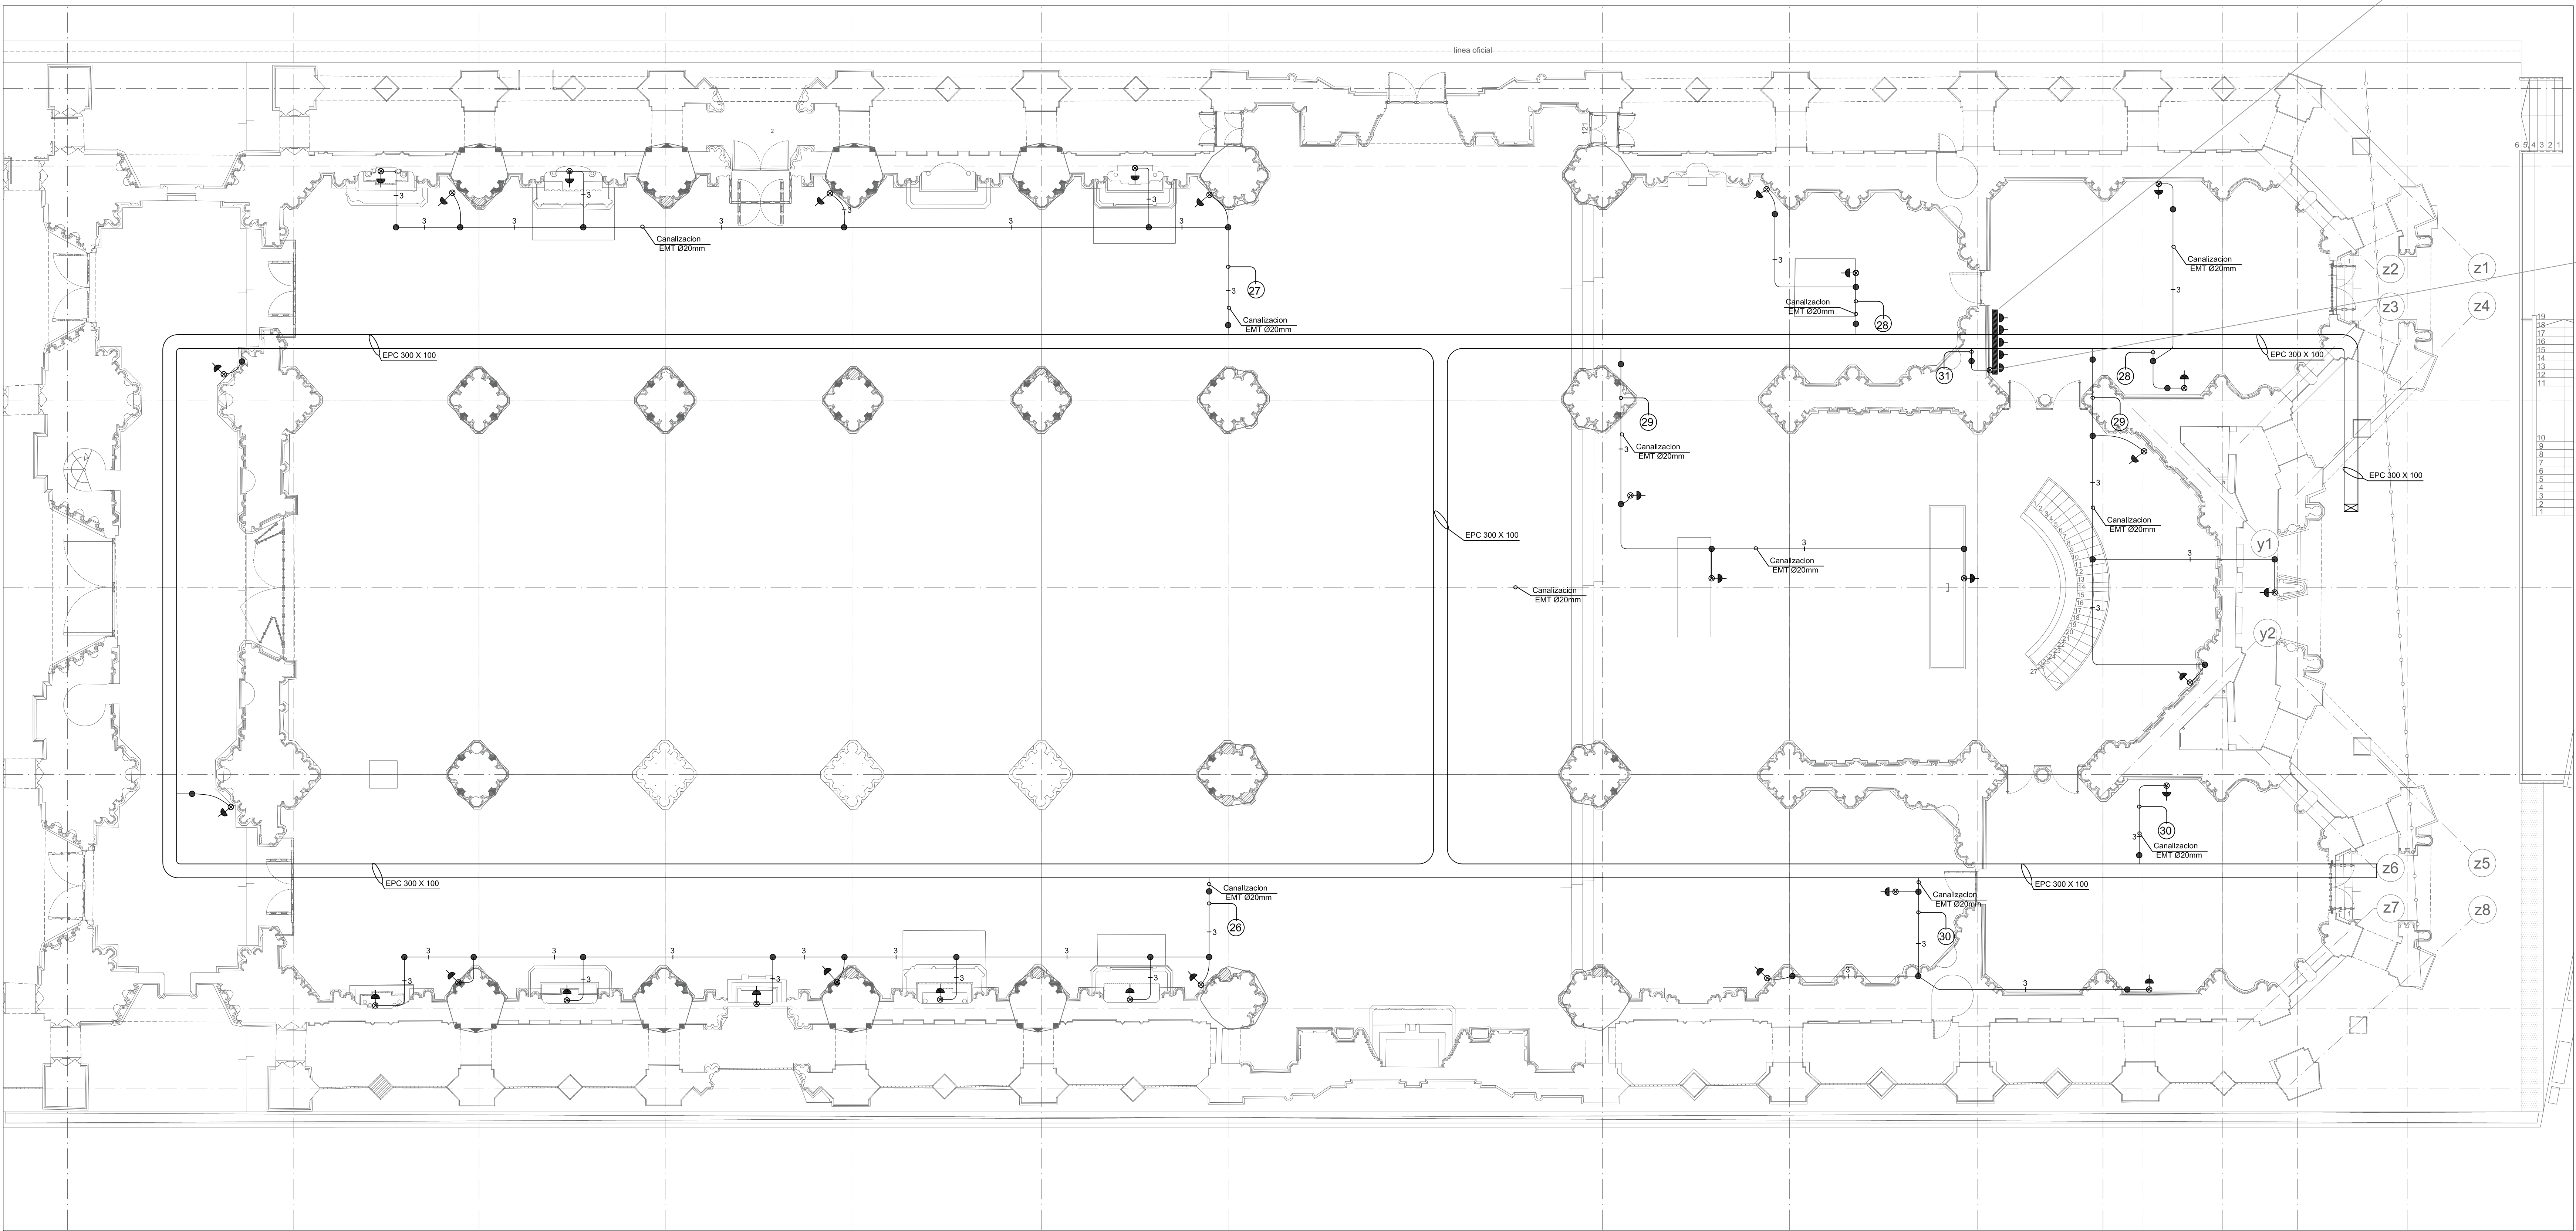


PLANTA DE ENCHUFES PRIMER NIVEL
ESC: 1/100

SÍMBOLOGÍA	DATOS TÉCNICOS
	EQUIPO DE MEDIDA
	PERFIL 75X75X2
	PASADA EN MURO „LOZA
	CAJA DERIVACION METALICA
	TUBERIA EMT(Ødiam. esp.).
	ESCALERILLA 300X100 ALUMBRADO
	BANDEJA DLP 105X50
	ENCHUFE NORMAL 10 amp
	INTERRUPTOR 9-12
	INTERRUPTOR 9-32
	N° DE CIRCUITO ILUMINACION
	N° DE CIRCUITO ENCHUFE

Notas:

- 1.-Todos los artefactos (enchufes) serán montados a 0,35m. salvo indicación contraria en planos.
- 2.-Todos los artefactos (enchufes) que sean montados sobre muros de mampostería serán a 1,20mts. salvo indicación contraria en planos.
- 3.-Todas las canalizaciones que se ejecuten pre-embutidas serán en ducto p.v.c., las que van sobrepuentes serán en tubo de hierro y las que van en el suelo serán en ducto p.v.c., salvo las que van a la vista en exterior o expuestas a daños mecánicos serán c.a.p.
- 4.-Las canalizaciones en sector de baños deben ser a prueba de salpicaduras IP 55.
- 5.-El dimensionado de todos los circuitos, se efectuará en conductor #13/1 mm2 aislación EVA, salvo indicación contraria en planos.
- 6.-El conductor neutro será de igual sección que el conductor de fase (#13/1 mm2), en los circuitos de enchufes y empalmes.
- 7.-Toda instalación, recorrido y canalización en general se deberá ejecutar y coordinar en terreno con la empresa constructora y con los especialistas correspondientes, con el respectivo visto bueno de la I.T.O. Eléctrica.
- 8.-Las dimensiones de los tableros eléctricos solo son referencias, el contratista eléctrico que se adjudique la obra deberá presentar su respectivo lay-out para que sean coordinados con el respectivo visto bueno de la I.T.O. eléctrica y/o montante.
- 9.-Las bandejas portaconductores (p.p.c.) eléctricas deberán ser otimizadas con un cable de Cu desnudo de 6,37mm2 y deberá contar de tapa en todo su recorrido.
- 10.-Para los circuitos de enchufes, deberán quedar identificados en la placa de montaje de cada enchufe indicando el número de circuito a cual corresponde.
- 11.-Las materiales que requieren certificación para su uso, cumplen con este requisito.
- 12.-Este plano es complementario a las Especificaciones Técnicas de la Obra, en caso de existir discrepancia el contratista consultará previamente no obstante, estas últimas prevalecerán sobre el plano.
- 13.-Todas las luminarias exteriores deben considerar IP para ubicación intemperie, como mínimo IP65.
- 14.-En etapas de construcción se deben confirmar medidas de altura para montaje de luminarias.

CUADRO RESUMEN DE LAMINAS			
LÁMINA	CONTENIDO	LÁMINA	CONTENIDO
1	PLANTA ALUMBRADO Y ENCHUFES SUBTERRANEO	3	PLANTA ENCHUFES 1° NIVEL
2	PLANTA ALUMBRADO 1° NIVEL		
3	PLANTA ENCHUFES 1° NIVEL		
4	PLANTA ALUMBRADO DOBLE ALTURA-CORO, ENCHUFES CORO		
5	DIAGRAMA UNILINEAL Y DETALLES		
6	CUADROS DE CARGA		
7	CORRIENTES DÉBILES		

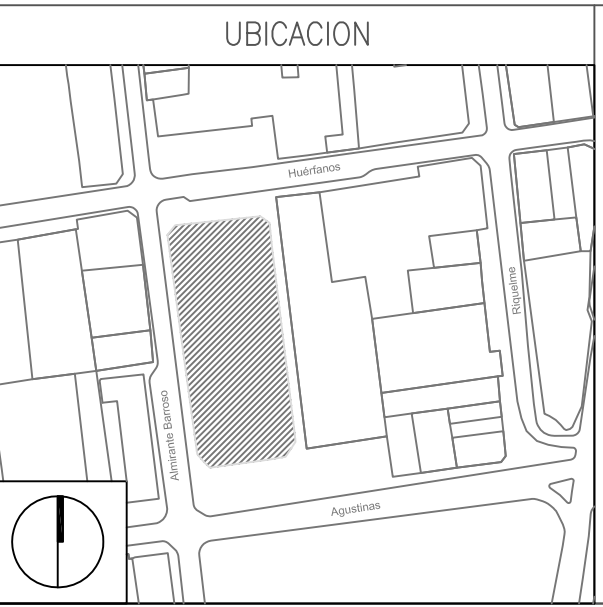

INSCRIPCION N° _____
FECHA : _____



REV.	POR	FECHA	MOTIVO
3	BOB	01/10/20	Revisión para documento BZE 97/2020
MODIFICACIONES			
CONTENIDO:			LÁMINA
PLANTA ENCHUFES 1° NIVEL			3
ARCHIVO-CAD :			DIMENSIONES FORMATO: mm
PROYECTO ELECTRICO DE ALUMBRADO RESTAURACIÓN BASILICA DEL SALVADOR			
CALLE : AGUSTINAS N°1781		LÁMINA 03 DE 07 ESCALA: INDICADA	
COMUNA : SANTIAGO		FECHA : DICIEMBRE 2019	
PROPIETARIO		PROYECTO: A.G.H. DIBUJO : C.A.A.	
PARRQUIA EL SALVADOR		REVISOR: A.G.H.-R.B.G.	
RUT: 63.332-7		INSTALADOR	
R.L.		ALEJANDRO QUEZADA HELMS	
RUT:		RUT: 15.472.775-2	
		INGENIERO ELECTRICO	
		LIC. SEC. 6058 A	