

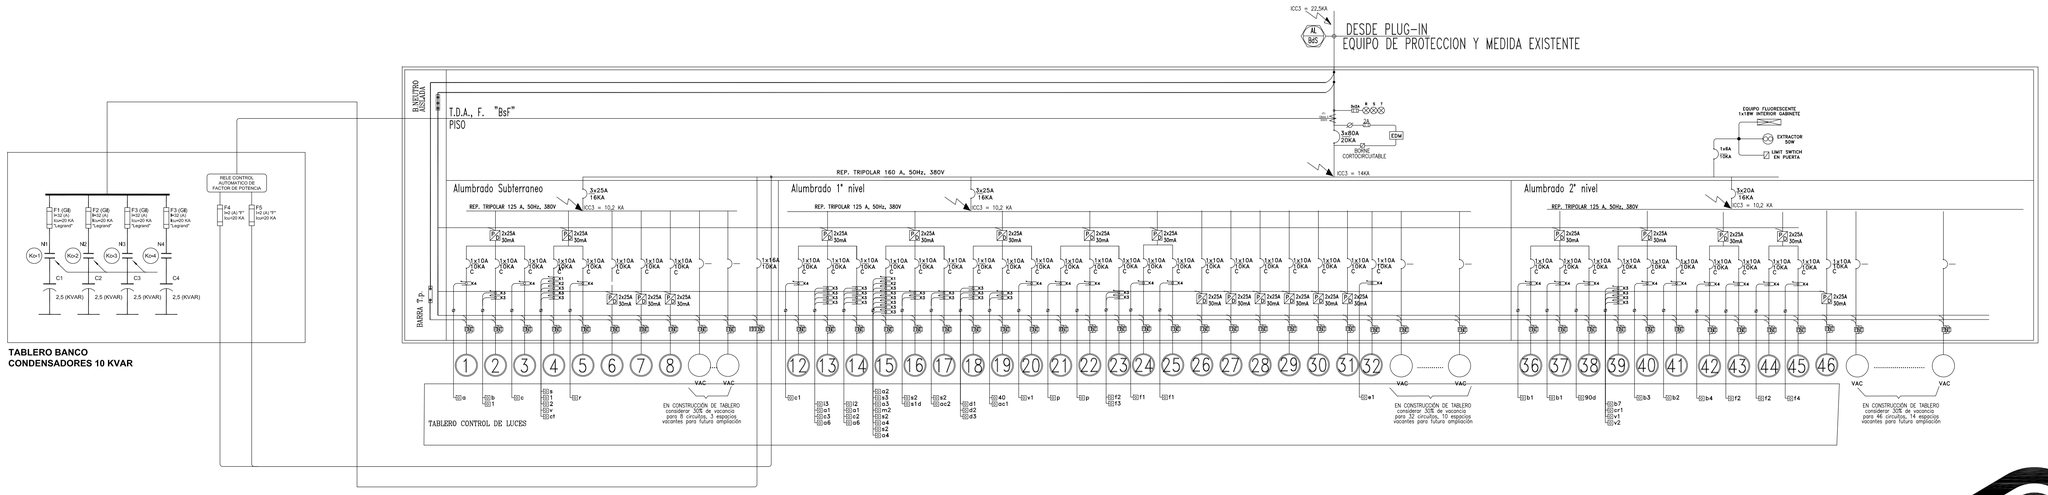


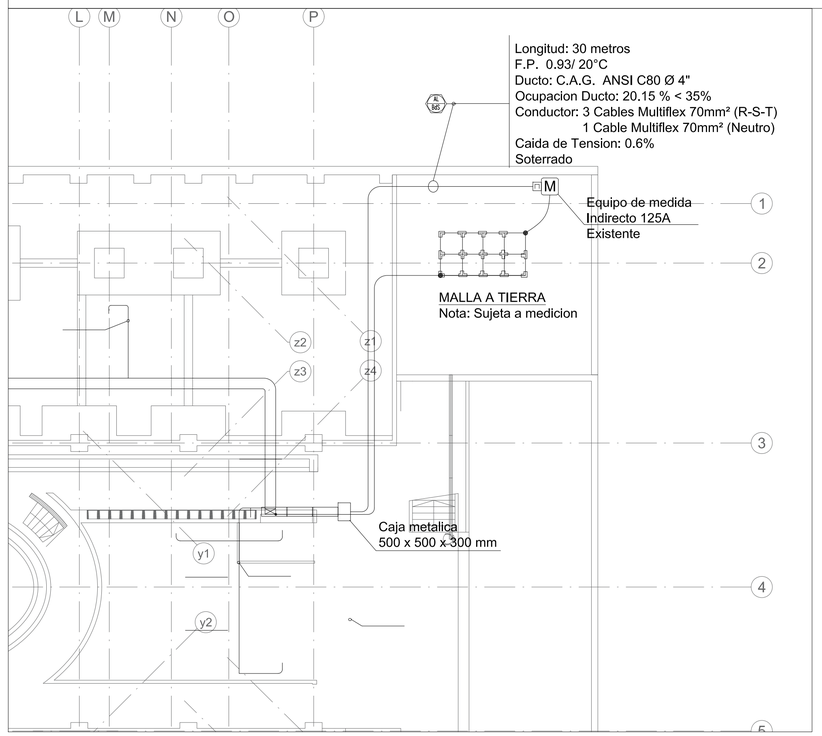

PLANTA EMPLAZAMIENTO EMPALME

SIN ESCALA

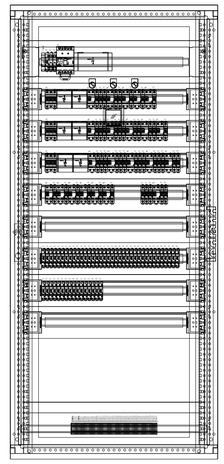

SIMBOLOGIA	
SIMBOLOGIA	DESCRIPCION
	INTERRUPTOR AUTOMATICO MONOFASICO
	INTERRUPTOR AUTOMATICO TRIFASICO
	PULSADOR
	LUCES PILOTOS ø22mm COLOR ROJO
	BORNERAS DE CONEXION
	PROTECTOR DIFERENCIAL MONOFASICO
	PROTECTOR DIFERENCIAL TRIFASICO
	CONTACTOR MONOFASICO AC-1 BOBINA 220V
	CONTACTOR TRIFASICO AC-3 BOBINA 220V
	RELOJ HORARIO
	SELECTOR DE TRES POSICIONES
	CIRCUITO DE ALUMBRADO NORMAL

NOTAS.:

1.- LA LLEGADA A LOS TABLEROS SERA POR SU PARTE SUPERIOR O INFERIOR RESPECTIVAMENTE.
2.- SECCION MINIMA PARA EL ALIMBRADO DE LOS CTOS. DE CONTROL (MUESTRAS DE TENSION) THW, N°14 AWG
3.- SECCION MINIMA PARA EL ALIMBRADO DE CTOS DE ALUMBRADO, Y FUERZA EN CABLE THW, N°12 AWG
4.- MARCA DE CONDUCTORES TIPO PUNTUAL (CONTROL Y FUERZA)
5.- ESTOS PLANOS SON COMPLEMENTARIOS CON LAS ESPECIFICACIONES TECNICAS GENERALES
6.- LOS MATERIALES QUE REQUIEREN CERTIFICACION PARA SU USO, CUMPLEN CON ESTE REQUISITO.
7.- CONSIDERAR UN 25% DE ESPACIO DISPONIBLE EN TODOS LOS TABLEROS ELECTRICOS (BARRAS, BORNERAS, DIFERENCIALES, AUTOMATICOS Y OTROS), ELEMENTOS PARA FUTUROS AUMENTOS. ESTOS PLANOS SE COMPLEMENTAN CON LAS ESPECIFICACIONES
8.- TODOS LOS ELEMENTOS DE CONTROL Y COMANDO PARA EQUIPOS DE CLIMA SERÁN MONTADOS POR ESPECIALISTA EN UN GABINETE INDEPENDIENTE.

DICSA INGENIERÍA Y PROYECTOS
PARA REVISIÓN
18 / 12 / 2020

REV.	POR	FECHA	MOTIVO
3	RRG	01/10/20	Revisión para documento ELE 57/2020


MODIFICACIONES

CONTENIDO:	LÁMINA
DIAGRAMA UNILINEAL Y DETALLES	5
ARCHIVO-CAD :	DIMENSIONES FORMATO: 1189 x 841 mm

CUADRO RESUMEN DE LAMINAS

LAMINA	
1	PLANTA ALUMBRADO Y ENCHUFES SUBTERRANEO
2	PLANTA ALUMBRADO 1° NIVEL
3	PLANTA ENCHUFES 1° NIVEL
4	PLANTA ALUMBRADO DOBLE ALTURA-CORO, ENCHUFES CORO
5	DIAGRAMA UNILINEAL Y DETALLES
6	CUADROS DE CARGA
7	CORRIENTES DÉBILES

UBICACION

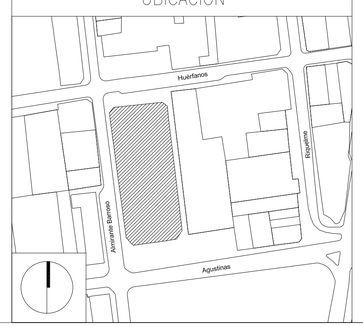

INSCRIPCION N° _____

FECHA : _____

DICSA INGENIERÍA

PROYECTO ELECTRICO DE ALUMBRADO

RESTAURACIÓN BASILCA DEL SALVADOR

CALLE : AGUSTINAS N°1781	LAMINA 05 DE 07 / ESCALA: INDICADA
	FECHA : DICIEMBRE 2019
COMUNA : SANTIAGO	PROYECTO: A.Q.H. / DIBUJO : C.A.A.
	REVISO : A.Q.H.-R.R.G.

PROPIETARIO

PARROQUIA EL SALVADOR
RUT: 453.326-7

R.L.:
RUT:

PROYECTO

ALEJANDRO QUEZADA HELMS
8.957.164-2
INGENIERO ELECTRICO
LIC. SEC. CLASE A