
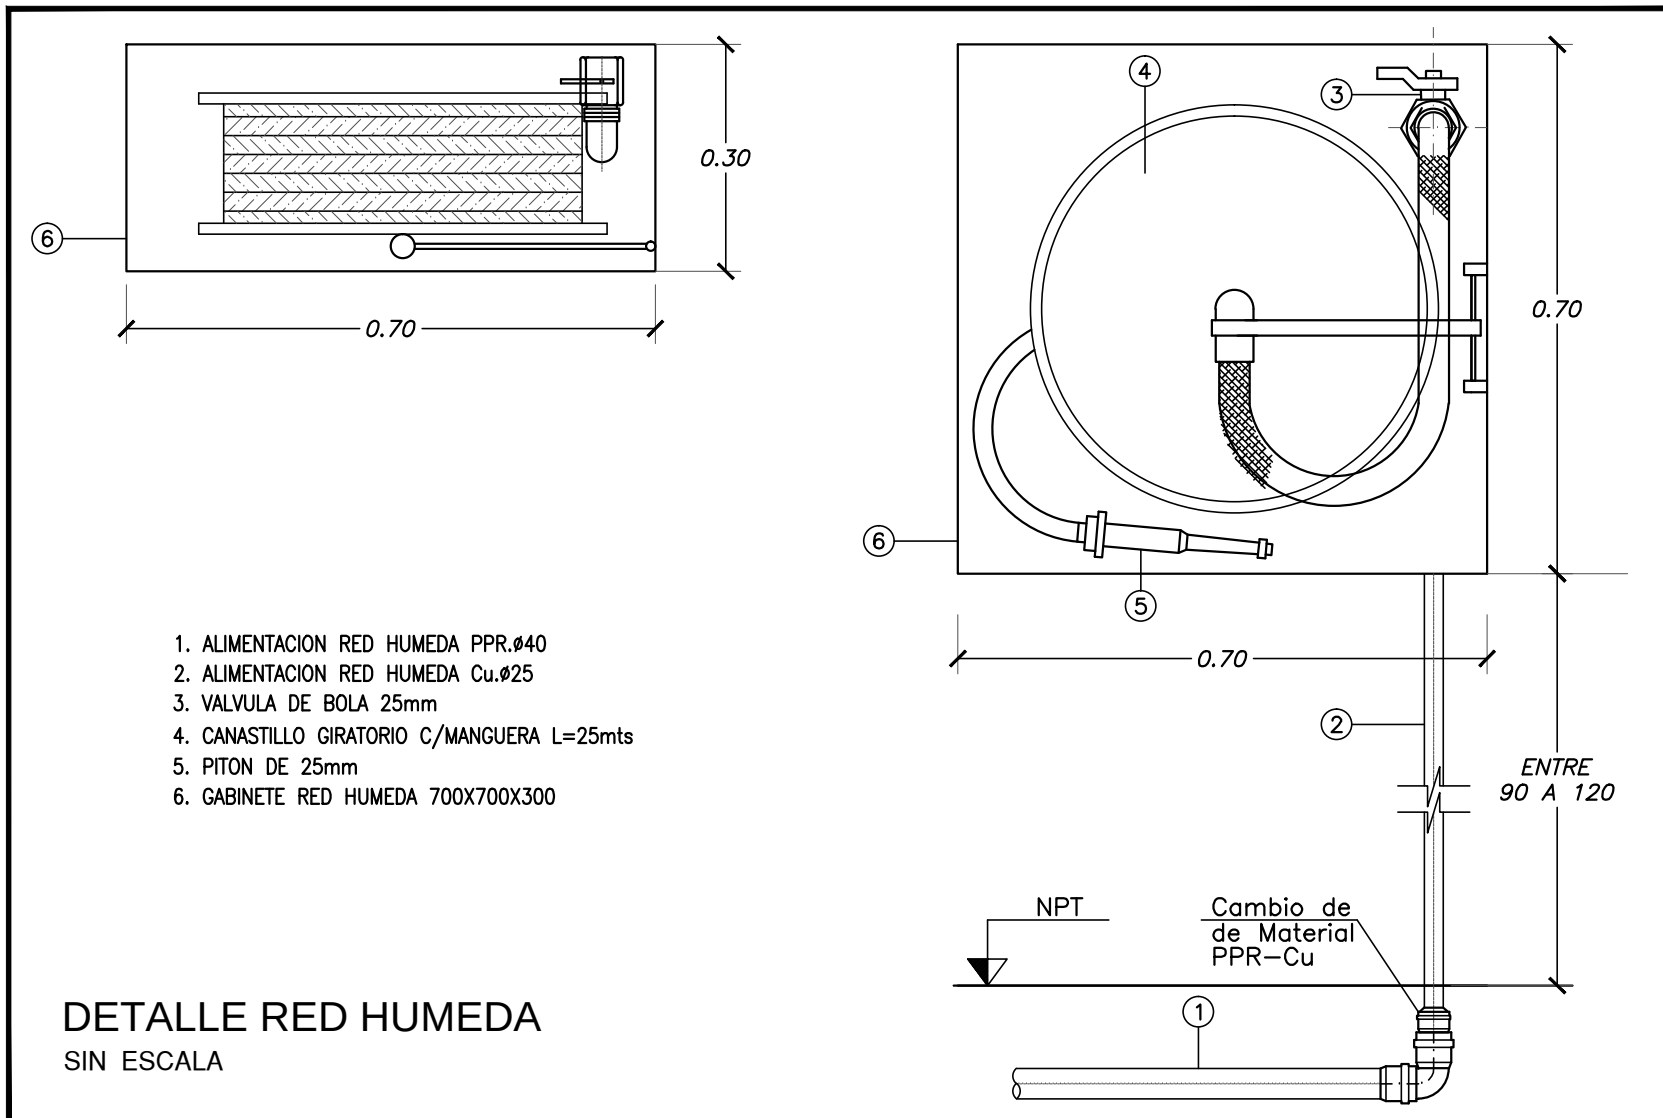
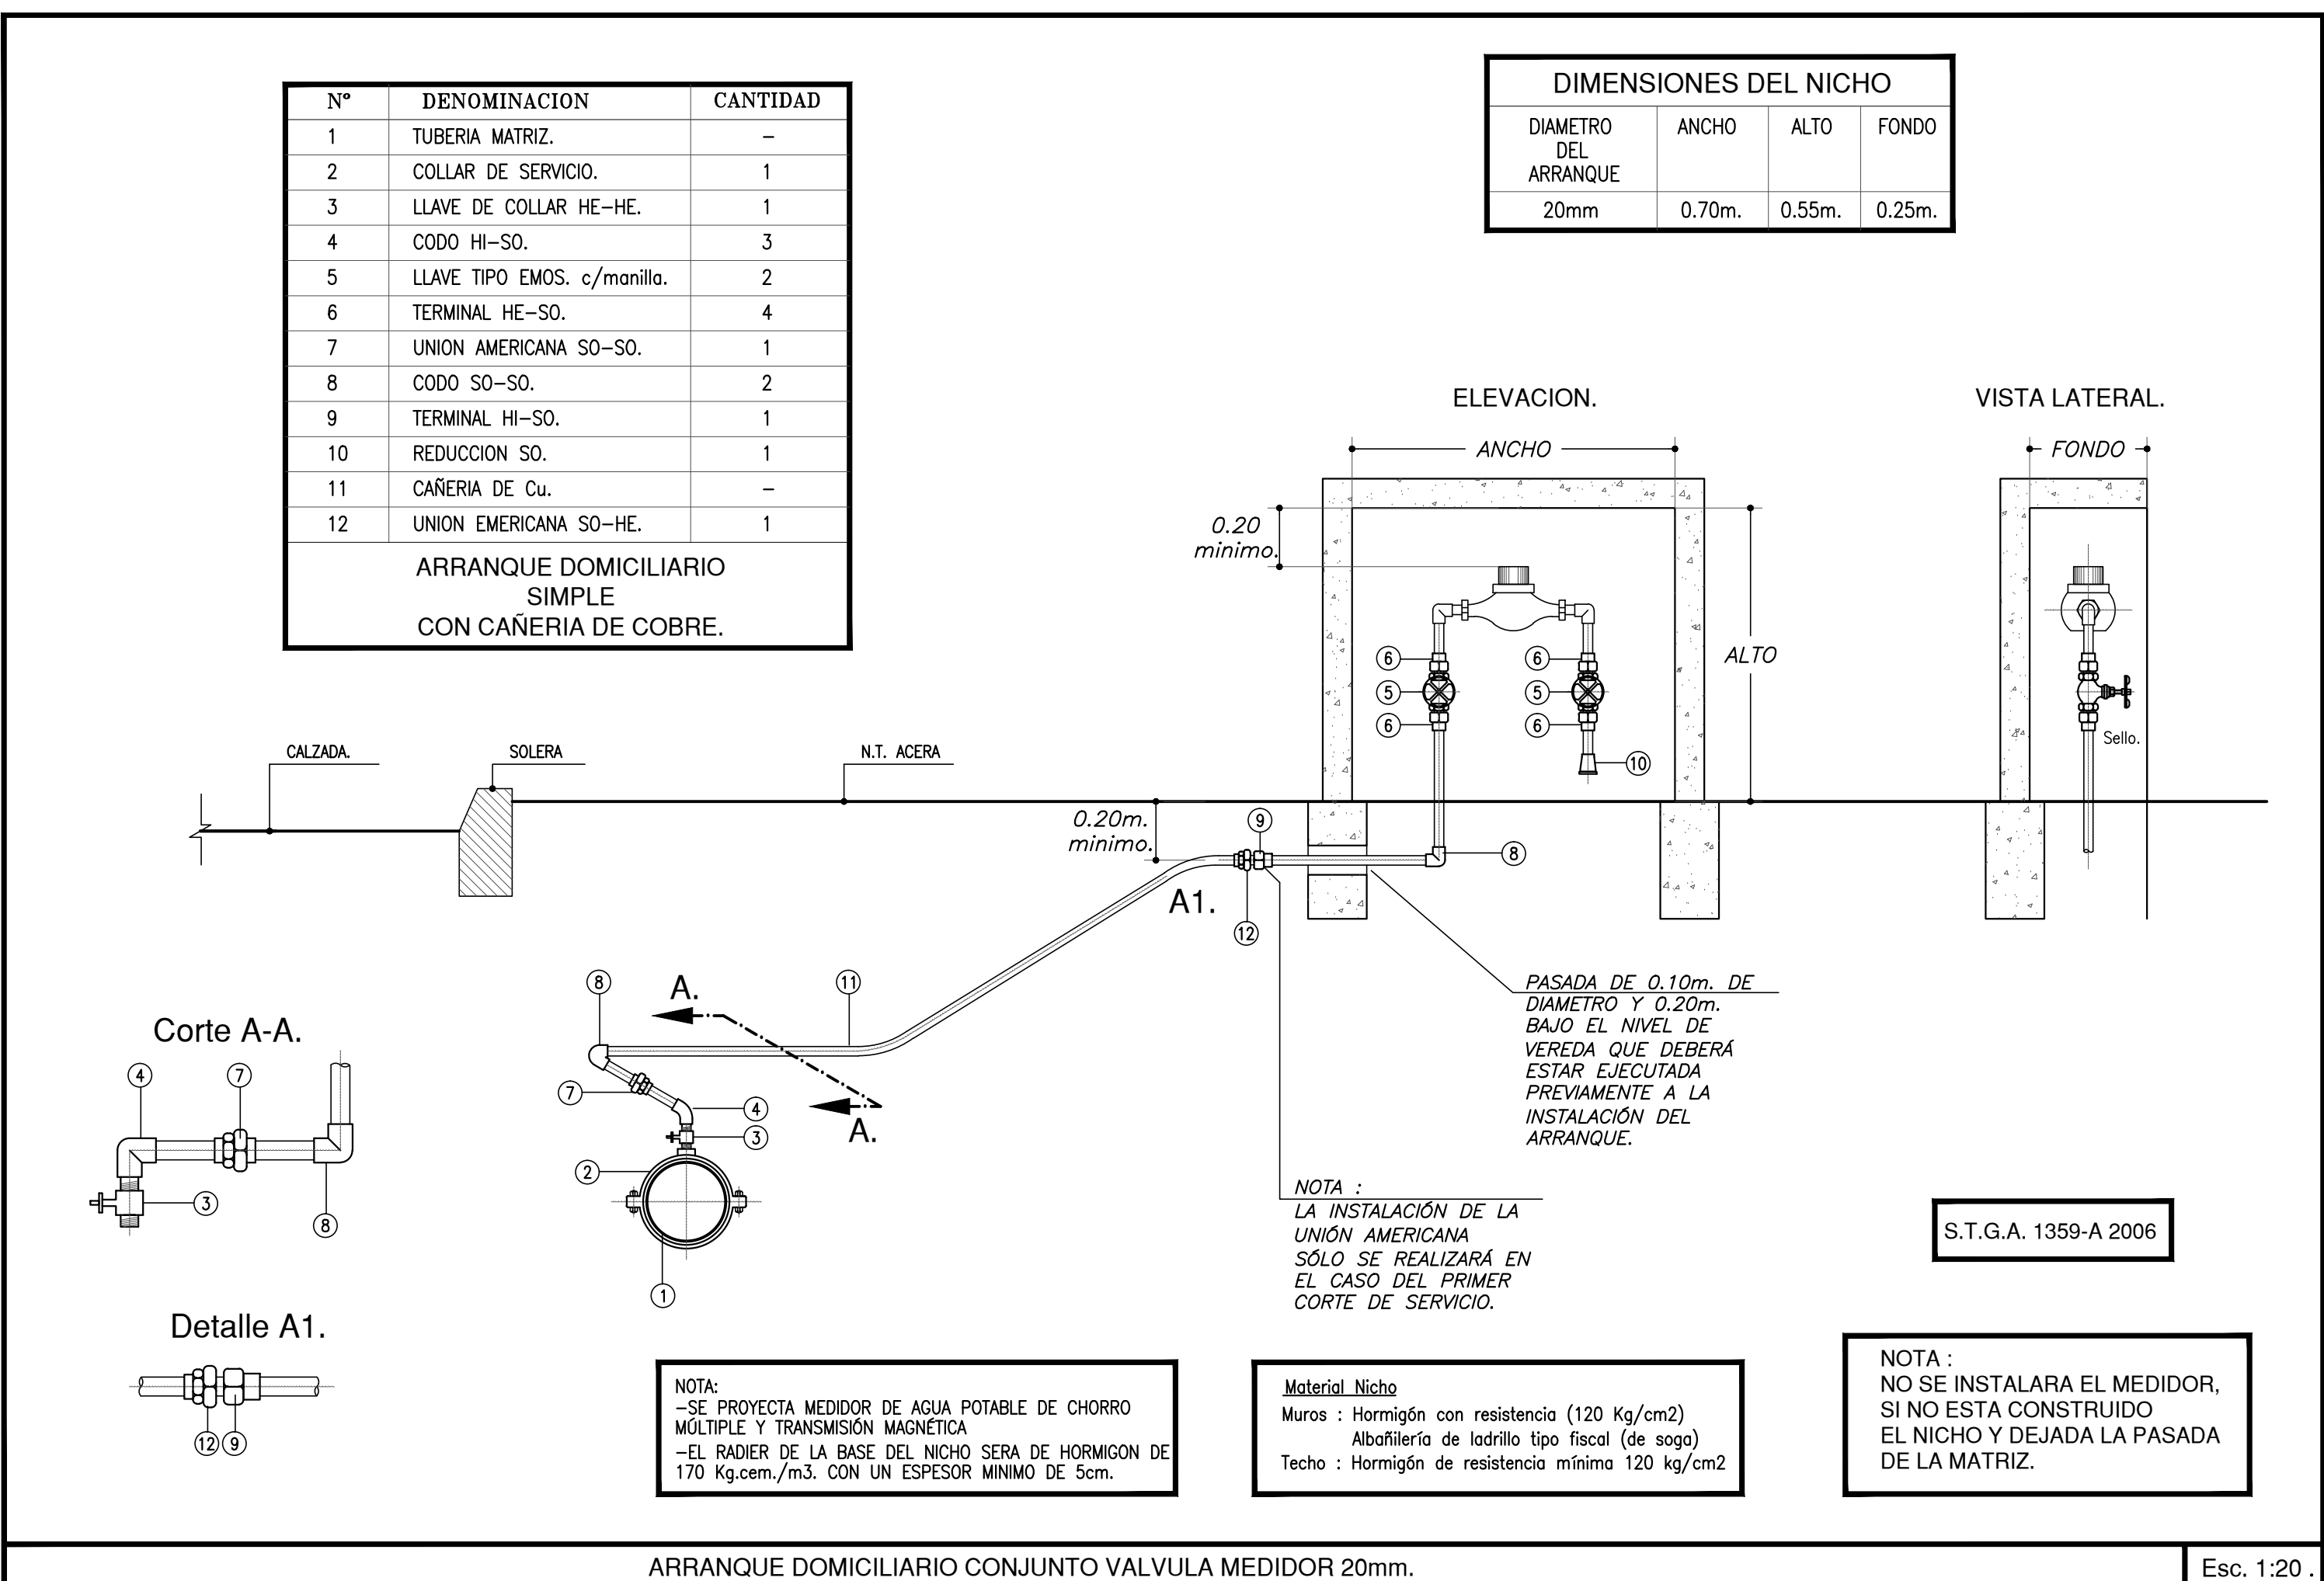
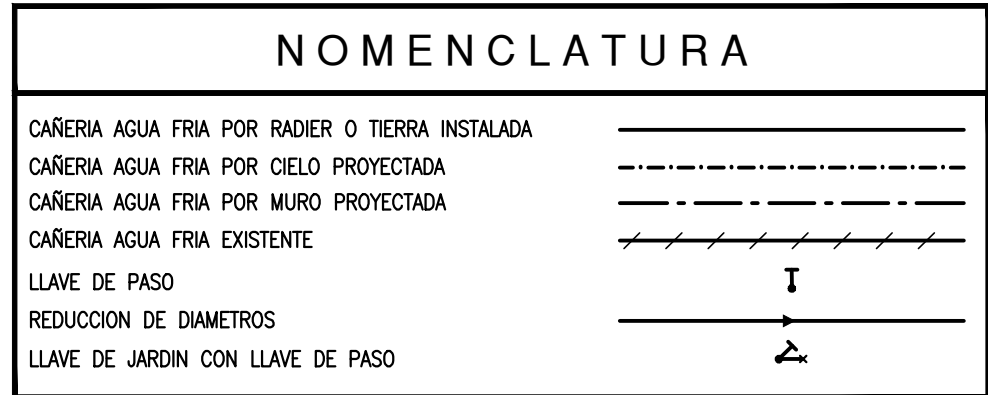
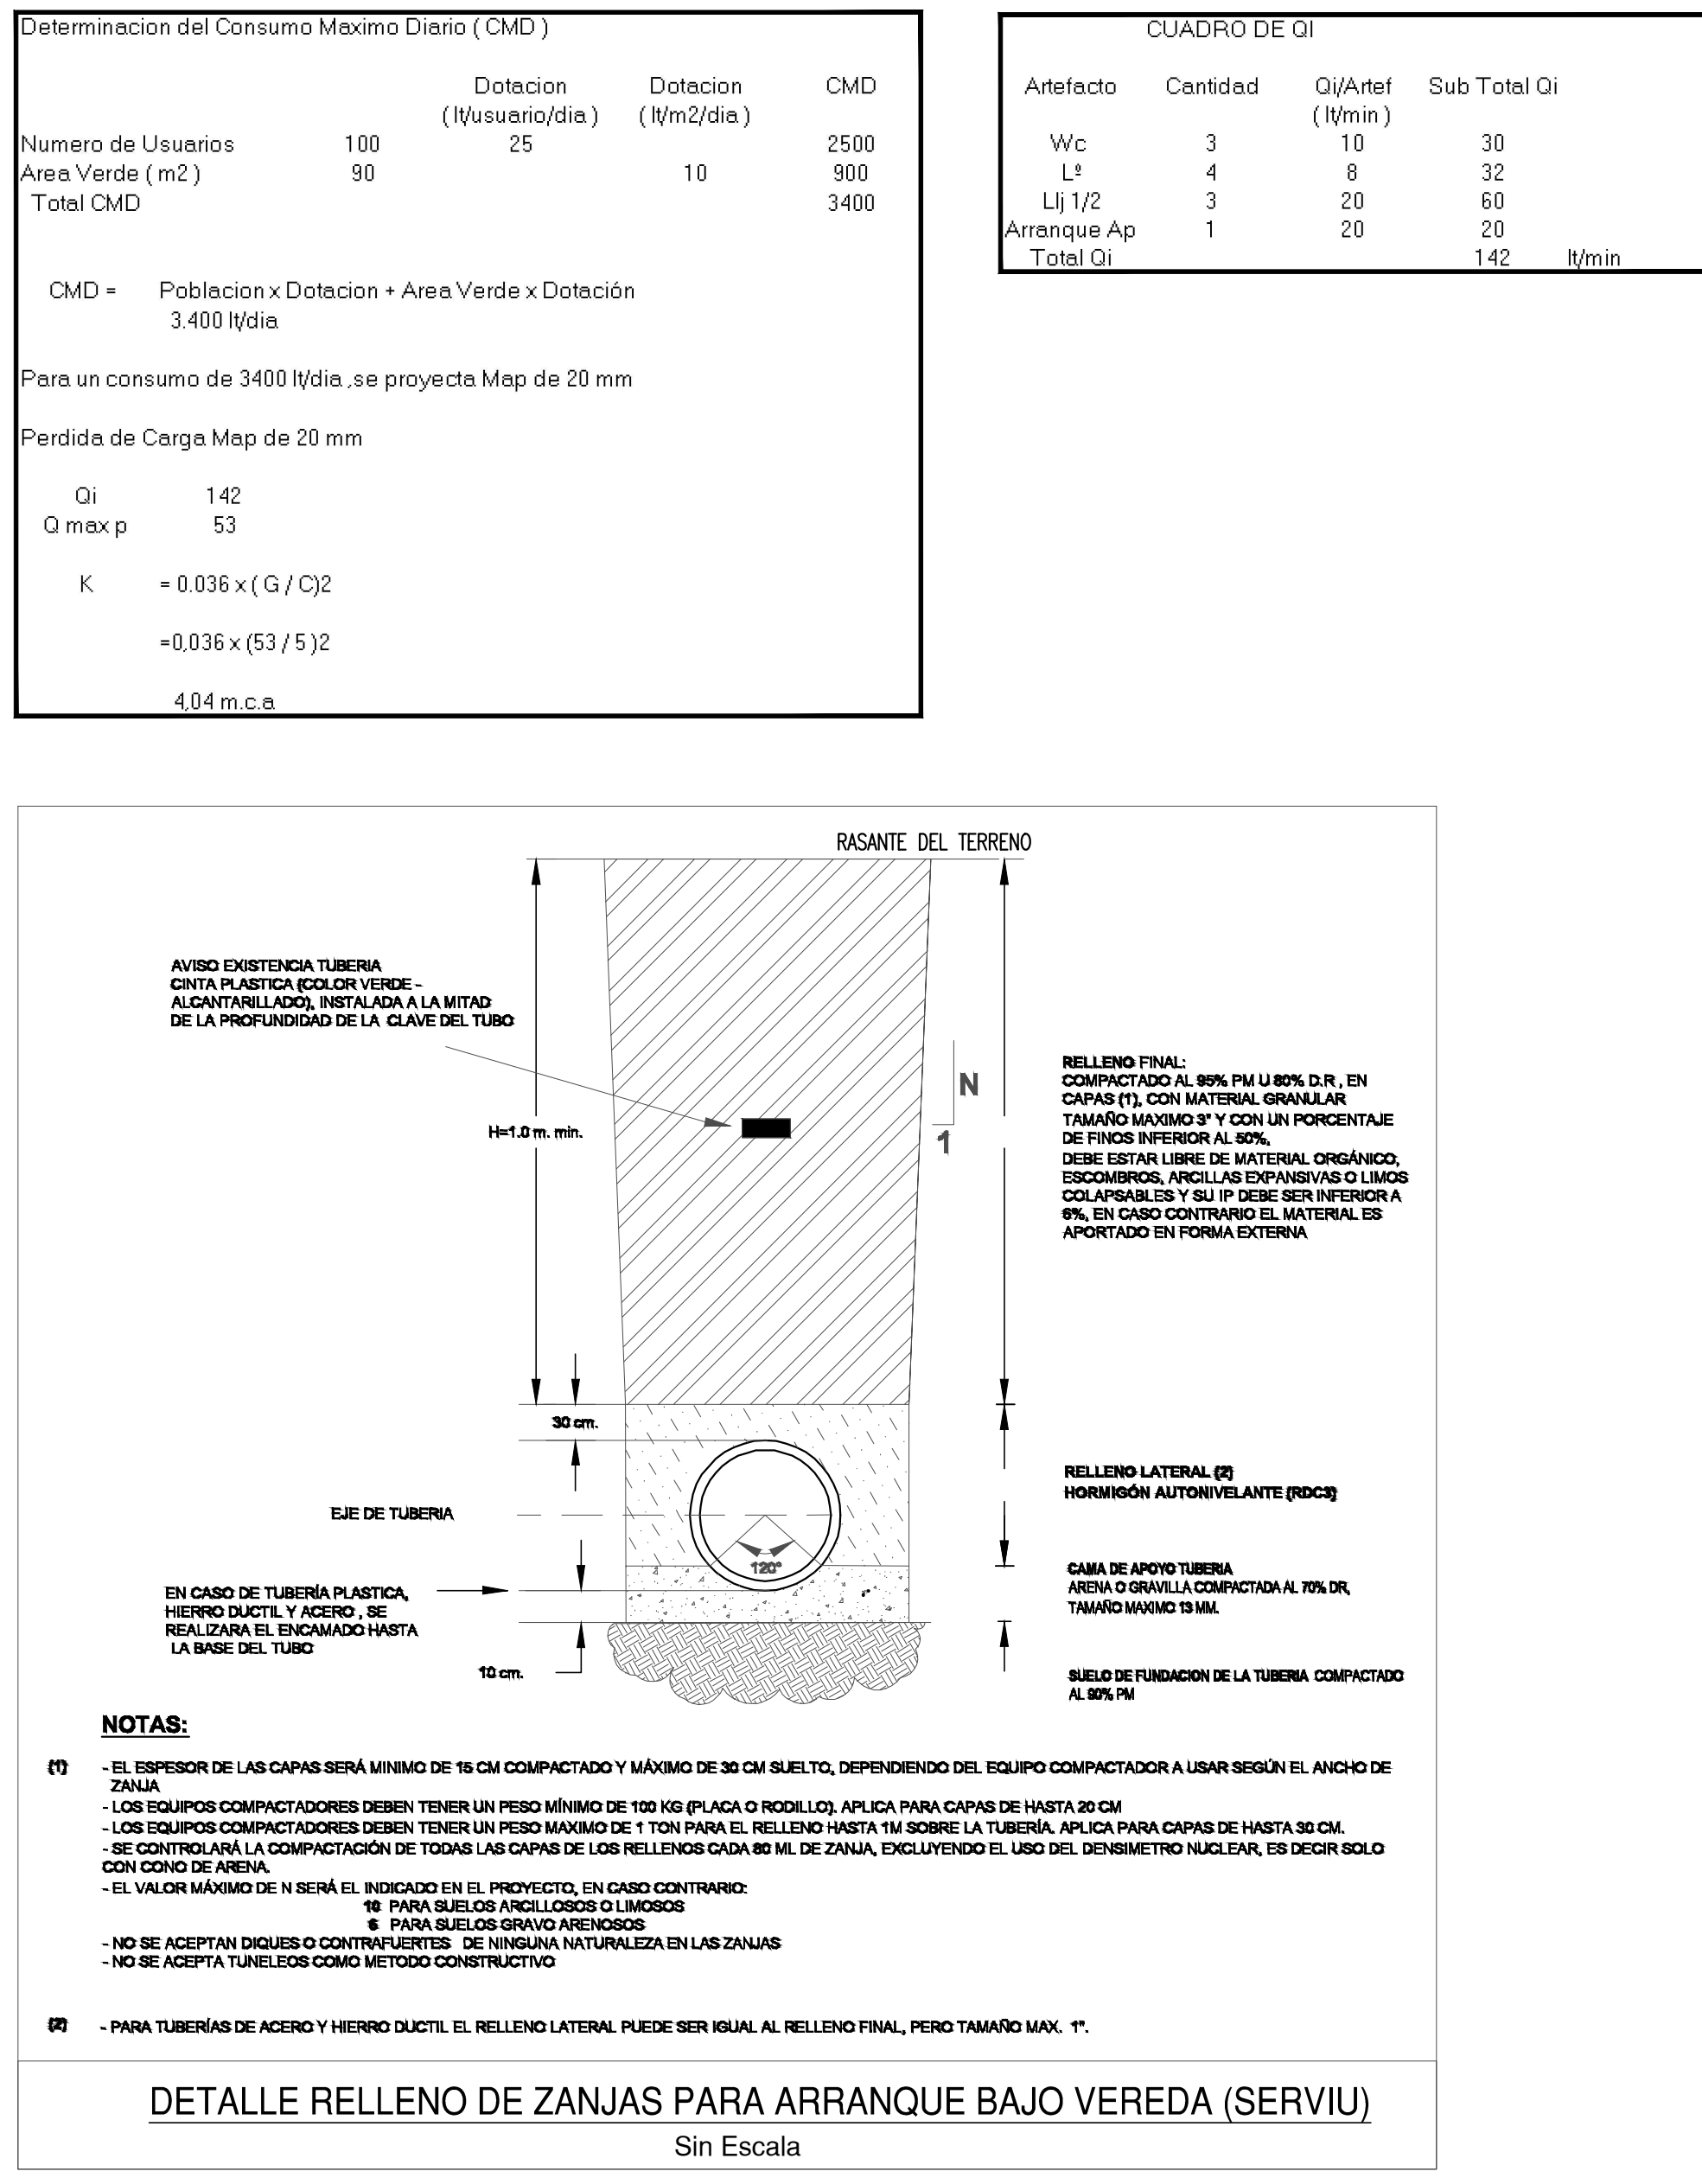


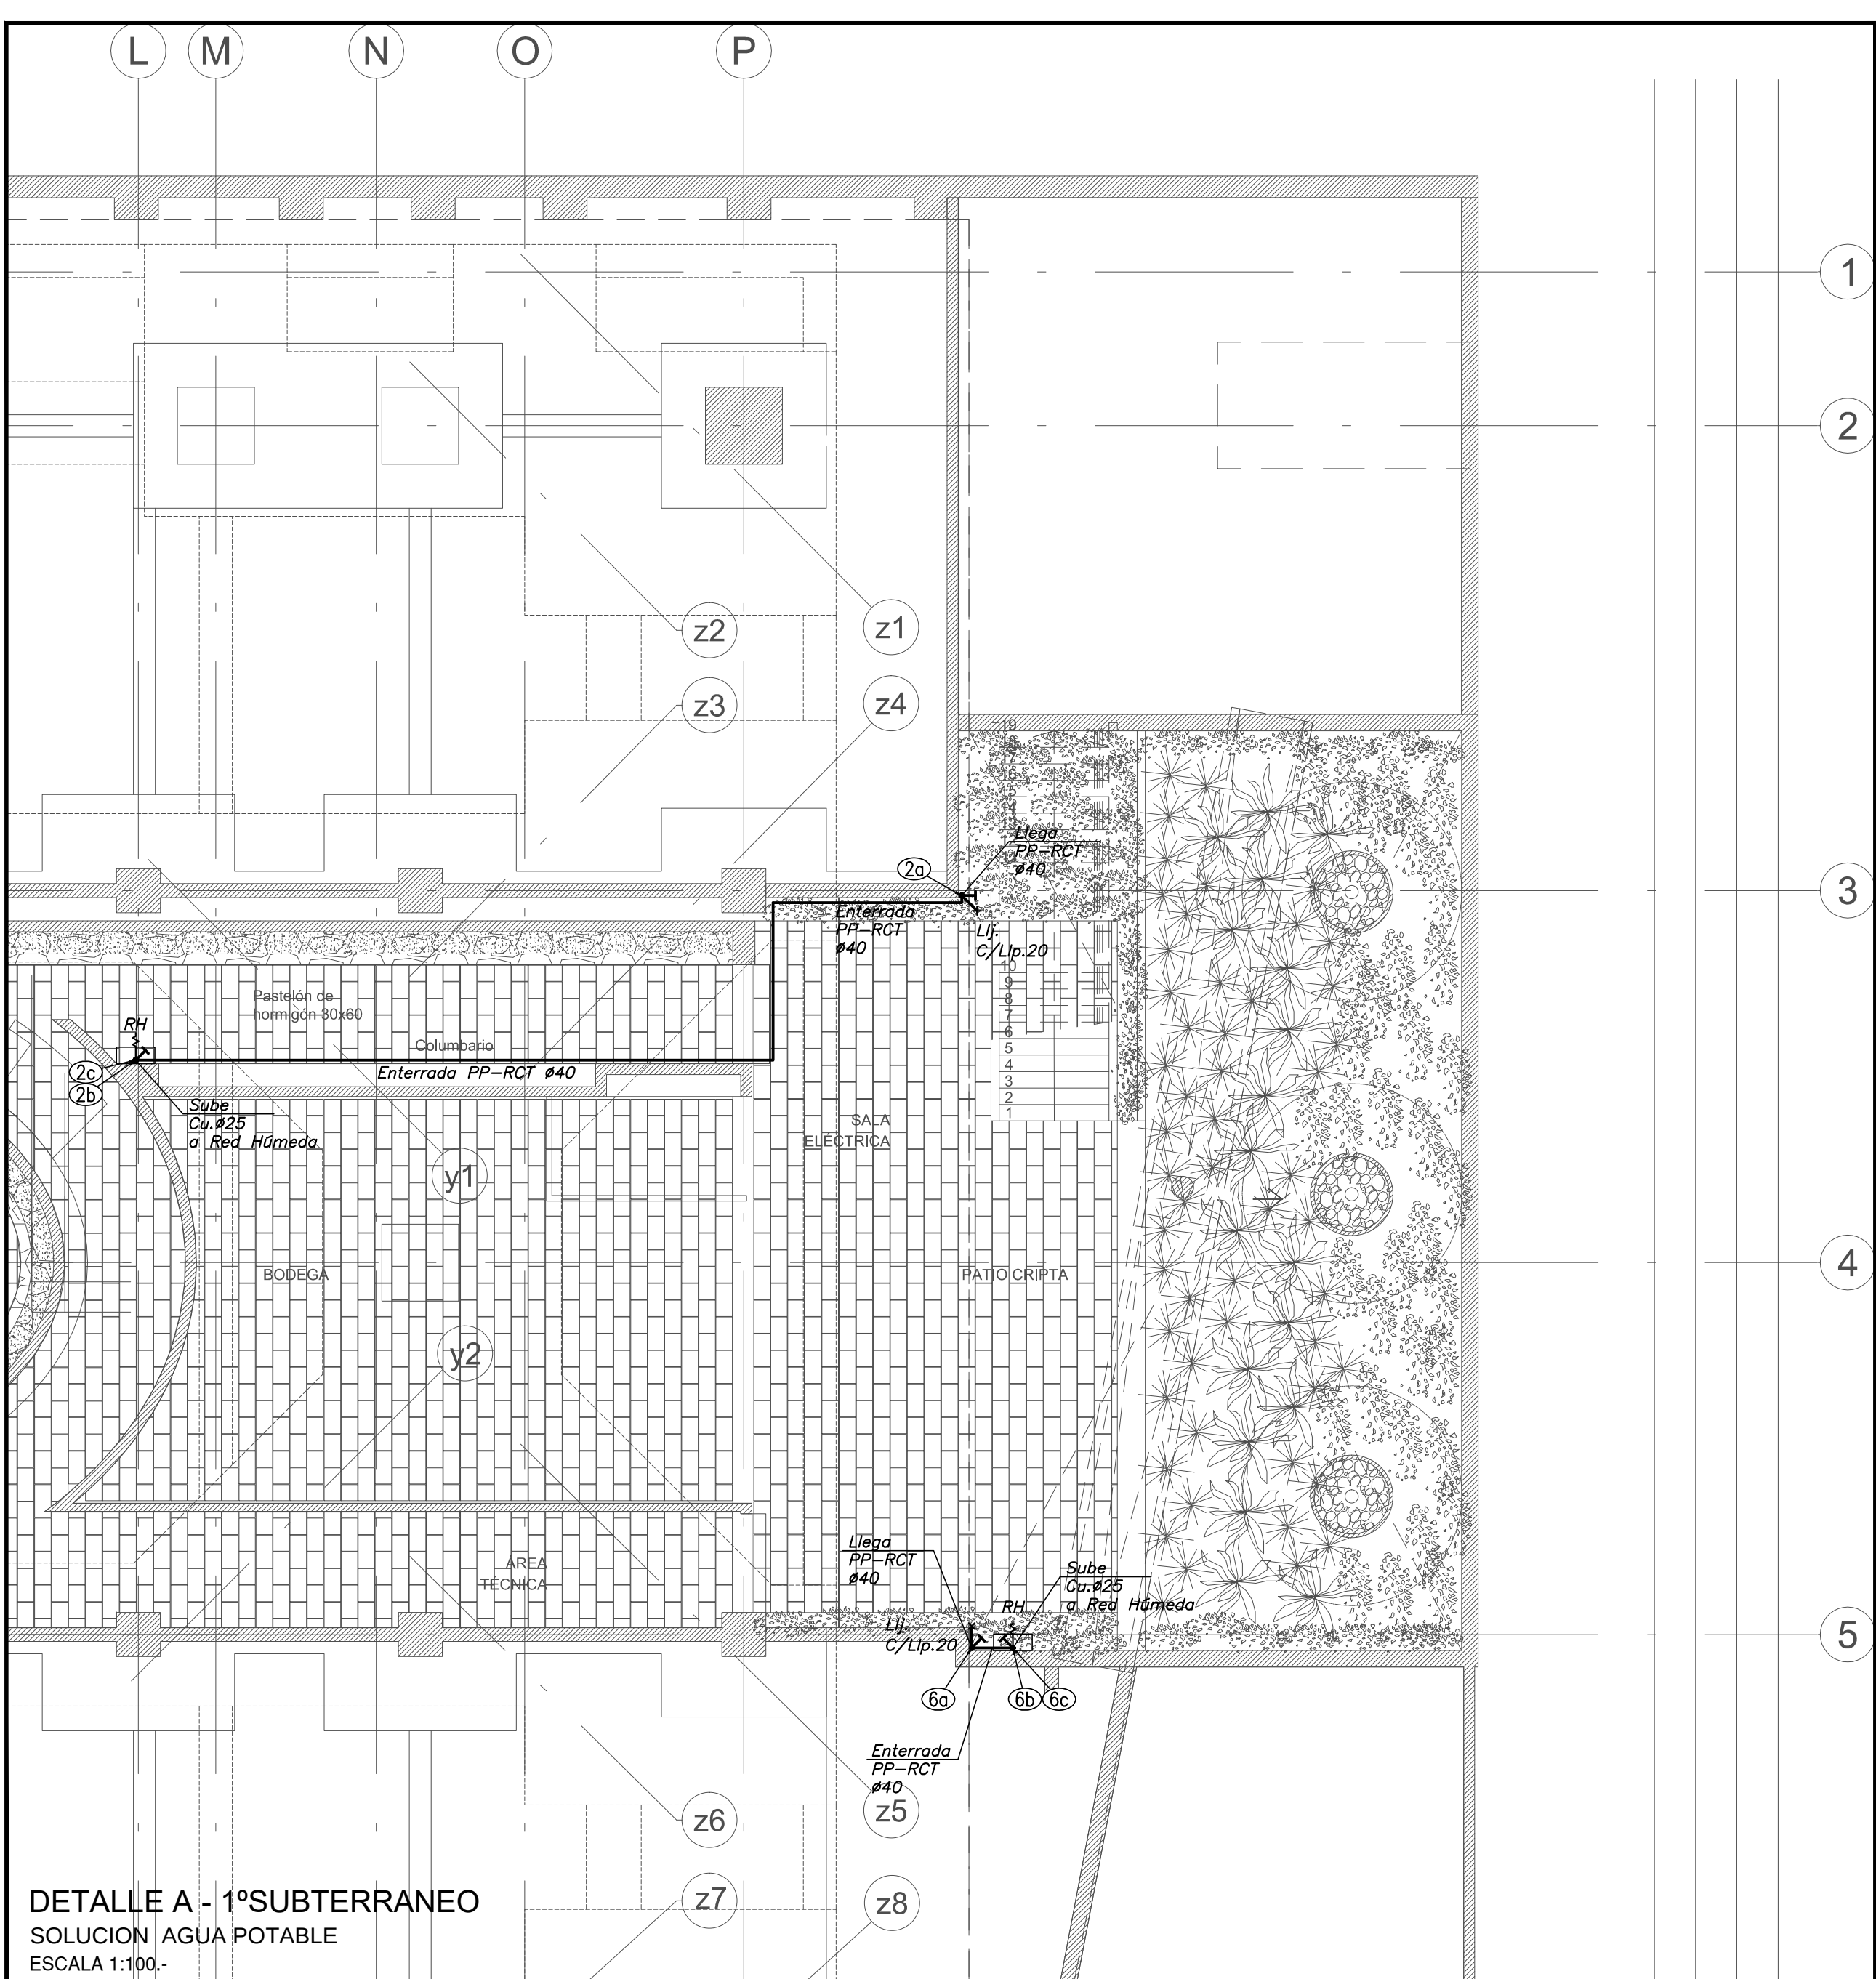

ANÁLISIS DE REACTORES Y HABILITACION BASICA DEL SALVADOR																MEMORIAS DE AGUA POTABLE											
FECHA: FEBRERO 2021																											
Tramo	Pto. In	Ql	Qm	Omp	MAT	D mm	D mm	V m³/s	Pérdida en Cañerías		Pérdida de piezas en el								f	J m.c.a.	fot	J m.c.a.	Cota	Presión m.c.a.			
									Cañ.	J m.c.a.	Pieza	Pieza	Pieza	Pieza	Pieza	Pieza	Pieza	Pieza							Pieza	Pieza	Pieza
AGUA FRÍA																											
MAP -																											
1-10	MAP - 1		142	53	PPR	40	29	1.33	3.40	0.064	0.212	1	2	10	1	0	0.100	0.319	0.003	100.20	14.66						
1-10	2 - 1	124	48	PPR	40	29	1.22	11.30	0.054	0.619	12	1	2	1	0	0.113	0.725	1.044	100.50	12.00							
1-10	2 - 3	104	43	PPR	40	29	1.08	1.00	0.043	0.043	12	1	0	0	0.035	0.079	1.122	100.50	12.22								
1-10	3 - 3a	44	24	PPR	25	18	1.55	7.80	0.146	1.139	14	1	0	0	0.219	1.358	2.480	100.50	11.58								
1-10	3b - 3	21	11	PPR	25	18	1.35	0.80	0.113	0.090	12	1	2	3	11	1	1.027	2.328	4.945	100.50	8.75						
1-10	3b - 4	18	18	PPR	25	18	1.18	1.47	0.089	1.301	14	1	2	3	11	1	1.027	2.328	4.945	100.50	8.75						
1-10	4 - 5	10	10	PPR	20	14.4	1.02	2.50	0.088	0.220	12	1	2	3	11	2	0.171	0.391	5.955	100.50	1.66						
1-10	3 - 6	60	29	PPR	40	29	0.74	14.80	0.021	0.318	12	1	2	1	0	0.042	0.359	1.481	100.50	12.22							
1-10	6 - 7	40	22	PPR	25	18	1.45	4.40	0.129	0.598	12	1	0	0	0.084	0.633	1.144	100.20	11.89								
1-10	7 - 8	8	20	20	PPR	25	14.4	2.05	4.50	0.317	1.428	14	1	2	2	10	1	0.811	2.240	4.354	100.20	9.65					
1-10	7 - 9	20	20	PPR	25	18	1.31	5.40	0.108	0.581	12	1	2	3	10	1	0.306	0.887	3.001	100.20	11.00						
1-10	1 - 1a	100	42	PPR	40	29	1.05	5.30	0.041	0.218	14	1	2	1	0	0.151	0.369	0.688	100.50	13.01							
1-10	1a - 1b	100	42	PPR	40	29	1.05	1.10	0.041	0.045	12	1	2	1	0	0.084	0.129	0.817	100.50	12.88							
1-10	1b - 1c	100	42	Qu L	25	26.04	1.30	1.50	0.086	0.129	2	2	10	1	0	0.172	0.302	1.119	102.00	11.08							
1-10	2 - 2a	100	42	PPR	40	29	1.05	5.30	0.041	0.218	14	1	2	1	0	0.151	0.369	1.413	96.20	16.59							
1-10	2a - 2b	100	42	PPR	40	29	1.05	16.00	0.041	0.741	14	1	2	2	0	0.202	0.942	2.355	96.20	15.64							
1-10	2b - 2c	100	42	PPR	25	26.04	1.30	1.50	0.086	0.129	2	2	10	1	0	0.172	0.302	2.657	97.70	13.84							
1-10	6 - 6a	100	42	PPR	40	29	1.05	5.10	0.041	0.210	14	1	2	1	0	0.151	0.361	1.821	96.20	16.16							
1-10	6a - 6b	100	42	PPR	40	29	1.05	4.30	0.041	0.177	14	1	2	2	0	0.202	0.379	2.242	96.20	15.78							
1-10	6b - 6c	100	42	Qu L	25	26.04	1.30	1.50	0.086	0.129	2	2	10	1	0	0.172	0.302	2.523	97.70	13.98							
Nota: En caso de incendio se considera que funciona solo 1 gabinete de incendio.																											

[illegible]