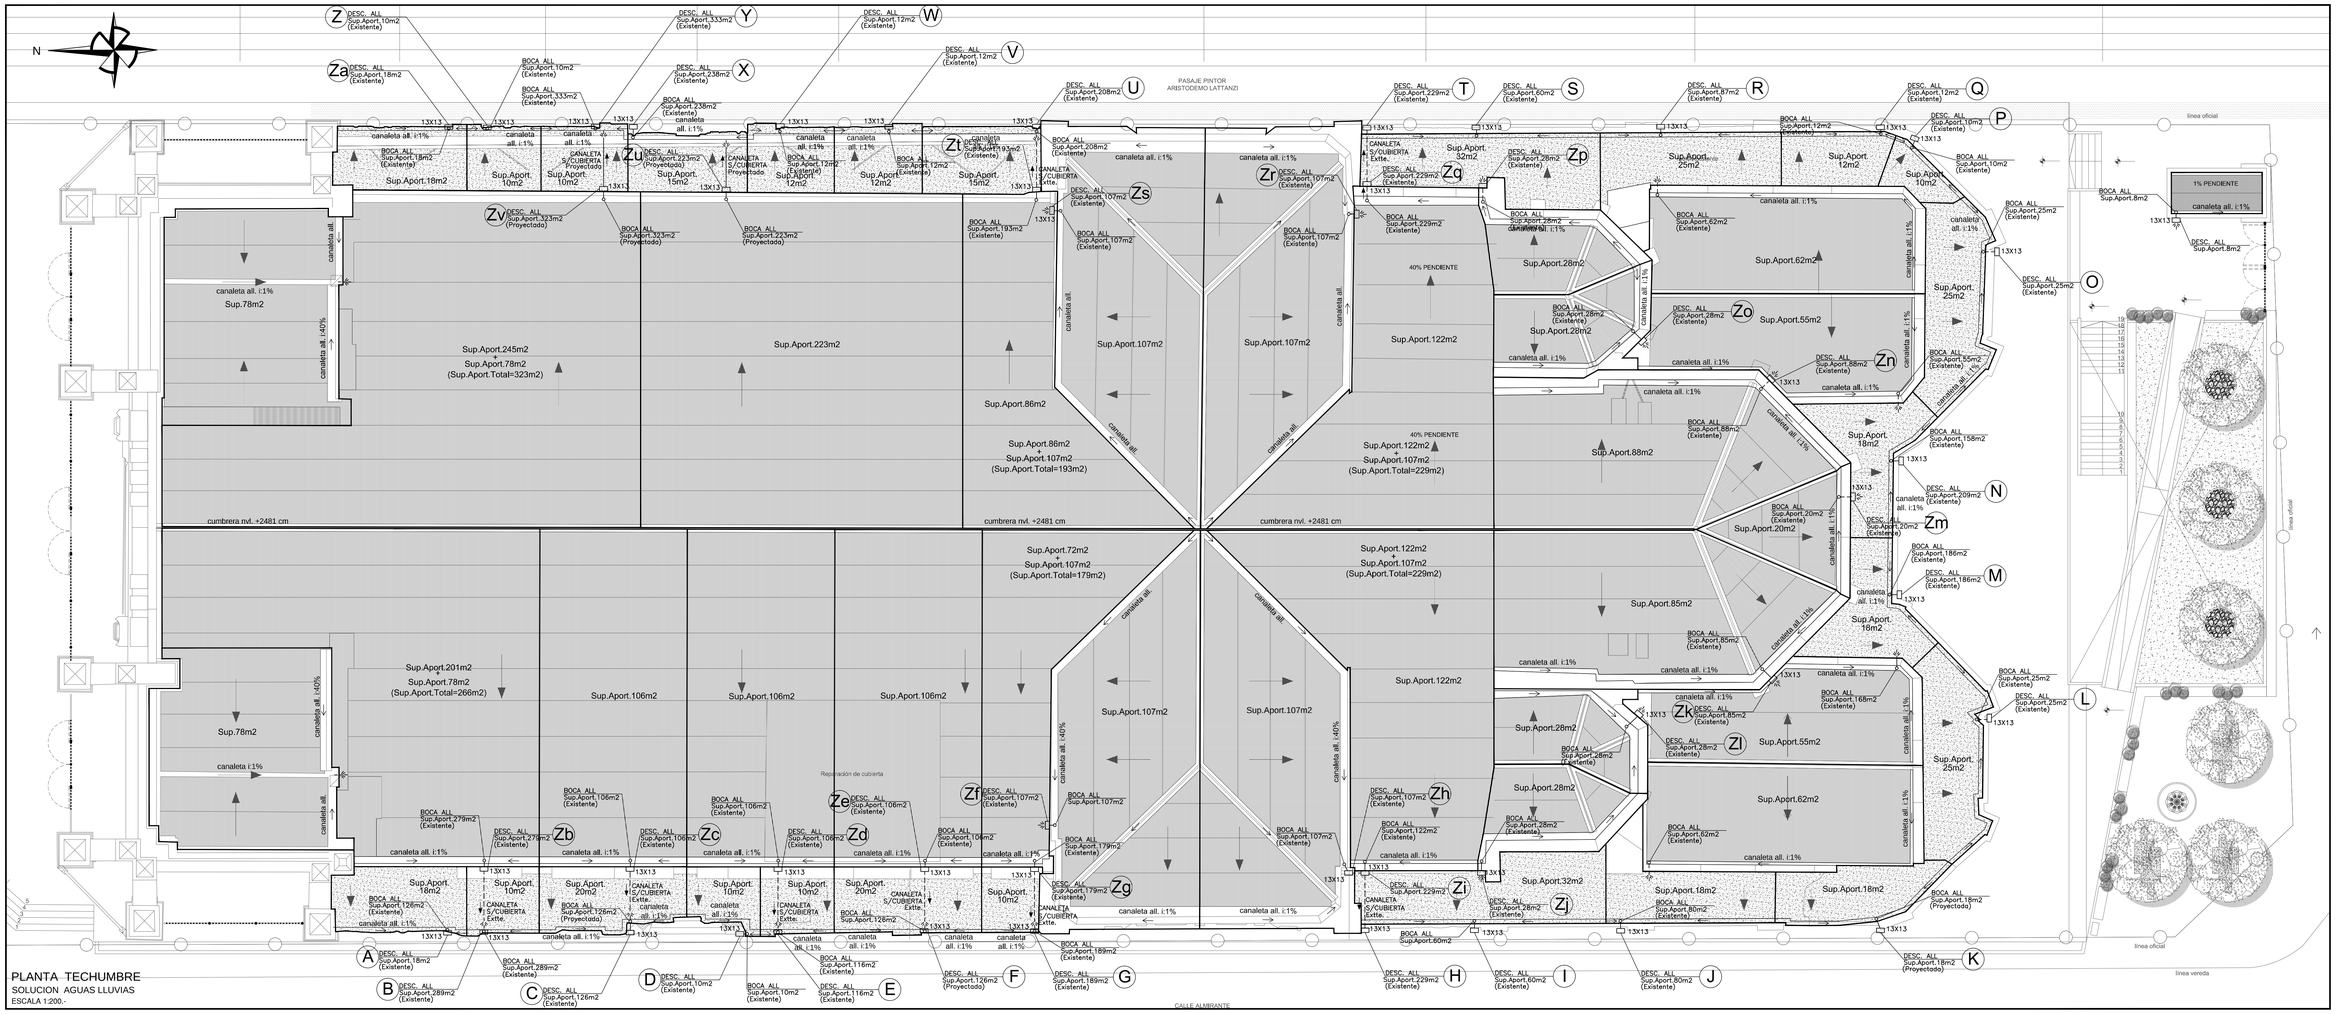

PLANTA TECHUMBRE
SOLUCION AGUAS LLUVIAS
ESCALA 1:200.-

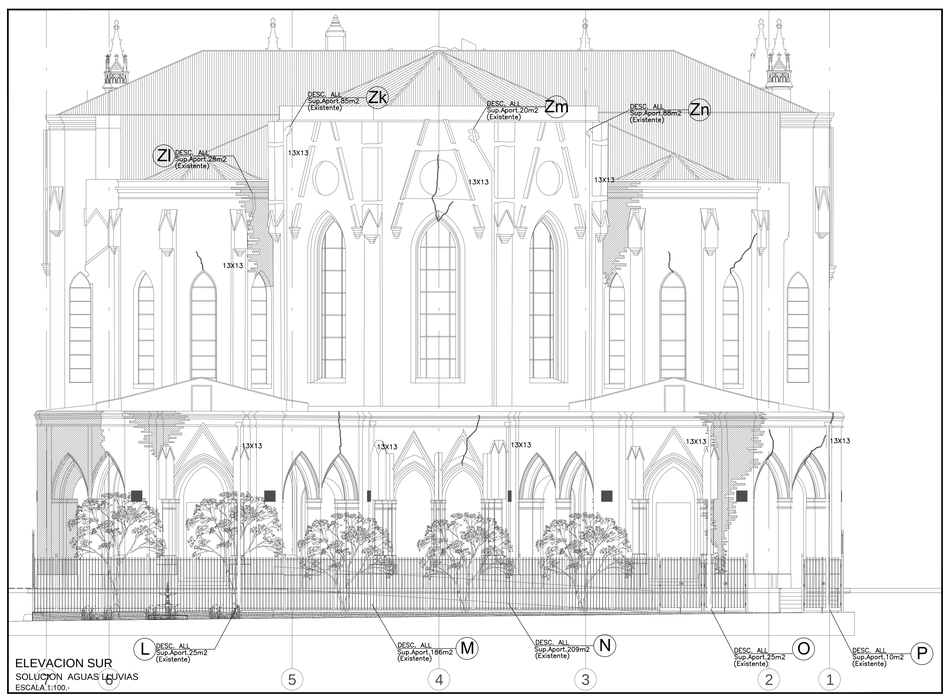

ELEVACION SUR
SOLUCION AGUAS LLUVIAS
ESCALA 1:100.-

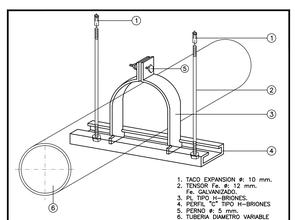

ABRAZADERA TIPO H-BRIONES COLGADA
SIN ESCALA.-

NOMENCLATURA

CAÑERIA PROYECTADA	———
CAÑERIA EXISTENTE	- - - - - -
C.I. A.LL. DESBARRADORA PROYECTADA	○
SENTIDO DE ESCURRIMIENTO	→
BAJADA AGUAS LLUVIAS	•
BOCA AGUAS LLUVIAS	○

CUADRO RESUMEN BAJADAS AGUAS LLUVIAS

BAJADA	SUP. APORTANTE (m2)	DESCARGA	OBSERVACIONES
A	18	A CALZADA	EXISTENTE
B	289	A CALZADA	EXISTENTE
C	126	A CALZADA	EXISTENTE
D	10	A CALZADA	EXISTENTE
E	116	A CALZADA	EXISTENTE
F	126	A CALZADA	PROYECTADA
G	189	A CALZADA	EXISTENTE
H	229	A CALZADA	EXISTENTE
I	60	A CALZADA	EXISTENTE
J	80	A CALZADA	EXISTENTE
K	18	A CALZADA	PROYECTADA
L	25	A DREN	EXISTENTE
M	186	A DREN	EXISTENTE
N	209	A DREN	EXISTENTE
O	25	A DREN	EXISTENTE
P	10	A VEREDA	EXISTENTE
Q	12	A VEREDA	EXISTENTE
R	87	A VEREDA	EXISTENTE
S	60	A VEREDA	EXISTENTE
T	229	A VEREDA	EXISTENTE
U	208	A VEREDA	EXISTENTE
V	12	A VEREDA	EXISTENTE
W	12	A VEREDA	EXISTENTE
X	238	A VEREDA	EXISTENTE
Y	333	A VEREDA	EXISTENTE
Z	10	A VEREDA	EXISTENTE
Za	18	A VEREDA	EXISTENTE
Zb	279	A CORREDOR EXTERIOR 2ºPISO	EXISTENTE
Zc	106	A CORREDOR EXTERIOR 2ºPISO	EXISTENTE
Zd	106	A CORREDOR EXTERIOR 2ºPISO	EXISTENTE
Ze	106	A CORREDOR EXTERIOR 2ºPISO	EXISTENTE
Zf	107	A CORREDOR EXTERIOR 2ºPISO	EXISTENTE
Zg	179	A CORREDOR EXTERIOR 2ºPISO	EXISTENTE
Zh	107	A CORREDOR EXTERIOR 2ºPISO	EXISTENTE
Zi	229	A CORREDOR EXTERIOR 2ºPISO	EXISTENTE
Zj	28	A CORREDOR EXTERIOR 2ºPISO	EXISTENTE
Zk	85	A CORREDOR EXTERIOR 2ºPISO	EXISTENTE
Zl	28	A CORREDOR EXTERIOR 2ºPISO	EXISTENTE
Zm	20	A CORREDOR EXTERIOR 2ºPISO	EXISTENTE
Zn	88	A CORREDOR EXTERIOR 2ºPISO	EXISTENTE
Zo	28	A CORREDOR EXTERIOR 2ºPISO	EXISTENTE
Zp	28	A CORREDOR EXTERIOR 2ºPISO	EXISTENTE
Zq	229	A CORREDOR EXTERIOR 2ºPISO	EXISTENTE
Zr	107	A CORREDOR EXTERIOR 2ºPISO	EXISTENTE
Zs	107	A CORREDOR EXTERIOR 2ºPISO	EXISTENTE
Zt	193	A CORREDOR EXTERIOR 2ºPISO	EXISTENTE
Zu	223	A CORREDOR EXTERIOR 2ºPISO	PROYECTADA
Zv	323	A CORREDOR EXTERIOR 2ºPISO	PROYECTADA
SUP. TOTAL TECHUMBRE	**2935**		

CUADRO REVISIONES AGUAS LLUVIAS

REV.	FECHA	MODIFICACIÓN	ATENDIÓ
-	-	-	-
A	05/02/2021	AGUAS LLUVIAS BASILICA DEL SALVADOR	C.S.D.

PROYECTO	PROY. M.A.D.	NOMBRE ARCHIVO	FECHA	VERSION
	DIB. C.S.D.	IS_BASILICA_EL_SALVADOR	FEBRERO 2020	A
	REV. M.A.D.			

PROYECTO DE INSTALACION DE AGUAS LLUVIAS DOMICILIARIA

PROYECTO INFORMATIVO	Lamina
N°: Fecha:	N° 01 DE 03
AVISO DE INICIO N°	FECHA :
CERTIFICADO DE FACTIBILIDAD N° 6422	FECHA : 01/07/2019

RESTAURACIÓN Y HABILITACIÓN BASILICA DEL SALVADOR

HUERFANOS Nº1780 / AGUSTINAS Nº1781
Region Metropolitana

SANTIAGO ESCALAS INDICADAS

UBICACION
N

FIRMAS

PROYECTISTA

MARIA ANGELICA DENEGRI D.
INGENIERO CIVIL U.CH.
RUT: 6.060.156-9
REINA VICTORIA 6842 - LA REINA
FONO: 22 895 20 08
adenegri@dyingenieros.cl

PROPIETARIO

ARZOBISPADO DE SANTIAGO
RUT: 81.795.100-7
PLAZA DE ARMAS 444, SANTIAGO

CONTRATISTA

(CONTRATISTA)
PROFESION : ********
RUT : ********
DOMICILIO : ********
FONO : ********
E-mail : ********

PROYECTO DEFINITIVO
CERTIFICADO DE RECEPCION
N°_____ Fecha _____

FIRMA EMPRESA DE SERVICIOS SANITARIOS