



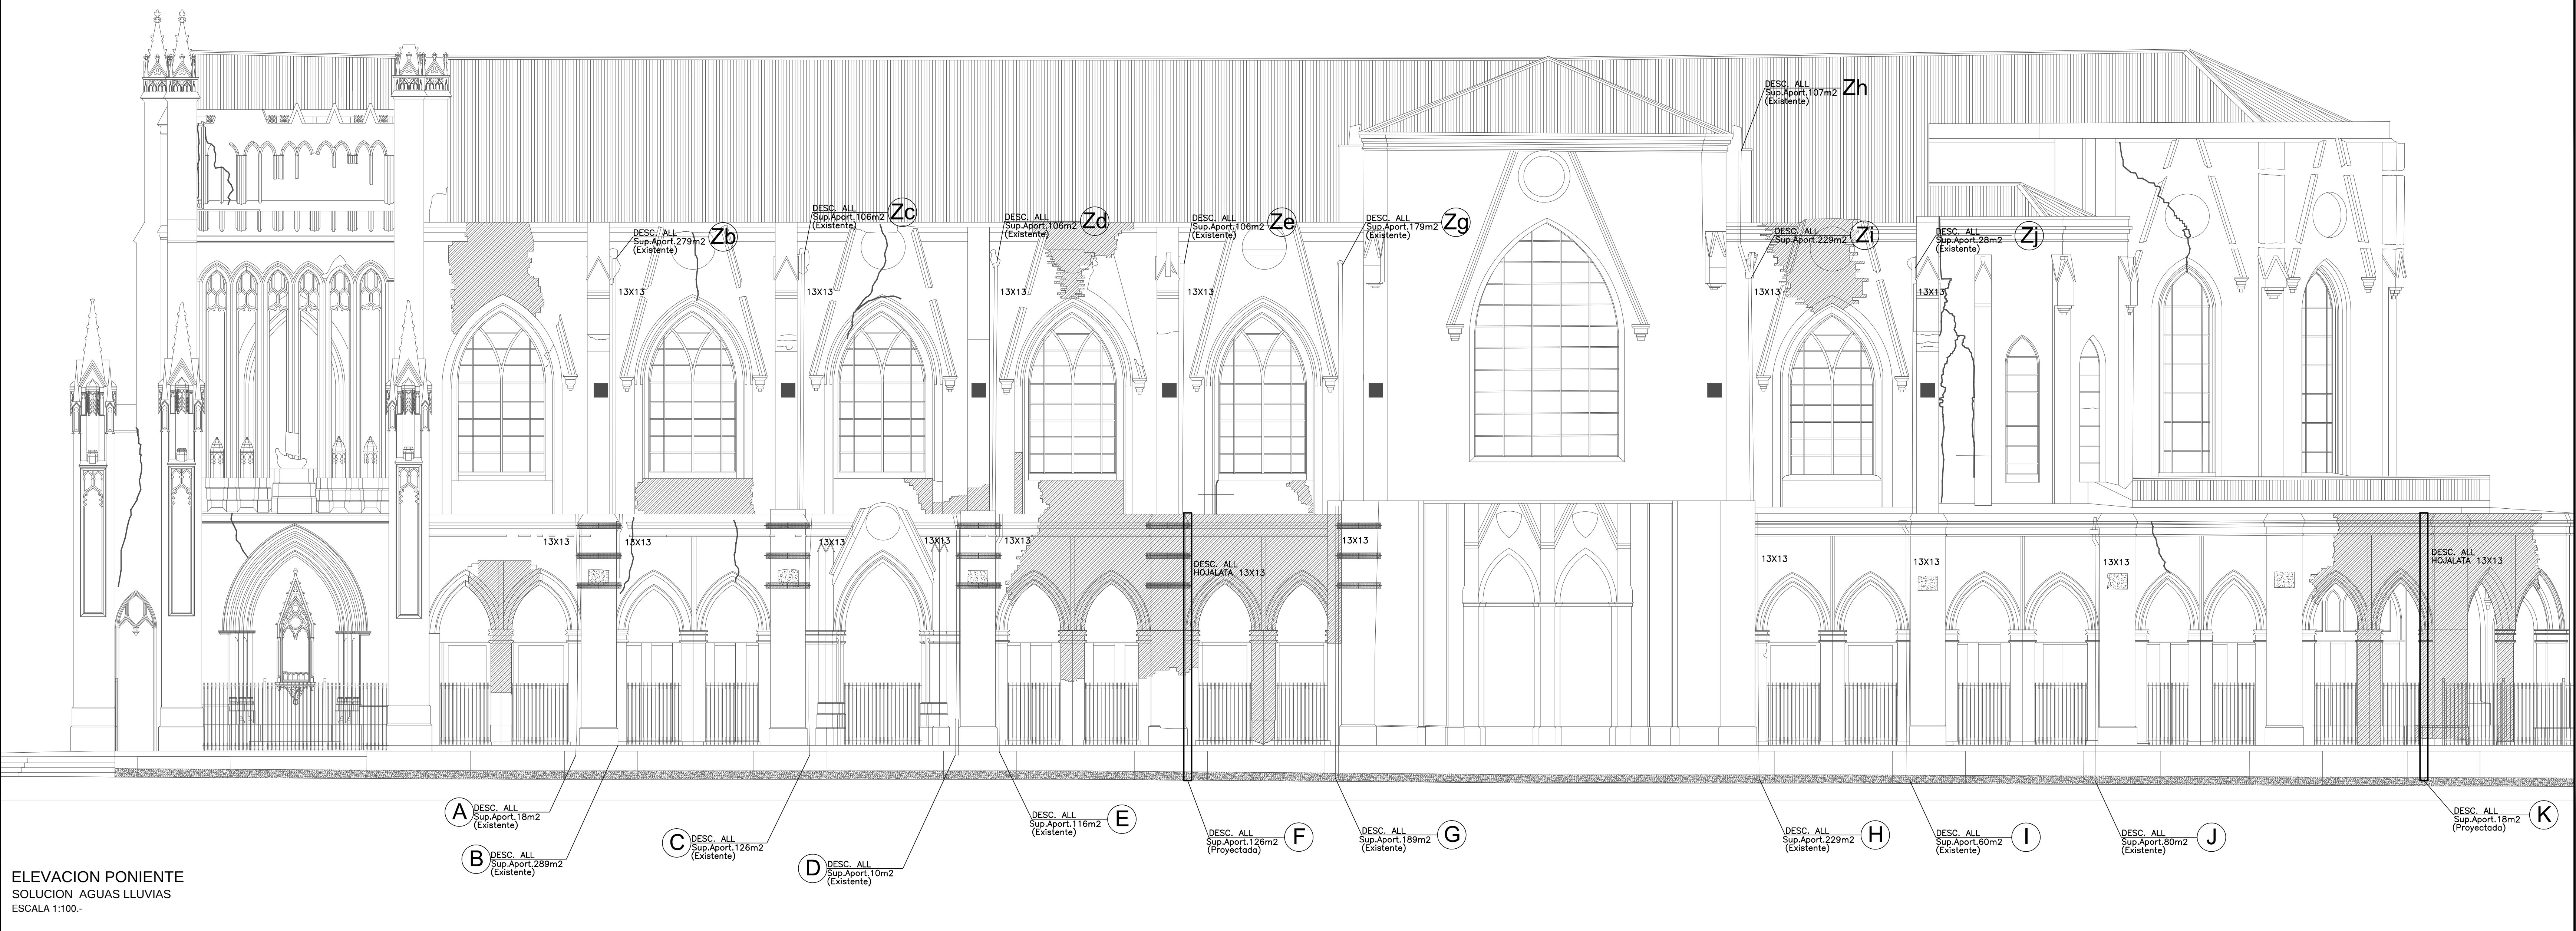

ELEVACION PONIENTE
SOLUCION AGUAS LLUVIAS
ESCALA 1:100.-

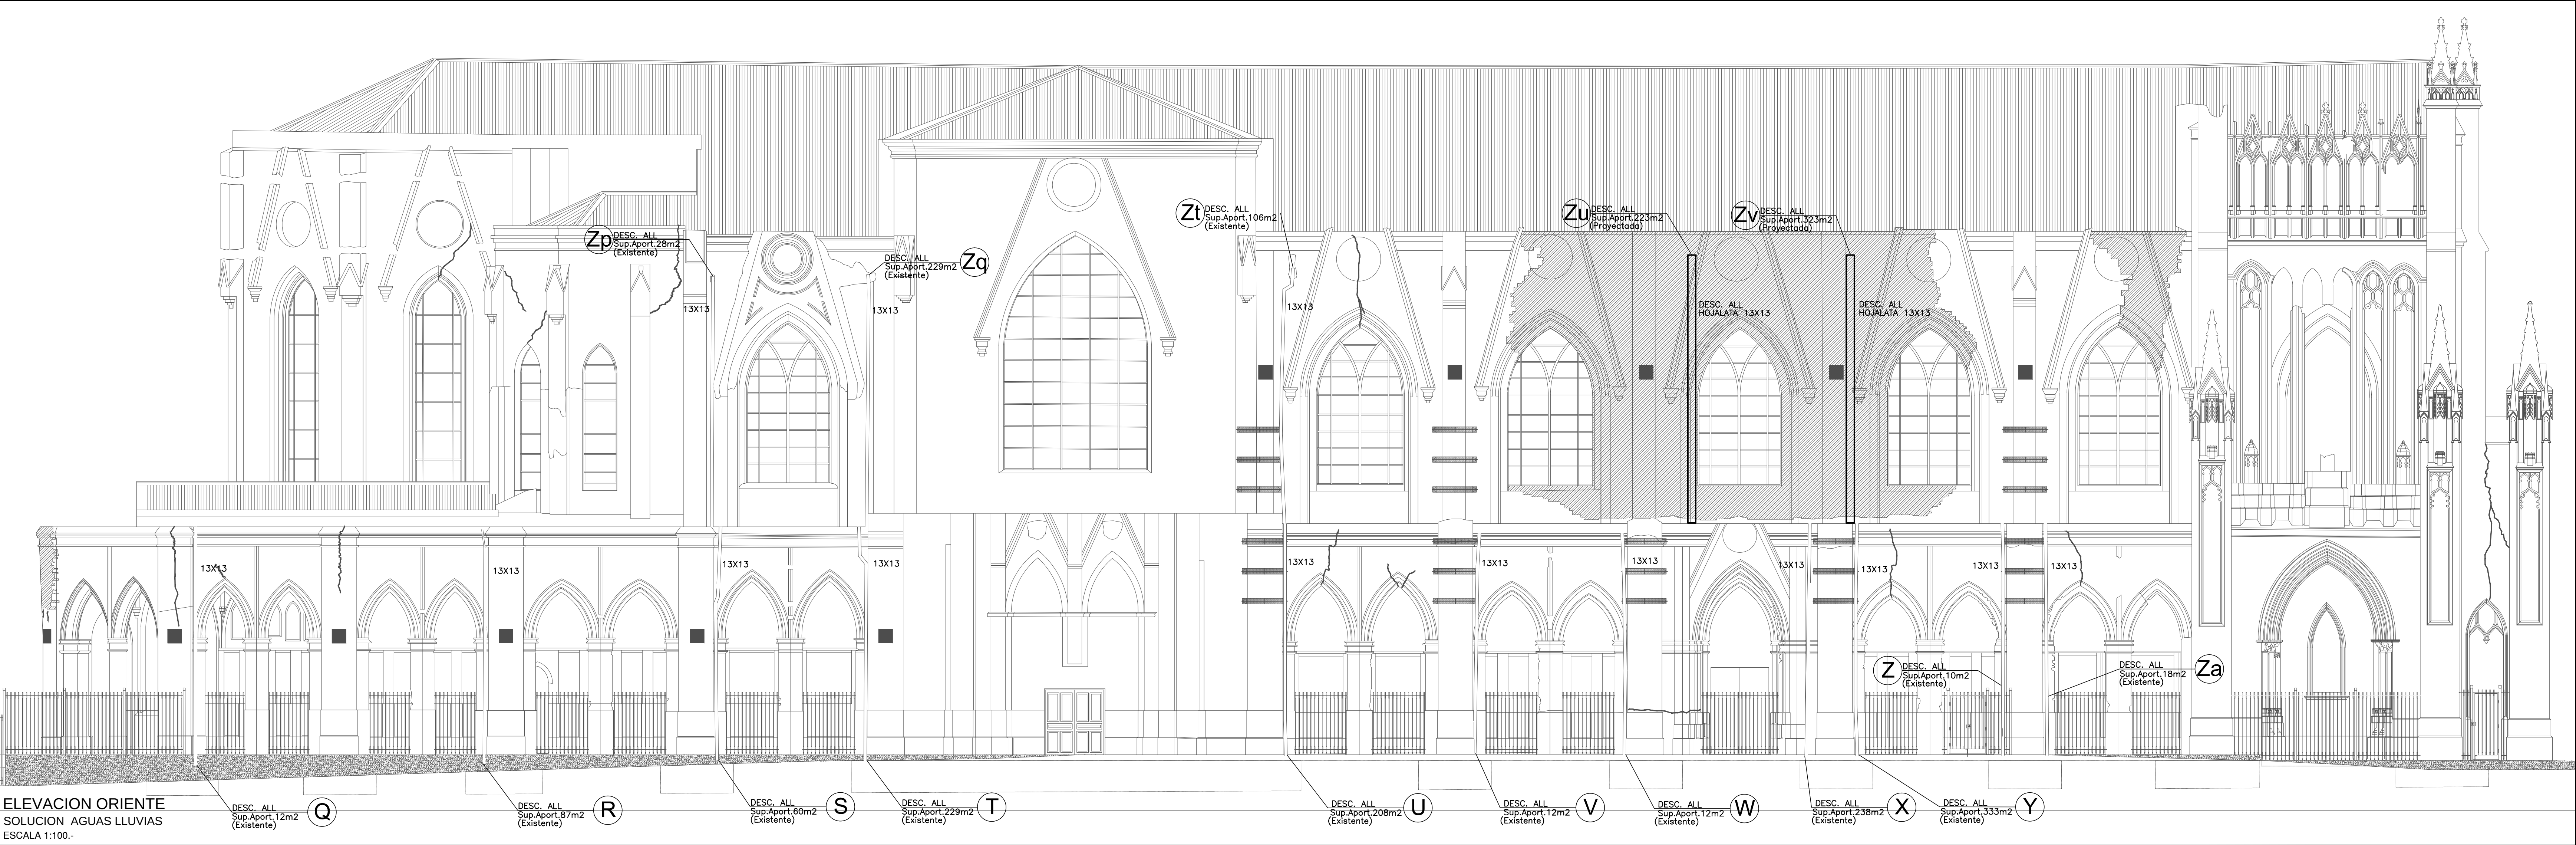

ELEVACION ORIENTE
SOLUCION AGUAS LLUVIAS
ESCALA 1:100.-

PROYECTO	INFORMATIVO	Lamina
Nº:	Fecha:	Nº 03 DE 03
AVISO DE INICIO	Nº	FECHA :
CERTIFICADO DE FACTIBILIDAD	Nº 6422	FECHA : 01/07/2019
RESTAURACIÓN Y HABILITACIÓN BASILICA DEL SALVADOR		
HUERFANOS Nº1780 / AGUSTINAS Nº1781 Region Metropolitana		
SANTIAGO		ESCALAS INDICADAS
UBICACION		
FIRMAS		
PROYECTISTA	PROPIETARIO	
MARIA ANGELICA DENEGRIO D. INGENIERO CIVIL U.O.H. RUT: 8.000.156-4 SENA VICTORIA 6962 - LA RENA FONO: 22 895 20 08 amarecua2@gmail.com	ARZOBISPADO DE SANTIAGO RUT: 81.795.100-7 PLAZA DE ARMAS 444, SANTIAGO	
CONTRATISTA	PROYECTO DEFINITIVO CERTIFICADO DE RECEPCION	
CONTRATISTA PROFESION : RUT : DOMICILIO : FONO : E-mail :	Nº Fecha FIRMA EMPRESA DE SERVICIOS SANITARIOS	