
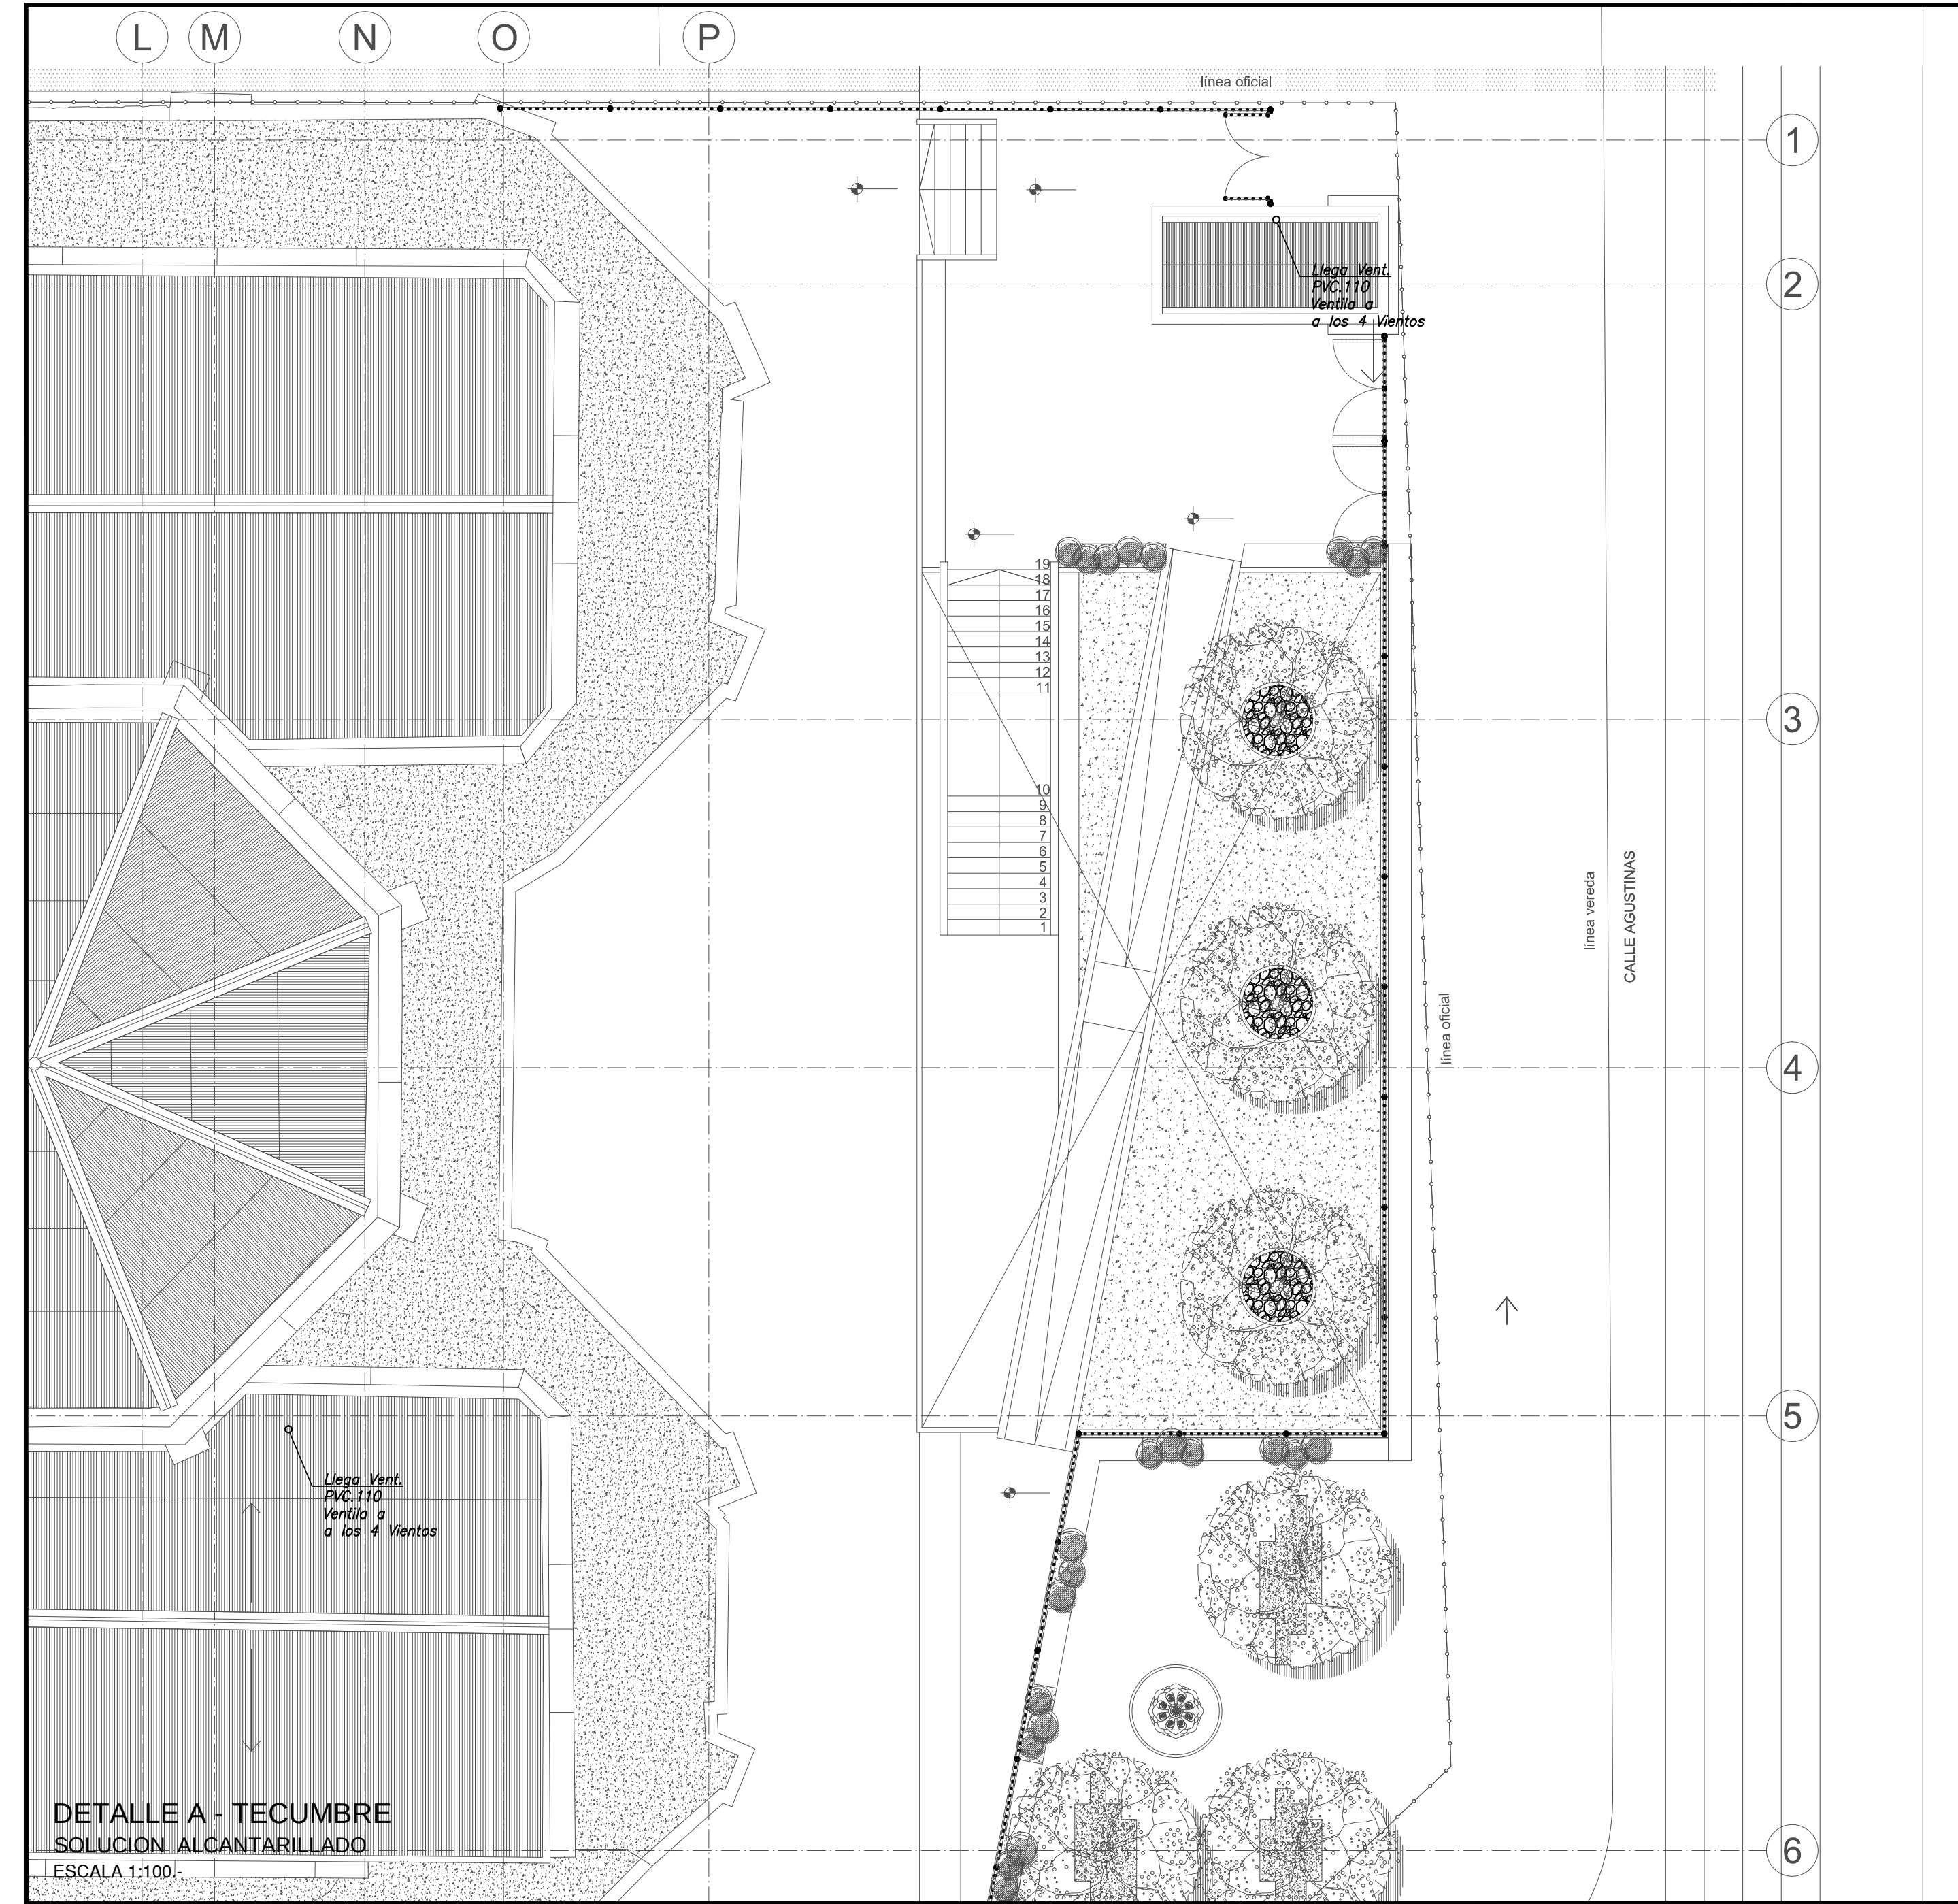
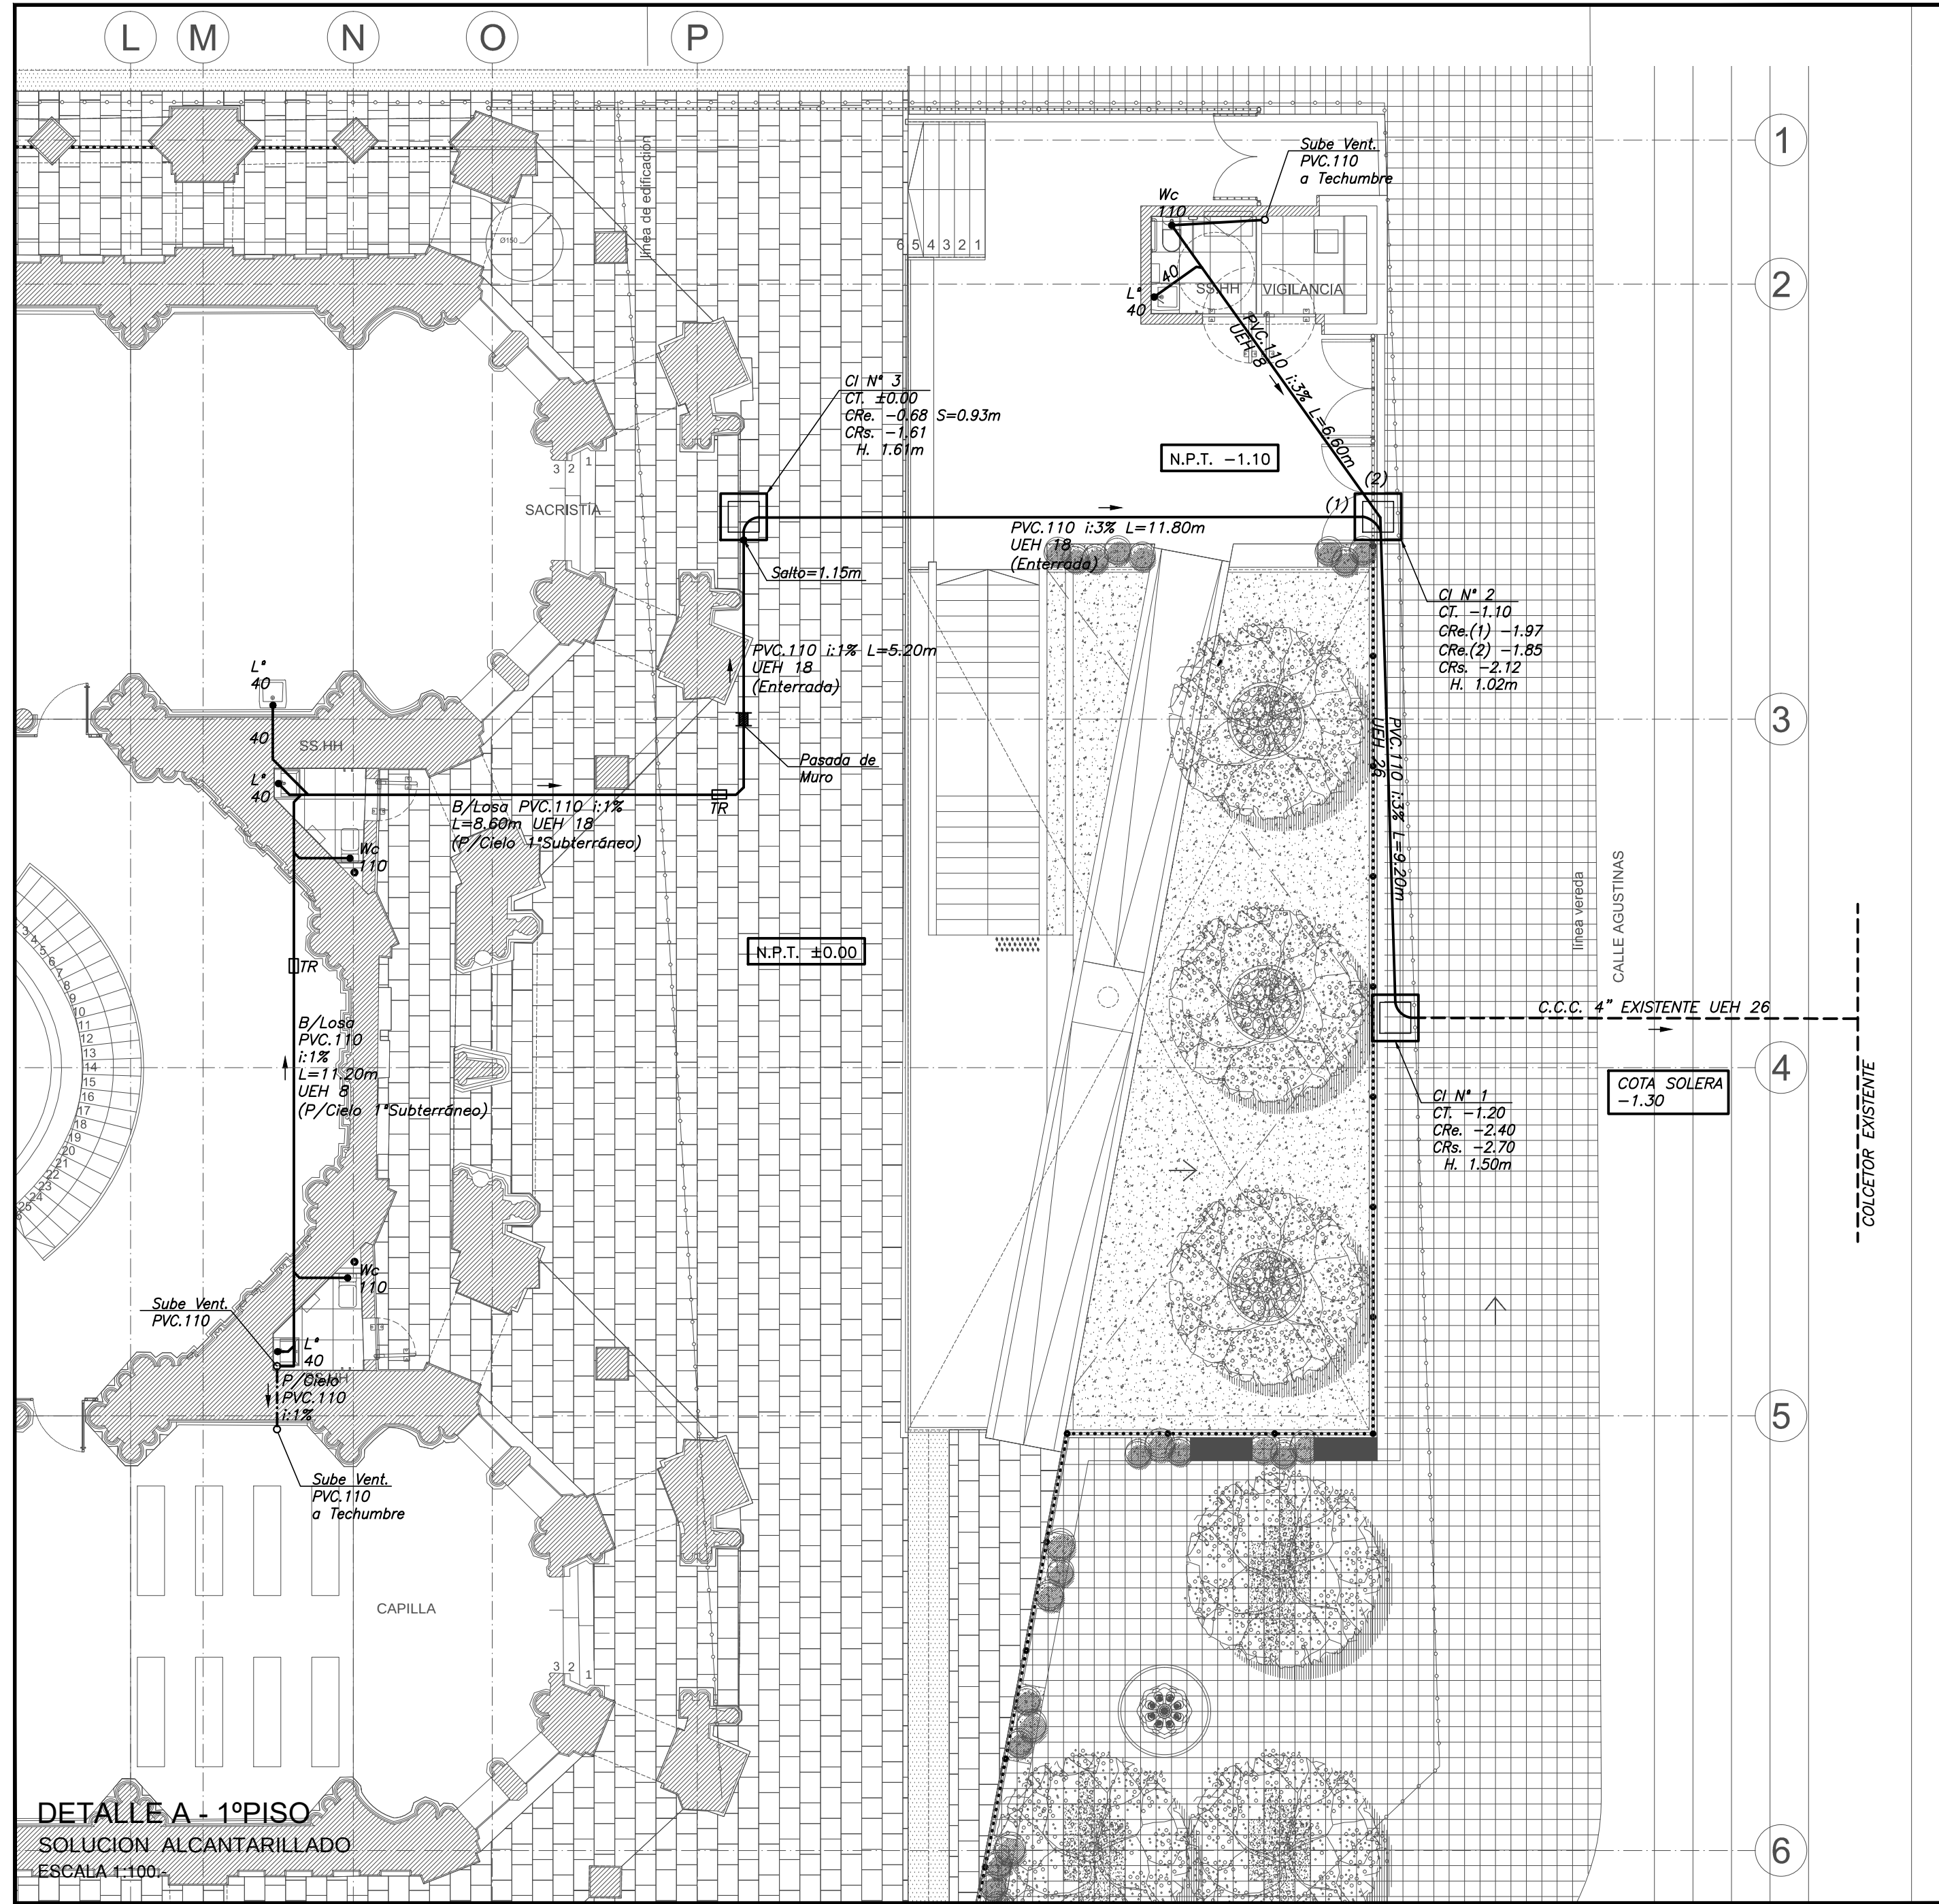


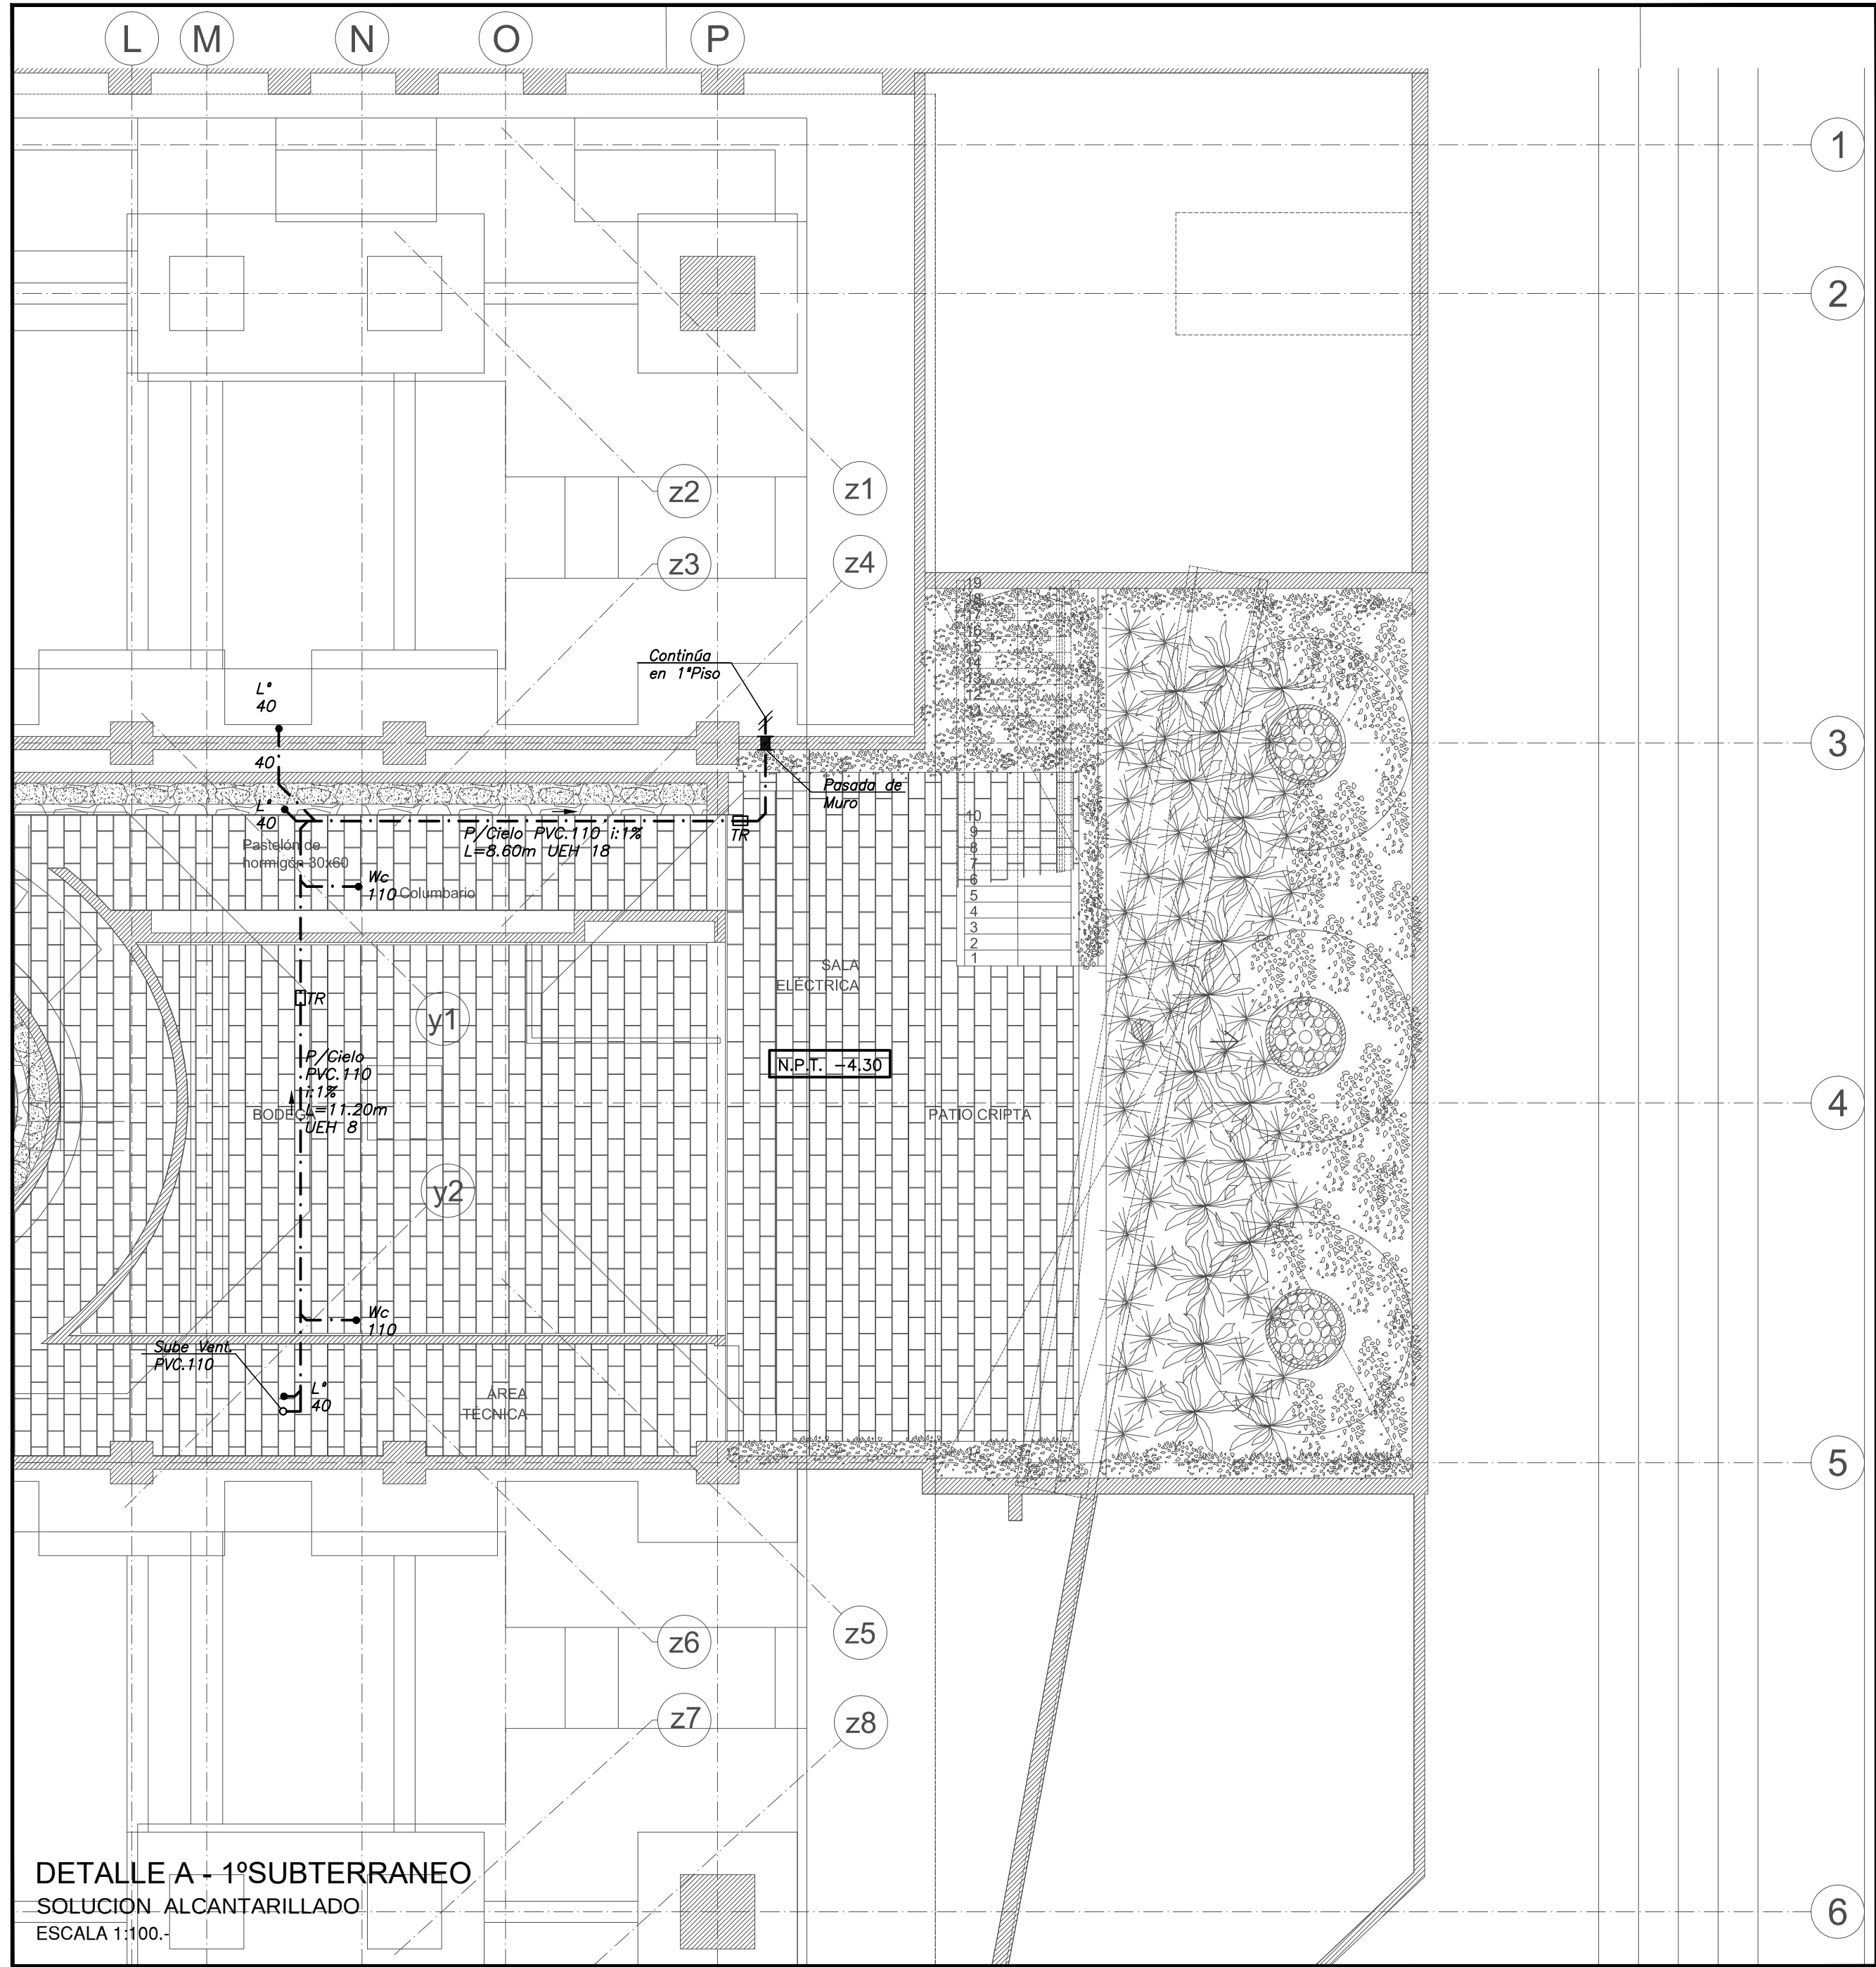






CUADRO DE UEH				
Artefacto	Cantidad	UEH / Artef	Sub Total UEH	
Wc	3	6	18	
L*	4	2	8	
Total Oi			26	

CUADRO DE CAMARAS PROYECTADAS				
CAMARAS DOMICILIARIAS ALCANTARILLADO				
Nº	ALTO	ANCHO	LARGO	ESCALINES
1	1.50	0.70	1.00	5
2	1.02	0.70	1.00	3
3	1.61	0.70	1.00	5

TOODAS LAS REDES DE AGUAS ANONAS QUE SE INFORMAN, TANTO EN LA FACTIBILIDAD COMO EN LOS PROYECTOS DOMICILIARIOS, TIENEN CARACTER REFERENCIAL. POR LO TANTO, SI ARRIVASE DOMICILIARIO DE AGUA POTABLE O UNA UNIDAD DOMICILIARIA ES CONSTRUIDA POR UN CONTRATISTA PARTICULAR, DEBERAN EFECTUARSE POR SU CUENTA, LAS CALIDADES CORRESPONDIENTES, CON EL FIN DE VERIFICAR EN TERRENO, LAS COORDENADAS EXACTAS DE LAS REDES DE AGUAS ANONAS QUE SE INFORMAN, TANTO EN AGUAS POTABLES COMO EN ALCANTARILLADO. DE EXISTIR INTERFERENCIAS EN LA FUTURA CONDICION O DIFAMIA, NO DEBE USARSE TUNELADORA.

NOMENCLATURA	
CAMERA POR TIERRA O BAO LISO PROYECTADO	_____
ALCANTARILLADO EXISTENTE	_____
ALCANTARILLADO POR SOBRE LOSA PROYECTADO	_____
ALCANTARILLADO POR CIELO PROYECTADO	_____
SENIDO DE ESCURRIMIENTO	_____
CAMARA DE INSPECCION PROYECTADA	_____

NOTA:
LAS INSTALACIONES DE ALCANTARILLADO SE EJECUTARAN EN TUBERIAS DE POLICLORURO DE VINILO (PVC SANITARIO BLANCO) CON UNIONES CAMPANA-ESPIGA Y ANILLO DE CAUCHO (ANGER).
NORMAS: CAÑERIAS: Nch 1635; PIEZAS: Nch 1779.

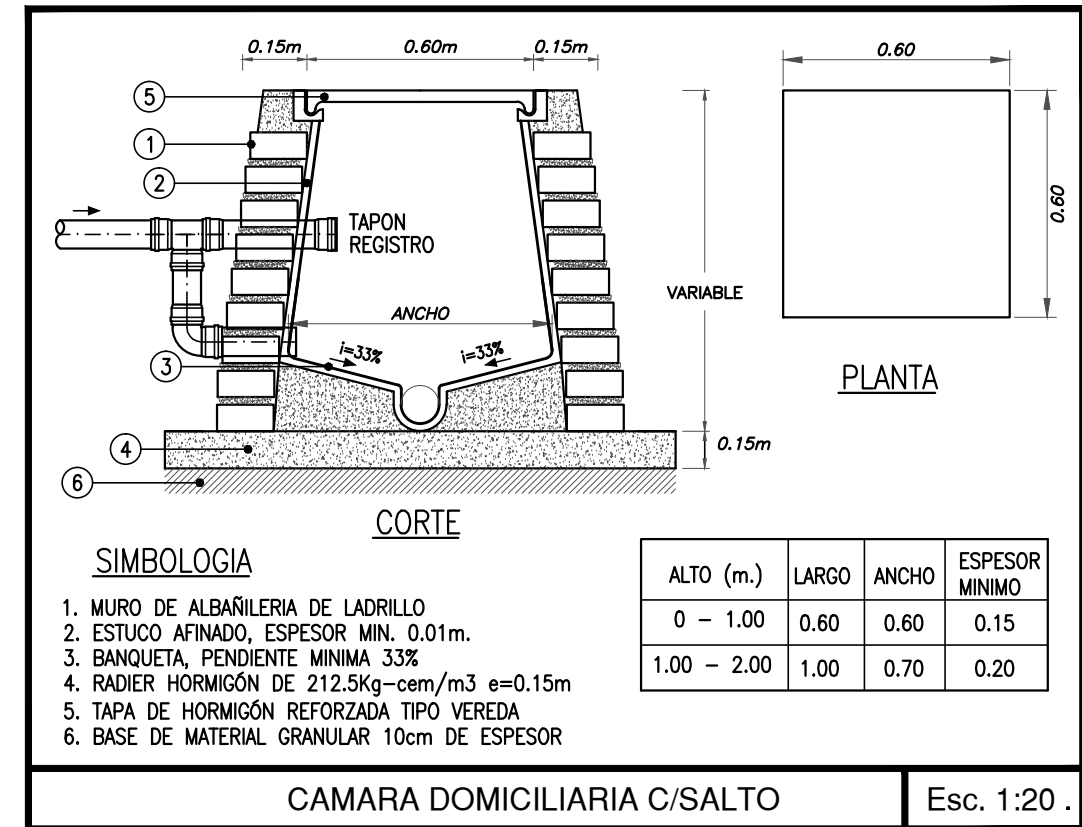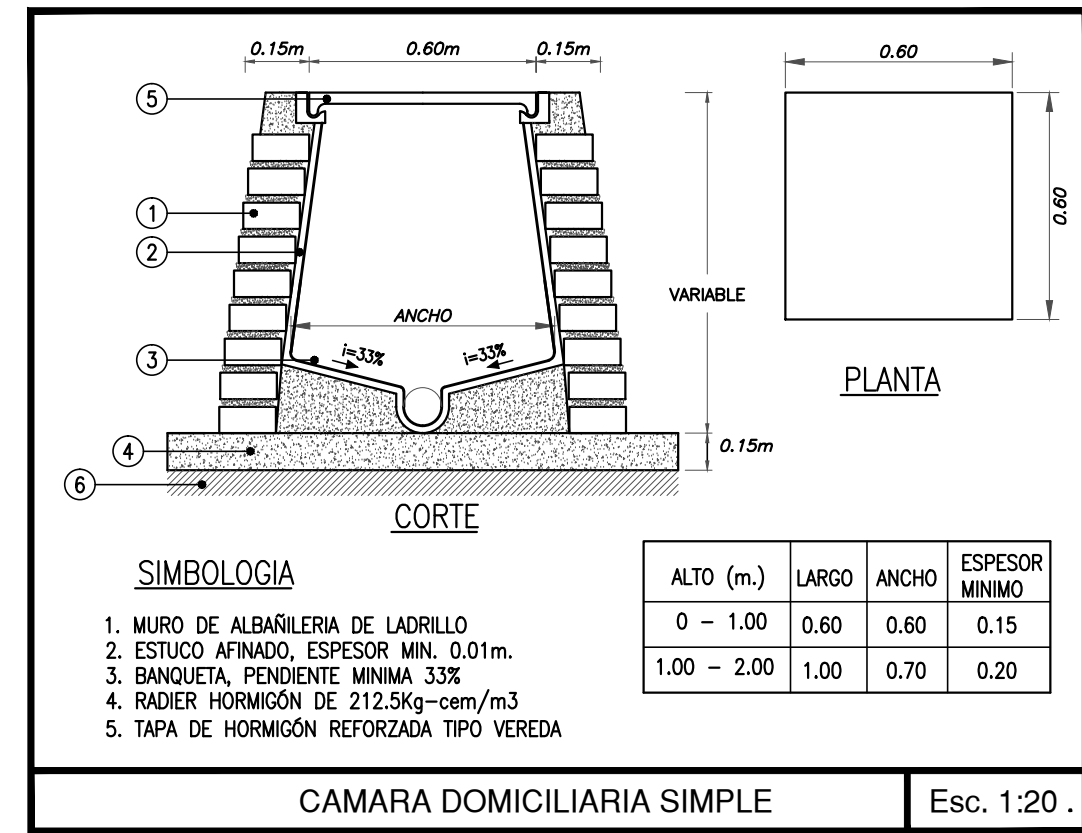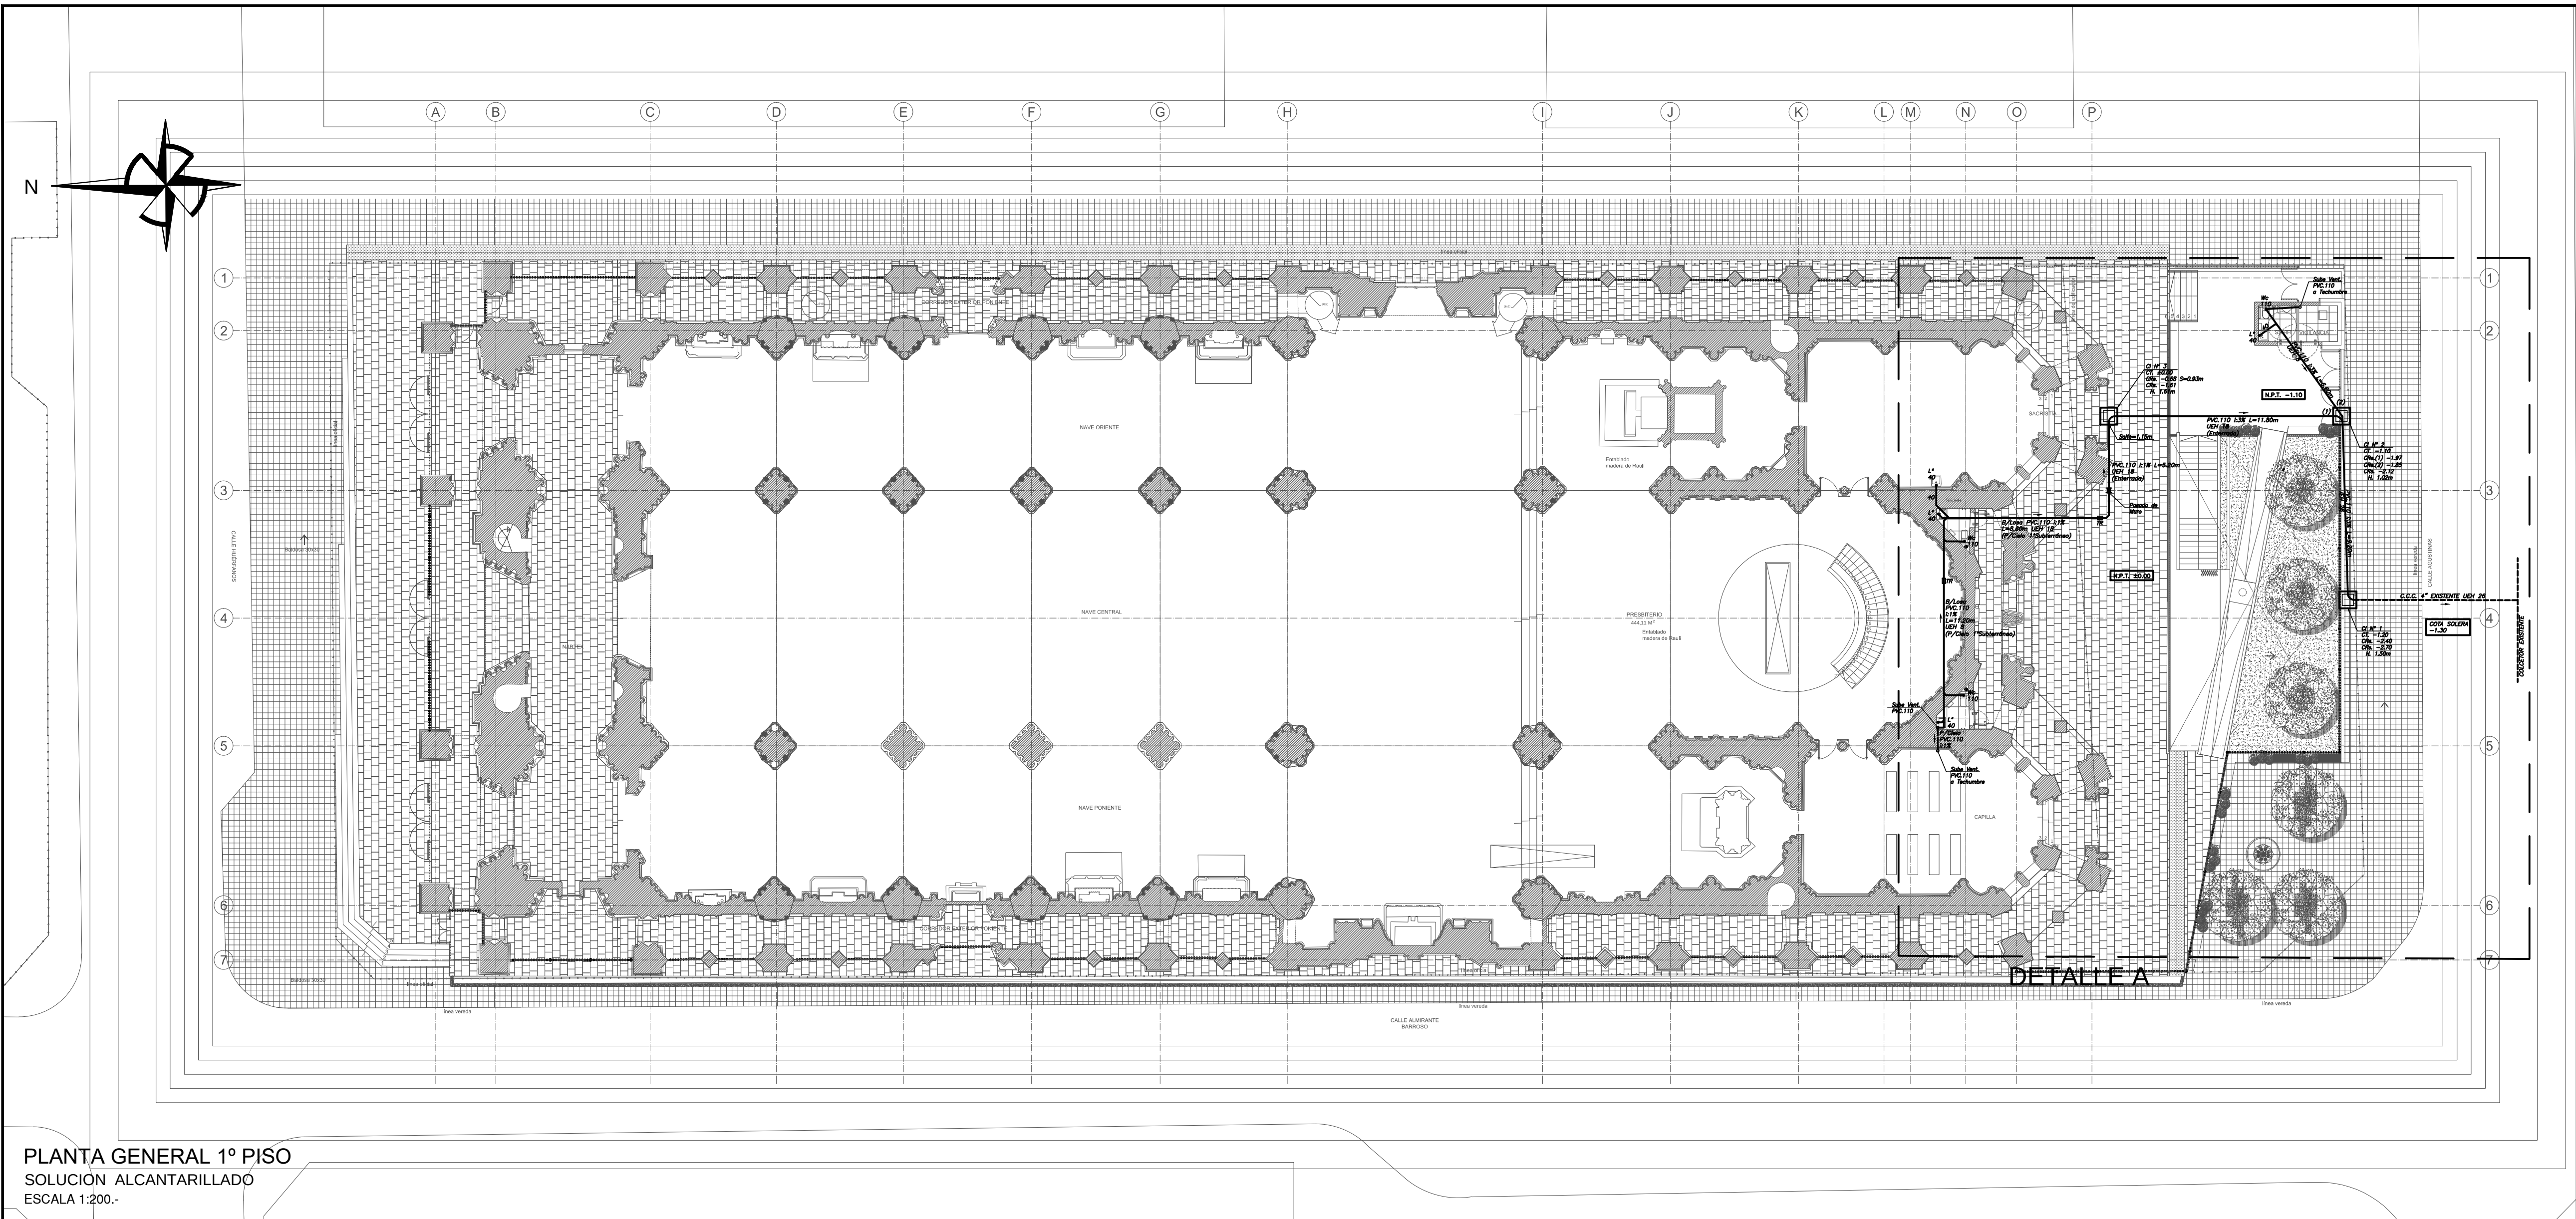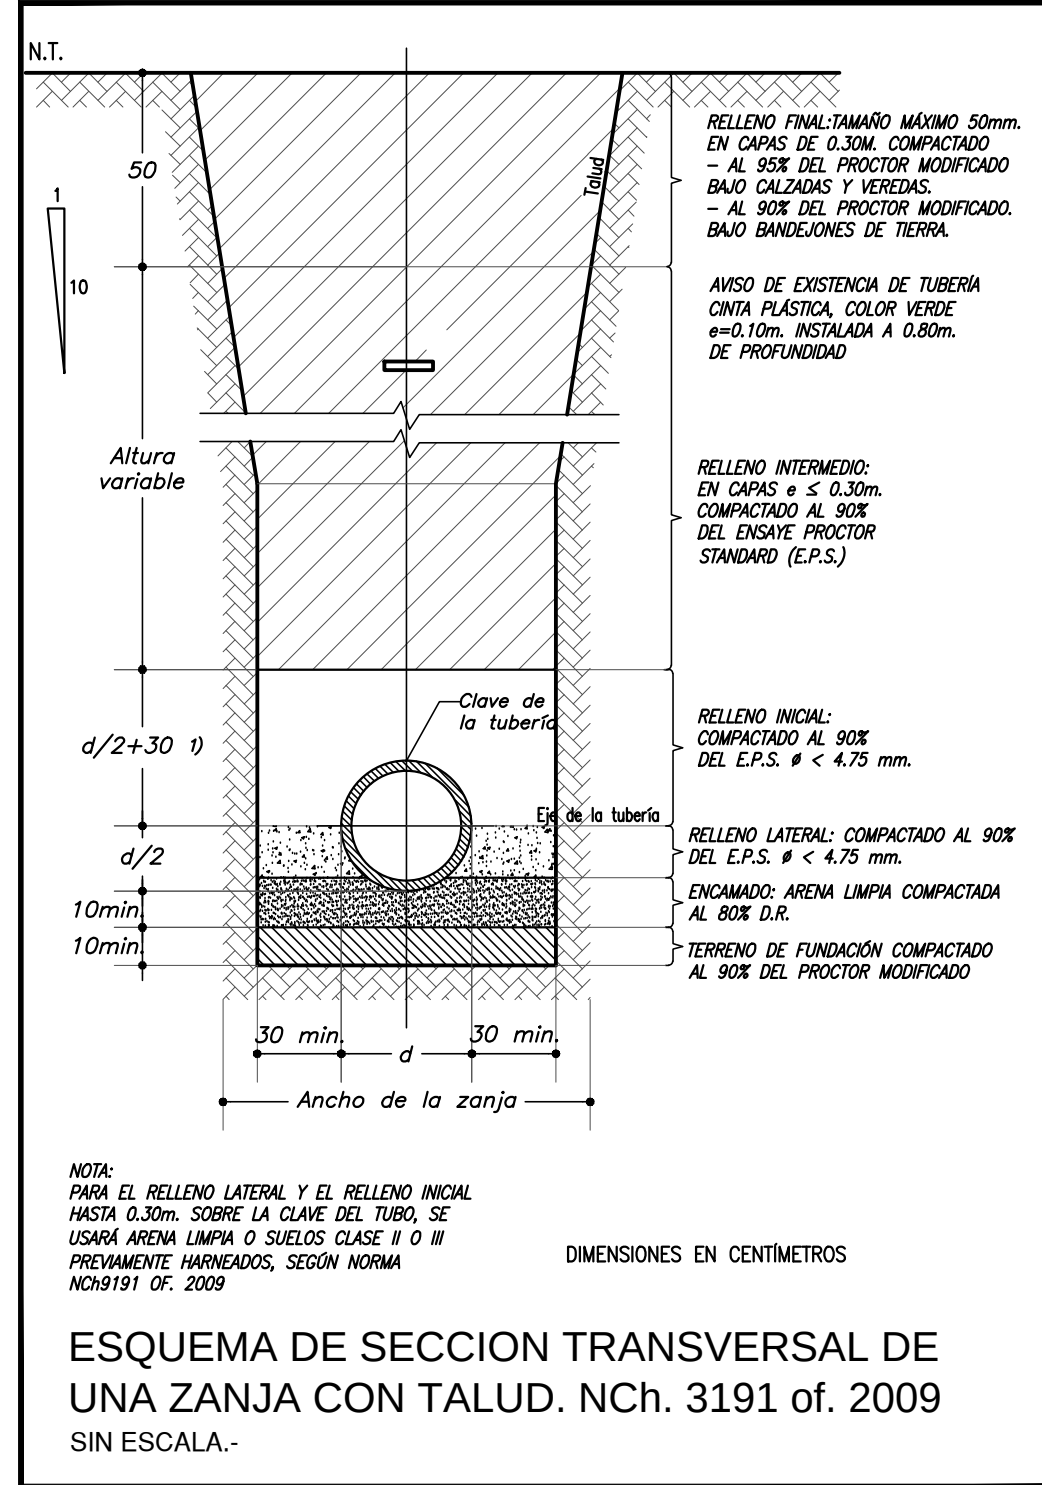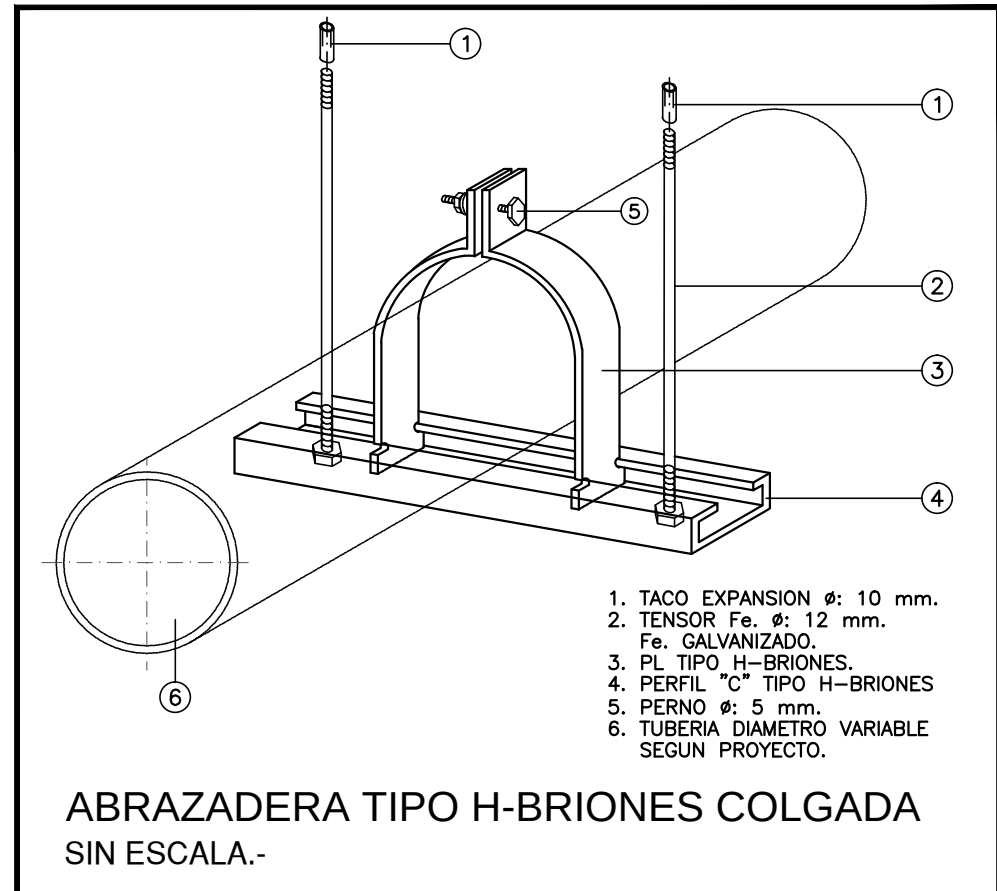

PROYECTO DE INSTALACION DE ALCANTARILLADO DOMICILIARIA	
PROYECTO	INFORMATIVO
Nº:	Fecha:
Nº	01 DE 01
AVISO DE INICIO N°	
FECHA :	
CERTIFICADO DE FACTIBILIDAD N° 6422	
FECHA : 01/07/2019	
RESTAURACIÓN Y HABILITACIÓN BASILICA DEL SALVADOR	
HUERFANOS N°1780 / AGUSTINAS N°1781	
Region Metropolitana	
SANTIAGO	ESCALAS INDICADAS
UBICACION	
FIRMAS	
PROYECTISTA	PROPIETARIO
MARIA ANGELICA DENEGRIO D.	ARZOBISPADO DE SANTIAGO
INGENIERO CIVIL UCH.	RUT: 81.795.100-7
RENA VICTORIA 6802 - LA RENA	PLAZA DE ARMAS 444, SANTIAGO
CONO: 22 885 20 08	
CONTRATISTA	PROYECTO DEFINITIVO
PROFESION	CERTIFICADO DE RECEPCION
Nº	Fecha
CONTRATISTA	FIRMA EMPRESA DE SERVICIOS SANITARIOS
PROYECTO	PROYECTO
PROY. M.A.D.	NOMBRE ARCHIVO
CONO	VERSIÓN
REV. M.A.D.	
FECHA	FEBRERO 2021
CONO	A