
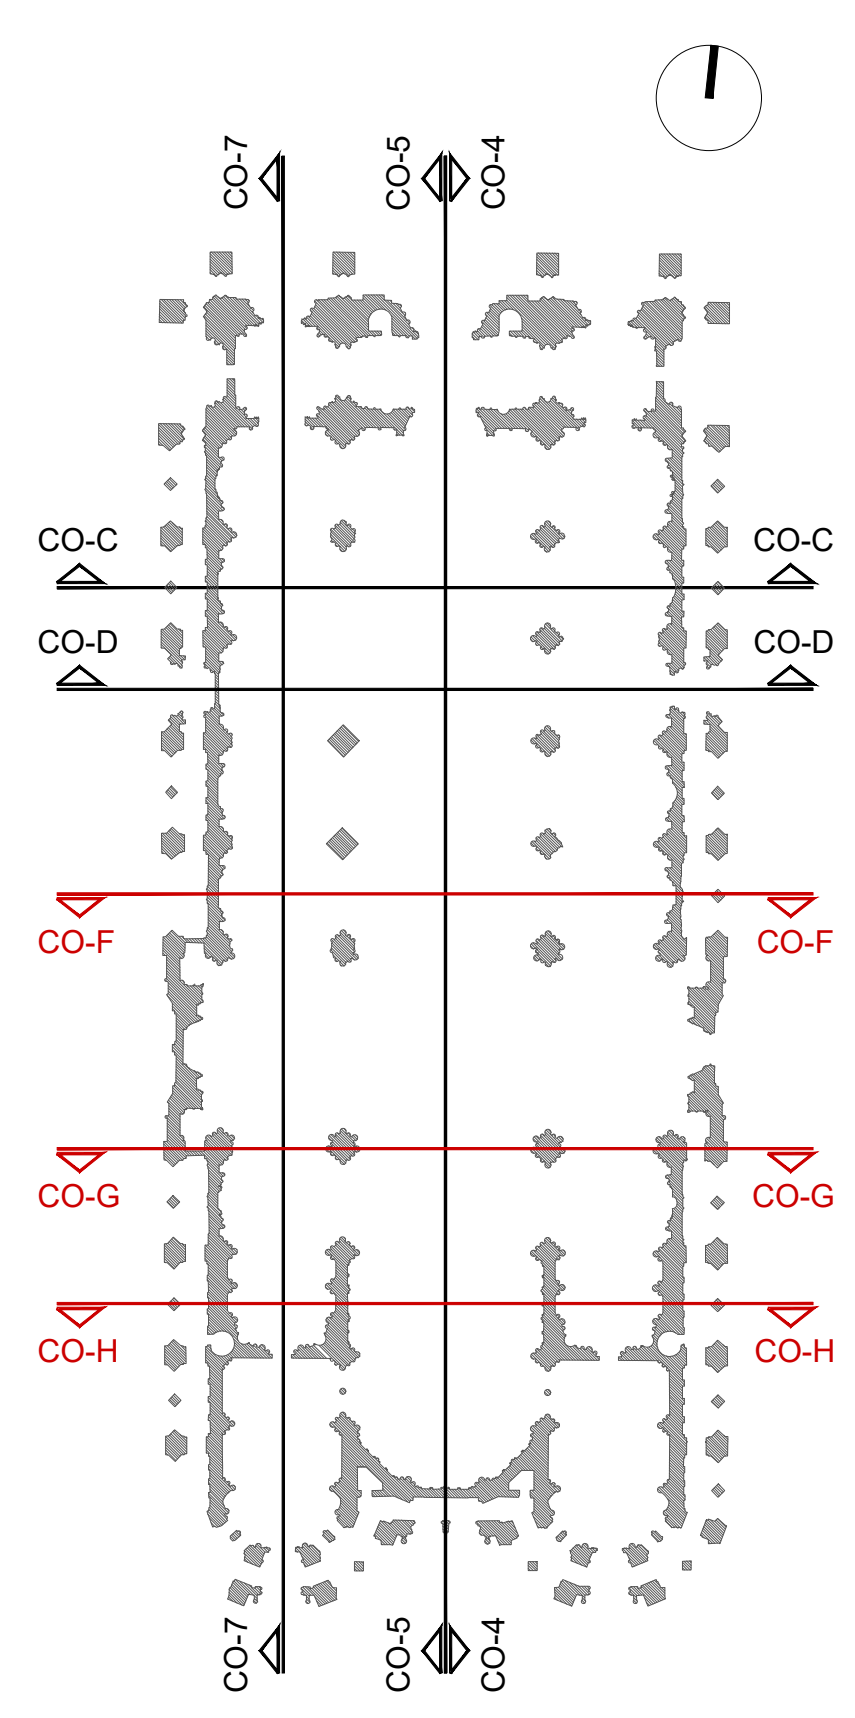
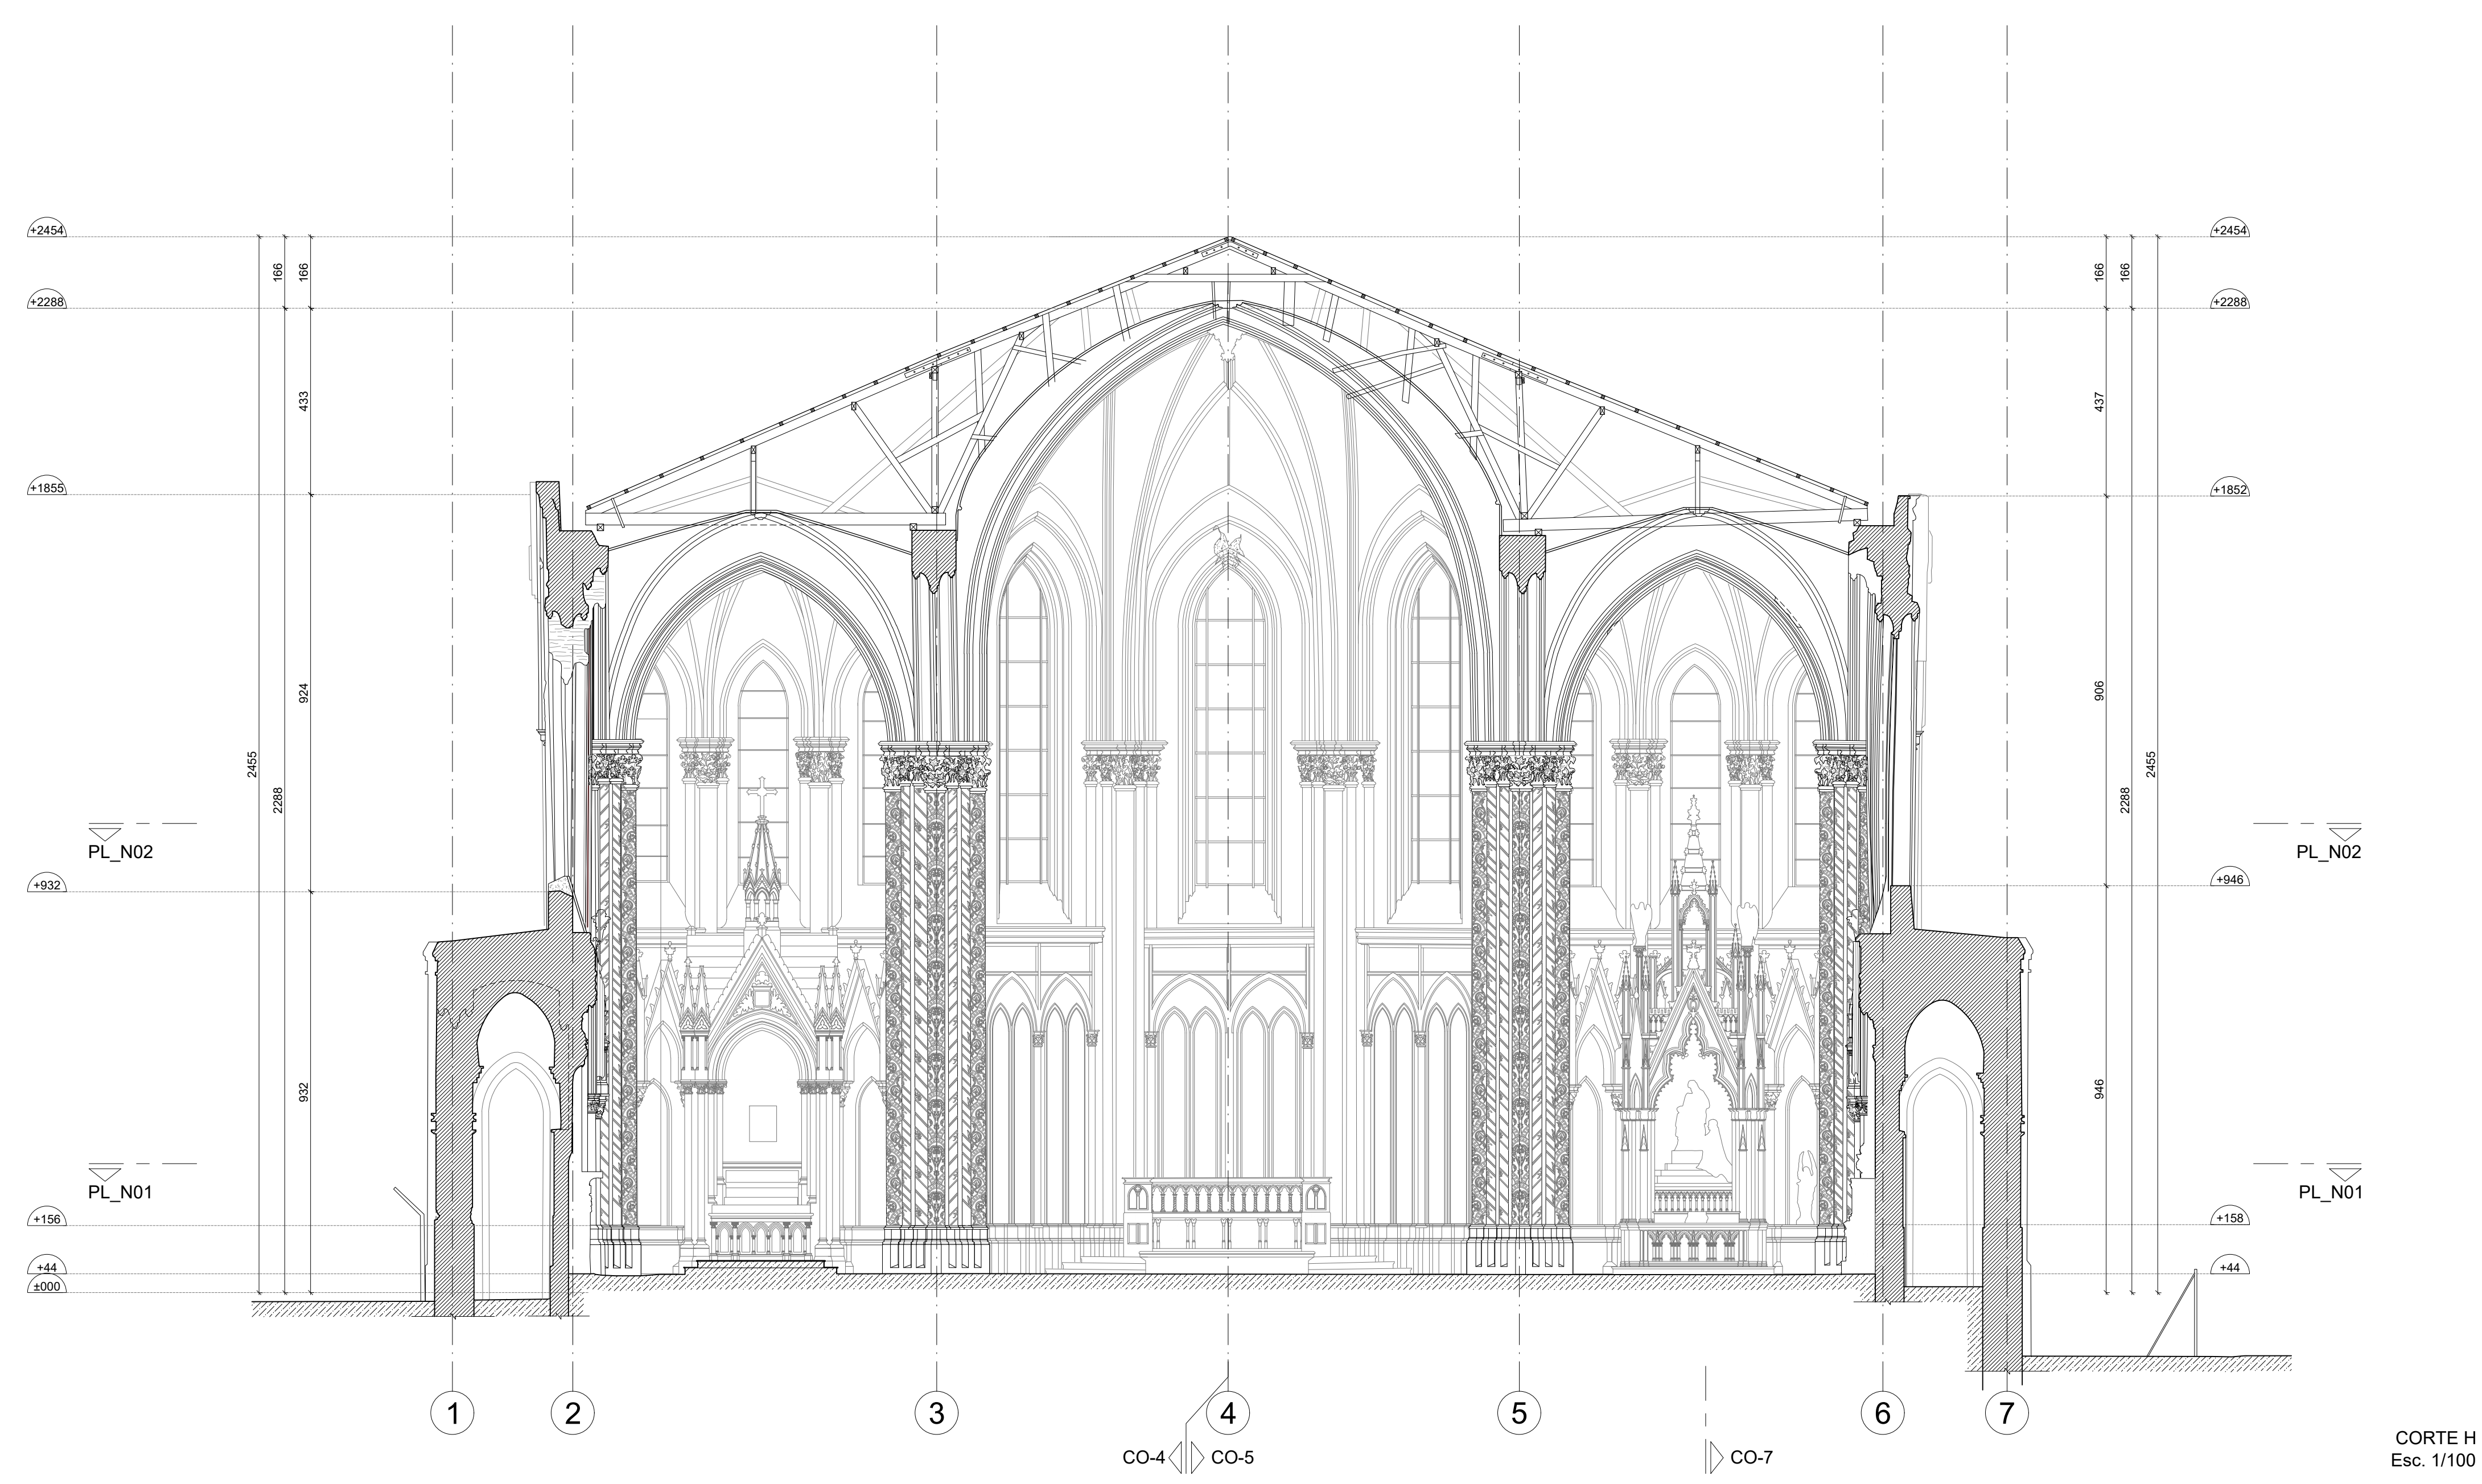


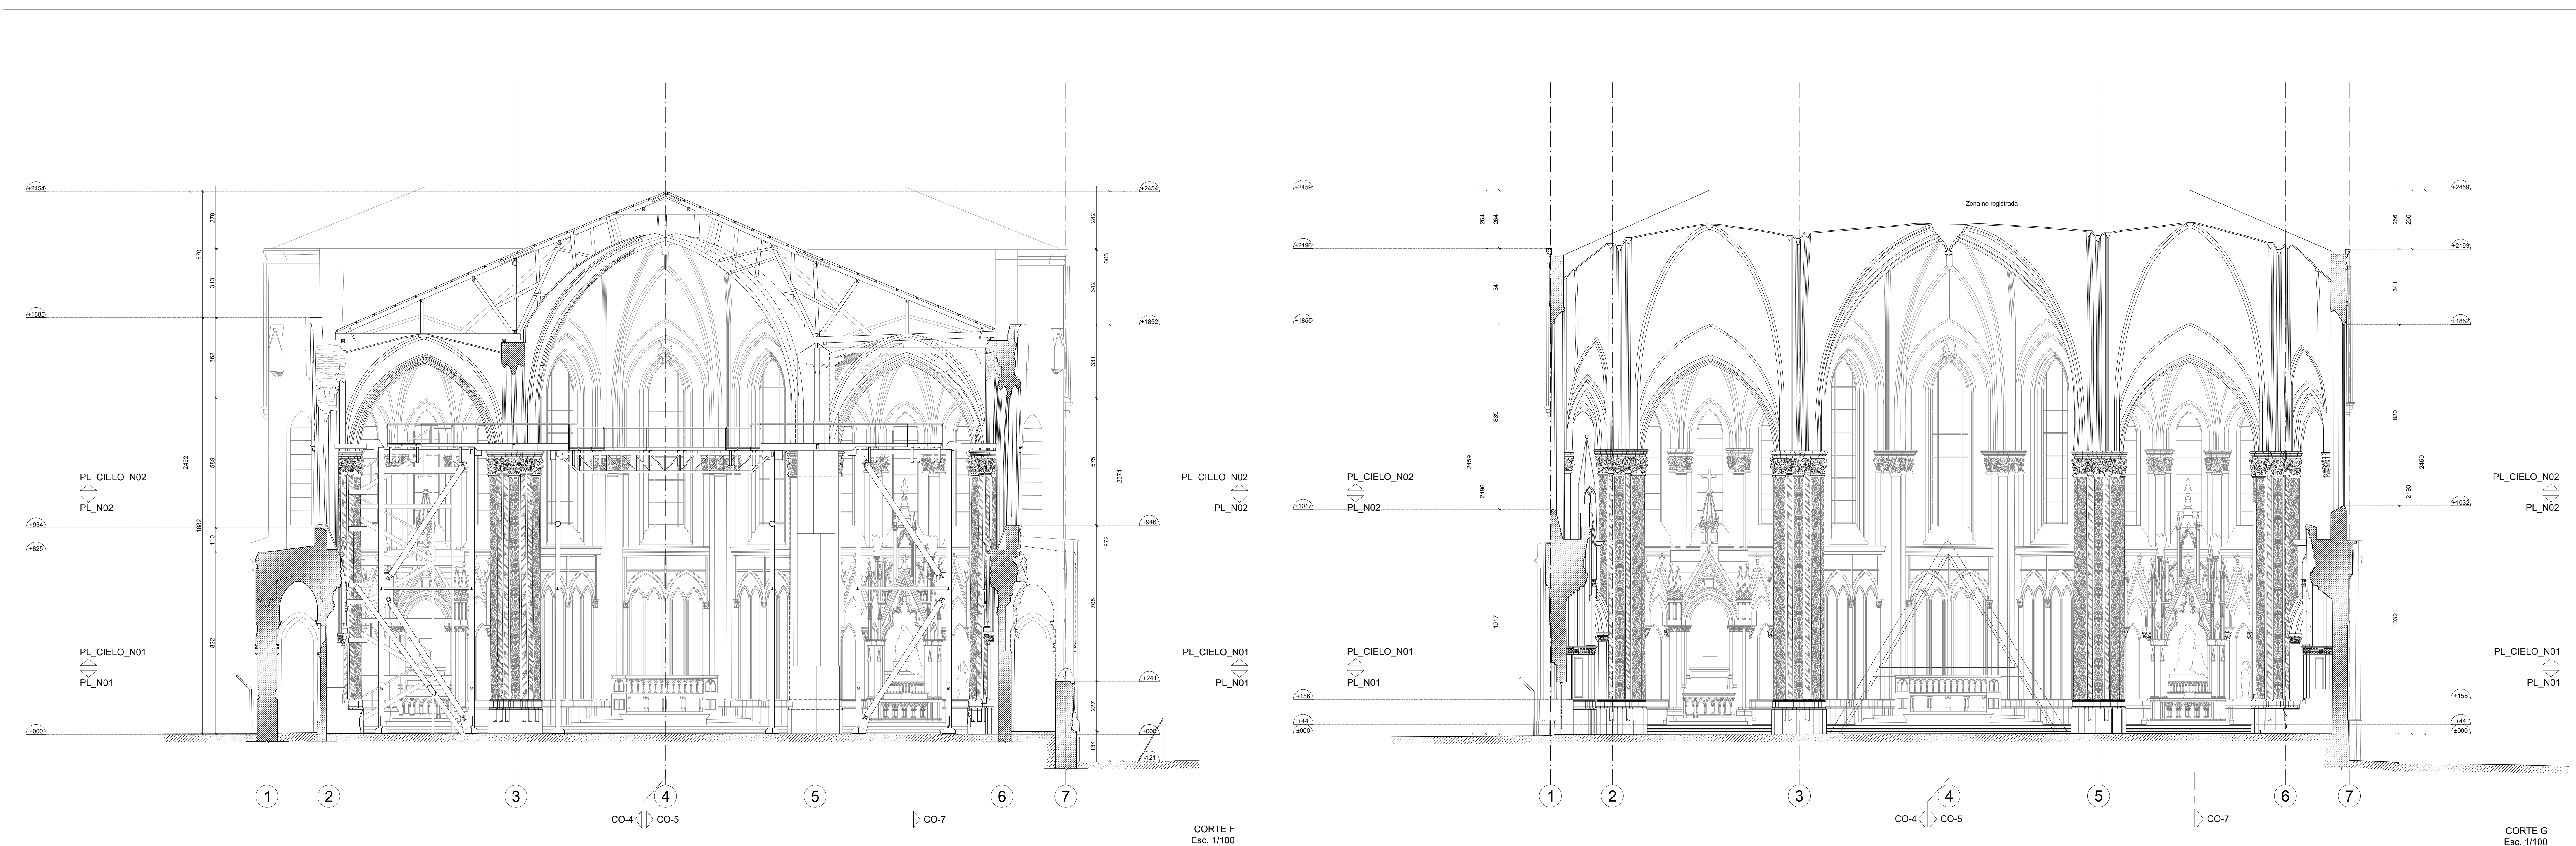

SIMBOLOGIA

- Laguna y/o pérdida de material
- Elementos faltantes
- Albanilería

Plano de referencia

Modificaciones

Índice	Fecha	Cambios
A	26/03/19	Primera emisión
B	07/06/19	Segunda emisión
C	30/07/19	Tercera emisión
D	09/12/19	Cuarta emisión
E	19/12/19	Quinta emisión
F	13/06/20	Sexta emisión
G	14/08/20	Séptima emisión
H	08/10/20	Octava emisión

Propietario

Arzobispado de Santiago
81.795.100 - 7
Plaza de Armas 444, Santiago

Representantes Legales
Sebastián Ríos Rivas
9.868.551-0
Bernardita Soto Velasco
11.863.234-6
El Bosque Sur 130, Piso 15, Providencia

Entidad Colaboradora del Proyecto de Restauración
Fundación Basílica del Salvador
65.148.980-6

TÁNDEM limitada
Joaquín Walker Morfín 3528, Ríñoco
Santiago - Chile
+562 2980 44 10
contacto@tandemlimitada.cl

Profesionales responsables
Dino Bozzi F.
Arquitecto
Francisco Prado G.
Constructor Civil

RESTAURACIÓN Y HABILITACIÓN
BASILICA DEL SALVADOR
Huérfanos 1736 - Santiago
Región Metropolitana

CORTES TRANSVERSALES
F.G.Y.H.

Índice	Fecha	Escala
TD 1838	LEV	PL

Emisor: Proyecto
Revisó: JAC/PLU
Cada: DE
Tipo: Zona
Zona: H
Índice: H

LEV 10