


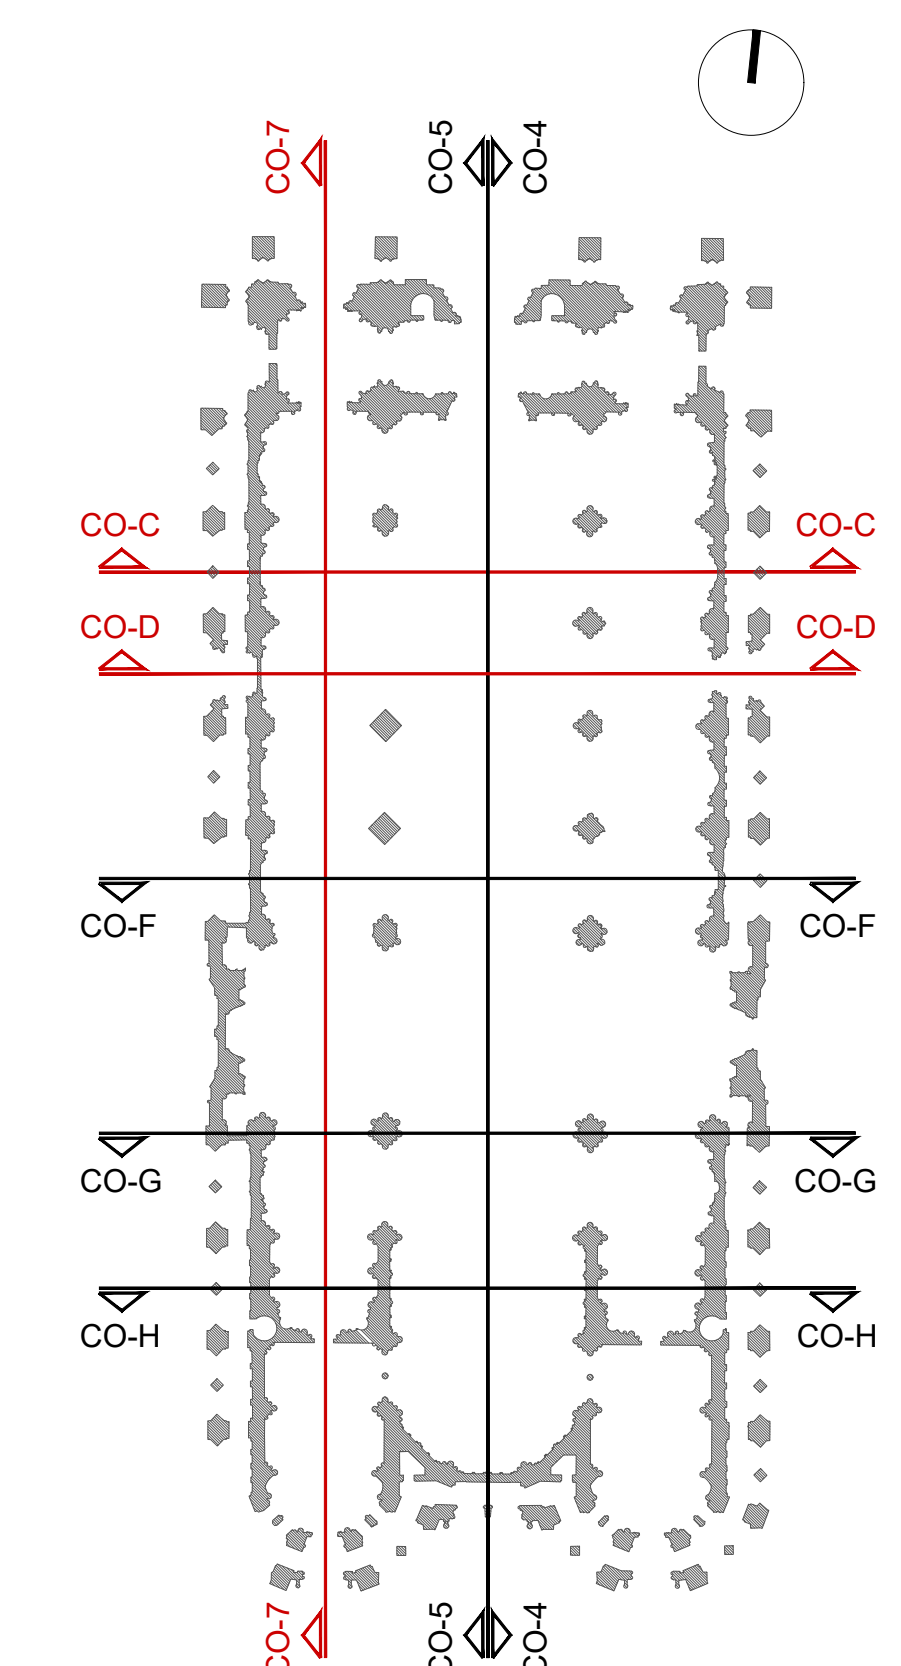


Plano de referencia



Modificaciones

Índice	Fecha	Cambios
A	07/09/19	Primera emisión
B	12/07/19	Segunda emisión
C	30/07/19	Tercera emisión
D	09/12/19	Cuarta emisión
E	19/12/19	Quinta emisión
F	13/02/20	Sexta emisión
G	14/02/20	Séptima emisión
H	06/10/20	Octava emisión

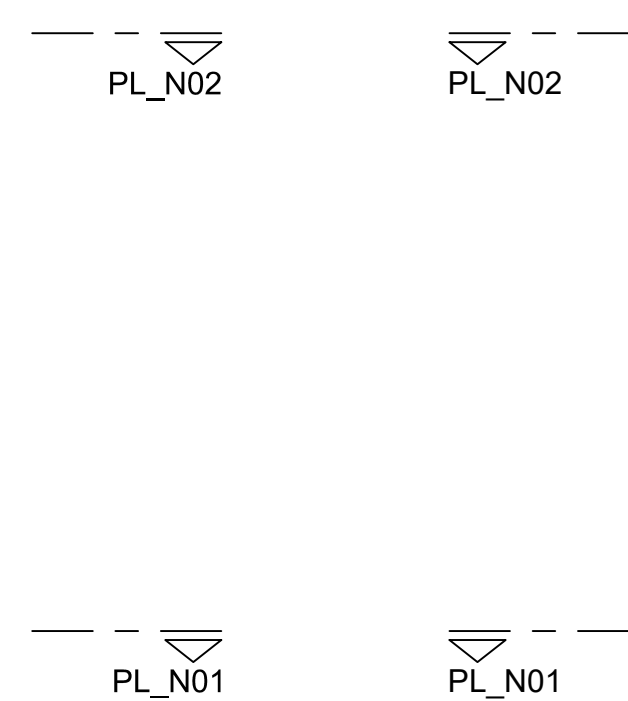PAT
07

CORTE C
Esc. 1/100



CORTE D
Esc. 1/100