

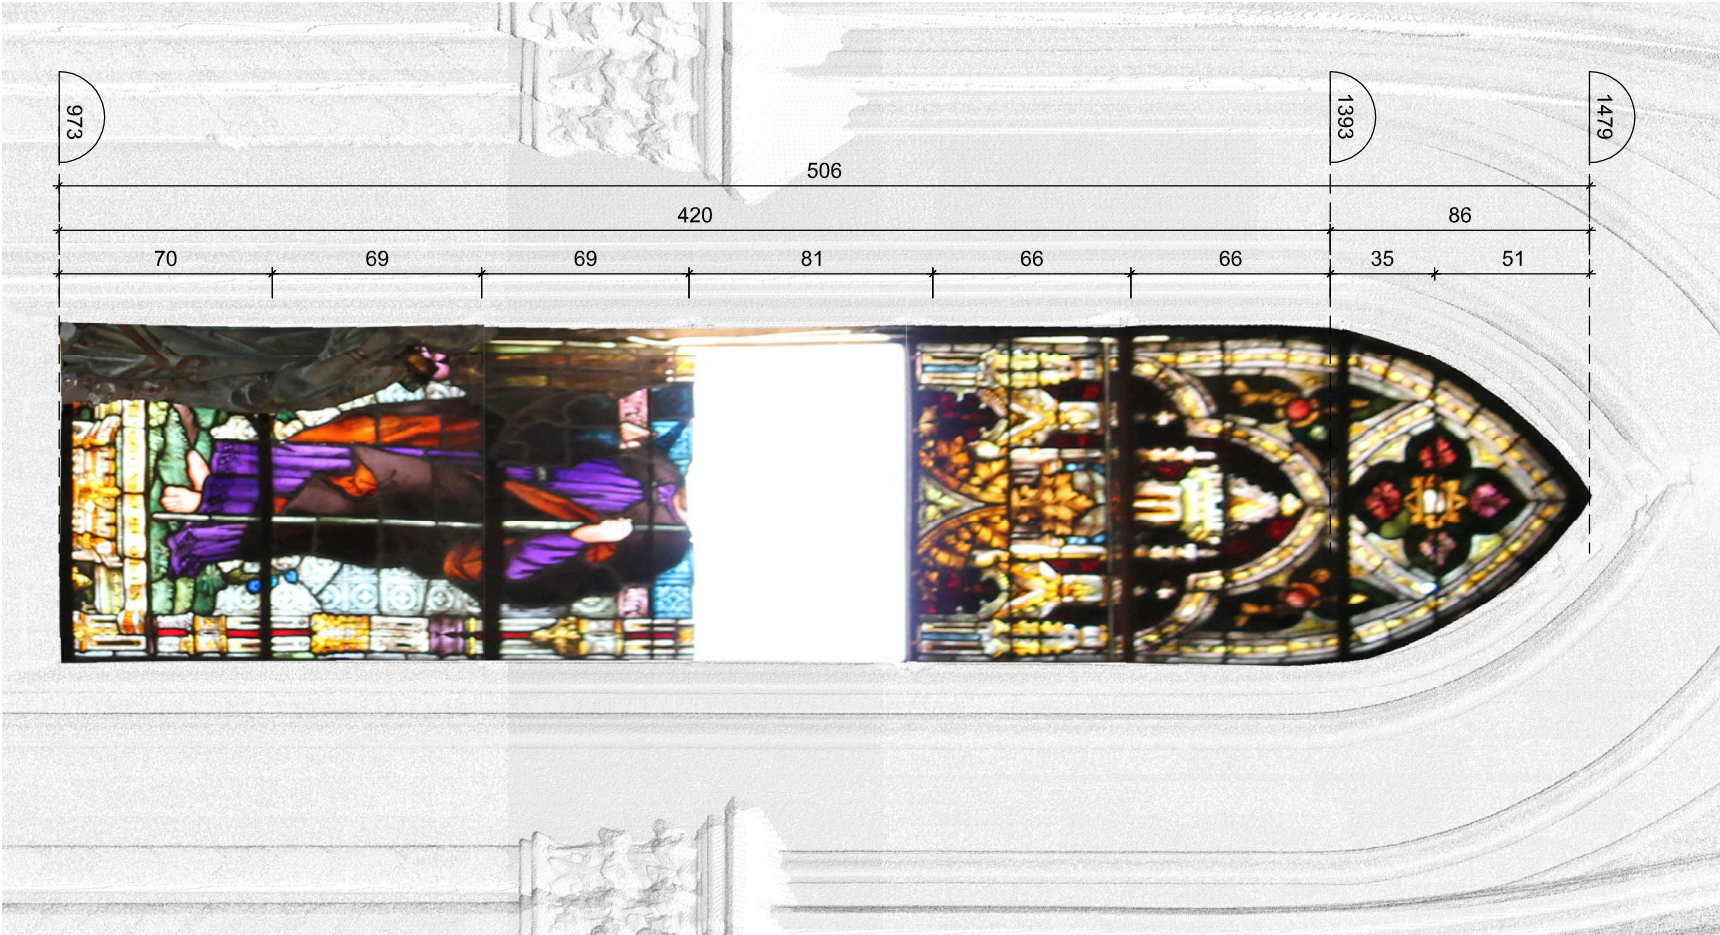


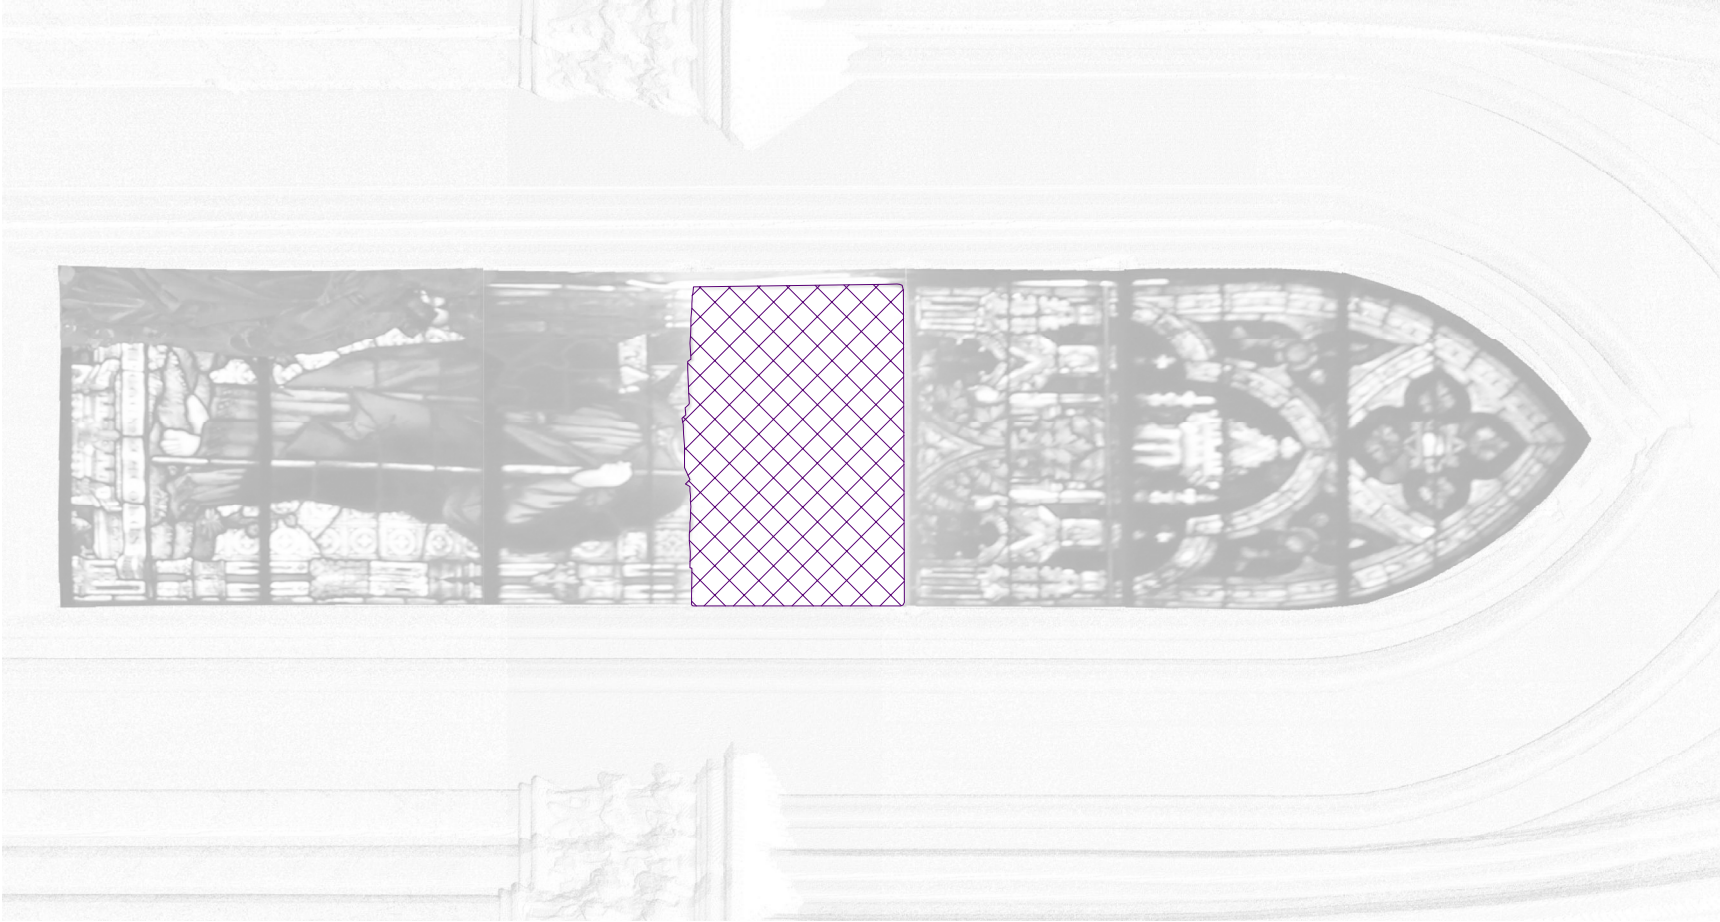

Elevación
Esc. 1/25

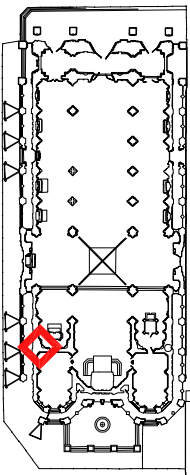

Levantamiento de Daños
Esc. 1/25

Ubicación						
						
			Arqto. Dino Bozzi F. TÁNDEM Limitada contacto@tandemlimitada.cl			
DIRECCIÓN DE ARQUITECTURA DIRECCIÓN REGIONAL METROPOLITANA						
PROYECTO: REPARACIÓN PARCIAL BASÍLICA DEL SALVADOR STGO						
BASÍLICA DEL SALVADOR			ES			
Huérfanos 1796 - Santiago Región Metropolitana						
LEVANTAMIENTO VITRAL 25			1/25	Ago. 13		
"San Jacobo"			Escala	Fecha		
TD	TD	LEV	DET	-		
1305						
Emisor	Proyecto	Fase	Tipo	Zona		
Dibujó: RM	Control: VI	Archivo de ref.: TD_1212_LEV_ES_VI-15-25.dwg				