



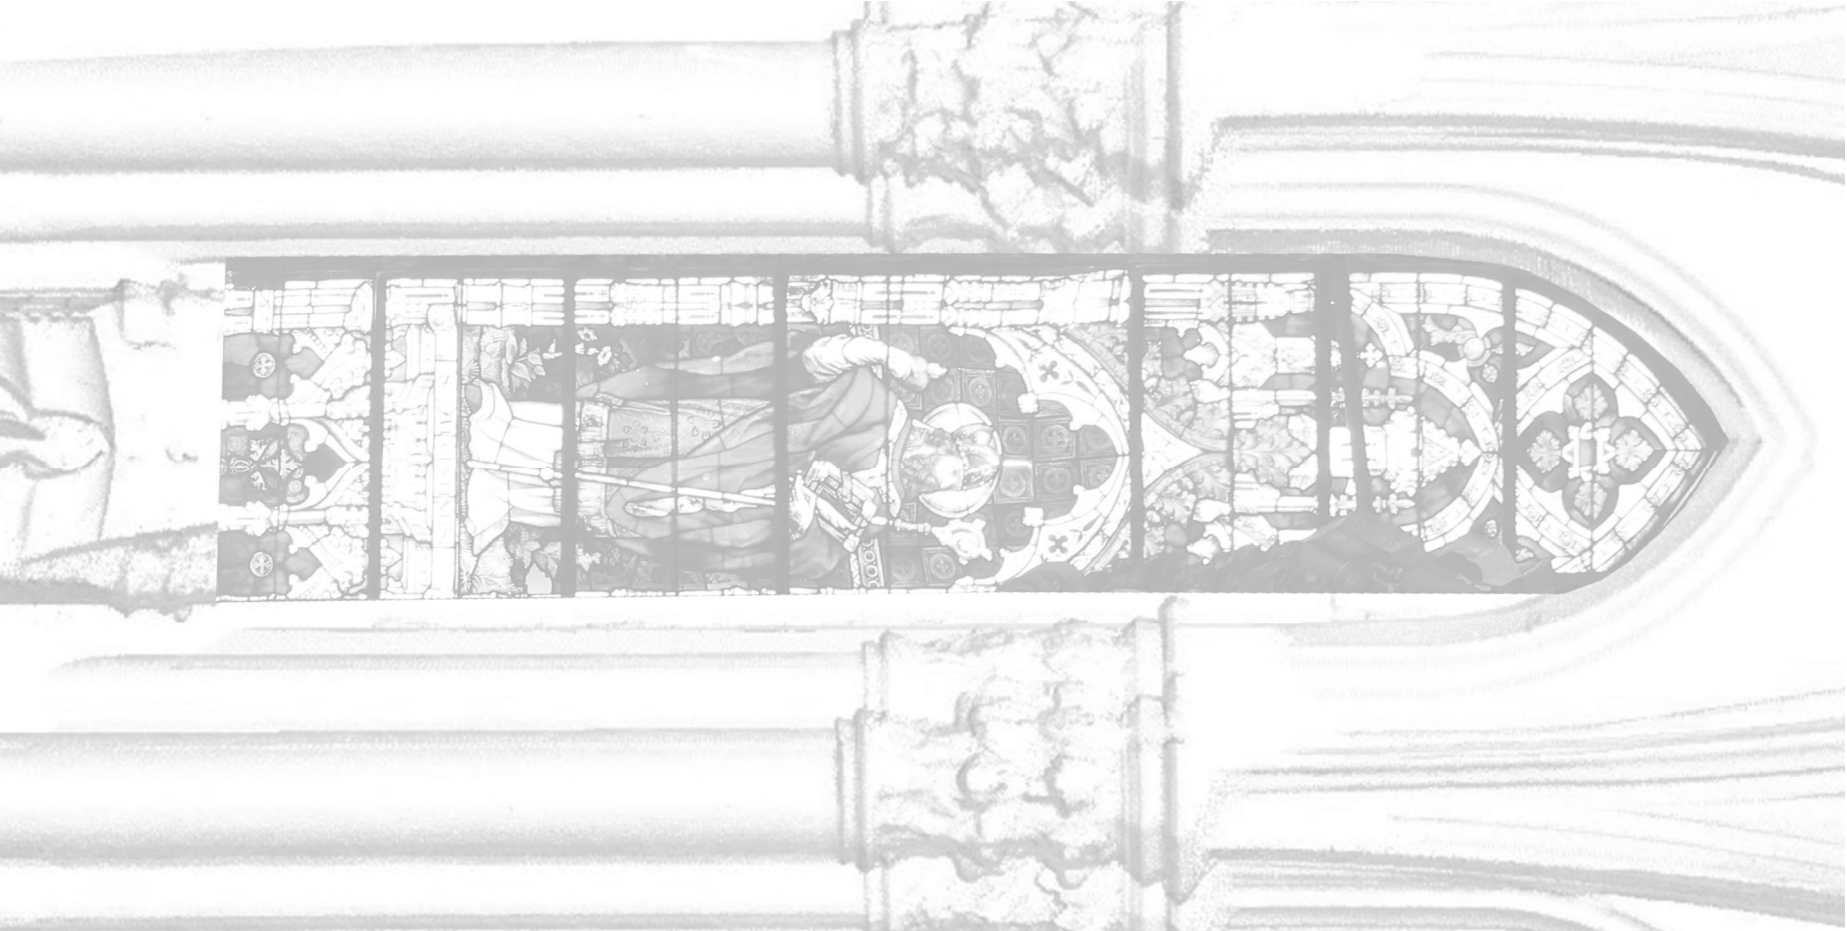

Elevación - Esc. 1/25

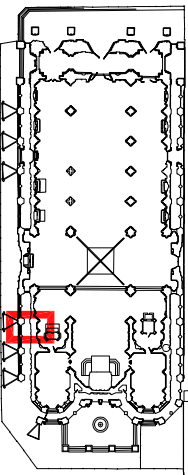

Levantamiento de Daños - Esc. 1/25

Ubicación									
					PROYECTO				
					Arqto. Dino Bozzi F. TÁNDEM Limitada contacto@tandemlimitada.cl				
DIRECCIÓN DE ARQUITECTURA DIRECCIÓN REGIONAL METROPOLITANA									
PROYECTO: REPARACIÓN PARCIAL BASÍLICA DEL SALVADOR STGO									
BASÍLICA DEL SALVADOR								ES	
Huérfanos 1796 - Santiago Región Metropolitana								Vi-26	
LEVANTAMIENTO VITRAL 26				1/25		Ago. 13			
"San Agustín"				Escala		Fecha			
TD		TD 1305		LEV	DET	-		A	
Emisor		Proyecto		Fase		Tipo		Zona	
Dibujó: RM		Controló: VI		Archivo de ref.: TD_1212_LEV_ES_Vi-26-34.dwg					