
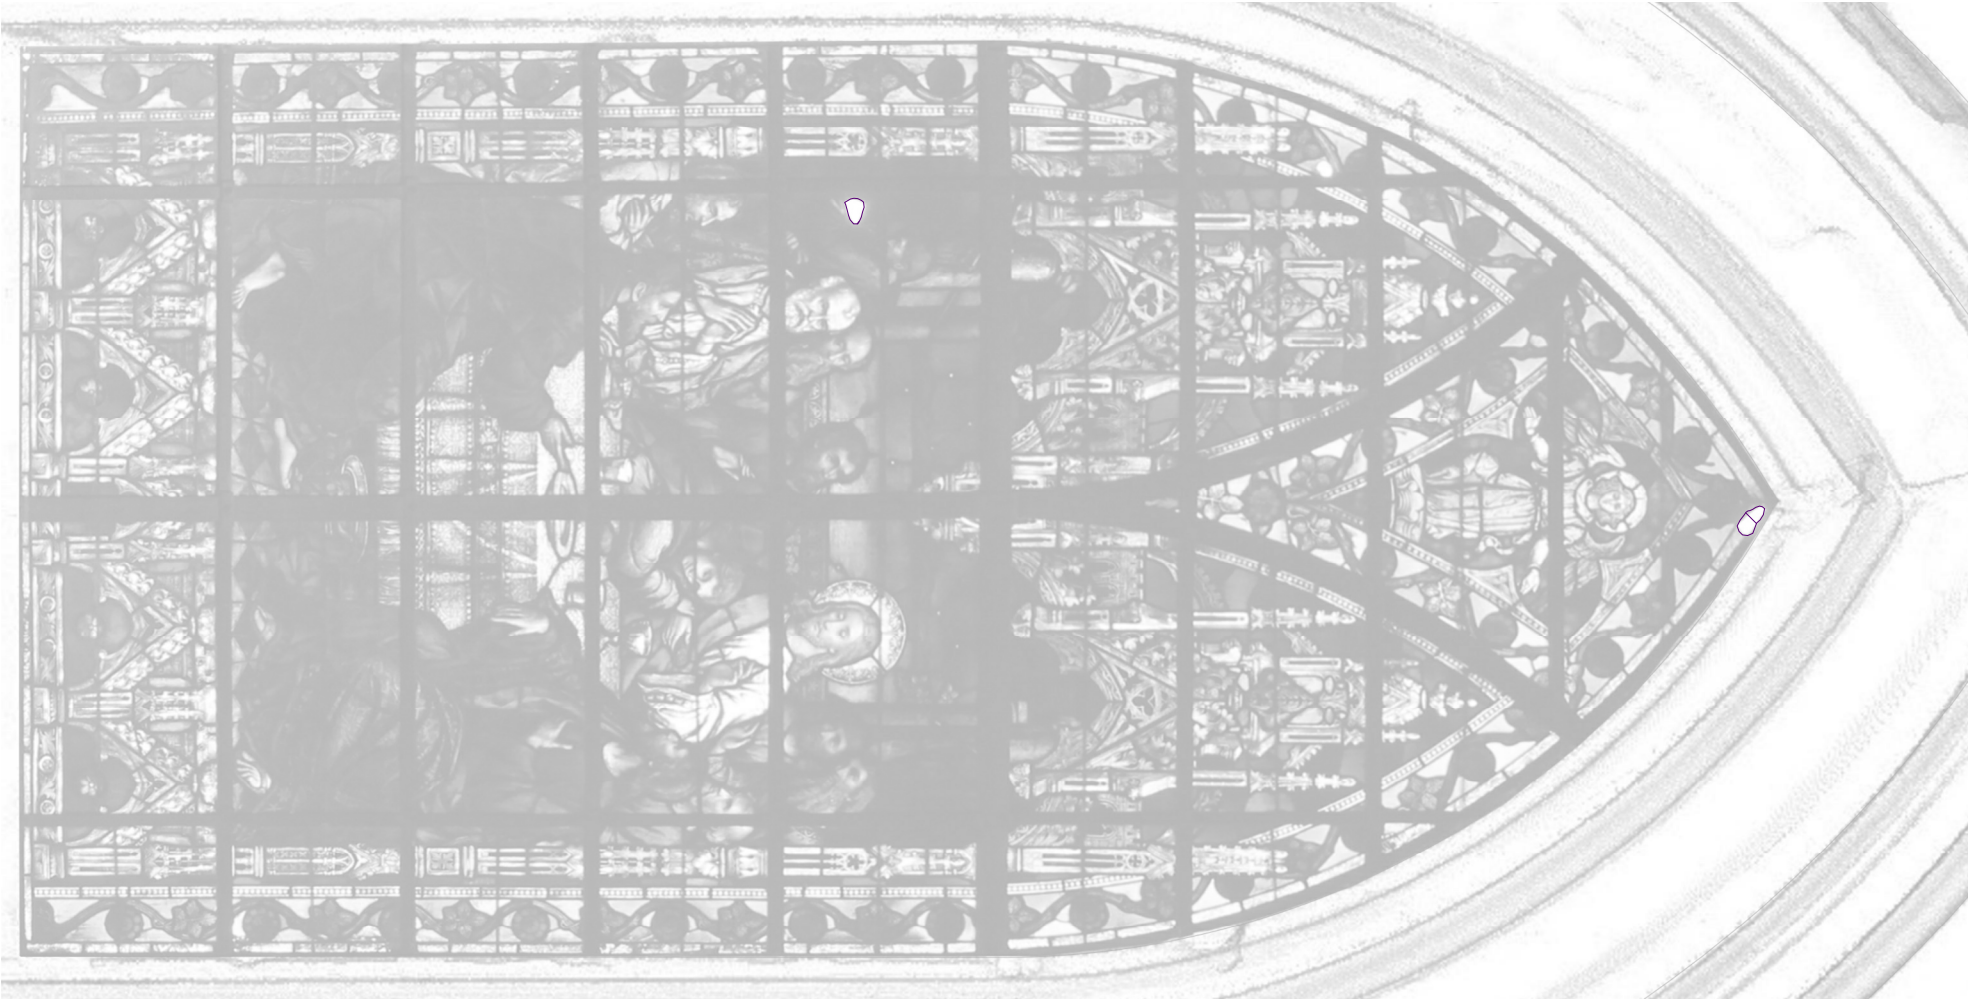


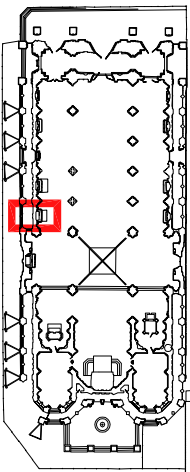

Elevación - Esc. 1/25

Levantamiento de Daños - Esc. 1/25

Ubicación				
				
PROYECTO			Arqto. Dino Bozzi F. TÁNDEM Limitada contacto@tandemlimitada.cl	
				
DIRECCIÓN DE ARQUITECTURA DIRECCIÓN REGIONAL METROPOLITANA				
PROYECTO: REPARACIÓN PARCIAL BASÍLICA DEL SALVADOR STGO				
BASÍLICA DEL SALVADOR			ES	
Huérfanos 1796 - Santiago Región Metropolitana			Vi-29	
LEVANTAMIENTO VITRAL 29			1/25	Ago. 13
"La Última Cena"			Escala	Fecha
TD	TD	LEV	DET	A
1305				
Emisor	Proyecto	Fase	Tipo	Zona
RM	VI	Archivo de ref.: TD_1212_LEV_ES_Vi-29-3d.dwg		