



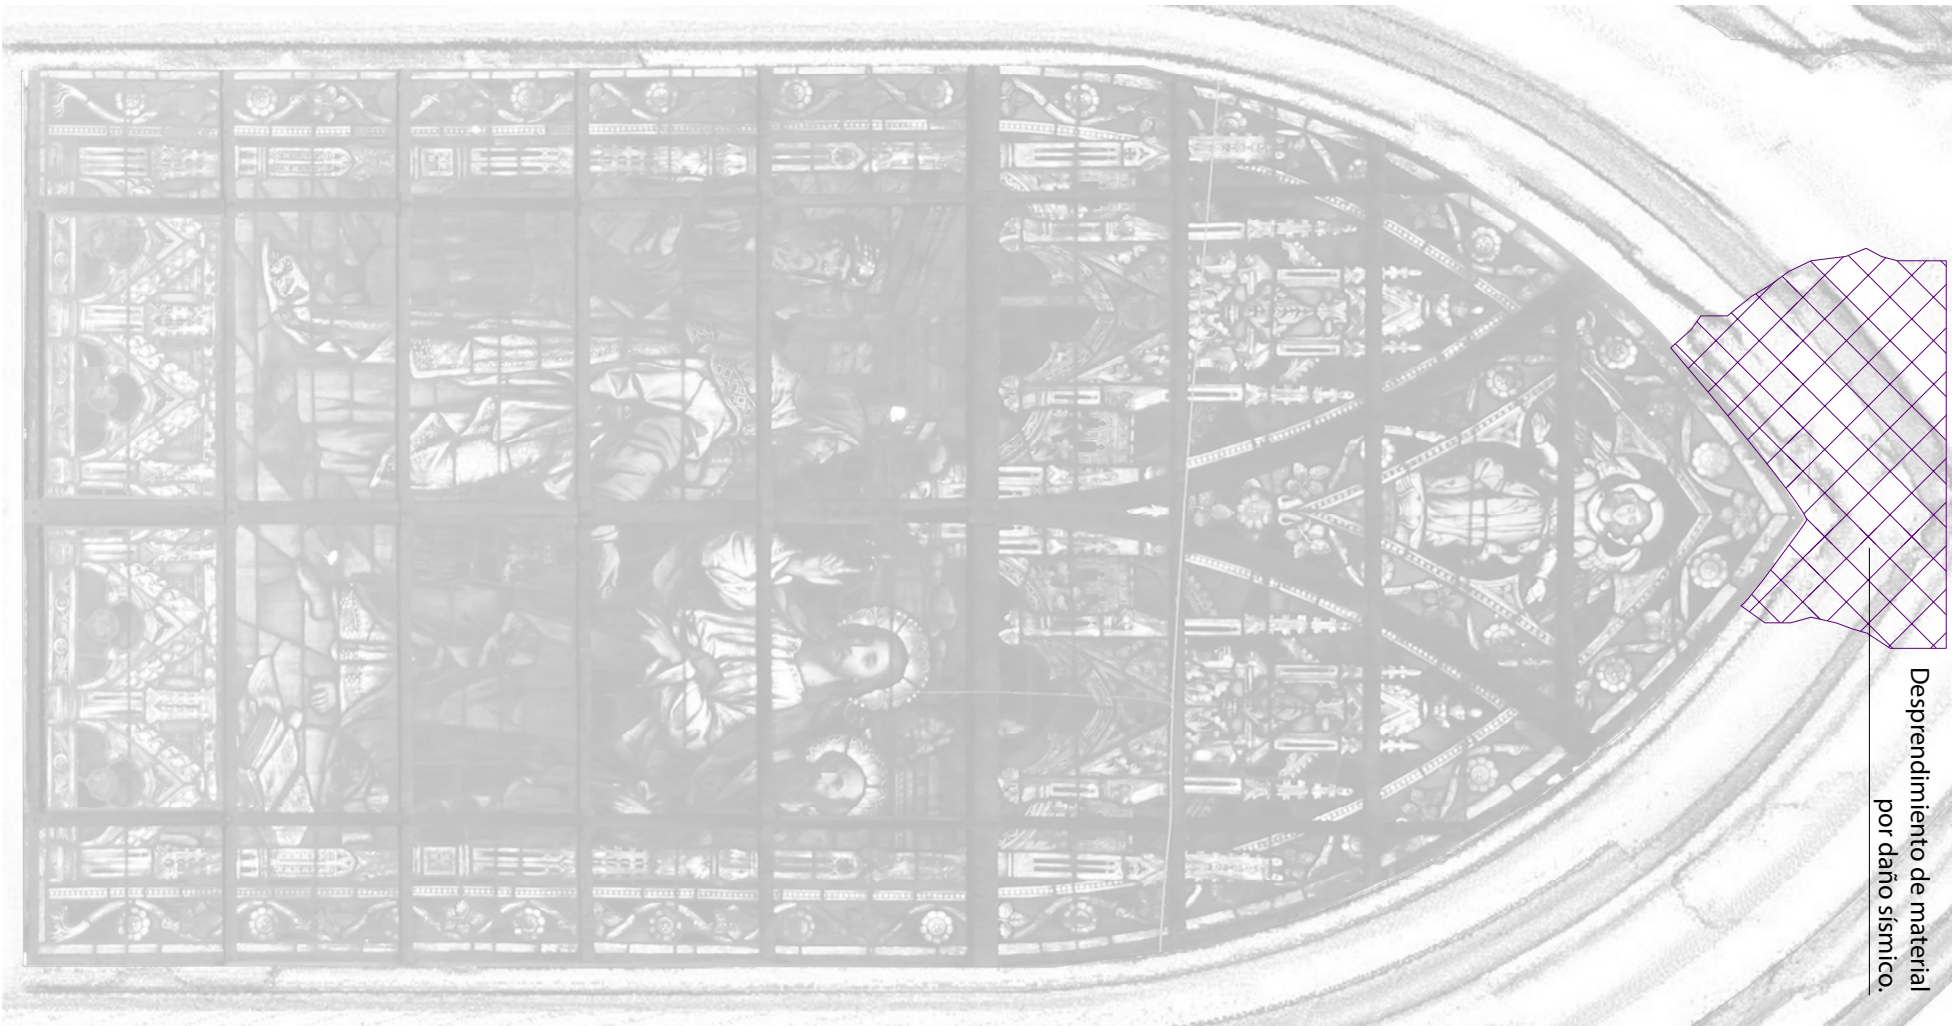

Elevación - Esc. 1/25

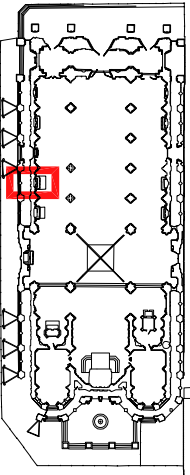

Levantamiento de Daños - Esc. 1/25

Ubicación							
PROYECTO					DIRECCIÓN DE ARQUITECTURA DIRECCIÓN REGIONAL METROPOLITANA		
PROYECTO: REPARACIÓN PARCIAL BASÍLICA DEL SALVADOR STGO					Arqto. Dino Bozzi F. TÁNDEM Limitada contacto@tandemlimitada.cl		
BASÍLICA DEL SALVADOR					ES		
Huérfanos 1796 - Santiago Región Metropolitana					VI-30		
LEVANTAMIENTO VITRAL 30					1/25	Ago.13	
"Al César lo que es del César..."					Escala	Fecha	
TD	TD	LEV	DET	-	A		
Emisor	Proyecto	Fase	Tipo	Zona	Índice		
Dibuj: RM	Control: VI				Archivo de ref.: TD_1212_LEV_ES_VI-26-34.dwg		