



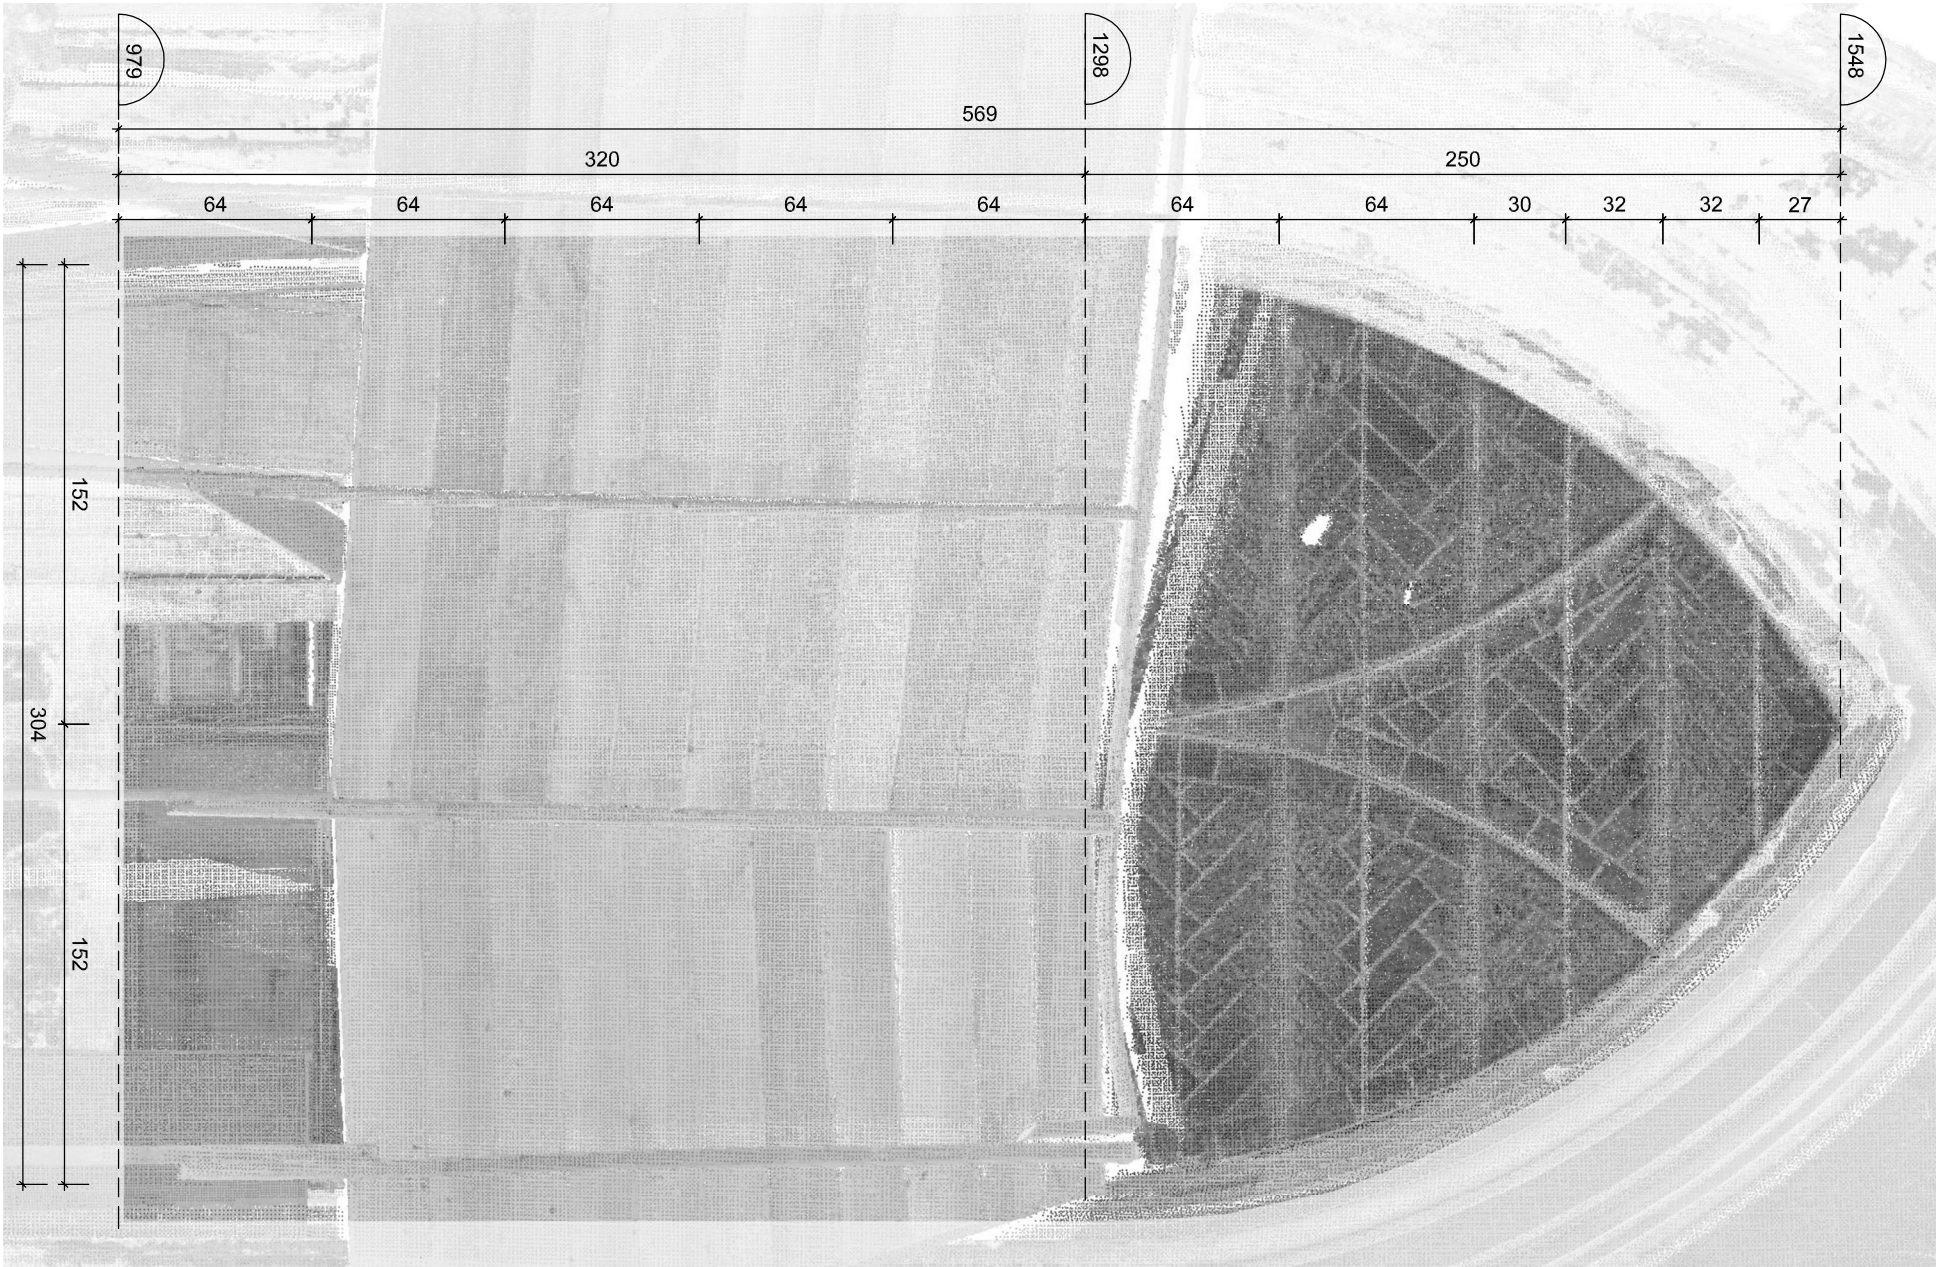

Elevación - Esc. 1/25

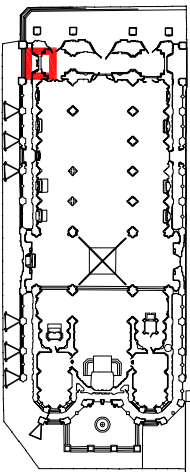

Levantamiento de Daños - Esc. 1/25

Ubicación														
					PROYECTO									
					Arqto. Dino Bozzi F. TÁNDEM Limitada contacto@tandemlimitada.cl									
DIRECCIÓN DE ARQUITECTURA DIRECCIÓN REGIONAL METROPOLITANA														
PROYECTO: REPARACIÓN PARCIAL BASÍLICA DEL SALVADOR STGO														
BASÍLICA DEL SALVADOR														
Huérfanos 1796 - Santiago Región Metropolitana								ES						
VI-34														
LEVANTAMIENTO VITRAL 34				1/25		Ago. 13								
vitral geométrico en coro				Escala		Fecha								
TD	TD	LEV	DET	-		A								
Emisor	Proyecto	Fase		Tipo	Zona	Índice								
Dibuj: RM	Control: VI			Archivo de ref.: TD_1212.LEV.ES_V426-34.dwg										