




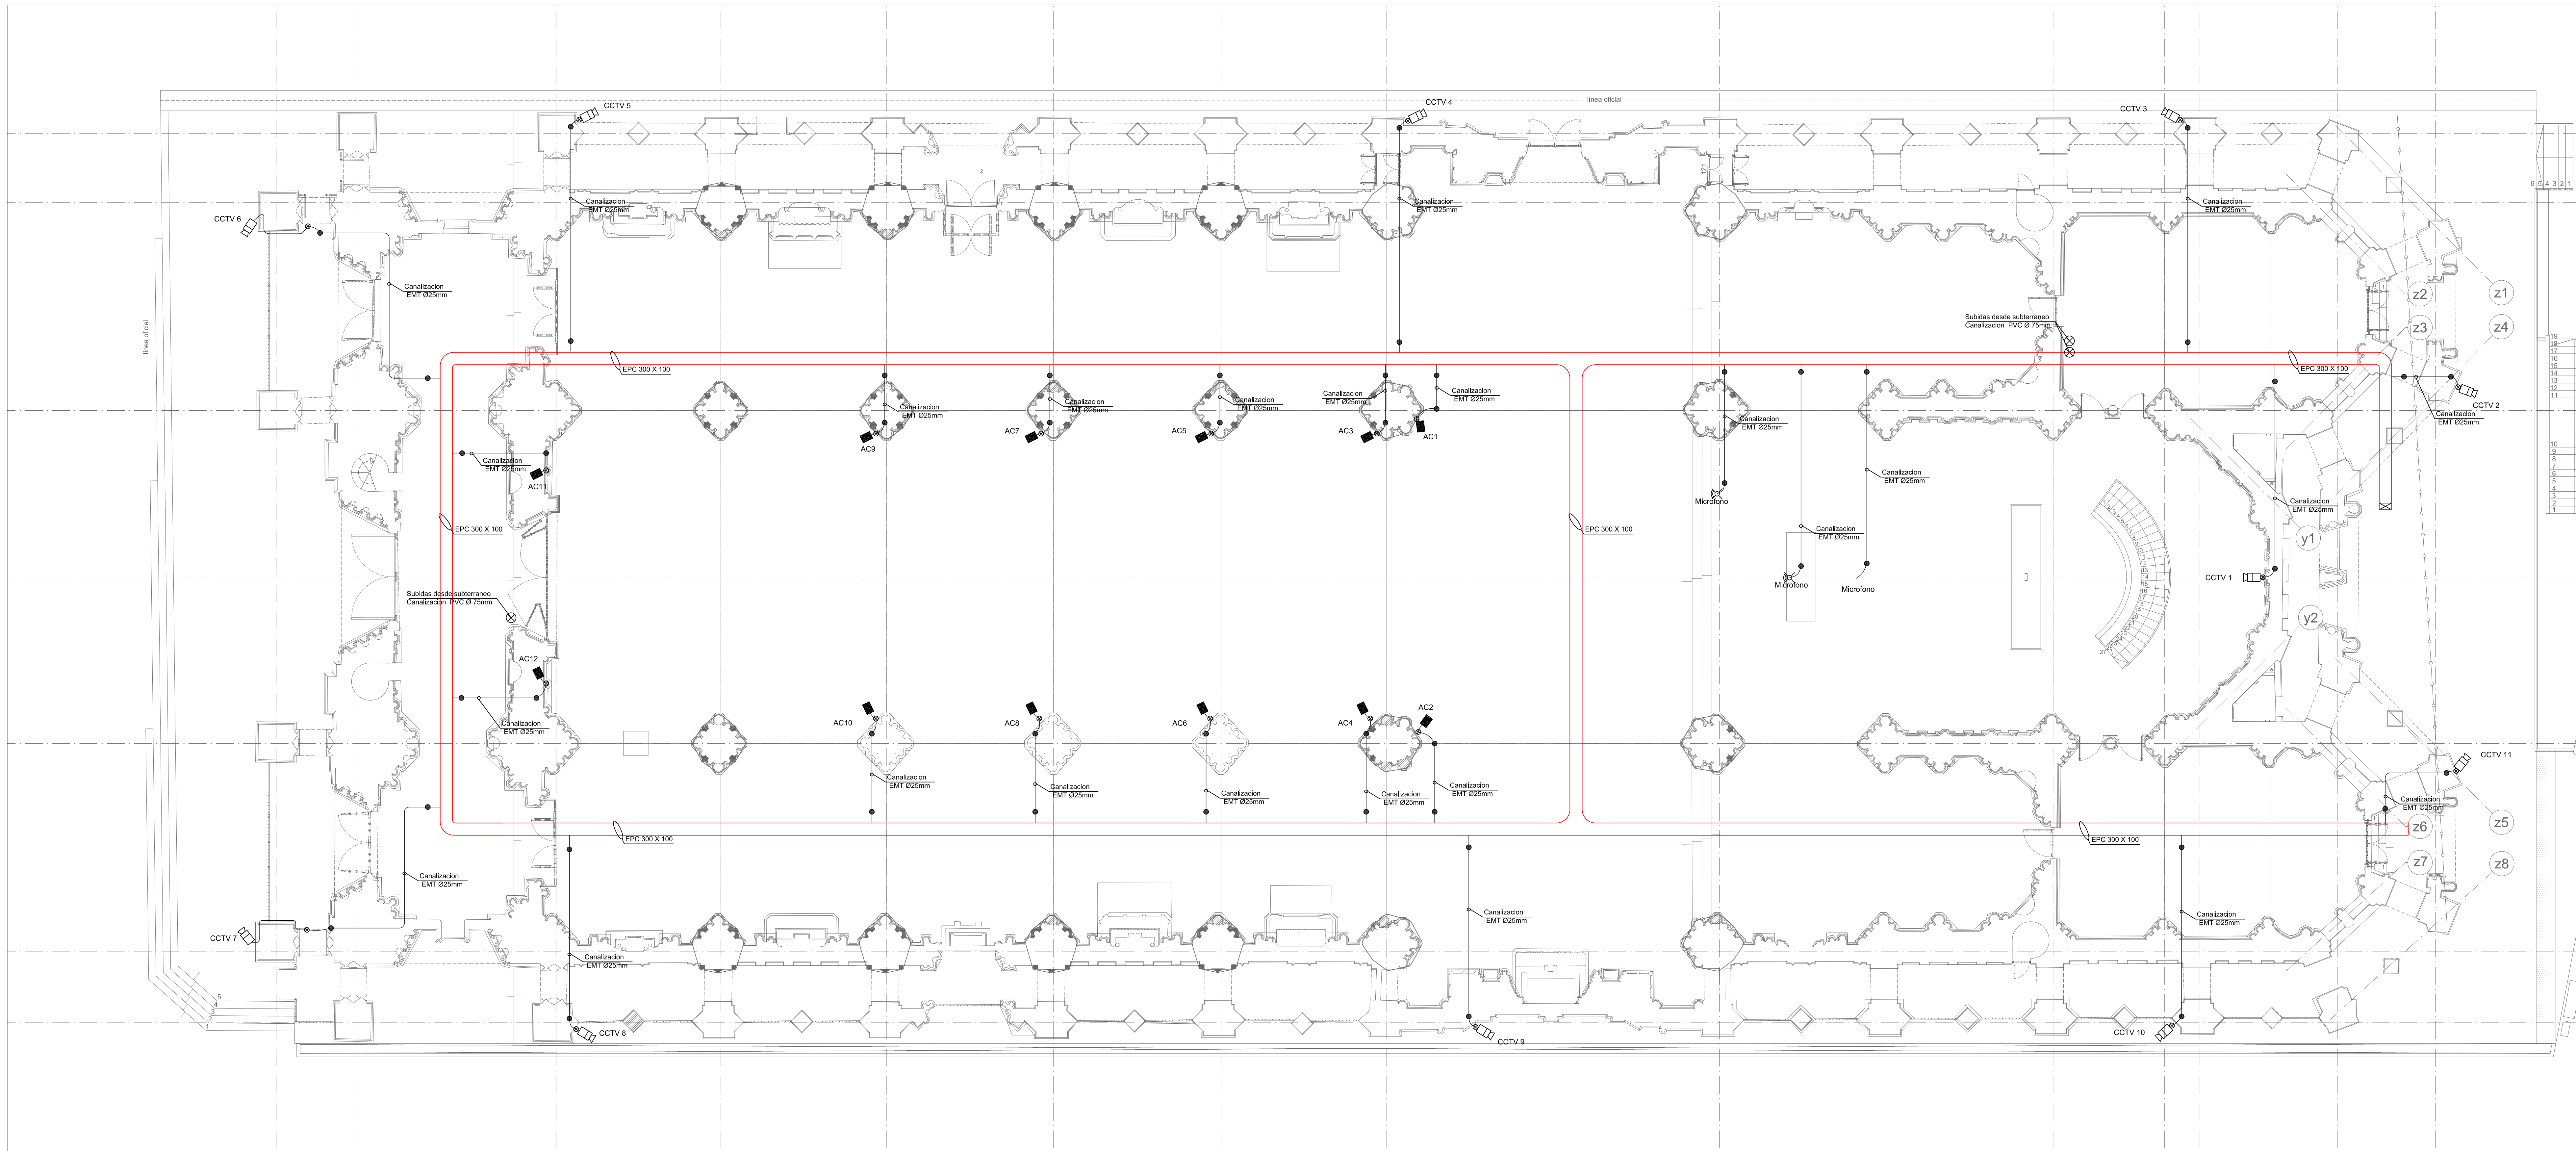

SIMBOLOGIA	DATOS TECNICOS
	PUNTO CONEX. CAMARAS CCTV
	PUNTO CONEX. DE PARLANTES
	MICROFONO
	AMPLIFICADOR DE AUDIO
	EQUALIZADOR DE AUDIO
	MESCLADOR CANALES AUDIO
	ESCALERILLA 300X100 CCDD

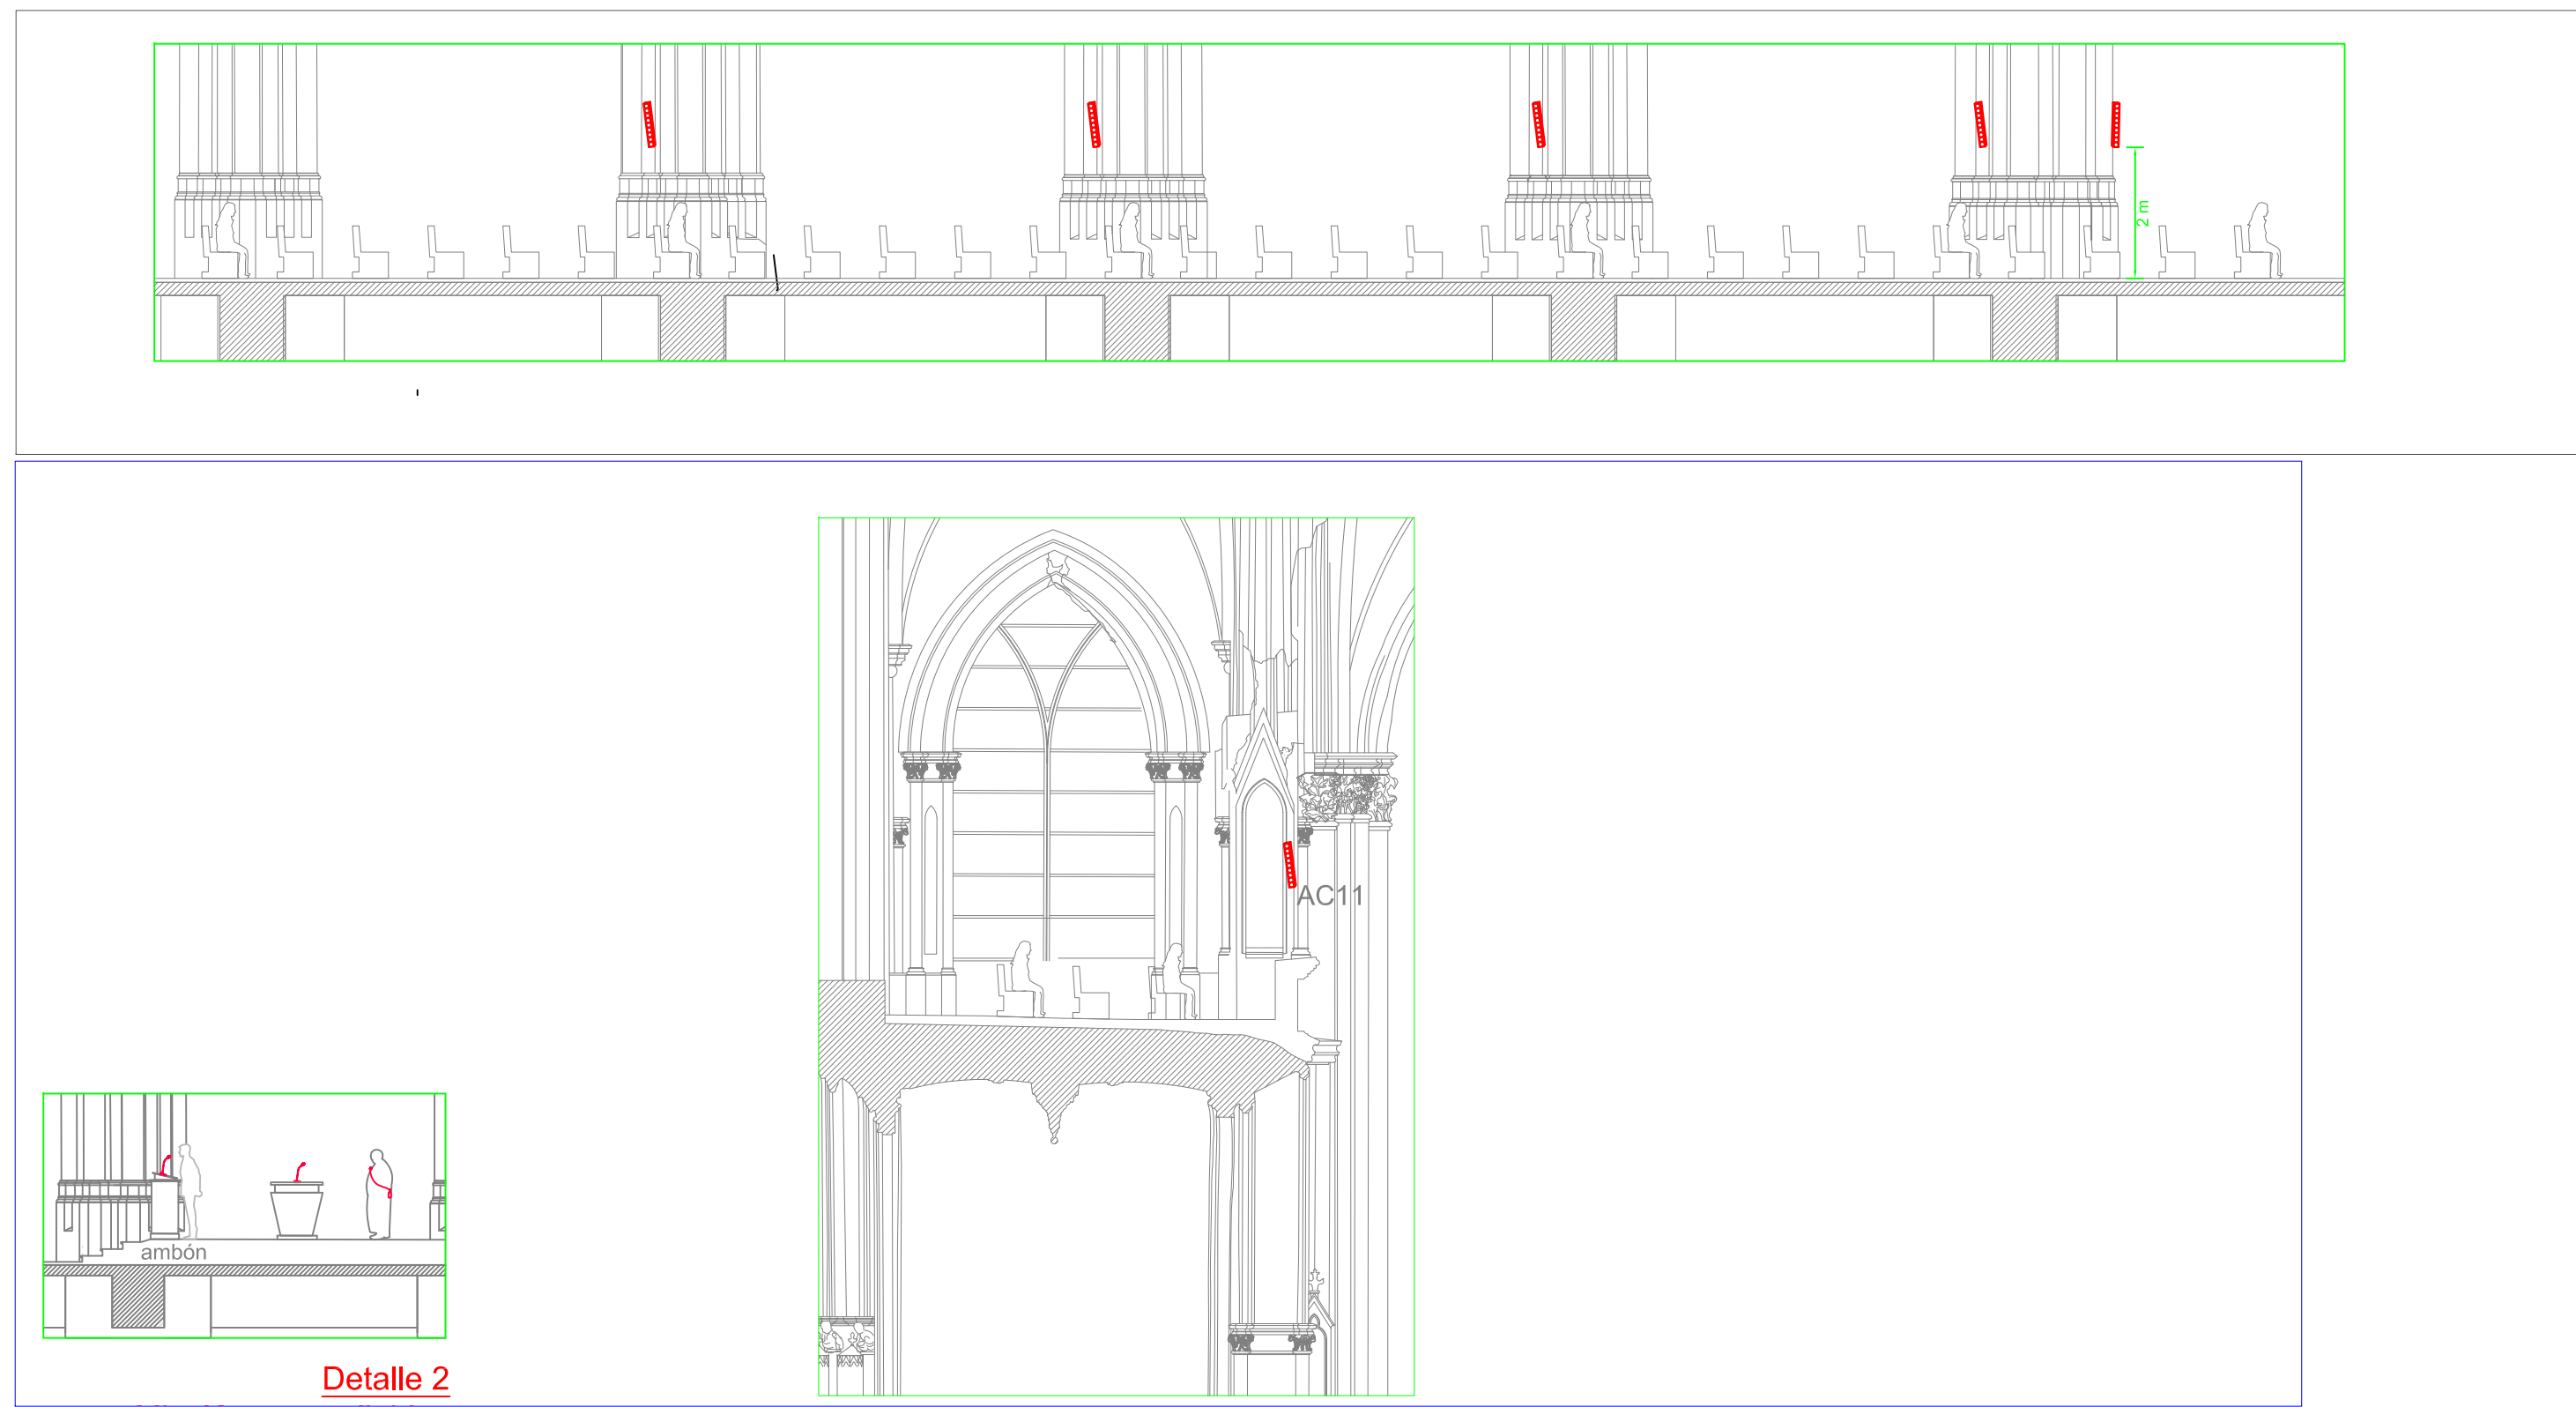

PLANTA DE CORRIENTES DEBILES
ESC. 1:100

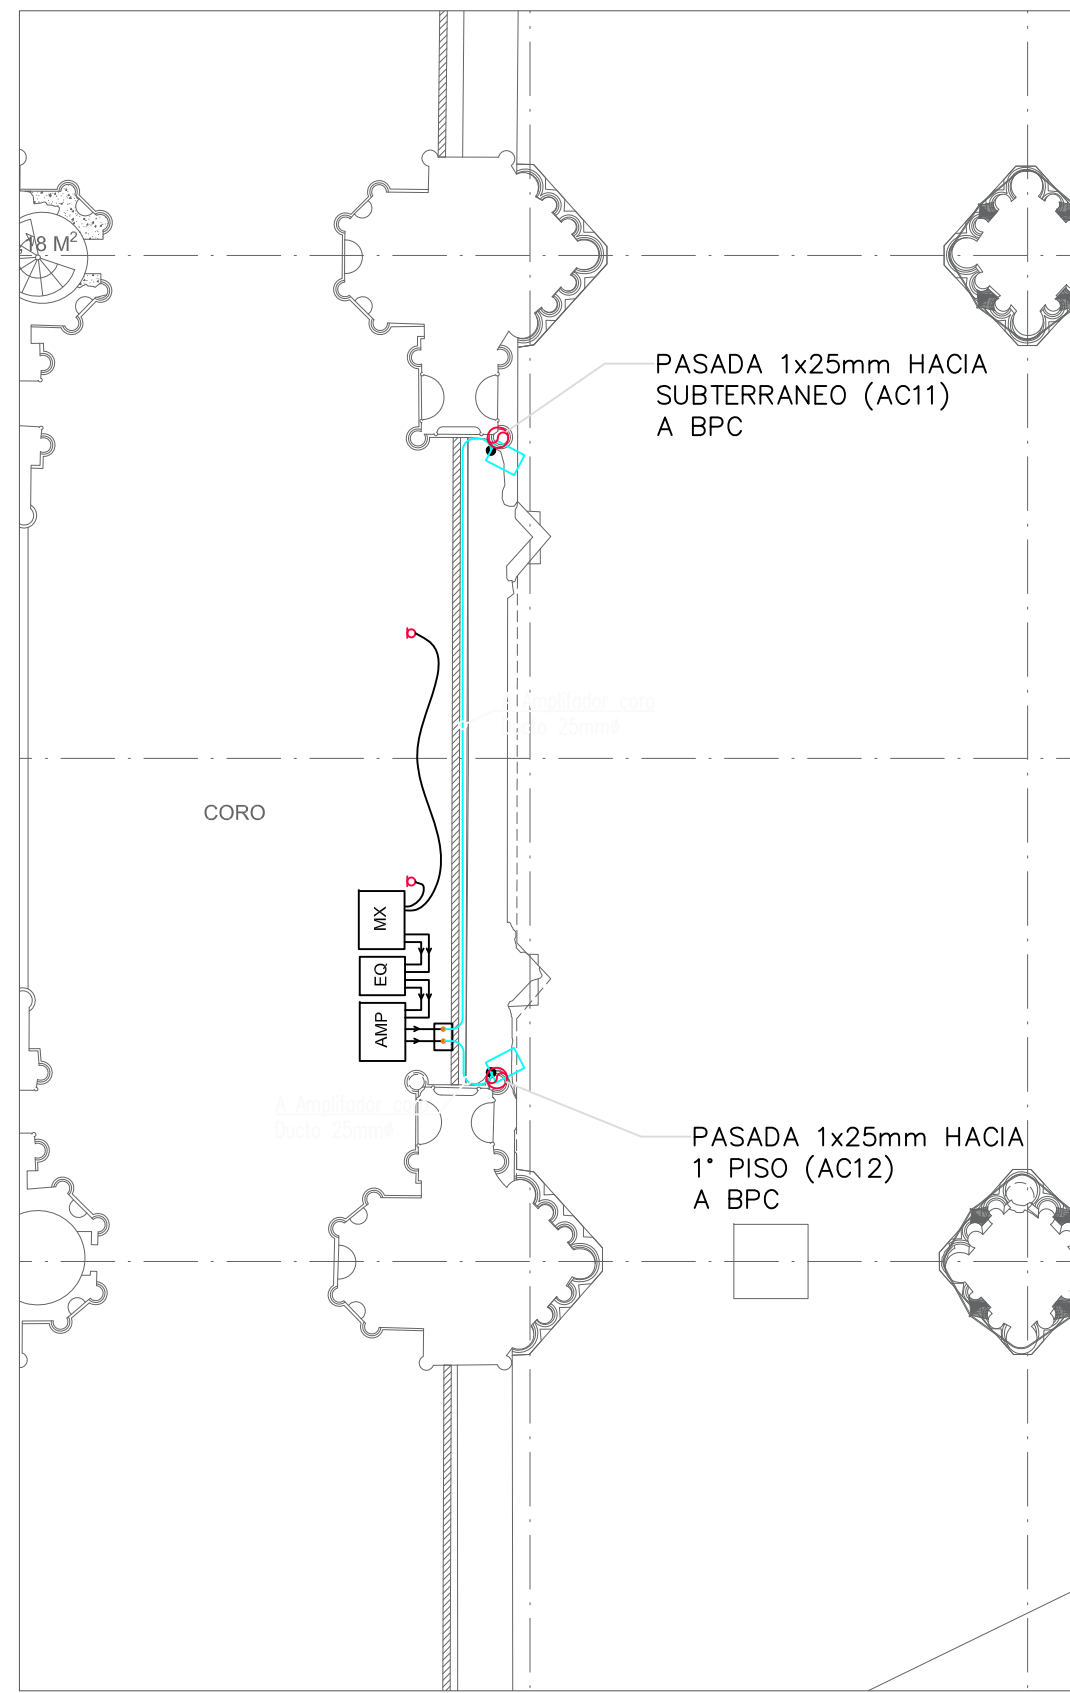

3	BRG	01/10/20	Revisión para documento ESE 07/2020
REV	POR	FECHA	MOTIVO
MODIFICACIONES			
CONTENIDO:	CORRIENTES DEBILES		
ARCHIVO-CAD :	DIMENSIONES FORMATO: 1189 x 841 mm		




PROYECTO ELECTRICO DE ALUMBRADO
RESTAURACIÓN BASILICA
DEL SALVADOR

CALLE : AGUSTIN M1781	LAMINA 07 DE 07 ESCALA: INDICADA
PROYECTO : A.Q.H. [DIBUJO] : C.A.A.	FECHA : DICIEMBRE 2019
PROPIETARIO	PROYECTO

PARROQUIA EL SALVADOR
RUT: 833.326-7
R.L.:
RUT:

ALEJANDRO QUEZADA HELMS
RUT: 164-7
INGENIERO ELECTRICO
LIC. SEC. C.A.S. A

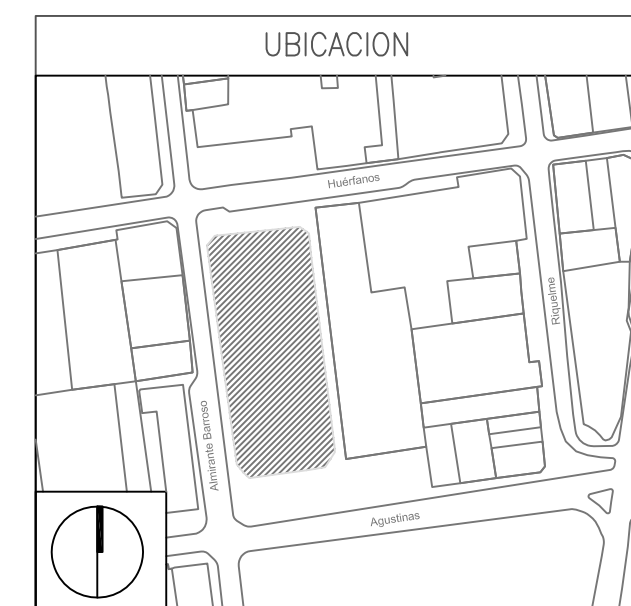

INSCRIPCION N° _____
FECHA : _____