


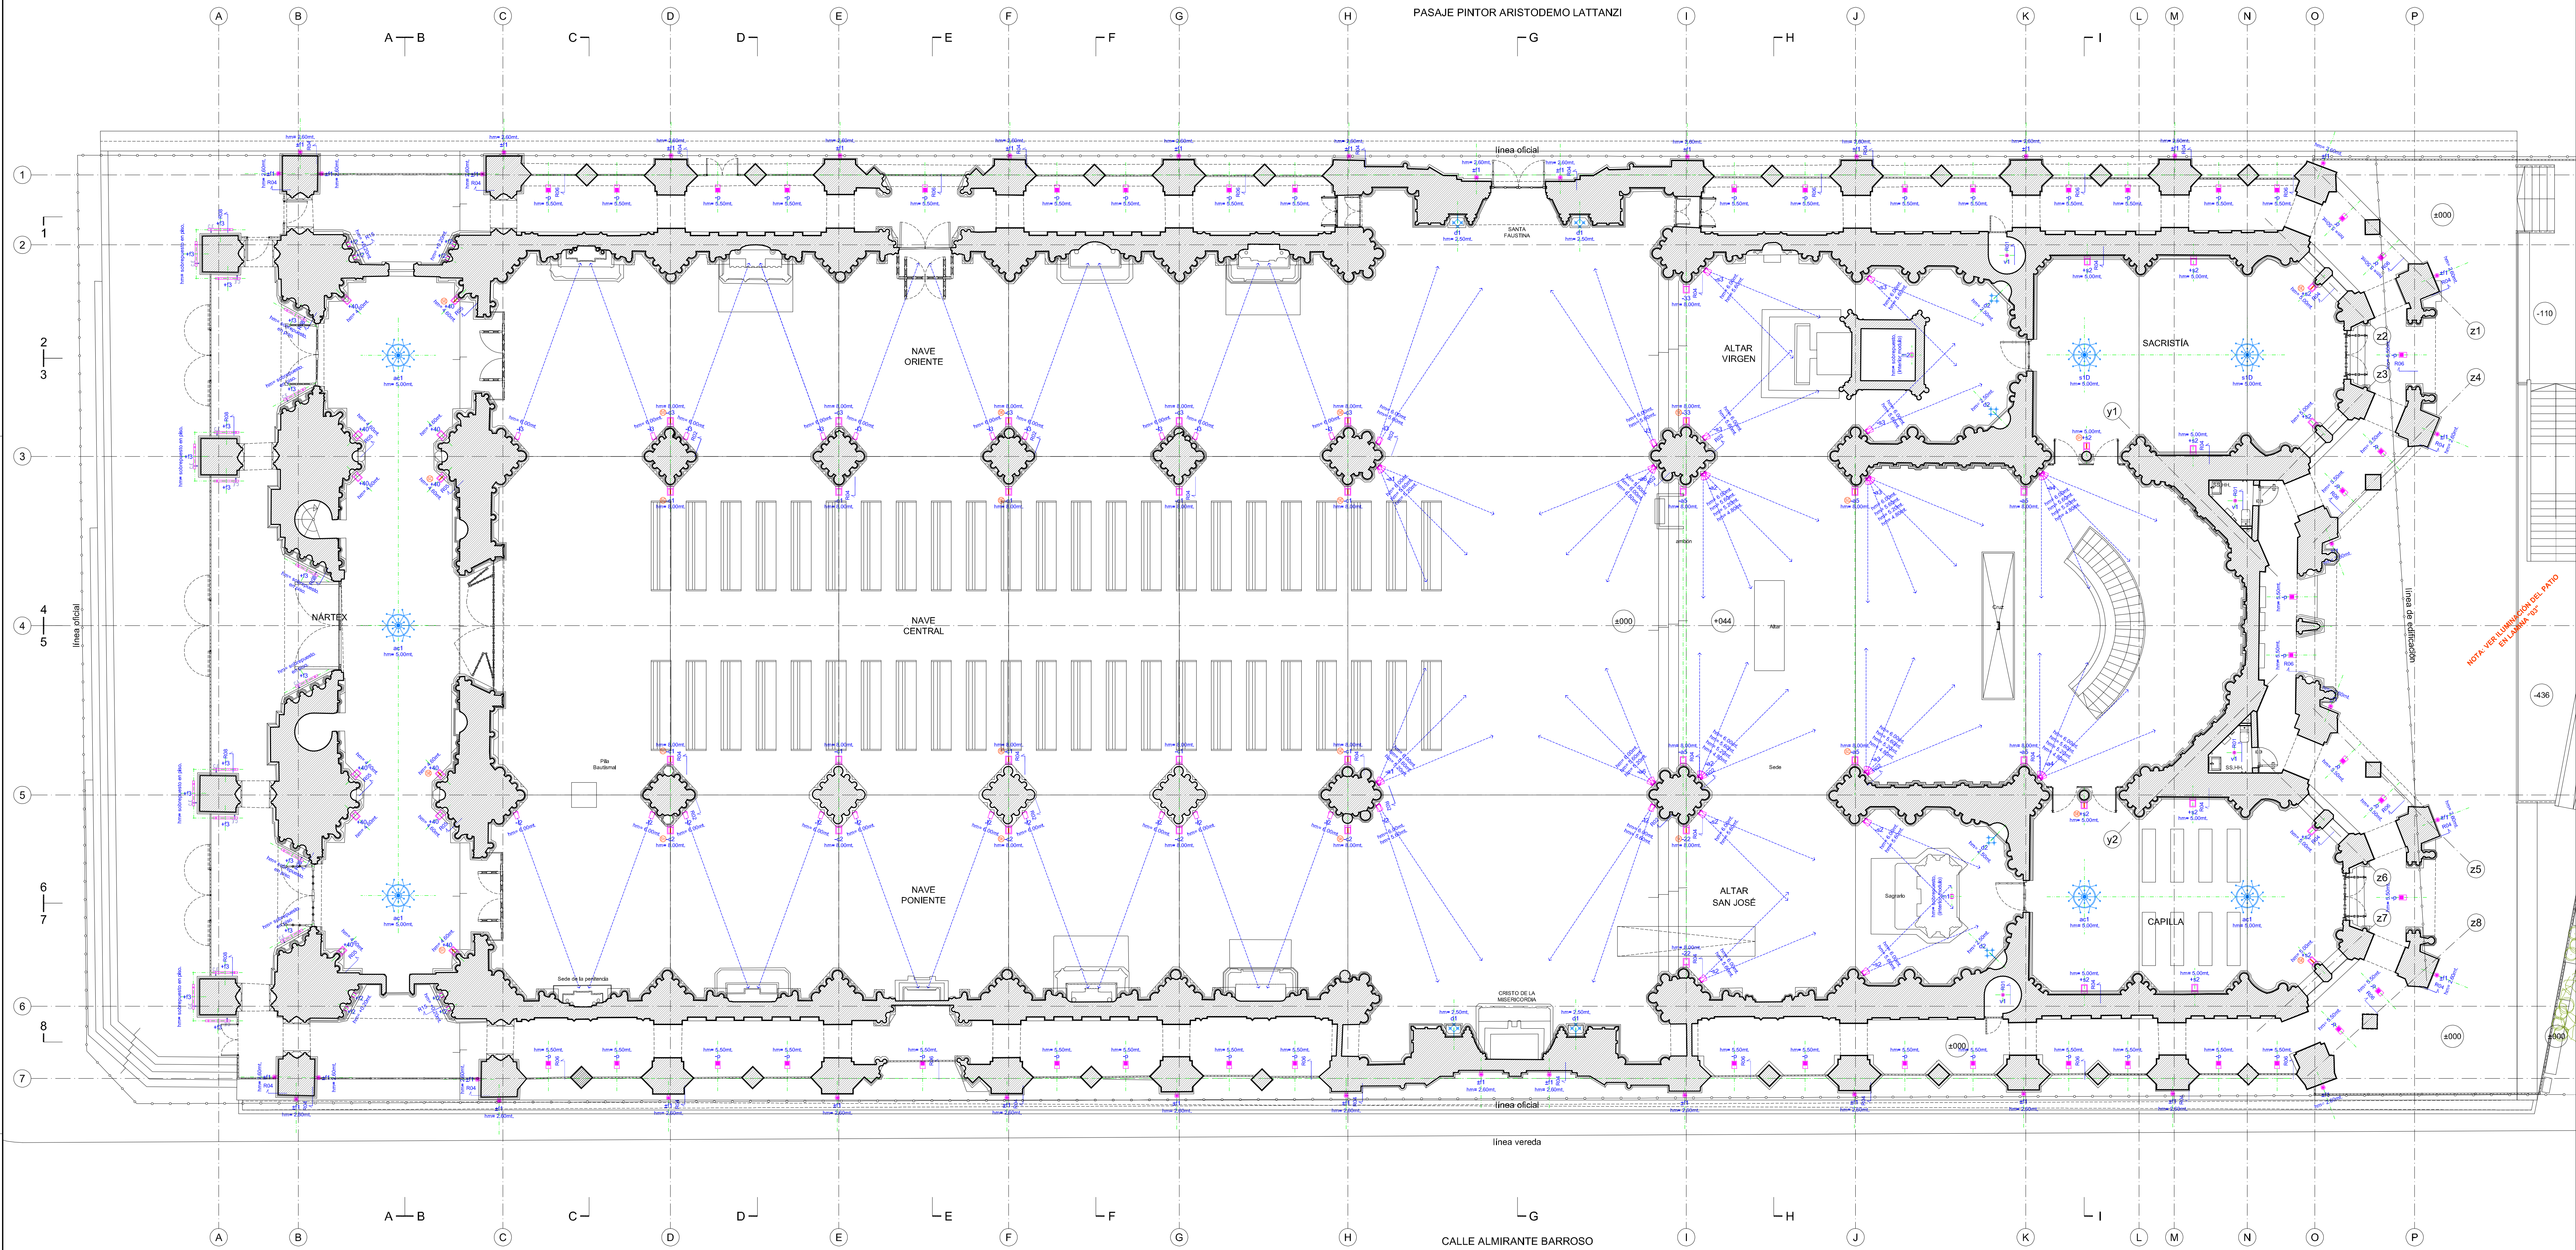

PLANTA DE ILUMINACIÓN
NIVEL NAVE CENTRAL
ESCALA: 1:100

NOTAS IMPORTANTES DEL PROYECTO

- T01 / GENERALES:**
- Todos los contenidos indicados en planos y/o especificaciones técnicas son de carácter informativo, siendo responsabilidad del proponente su verificación.
 - Punto de luz indica círculo independiente para iluminación puntual (no es una luminaria).
 - En cada espacio todas las luminarias que requieren recambio (Led Retrofit y/o fluorescente) deben ser de la misma marca para que no se produzcan diferencias de temperatura (T₁) y apariencia de color.
 - En cada ítem se indican las notas de montaje referentes a los luminarios.
 - Los requerimientos y fichas para los postes de las luminarias exteriores, se indican en la sección "T02".
 - La ubicación, distribución y cantidad de centros de luz indicados en el proyecto de iluminación prevalecen sobre el proyecto eléctrico.

T02 / PROVEEDORES:

- Se debe entregar una carta de garantía por los productos suministrados, indicando de forma clara las condiciones que aplican para su cumplimiento. También deben incluir los documentos técnicos que respalden la calidad de los luminarios, tales como certificados, ensayos nacionales y/o internacionales y los componentes requeridos por la S.E.C. si existieren conforme a la incorporación de nueva tecnología de iluminación.
- Todas las luminarias deben ser suministradas con las indicaciones de montaje y almacenamiento.
- Todos los equipos eléctricos (fuentes de poder y balastos) deben ser entregados por el proveedor, para garantizar la compatibilidad del sistema en cada luminario.
- Se debe solicitar muestra física de los luminarios, para:
- Coordinación en obra de los detalles de montaje.
- Revisión por parte del Mandante, Arquitectura y/o I.T.O. antes de la instalación.
- Aprobación por parte del Mandante, Arquitectura y/o proyectista.
- La constructora debe emitir planos y e.e.H. As Built.

T03 / PROPIETARIO (CONTRATISTA):

- Los luminarios deben corresponder a los especificados, sin variaciones en los requerimientos.
- No se aceptan luminarias alternativas a las especificadas, a no ser que sean de la misma marca y modelo.
- Si se requiere el cambio de los luminarios especificados, la responsabilidad del I.T.O. y el proyectista de iluminación la evaluación de alternativas que cumplan con las especificaciones de calidad requeridas para el proyecto.
- En los luminarios livianos industriales se indica el extremo de conexión, marcado con el ícono "C.E.", considerando un desplazamiento que permita el radio de curvatura normativo para el cable con cubierta E.V.A.
- Coordinación en obra de los detalles de montaje.
- Revisión por parte del Mandante, Arquitectura y/o I.T.O. antes de la instalación.
- Aprobación por parte del Mandante, Arquitectura y/o proyectista.
- La constructora debe emitir planos y e.e.H. As Built.

T04 / INSTALADOR:

- Se debe respetar la ubicación y distribución de los centros de los indicadores en los planos de iluminación, lo que prevalece sobre el proyecto eléctrico.
- En los luminarios livianos (botapuestas, embudillos, colgantes o tipo apalme) se debe considerar una copa de derivación indicada en el plano con el ícono "C.E." en el mínimo de cada círculo. Los otros luminarios de la cinta cuentan con sistema de interconexión incluido.
- En los luminarios livianos industriales se indica el extremo de conexión, marcado con el ícono "C.E.", considerando un desplazamiento que permita el radio de curvatura normativo para el cable con cubierta E.V.A.
- Los luminarios livianos embudillos consideran dos cables de suspensión, para anclarlos a la losa o estructura soporte.
- Los luminarios de sección circular consideran cables de suspensión independientes (uno para la carcasa, uno para la fuente de poder y uno para el cable de emergencia (cuando aplica)).
- La orientación de los luminarios exteriores debe corresponder a lo indicado en los esquemas de referencia.
- Para la instalación de los luminarios se deben retirar todos los elementos de empaque que puedan estar incluidos, en especial los plásticos que cubren los difusores y fuentes de poder.
- Los cables de alimentación con cubierta E.V.A. deben ser de un solo color para todo el proyecto, considerando blanco o negro.

T04 / INSTALADOR:

- Los cables de alimentación para circuito normal (Fase/Neutro/Tierra) deben ser conductores de tres cables y los que consideran circuito de emergencia (Fase/Neutro/Tierra + Fase para el auto-energado) deben ser de cuatro cables en el mismo conductor.
- Los cables de suspensión antistáticos de los luminarios deben ser multifilares y corresponder a los indicados en las especificaciones técnicas (sección "T01") y contar con las certificaciones y ensayos correspondientes.
- Los luminarios deben ser instalados con las fuentes de poder entregadas por el proveedor para cada ítem según correspondo, para asegurar la compatibilidad del sistema.
- Los luminarios no deben ser conectados directo a 220V sin fuente de poder.
- Se deben respetar las notas de montaje indicadas para cada ítem y las instrucciones entregadas por el proveedor.
- Se deben utilizar todos los accesorios de montaje entregados por el proveedor, para asegurar el funcionamiento de los luminarios.
- Para la instalación de los luminarios se deben retirar todos los elementos de empaque que puedan estar incluidos, en especial los plásticos que cubren los difusores y fuentes de poder.
- Cualquier accesorio de montaje entregado en obra debe ser sustituido por uno igual al original, en cuanto a materialidad y estética.
- Durante la instalación se debe evitar el encendido prolongado de los luminarios conectados al grupo electrógeno, con el objetivo de evitar variaciones de voltaje y desgaste de los componentes eléctricos de los luminarios.

4611 - RESTAURACION BASILICA DEL SALVADOR
PLANTA DE ILUMINACION NIVEL NAVE CENTRAL
ESCALA: 1:100

ITEM	CANTIDAD	SIMBOLOGIA	DATOS TECNICOS	LAMPARA
Q.0.1			FUENTE DE PODER ELECTRONICA INCORPORADA	LED CLASICA 2700...3000K
Q.0.2			FUENTE DE PODER ELECTRONICA INCORPORADA	LED CLASICA 2700...3000K
Q.0.3			FUENTE DE PODER ELECTRONICA INCORPORADA	LED CLASICA 2700...3000K
Q.0.4			FUENTE DE PODER ELECTRONICA INCORPORADA	LED CLASICA 2700...3000K
Q.0.5			FUENTE DE PODER ELECTRONICA INCORPORADA	LED CLASICA 2700...3000K
Q.0.6			FUENTE DE PODER ELECTRONICA INCORPORADA	LED CLASICA 2700...3000K
Q.0.7			FUENTE DE PODER ELECTRONICA INCORPORADA	LED CLASICA 2700...3000K
Q.0.8			FUENTE DE PODER ELECTRONICA INCORPORADA	LED CLASICA 2700...3000K
Q.0.9			FUENTE DE PODER ELECTRONICA INCORPORADA	LED CLASICA 2700...3000K
Q.0.10			FUENTE DE PODER ELECTRONICA INCORPORADA	LED CLASICA 2700...3000K
Q.0.11			FUENTE DE PODER ELECTRONICA INCORPORADA	LED CLASICA 2700...3000K
Q.0.12			FUENTE DE PODER ELECTRONICA INCORPORADA	LED CLASICA 2700...3000K
Q.0.13			FUENTE DE PODER ELECTRONICA INCORPORADA	LED CLASICA 2700...3000K
Q.0.14			FUENTE DE PODER ELECTRONICA INCORPORADA	LED CLASICA 2700...3000K
Q.0.15			FUENTE DE PODER ELECTRONICA INCORPORADA	LED CLASICA 2700...3000K
Q.0.16			FUENTE DE PODER ELECTRONICA INCORPORADA	LED CLASICA 2700...3000K

EDIC	FECHA	OBSERVACIONES	ILUM	ARG
E01				
E02				
