
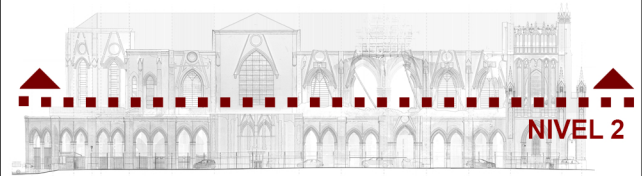
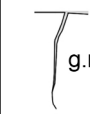
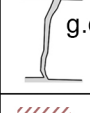


INDIVIDUACIÓN Y LOCALIZACIÓN PLANTA ANALIZADA:	
PLANTA DE CIELO NIVEL 2	
	
PATRÓN DE GRIETAS Y DEFORMACIONES	
	Grieta Capilar Inicial, g.i.i, y Avanzada, g.a.i En la primera fase de una Grieta Capilar, inicial, no es posible determinar directamente los puntos correspondientes de los "ciglios", sino solo las formas de fisuras, mientras en la fase avanzada es posible individuar ambos elementos de análisis.
	Grieta rotativa por Flexión, g.r.i El tronco durante el agretamiento experimenta una rotación rígida por la cual los dos "ciglios" de la grieta se alejan.
	Grieta de desprendimiento por Tracción, g.d.i El tronco está completamente separado del resto del edificio.
	Colapso parcial o pérdida de material
	Colapso total, descomposición localizada con expulsión de piezas. Levantado 9 febrero 2017
	Colapso total, descomposición localizada con expulsión de piezas. Levantado el 20 diciembre 2018
	Desprendimiento de viga o tirante metálico Desprendimiento de viga o tirante y pérdida de operabilidad o , y/o deformación severa de una llave.
	Daños levantados el 9 febrero 2017
	Daños levantados el 14 diciembre 2018
FENOMENOS DE DEGRADACION QUE REDUCEN LA EFICIENCIA ESTRUCTURAL	
	Degradación del ladrillo Erosión,Er.i, y Musgos líquenes y hongos, M.l.h.i
	Presencia de vegetación, Vi
	Discontinuidades estructurales Materialidad heterogénea (Hormigón, H.A., Acero, A., Tabiquería de acero y geso, T.a.g.i, Incannucciato, I.i)

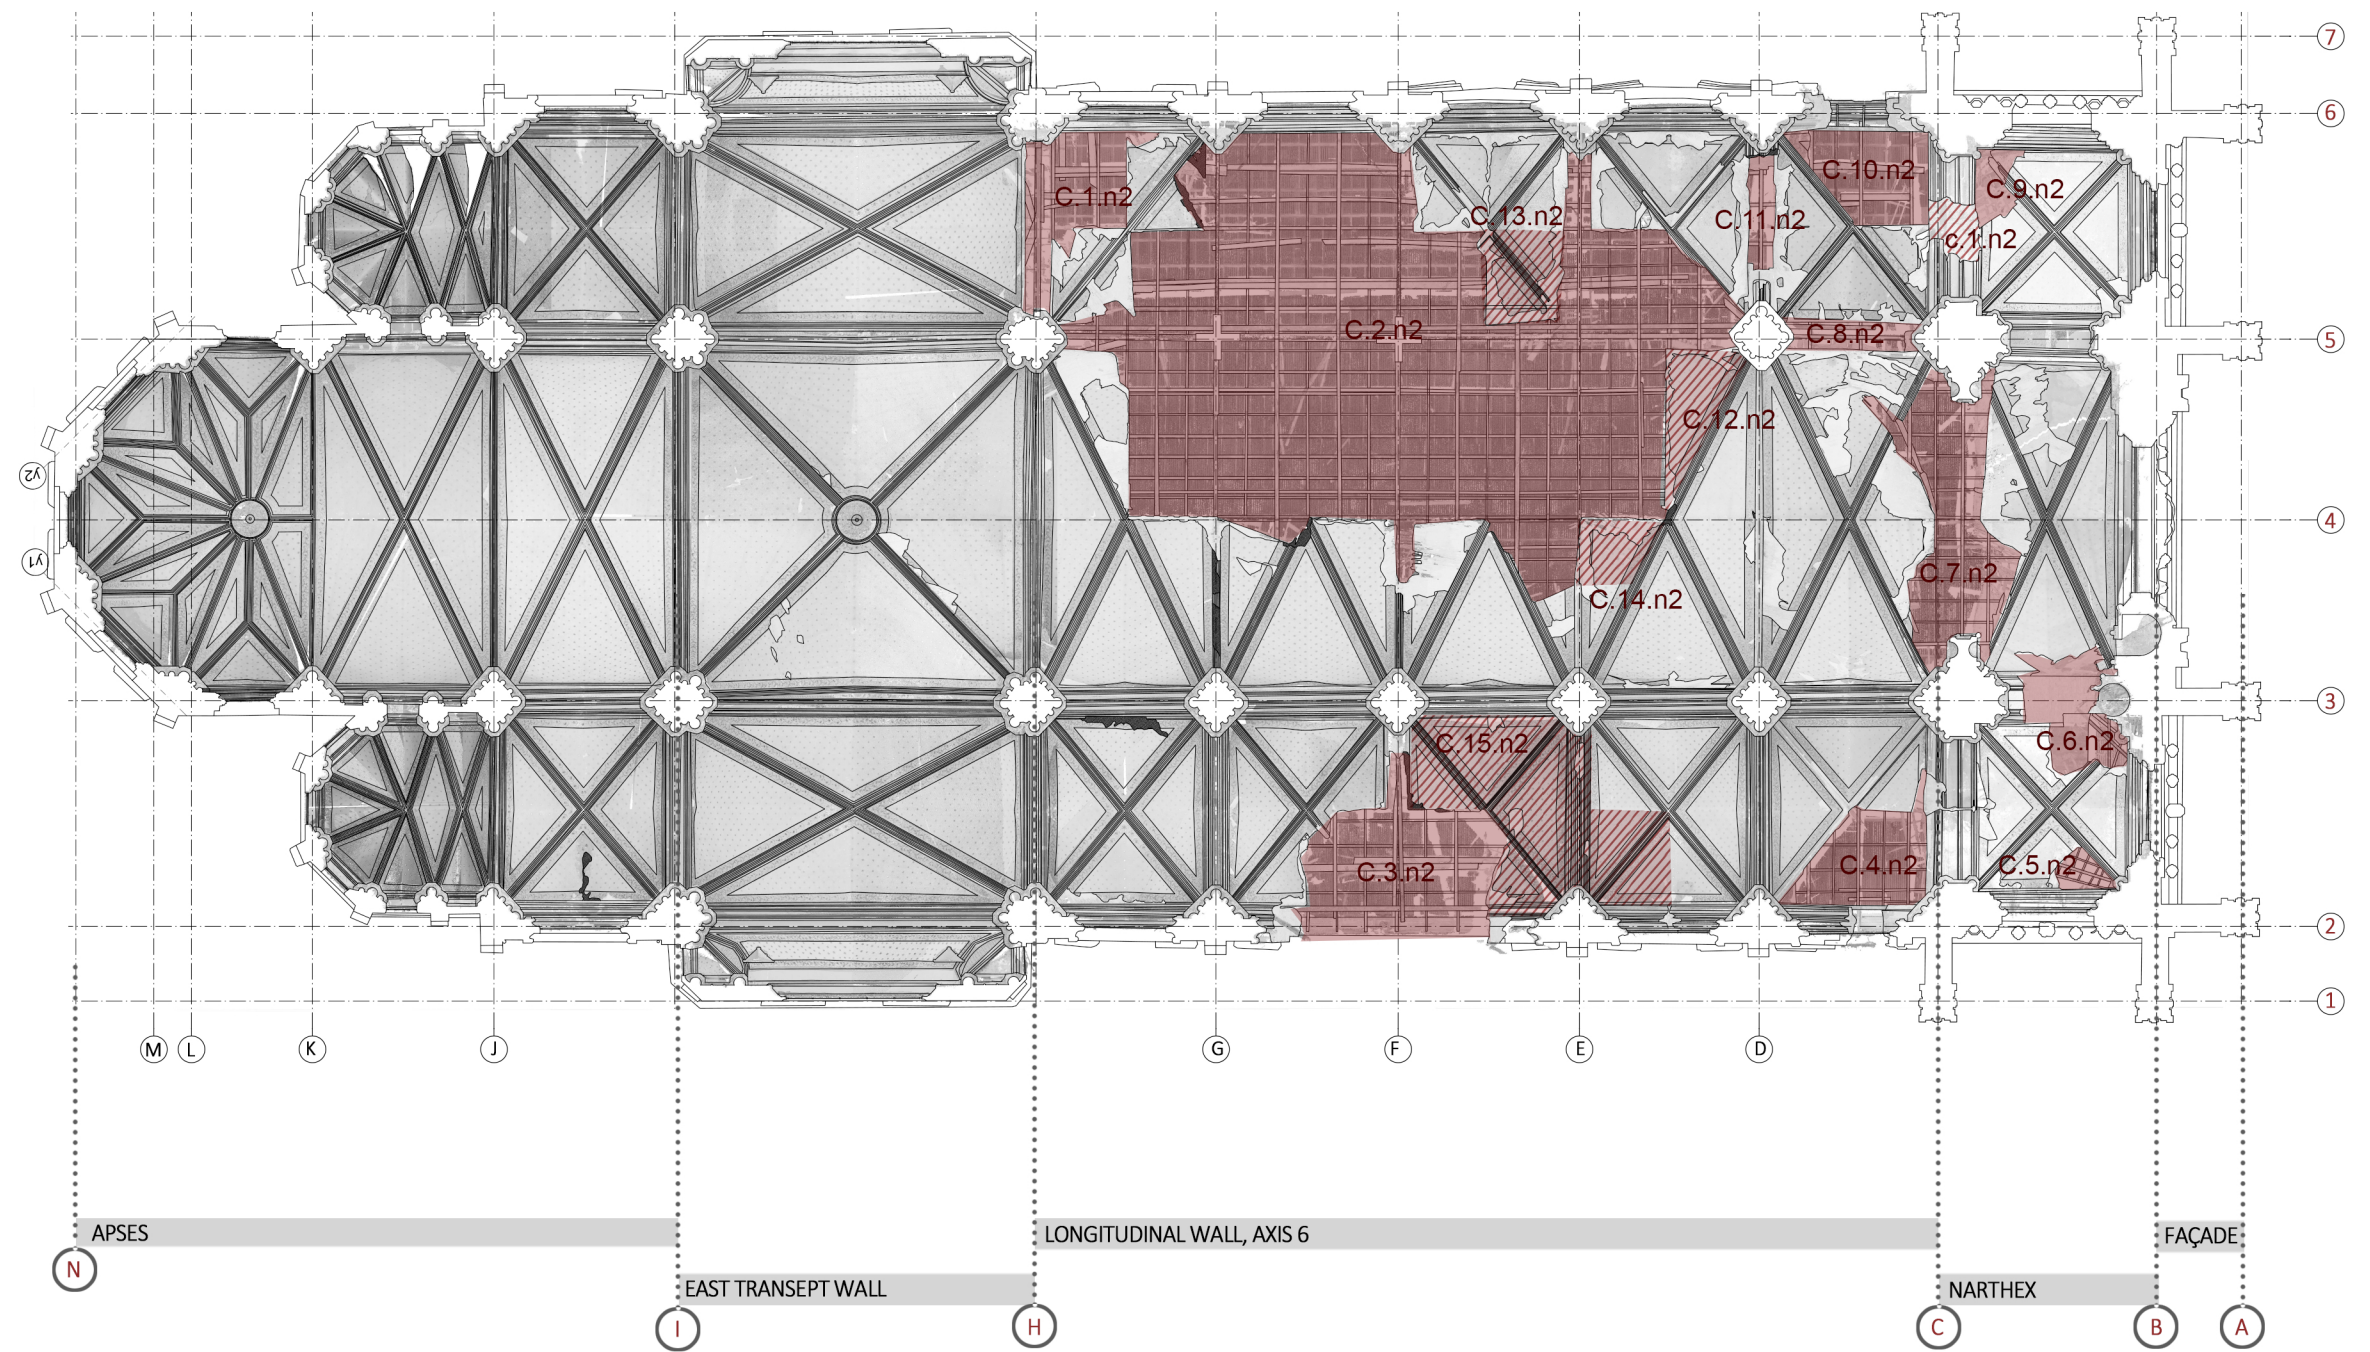

PLANIMETRIA CIELO NIVEL 2