

MONICA PEREZ & ASOCIADOS
a r q u i t e c t u r a d e l u z ®

Consultoría y Desarrollo de Proyectos de iluminación

Málaga 115 OF. 813 Las Condes, Santiago

Telefonos: 263 13 12, 228 23 38

e-mail: monica7@arquiluz.cl

PROYECTO DE ILUMINACION: 4611
RESTAURACIÓN BASÍLICA DEL SALVADOR


Edición "E"

14 de Agosto de 2020


PROYECTO

DETALLES Y ESQUEMAS DE REFERENCIA


NOTA GN01: Todas las medidas de las estructuras y sistemas de anclaje indicadas en los detalles, deben ser revisadas y validadas por el especialista de cálculo del proyecto.

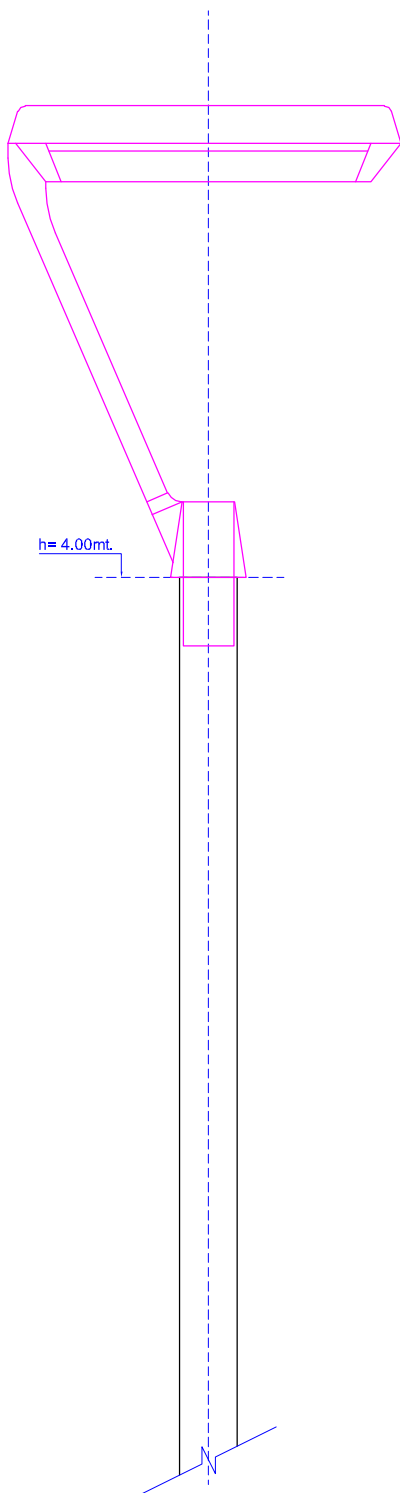


**VISTA LATERAL
CORONACION DE ANCLAJE**
esc. 1:10

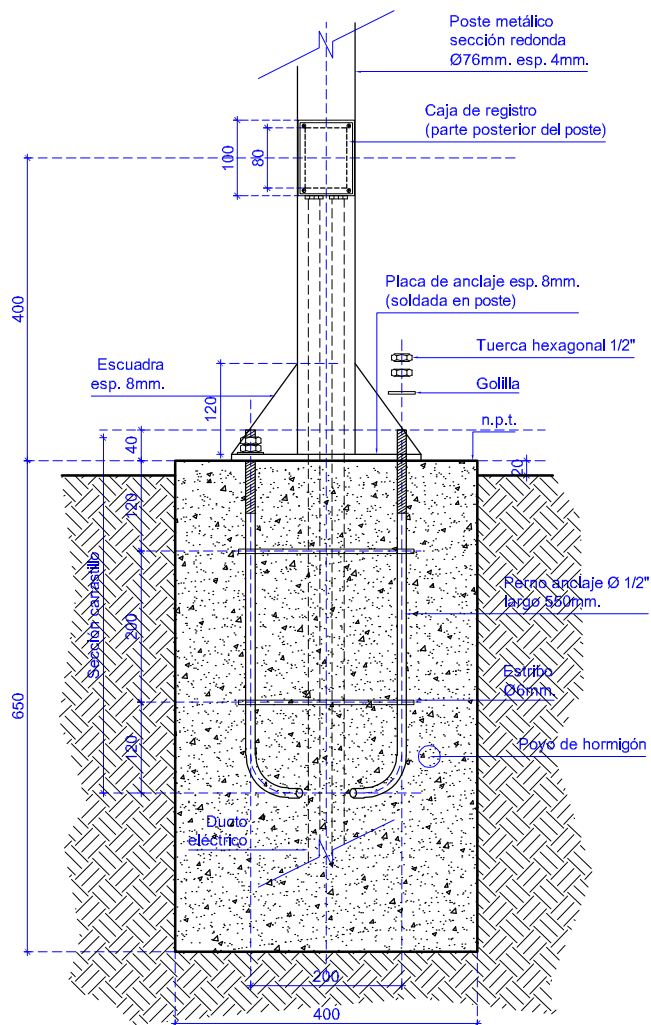


DETALLE ANCLAJE POSTE
esc. 1:10

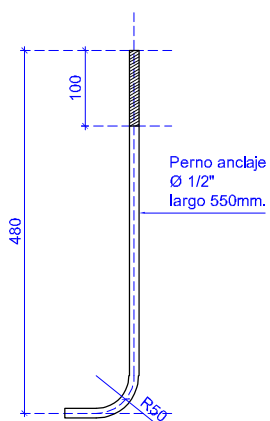

PERNO DE ANCLAJE
esc. 1:10

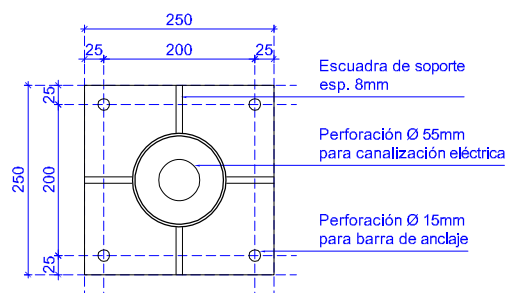

PLACA BASE DE ANCLAJE (Poste)
esc. 1:10

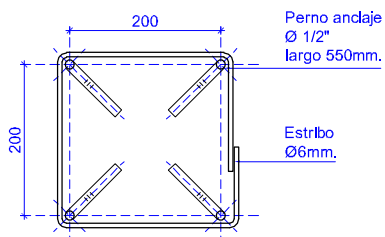


CANASTILLO DE ANCLAJE
esc. 1:10


ESQUEMA M01 / DETALLES

Poste E400-P. / Luminaria patio exterior (Anclaje para tierra).


NOTA GN01: Todas las medidas de las estructuras y sistemas de anclaje indicadas en los detalles, deben ser revisadas y validadas por el especialista de cálculo del proyecto.

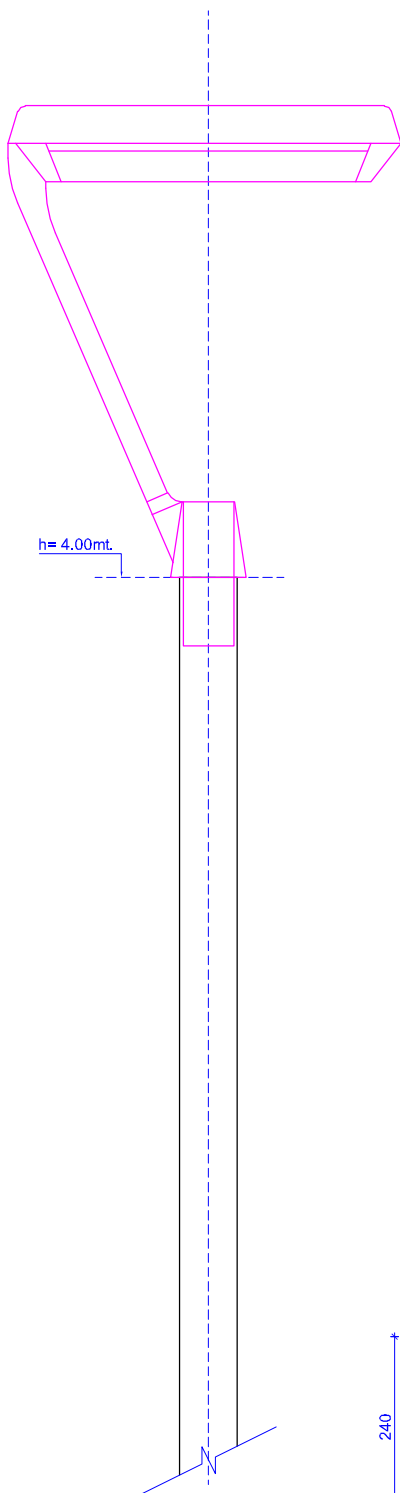


**VISTA LATERAL
CORONACION DE ANCLAJE**
esc. 1:10

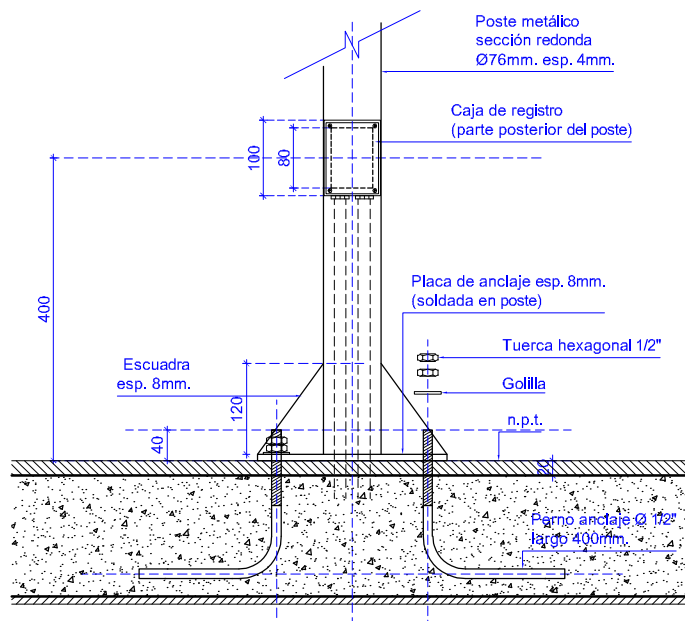


**DETALLE ANCLAJE POSTE
(EN LOSA)**
esc. 1:10

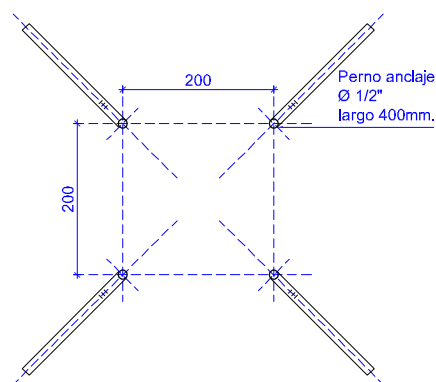

**PERNOS DE ANCLAJE POSTE
(EN LOSA)**
esc. 1:10

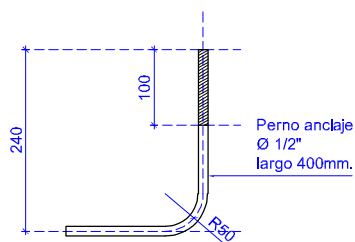

PERNO DE ANCLAJE
esc. 1:10

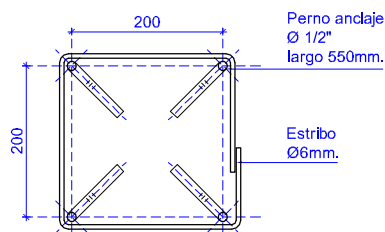


CANASTILLO DE ANCLAJE
esc. 1:10

ESQUEMA M02 / DETALLES


Poste E400-P. / Luminaria patio exterior (Anclaje para losa).

PROYECTO
EDICIÓN F02
AGOSTO / 2020


NOTA GN01: Todas las medidas de las estructuras y sistemas de anclaje indicadas en los detalles, deben ser revisadas y validadas por el especialista de cálculo del proyecto.

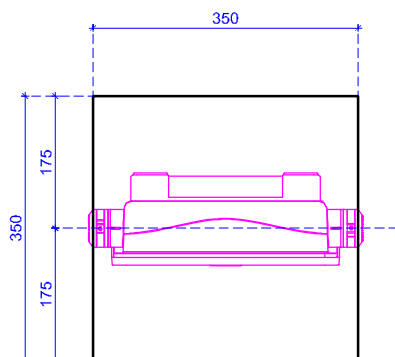

**DETALLE DE ANCLAJE
VISTA SUPERIOR**
esc. 1:10

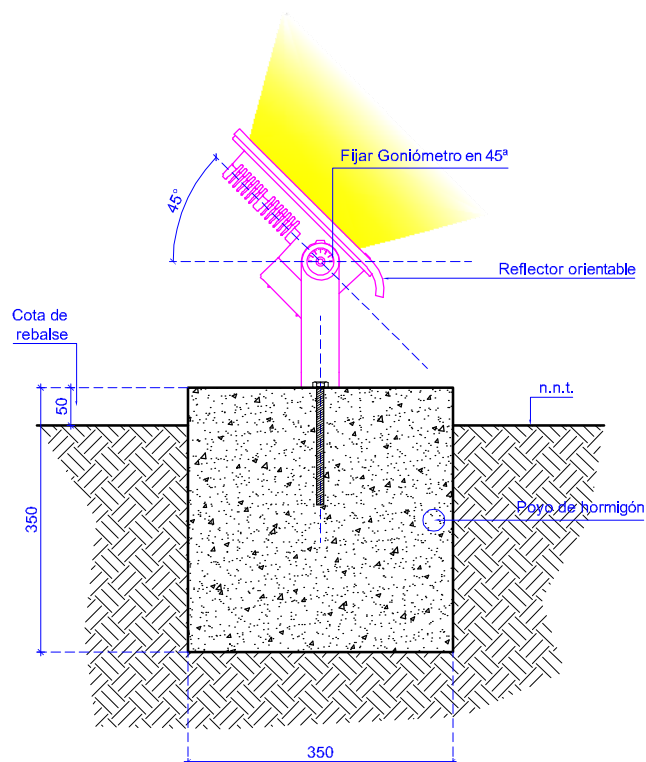

**DETALLE DE ANCLAJE
VISTA LATERAL / POSICION VALIDA**
esc. 1:10

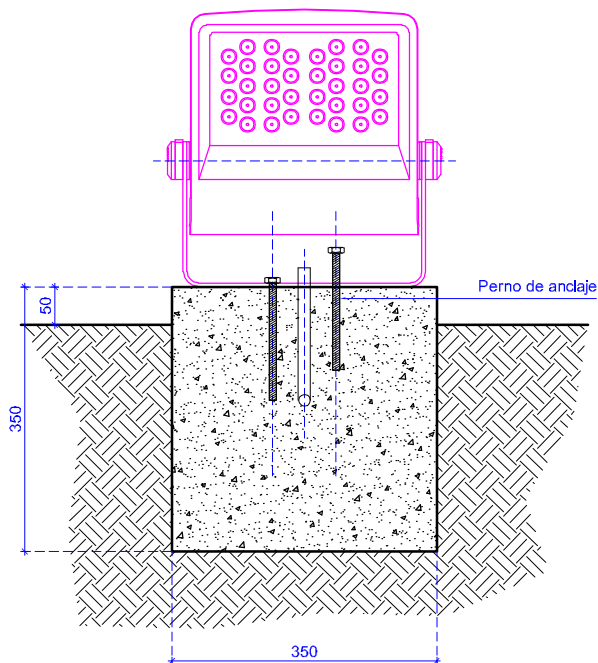


**DETALLE DE ANCLAJE
VISTA FRONTAL**
esc. 1:10


ESQUEMA M03 / DETALLES

Luminaria patio exterior "Talud" (Anclaje para tierra).


PROYECTO
EDICIÓN F02
AGOSTO / 2020

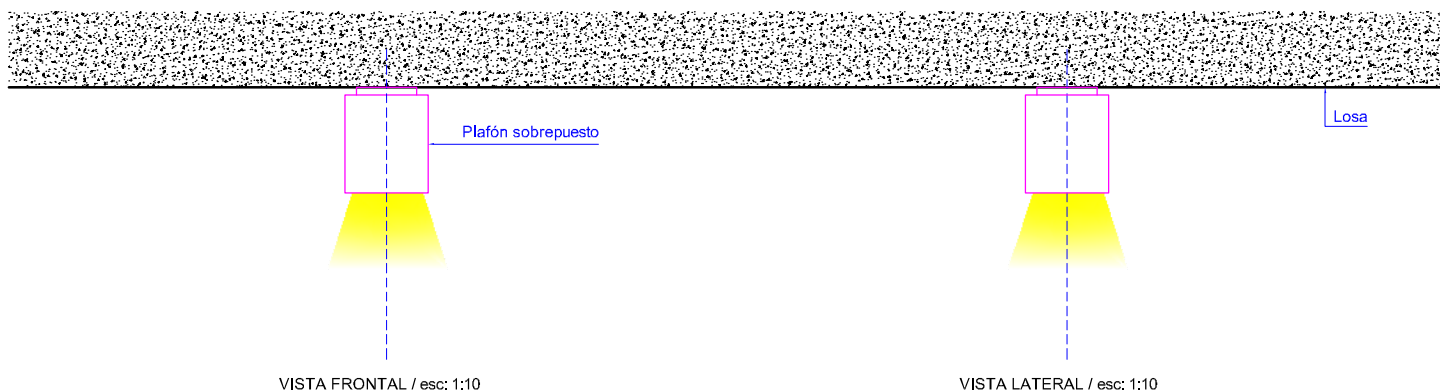


R01 ESQUEMA DE REFERENCIA / Luminaria spot. / sobrepuesta en losa. / Baños.

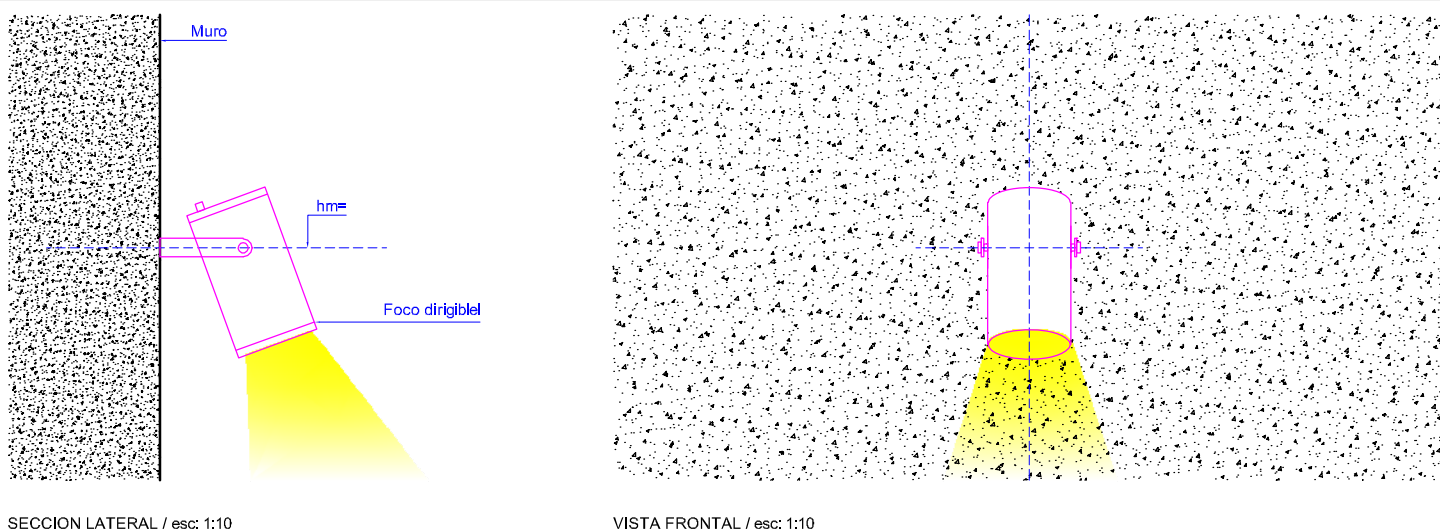


R02 ESQUEMA DE REFERENCIA / Luminaria tipo spot. / Adosada a muro o pilar. / Nave central y laterales.

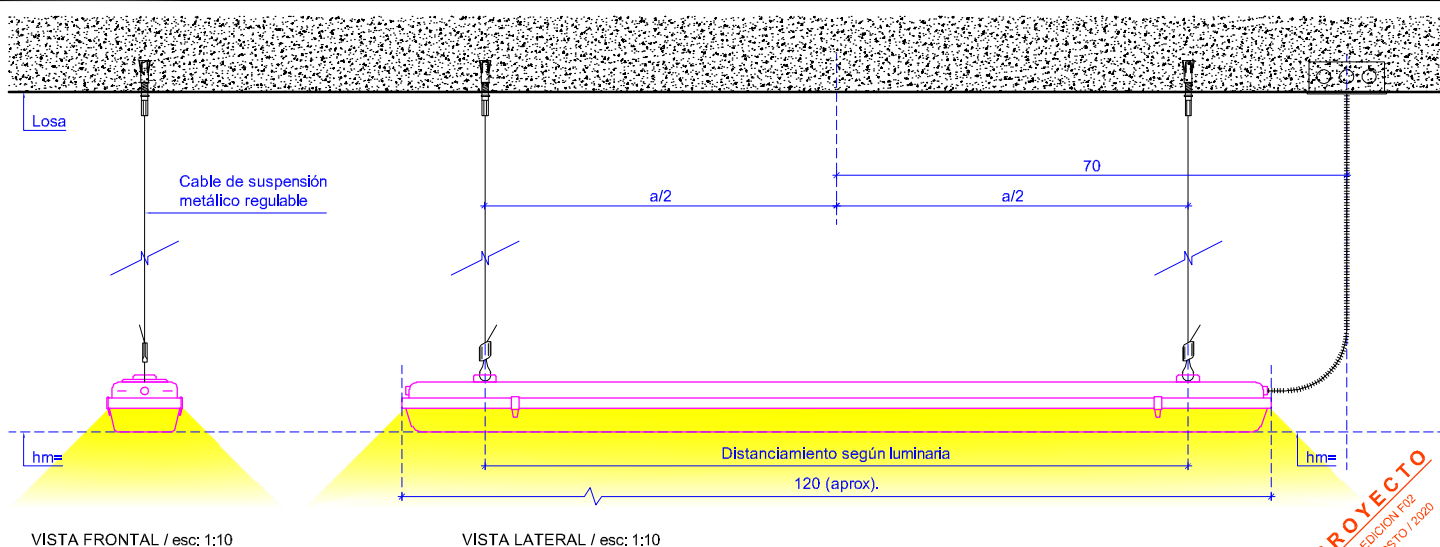

R03 ESQUEMA DE REFERENCIA / Luminaria hermética individual. / Colgante desde losa. / Bodegas y Sala eléctrica

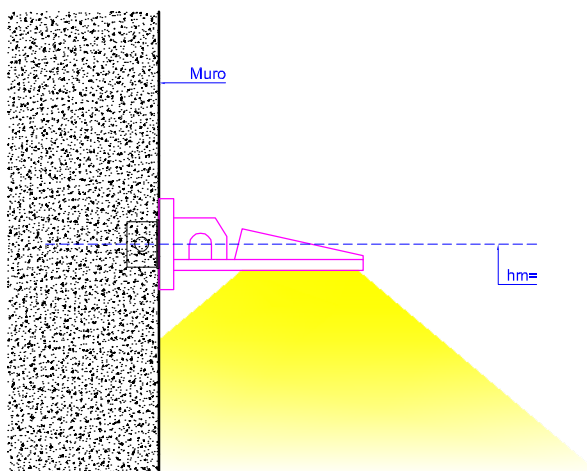


SECCION LATERAL / esc: 1:10

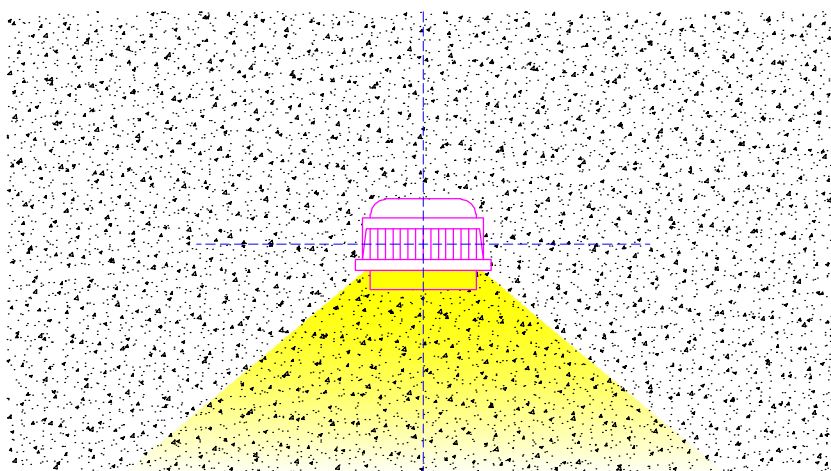


VISTA FRONTAL / esc: 1:10

R04 ESQUEMA DE REFERENCIA / Luminaria tipo proyector. / Adosada a muro o pilar. / Nave central.

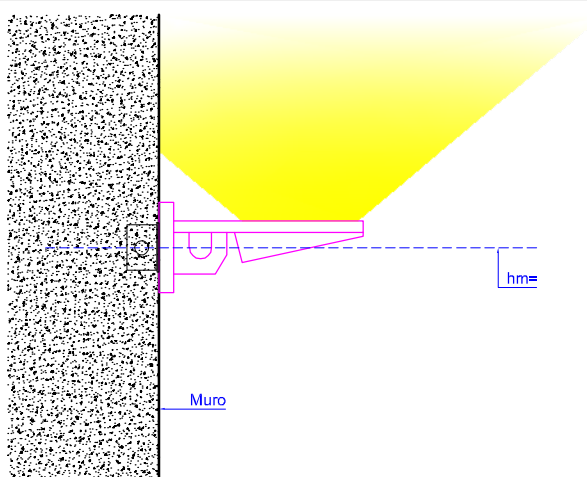


SECCION LATERAL / esc: 1:10

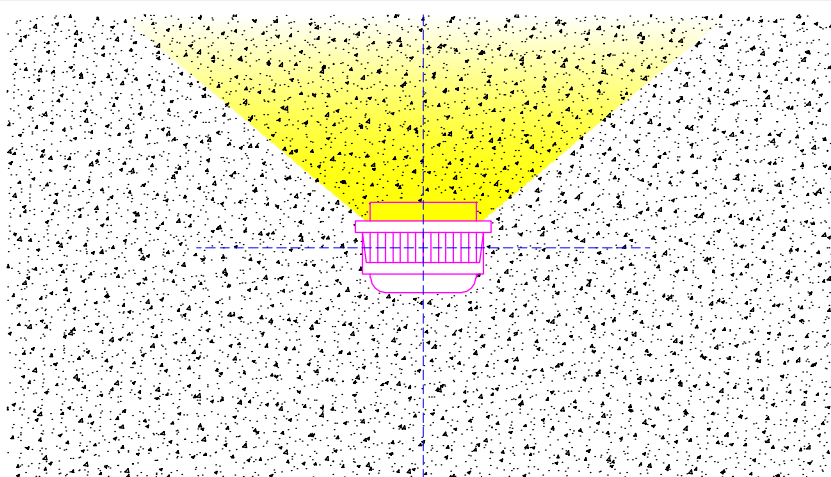


VISTA FRONTAL / esc: 1:10

R05 ESQUEMA DE REFERENCIA / Luminaria tipo proyector. / Adosada a muro o pilar. / Nave central.

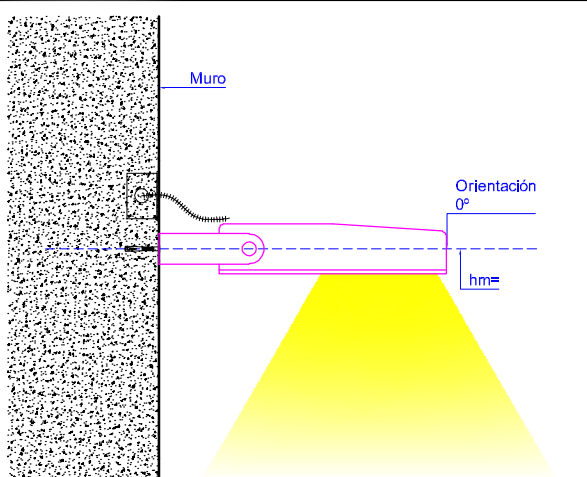


SECCION LATERAL / esc: 1:10

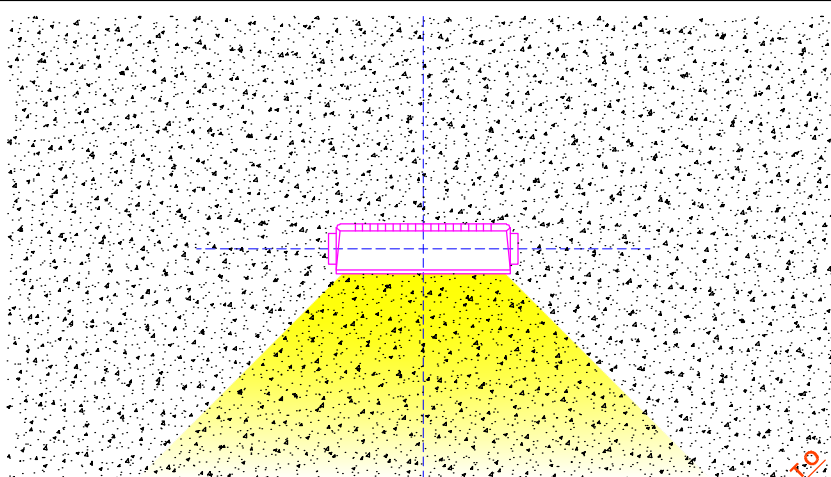


VISTA FRONTAL / esc: 1:10

R06 ESQUEMA DE REFERENCIA / Luminaria tipo proyector. / adosada a muro. / Pasillo laterales exteriores.

PROYECTO
EDICIÓN F02
AGOSTO 2020

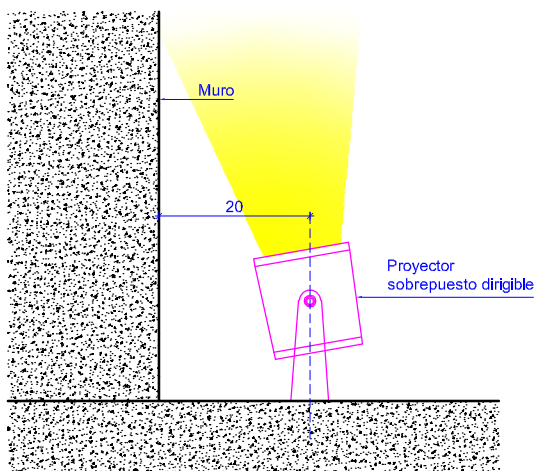


SECCION LATERAL / esc: 1:10

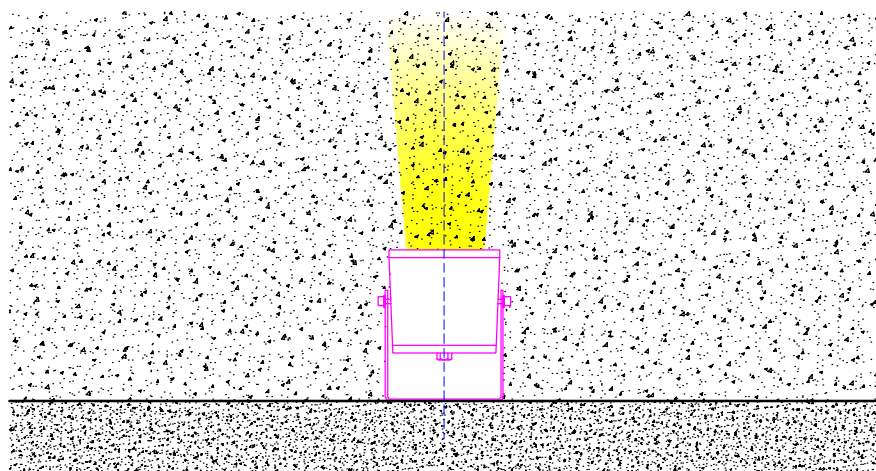


VISTA FRONTAL / esc: 1:10

R07 ESQUEMA DE REFERENCIA / Luminaria spot tipo proyector. / Sobrepuesta en piso o loseta. / Fachadas.

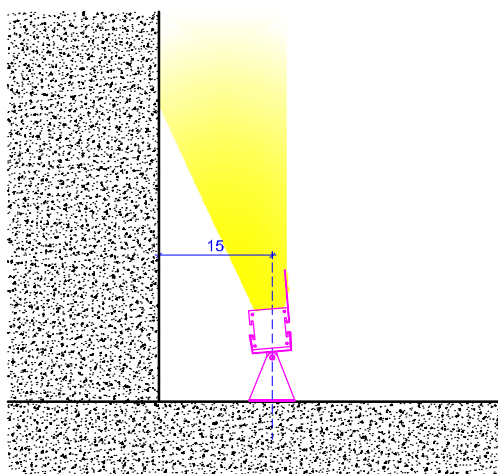


SECCION LATERAL / esc: 1:10

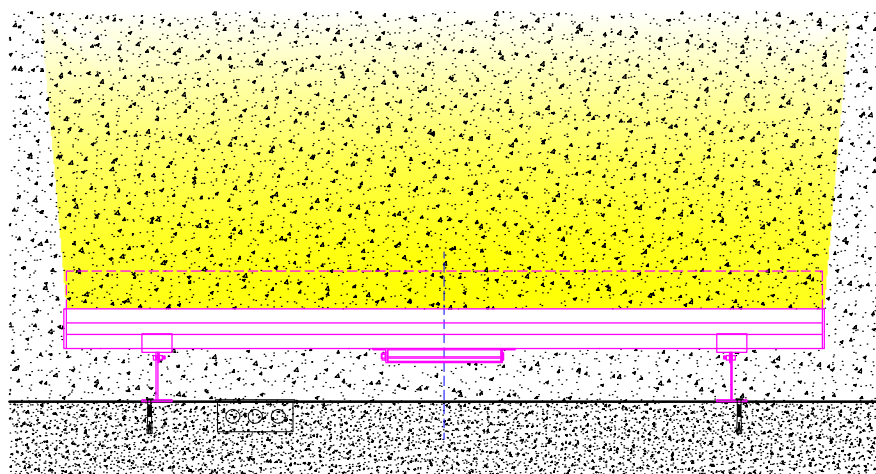


VISTA FRONTAL / esc: 1:10

R08 ESQUEMA DE REFERENCIA / Luminaria tipo proyector lineal. / Sobrepuesta en piso. / Fachada acceso y 2 nivel.

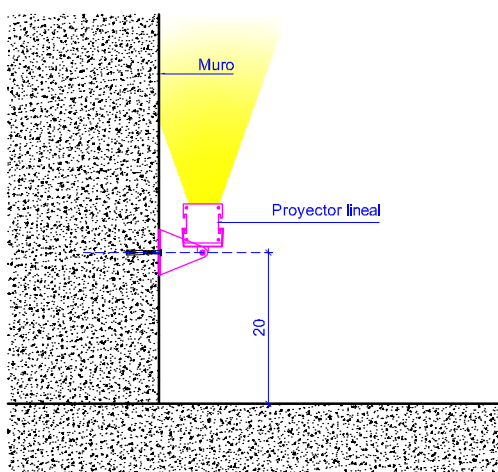


SECCION LATERAL / esc: 1:10

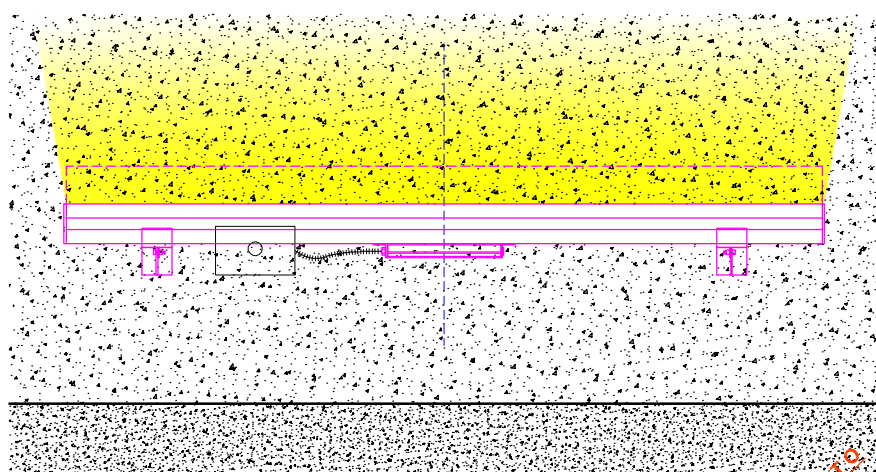


VISTA FRONTAL / esc: 1:10

R09 ESQUEMA DE REFERENCIA / Luminaria tipo proyector lineal. / Adosada a muro. / Fachadas.

PROYECTO
EDICIÓN F02
AGOSTO 2020

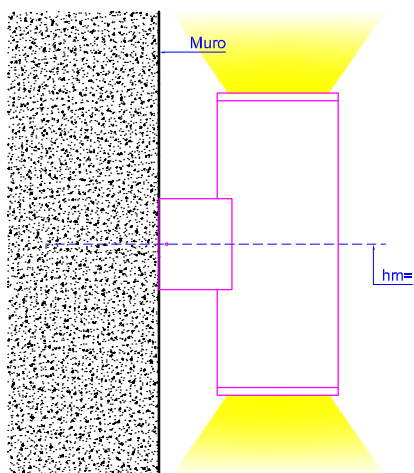


SECCION LATERAL / esc: 1:10

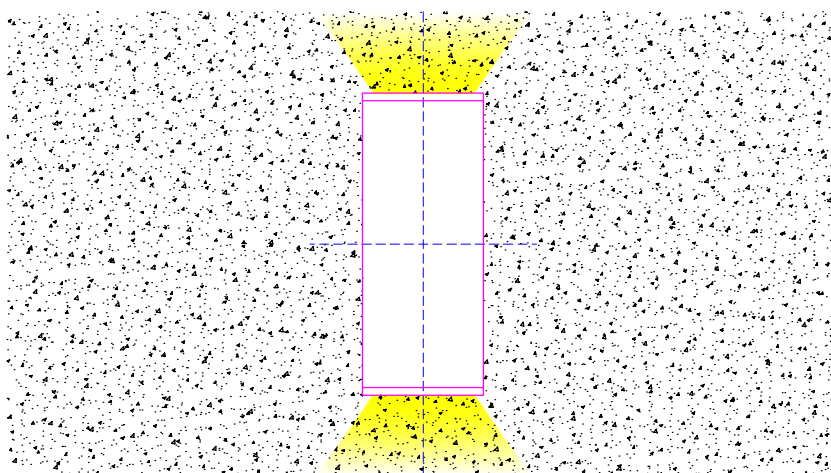


VISTA FRONTAL / esc: 1:10

R10 ESQUEMA DE REFERENCIA / Luminaria hermética, tipo aplique. / adosada a muro. / Fachadas y patio interior.

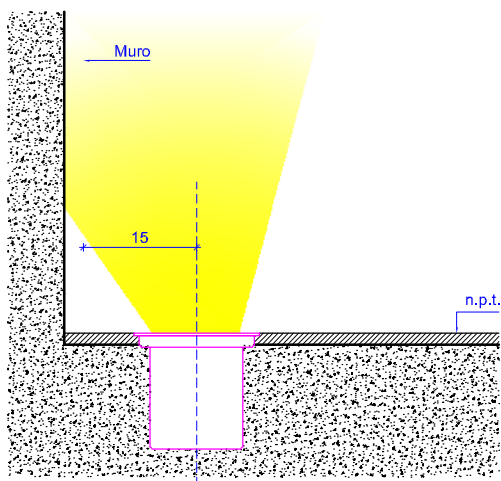


SECCION LATERAL / esc: 1:10

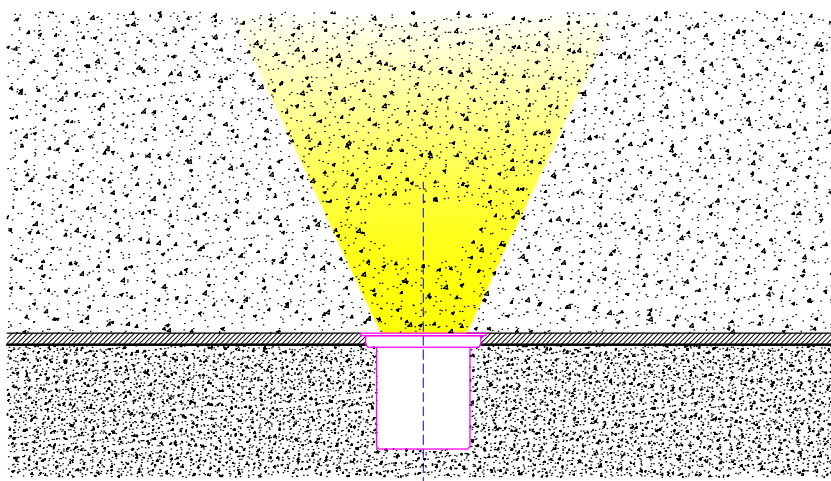


VISTA FRONTAL / esc: 1:10

R11 ESQUEMA DE REFERENCIA / Luminaria spot. / Embutida en piso. / Cripta.

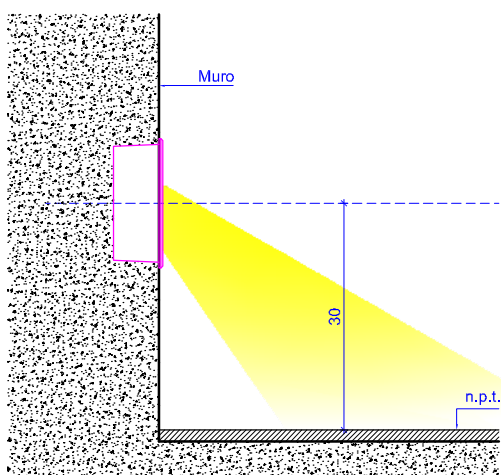


SECCION LATERAL / esc: 1:10

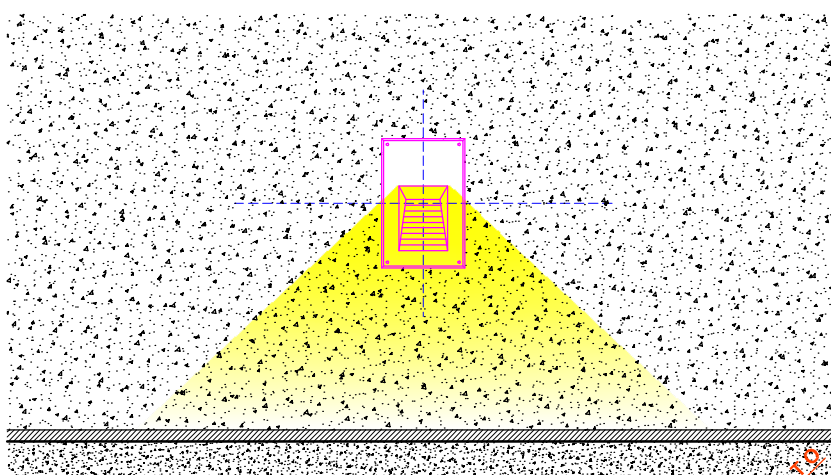


VISTA FRONTAL / esc: 1:10


R12 ESQUEMA DE REFERENCIA / Luminaria de luz rasante. / Embutida en muro. / Escalera acceso cripta.

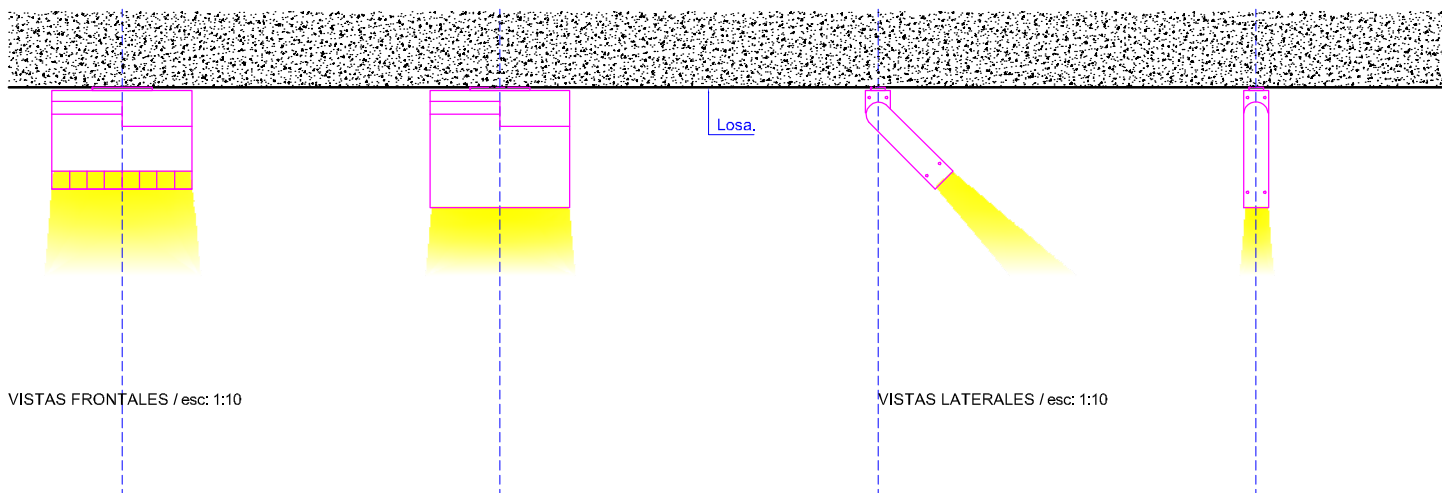

R13 ESQUEMA DE REFERENCIA / Luminaria tipo spot. / Sobrepuesta en losa o cielo. / Cripta.

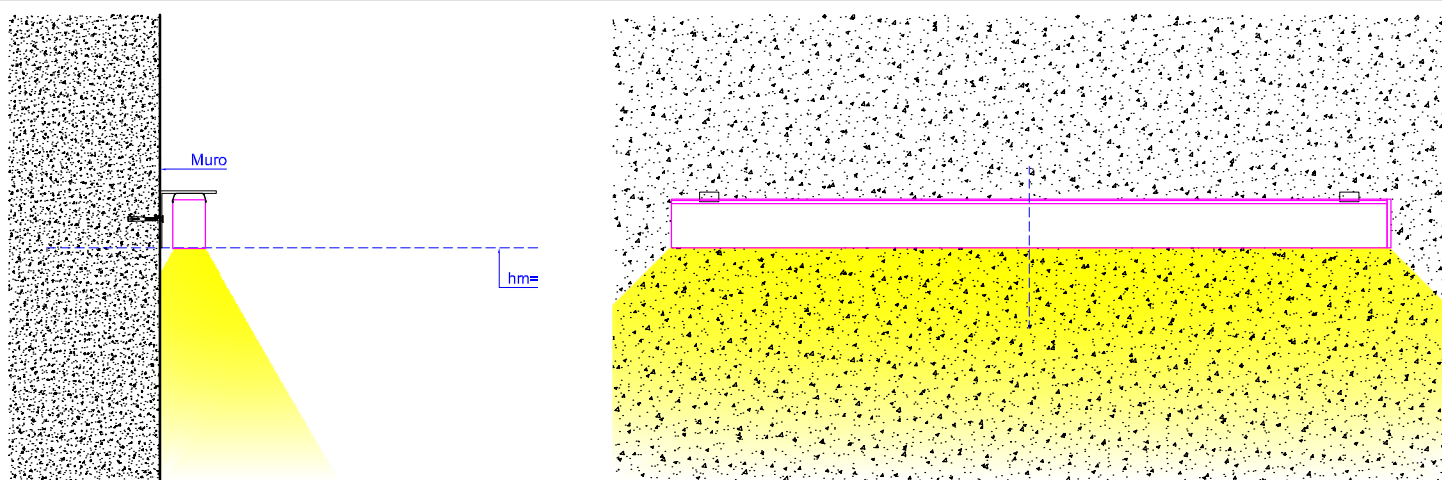

R14 ESQUEMA DE REFERENCIA / Luminaria lineal. / Adosada a muro. / Cripta.

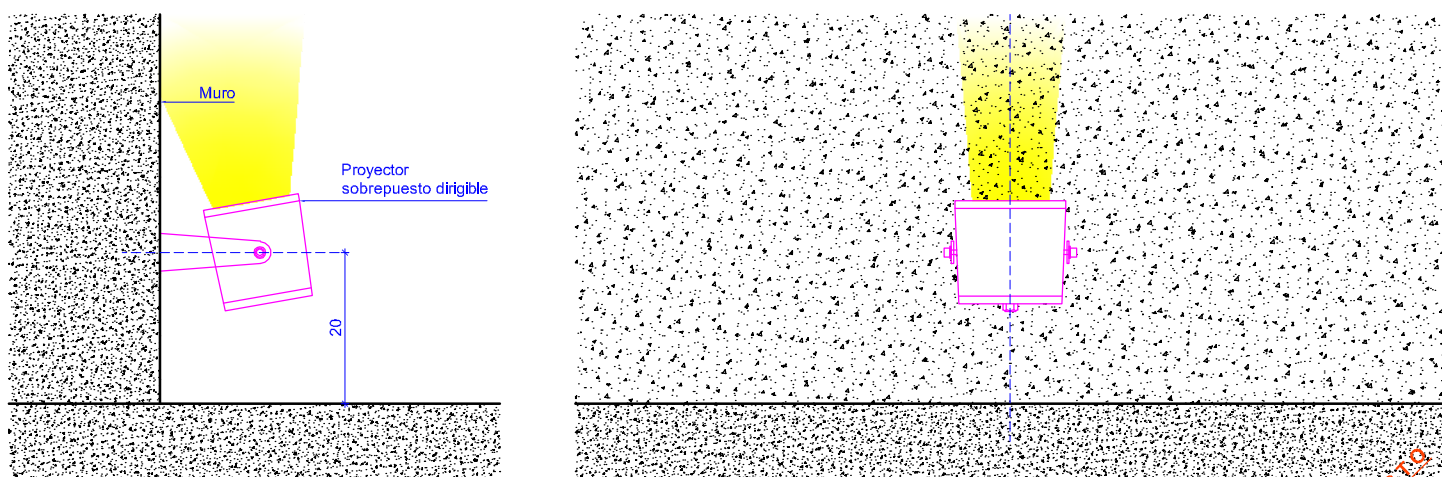

R15 ESQUEMA DE REFERENCIA / Luminaria spot tipo proyector. / Adosado a muro. / Fachadas.